



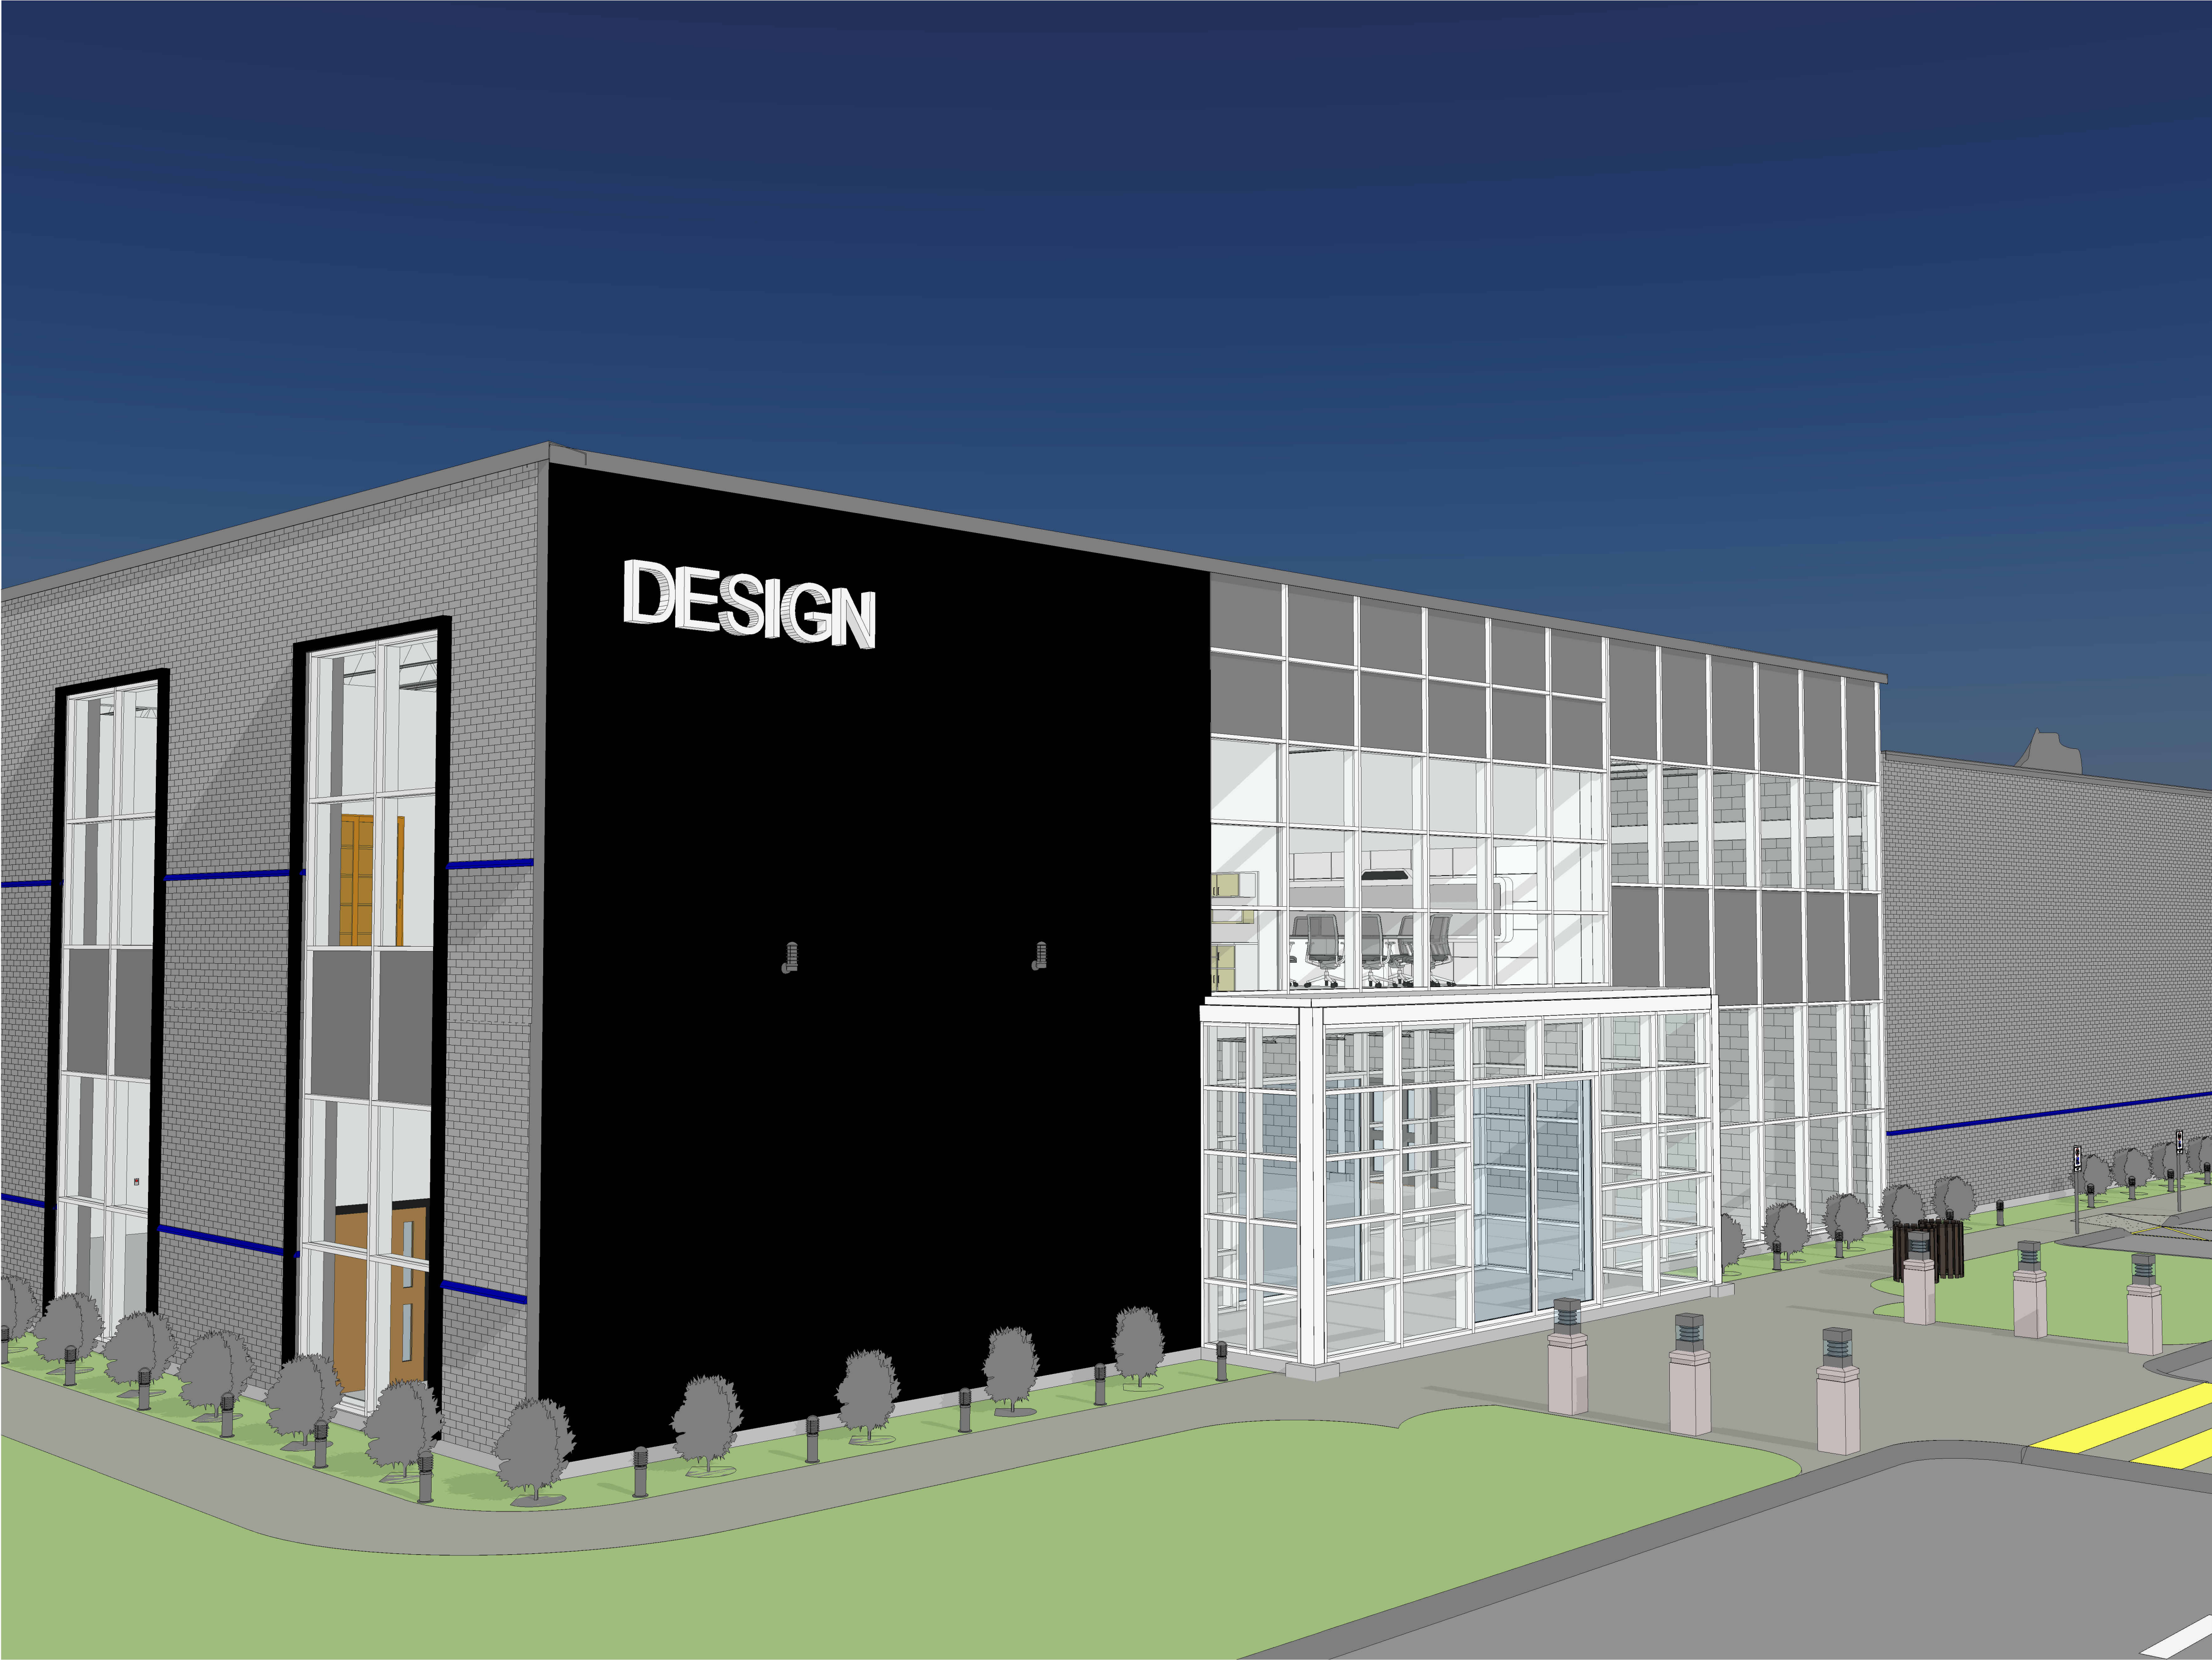

Sheet List		
Sheet Name	Sheet Number	Drawn By
SITE PLAN	D100	AN
SITE ISO	D100-1	AN
MAIN FLOOR PLAN	D101	AN
MAIN FLOOR ISO	D101-2	AN
LEVEL 2 FLOOR PLAN	D102	AN
LEVEL 2 FLOOR ISO	D102-3	AN
ELEVATIONS	D103	AN
ELEVATIONS	D104	AN




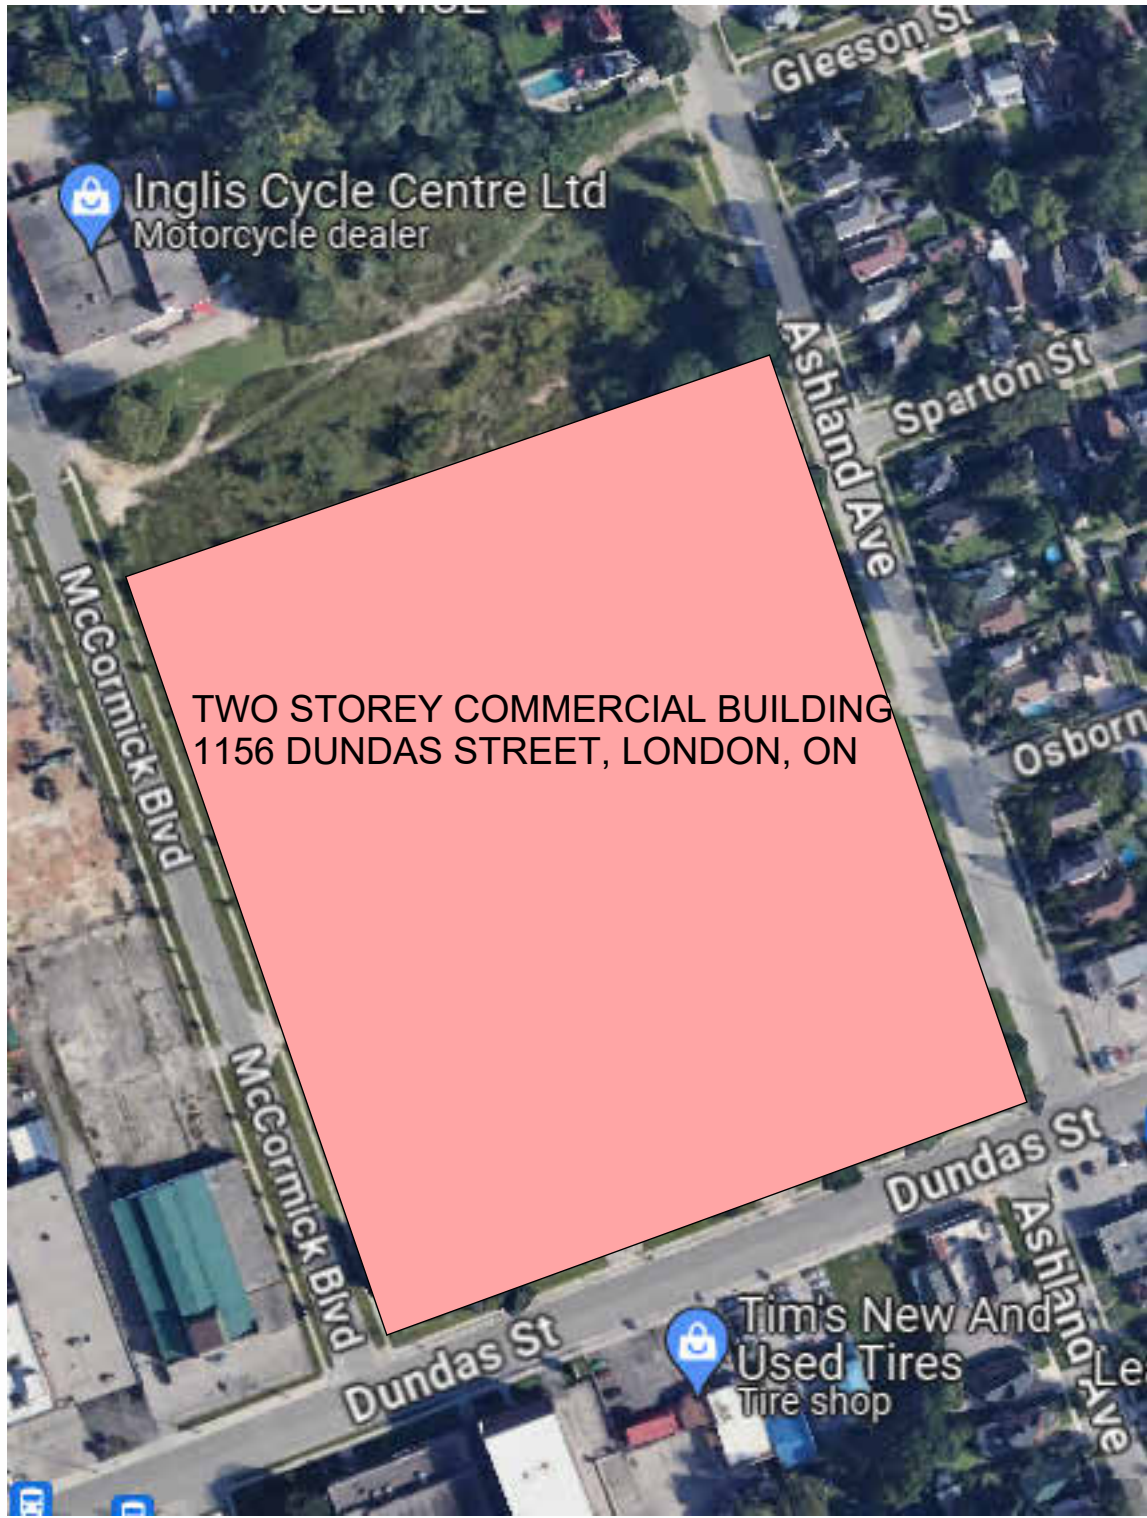



SITE KEYPLAN

TWO STOREY COMMERCIAL



ZONE: CSA2	ALLOWABLE	PROVIDED
LOT AREA (MIN):	17987.649 m ²	17987.649 m ²
LOT FRONTAGE (MIN):	30.0 m	176.4 m
LOT DEPTH (MIN):	30.0 m	102.0 m
FRONT & EXTERIOR SIDE YARD SETBACK (MIN):	8.0 m	8.0 m
REAR & INTERIOR SIDE YARD SETBACK (MIN):	8.0 m	8.0 m
LANDSCAPED AREA (MIN):	1798.7649 m ²	13996.7 m ²
LOT COVERAGE (MAX):	5396.2947 m ²	1227.3 m ²
BUILDING HEIGHT (MAX):	9.00 m	8.00 m
GROSS FLOOR AREA - GFA - (MAX):	10000 m ²	1558 m ²
GFA FOR OFFICE USE (MAX):	1500 m ²	346.5 m ²
GFA FOR COMMERCIAL AND PRIVATE SCHOOL USE (MAX):	1500 m ²	0 m ²
GFA FOR CINEMAS USE (MAX):	1000 m ²	0 m ²
PARKING REQUIREMENT:	0 SPACES	23 SPACES

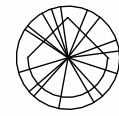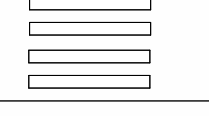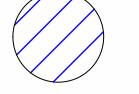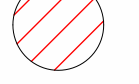
SITE LEGENDS											
	PROPOSED TREE		FENSE		TRASH CAN		BOLLARD		STREET LIGHT		PLANTS
		EXISTING TREE		HYDRO POLE		STOP SIGN		BARRIER FREE		CONC.SIDEWALK	
		DEMOLISH TREE		CROSSWALK		TRASH CAN		MAIN ENTRANCE		ASPHALT	
				MOLOK		FIRE ROUTE		SECONDARY ENTRY / EXIT		SOD	

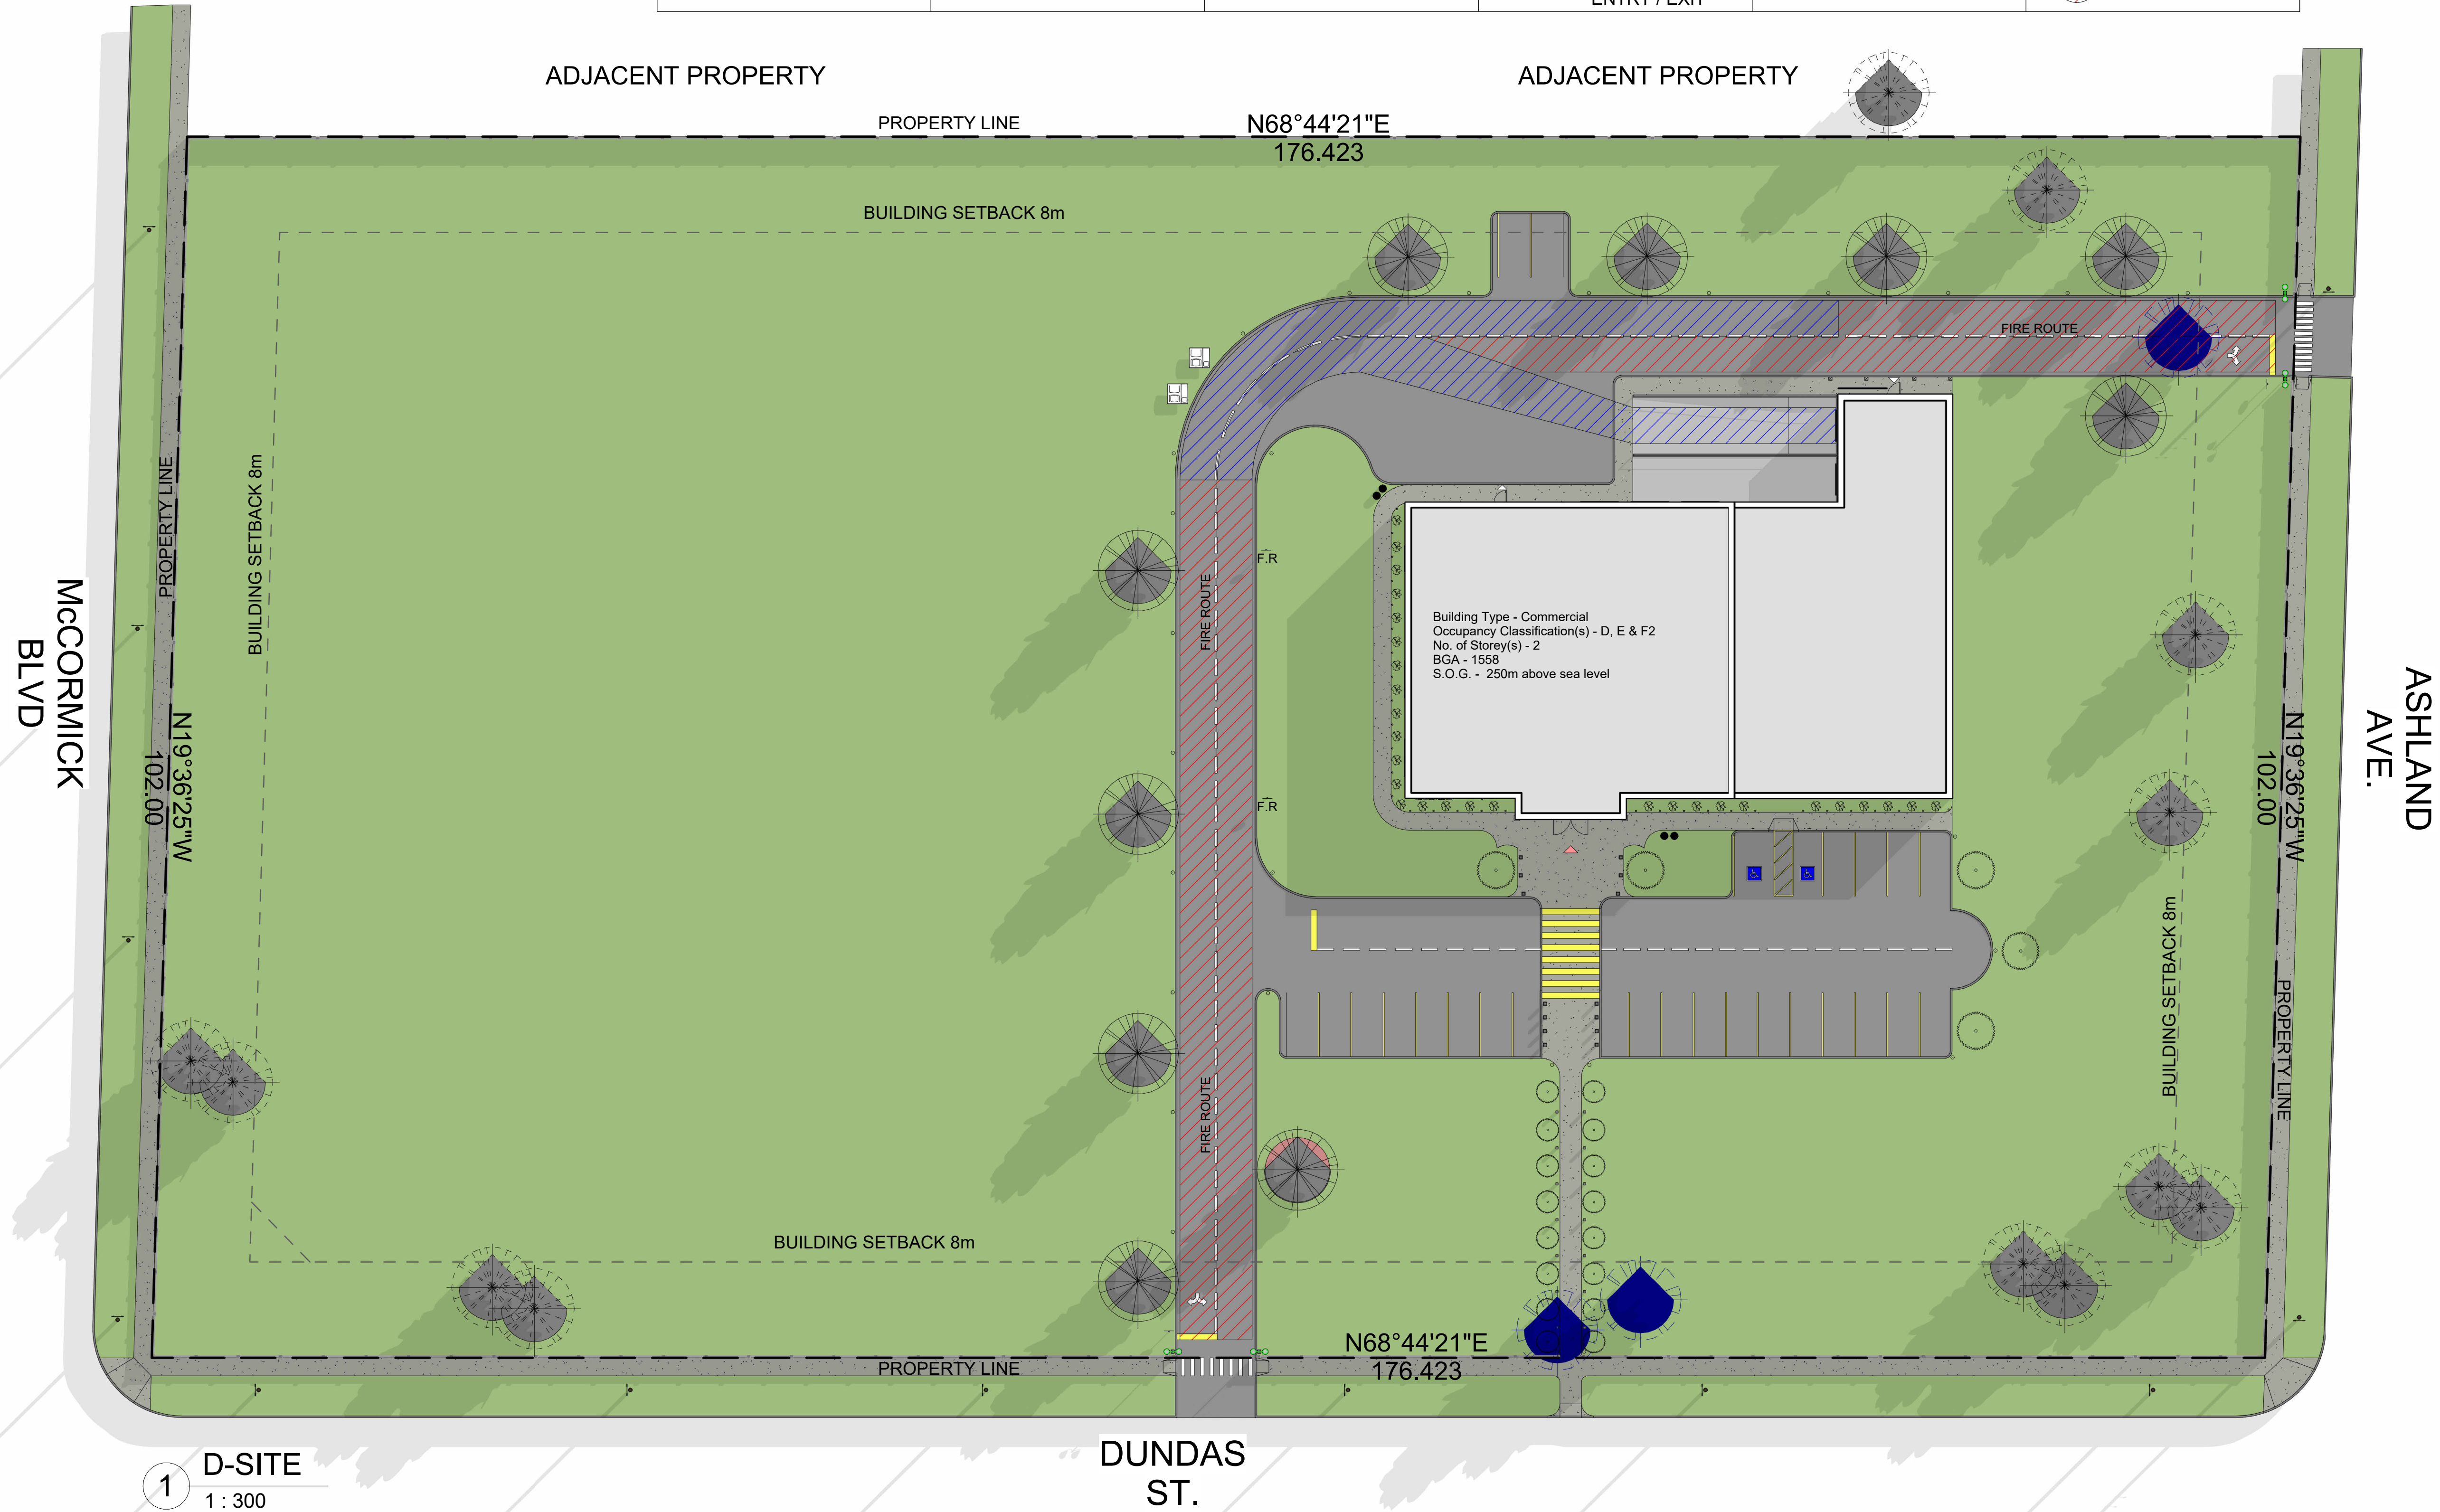

2401-RO1-1156DUNDASSTREET-LONDON-PROJECT03-AN
1156DUNDASSTREET-LONDON

SITE PLAN

1:300

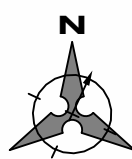

TWO STOREY COMMERCIAL




Architectural Technology

School of Building Technology

London Ontario Canada


AN 0001
D100

6/20/2024 6:22:03 PM

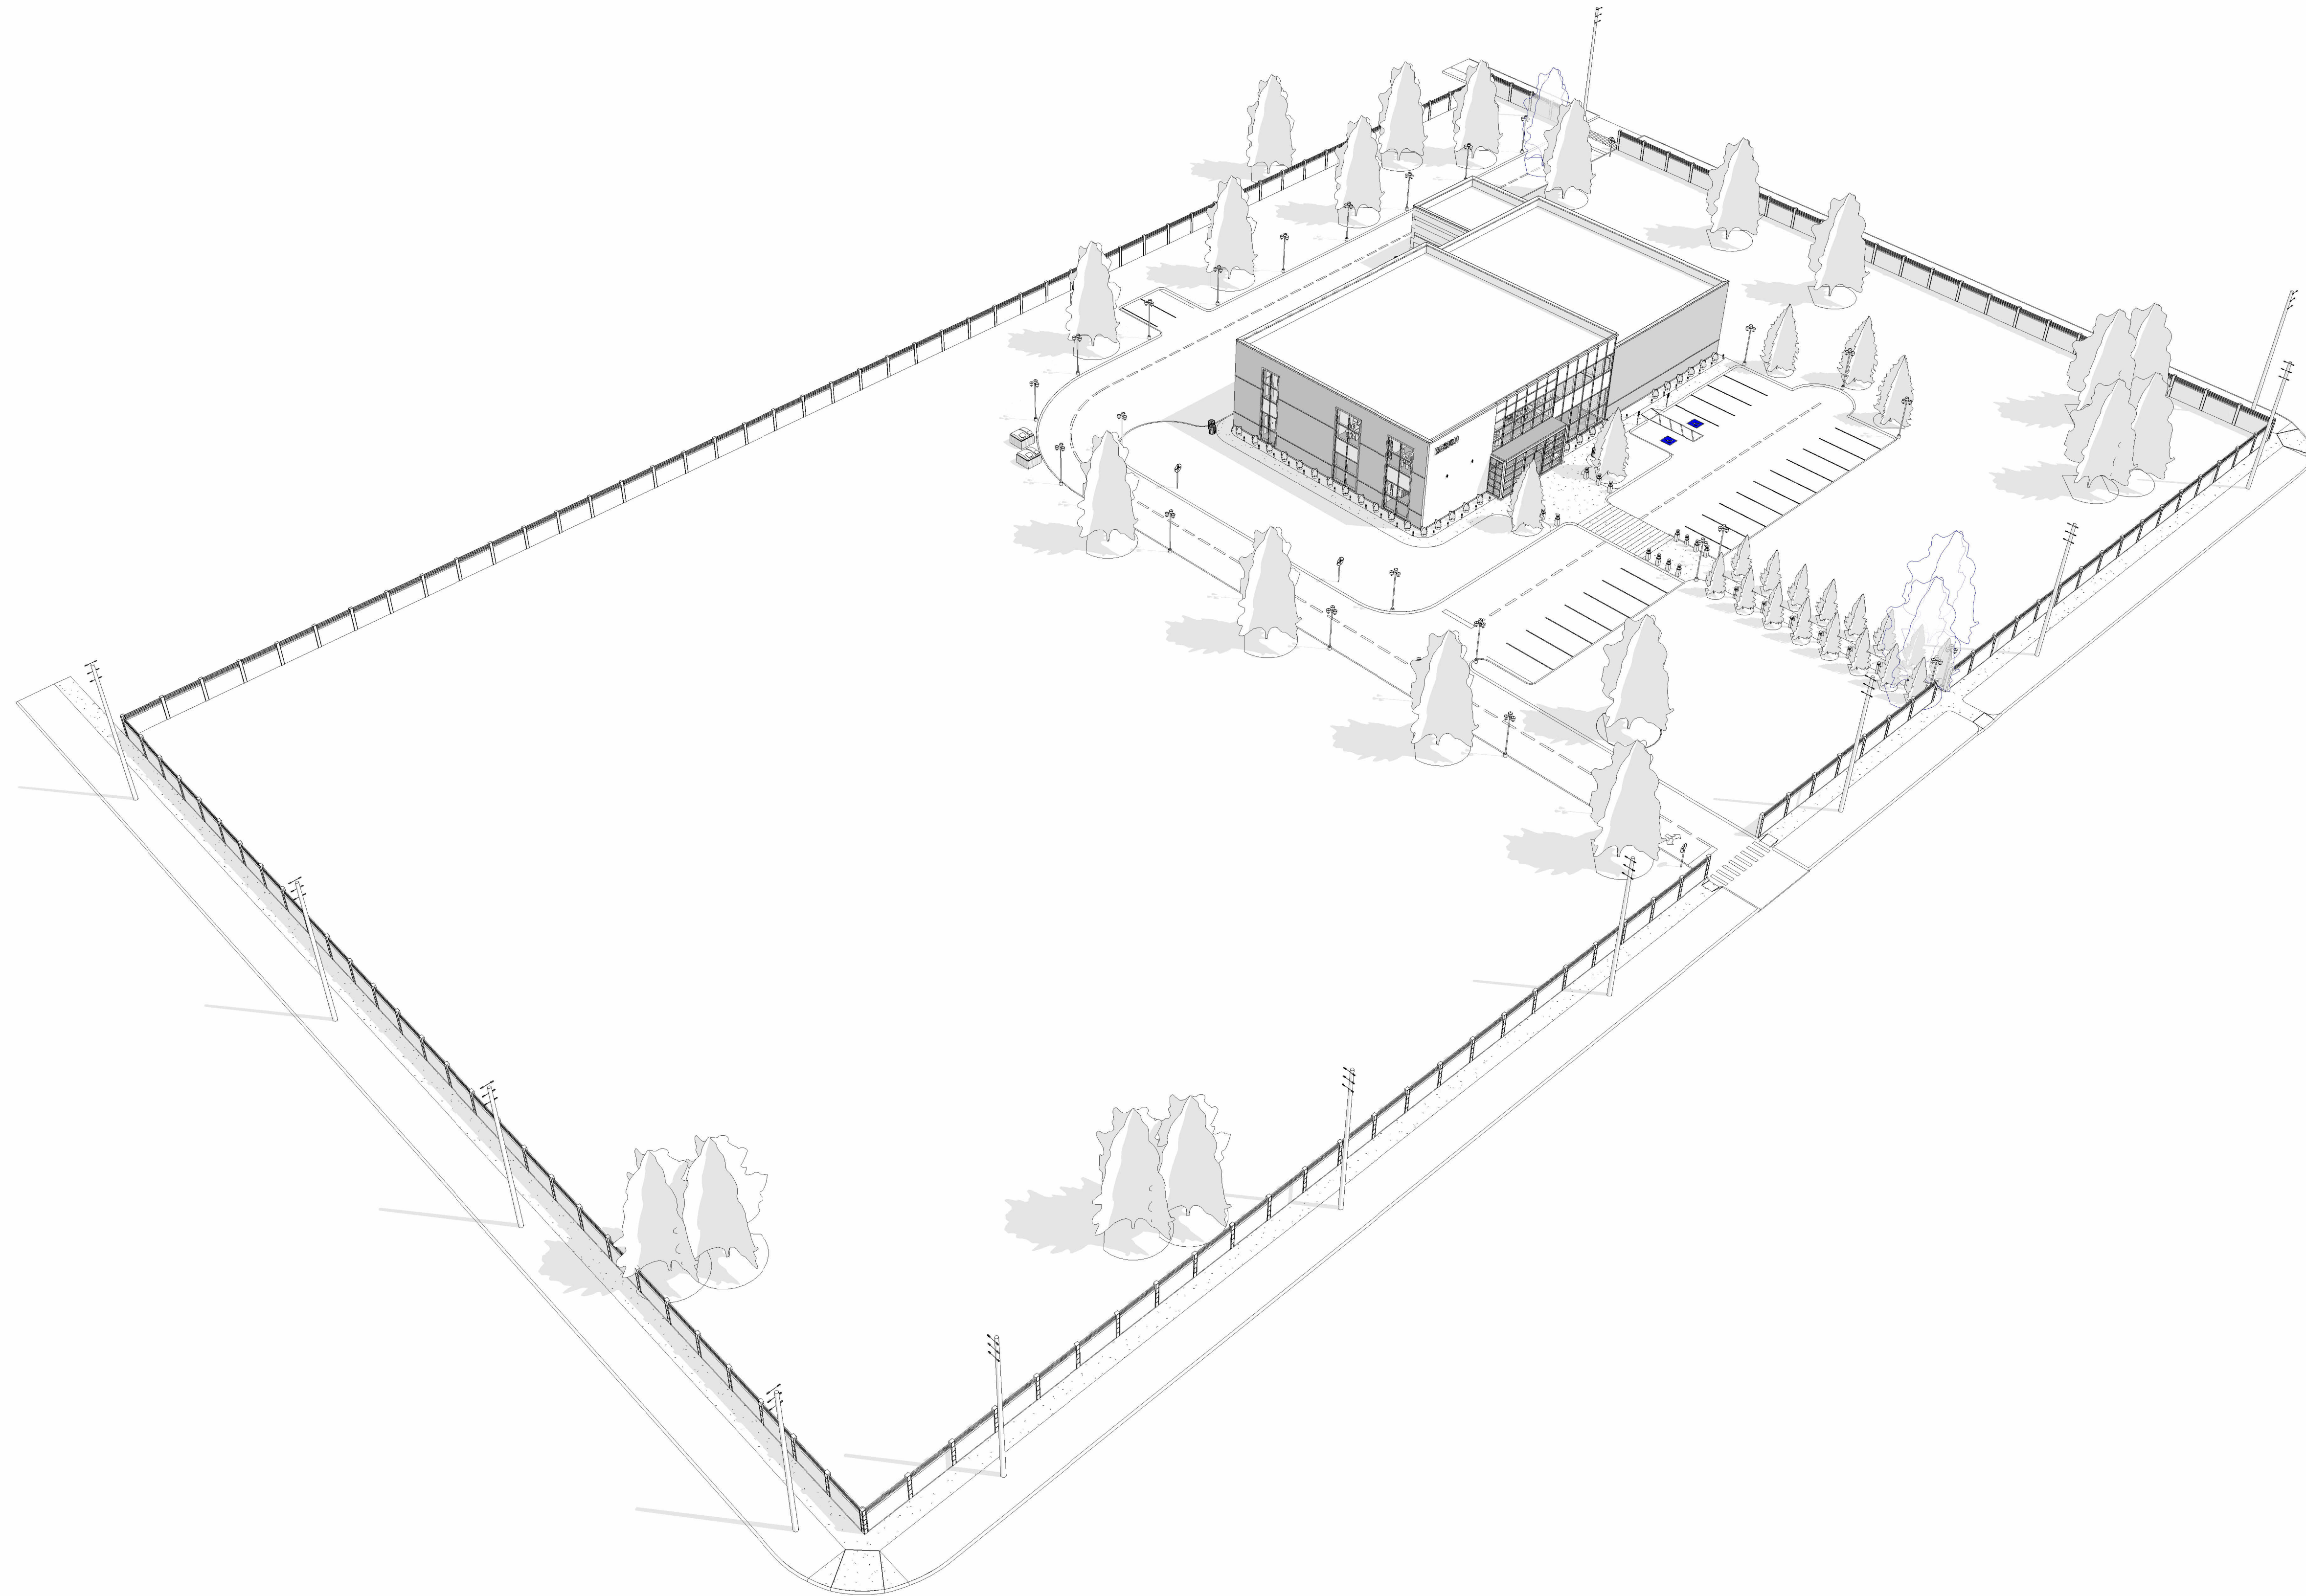

2401-RO1-1156DUNDASSTREET-LONDON-PROJECT03-AN
1156DUNDASSTREET-LONDON

SITE ISO

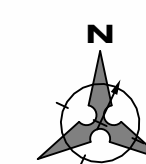

TWO STOREY COMMERCIAL



Architectural Technology

School of Building Technology

London Ontario Canada

Designer
0001
D100-1

6/20/2024 6:22:13 PM



Room Legend

- ELEVATOR
- EXIT STAIR
- IT CLOSET
- JANITOR
- LOG.OFFICE
- MECH/ELEC.
- OFFICE
- VESTIBULE
- W/C

TWO STOREY COMMERCIAL



Architectural Technology

School of Building Technology

London Ontario Canada

2401-RO1-1156DUNDASSTREET-LONDON-PROJECT03-AN
1156DUNDASSTREET-LONDON


MAIN FLOOR PLAN

1 : 100




AN 0001
D101

6/20/2024 6:22:17 PM

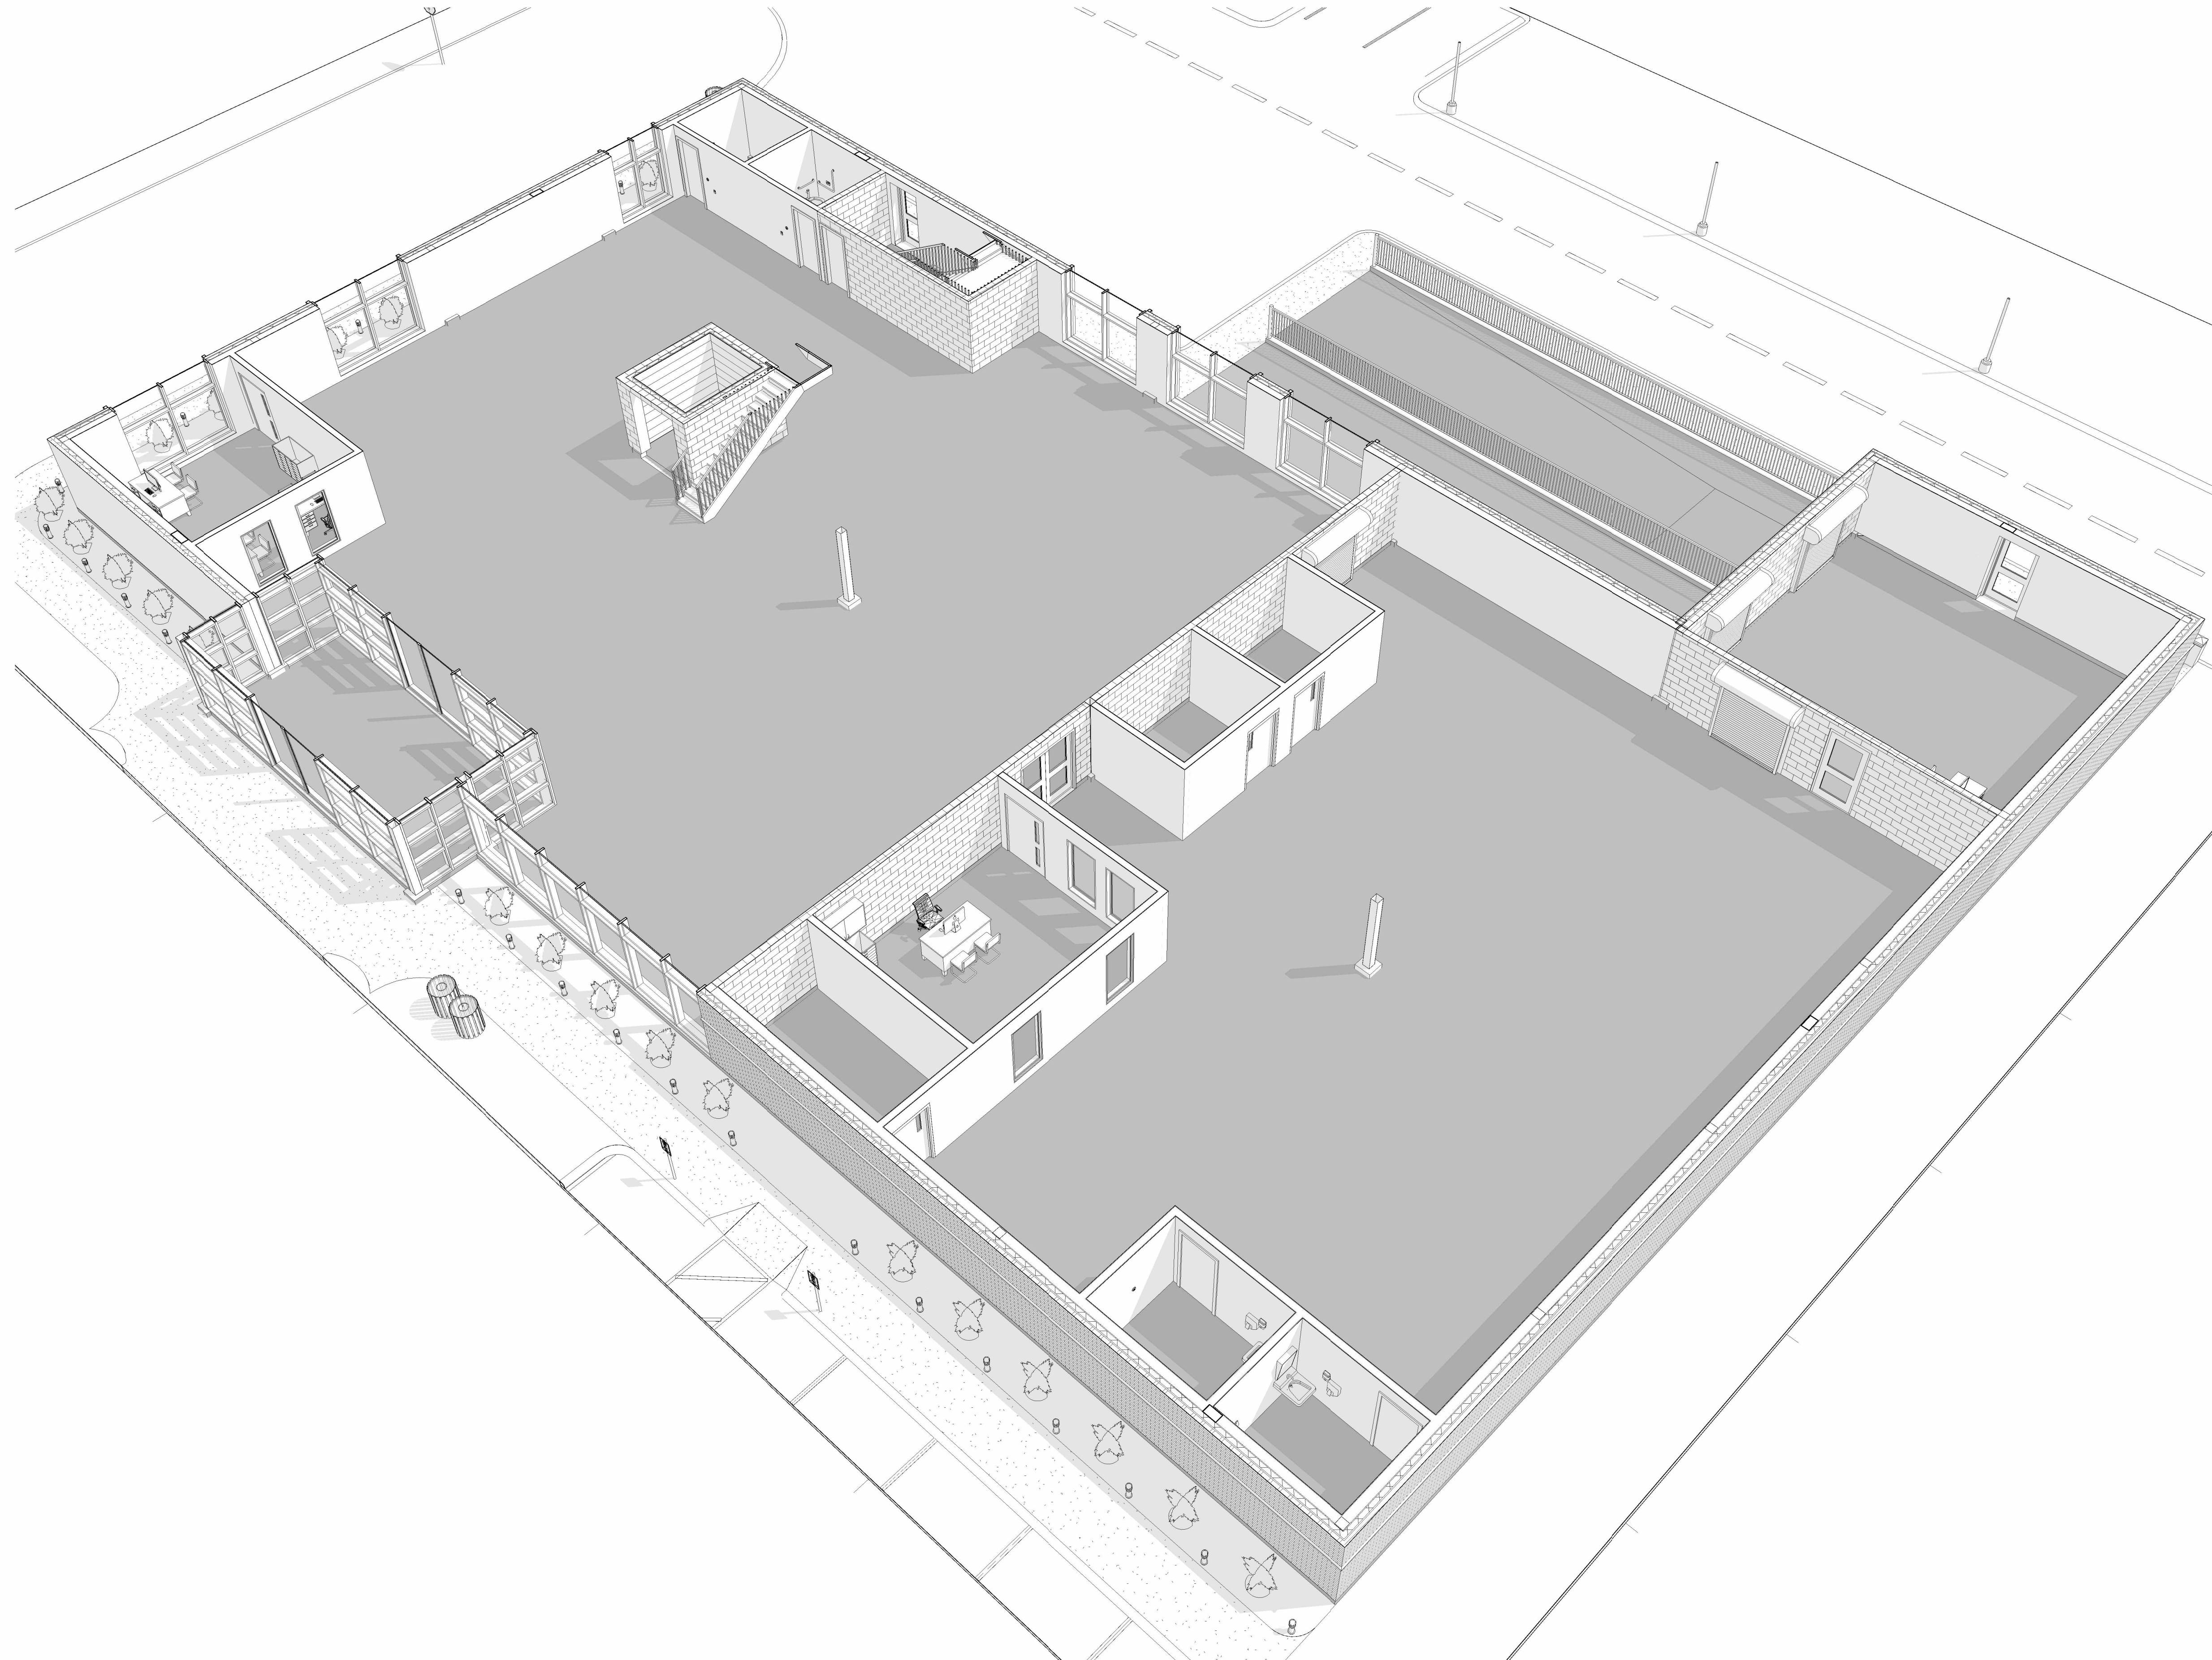

2401-RO1-1156DUNDASSTREET-LONDON-PROJECT03-AN
1156DUNDASSTREET-LONDON

MAIN FLOOR ISO

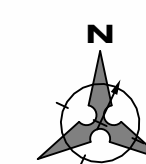

TWO STOREY COMMERCIAL




Architectural Technology

School of Building Technology

London Ontario Canada

AN 0001
D101-2

6/20/2024 6:22:23 PM

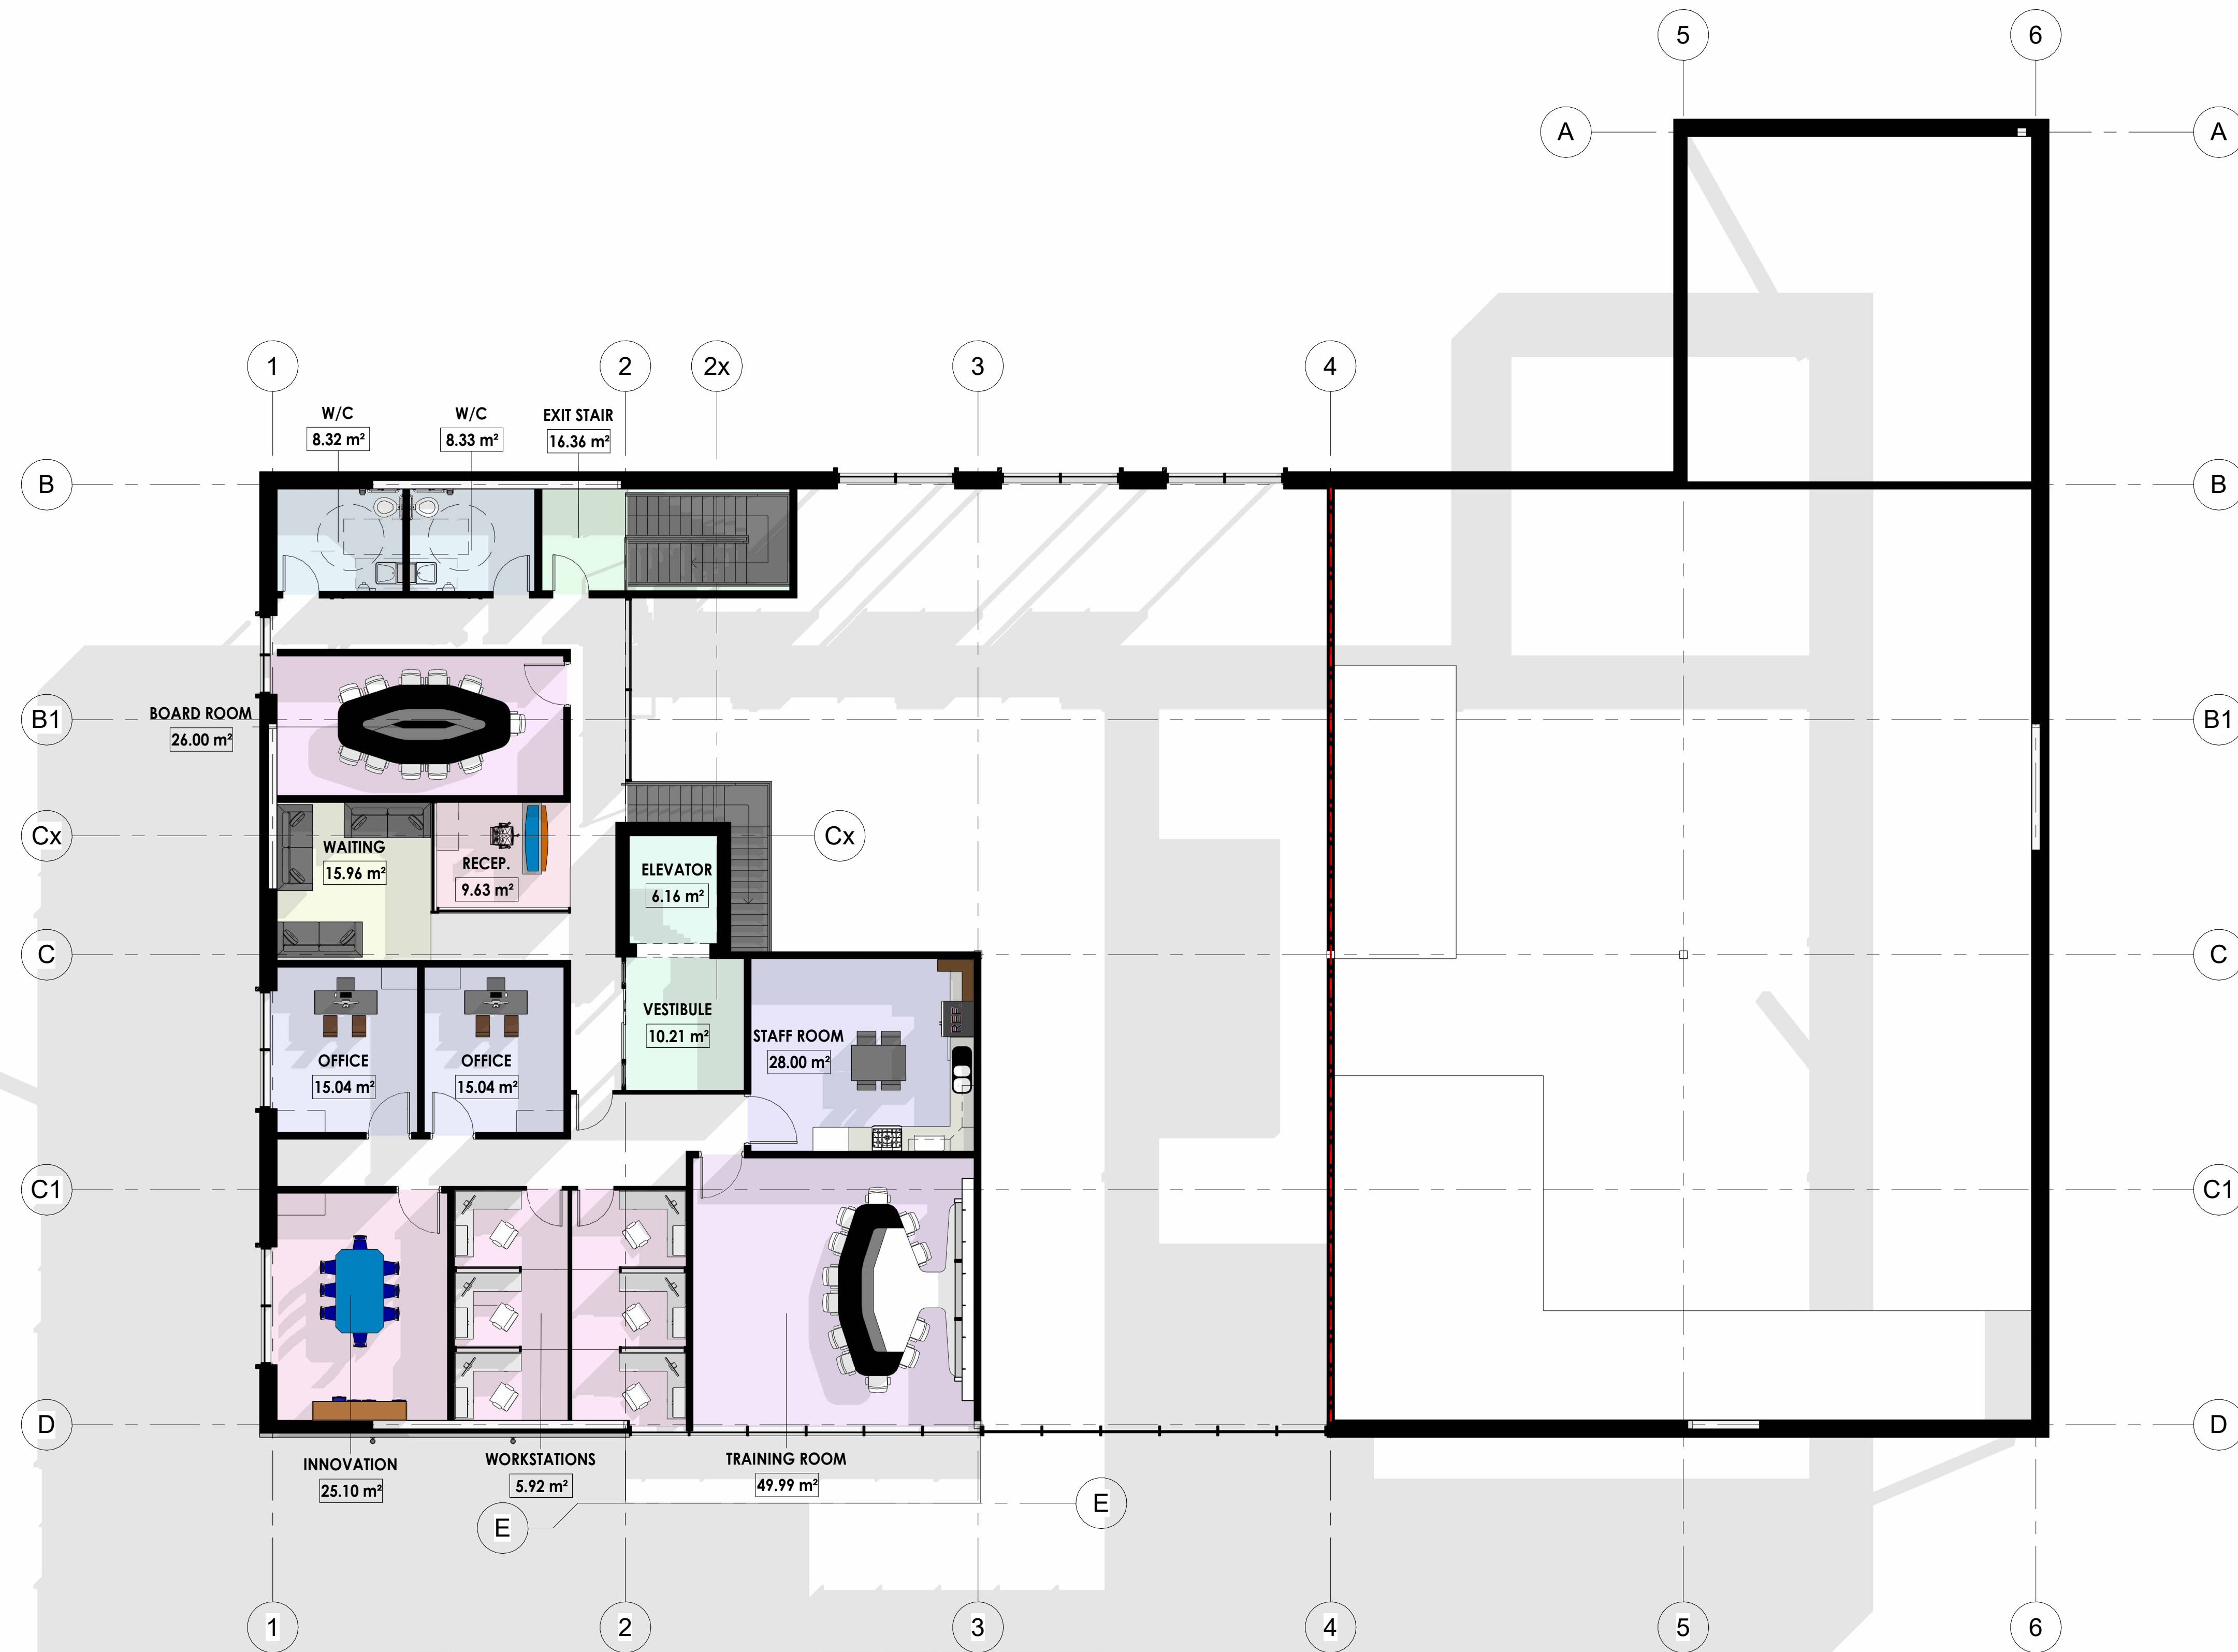

- Room Legend
- BOARD ROOM
 - ELEVATOR
 - EXIT STAIR
 - INNOVATION
 - OFFICE
 - RECEP.
 - STAFF ROOM
 - TRAINING ROOM
 - VESTIBULE
 - W/C
 - WAITING
 - WORKSTATIONS

1 D-LEVEL 2
1 : 100

2401-RO1-1156DUNDASSTREET-LONDON-PROJECT03-AN
1156DUNDASSTREET-LONDON

LEVEL 2 FLOOR PLAN

1 : 100



TWO STOREY COMMERCIAL




Architectural Technology

School of Building Technology

London Ontario Canada


AN 0001
D102

6/20/2024 6:22:29 PM

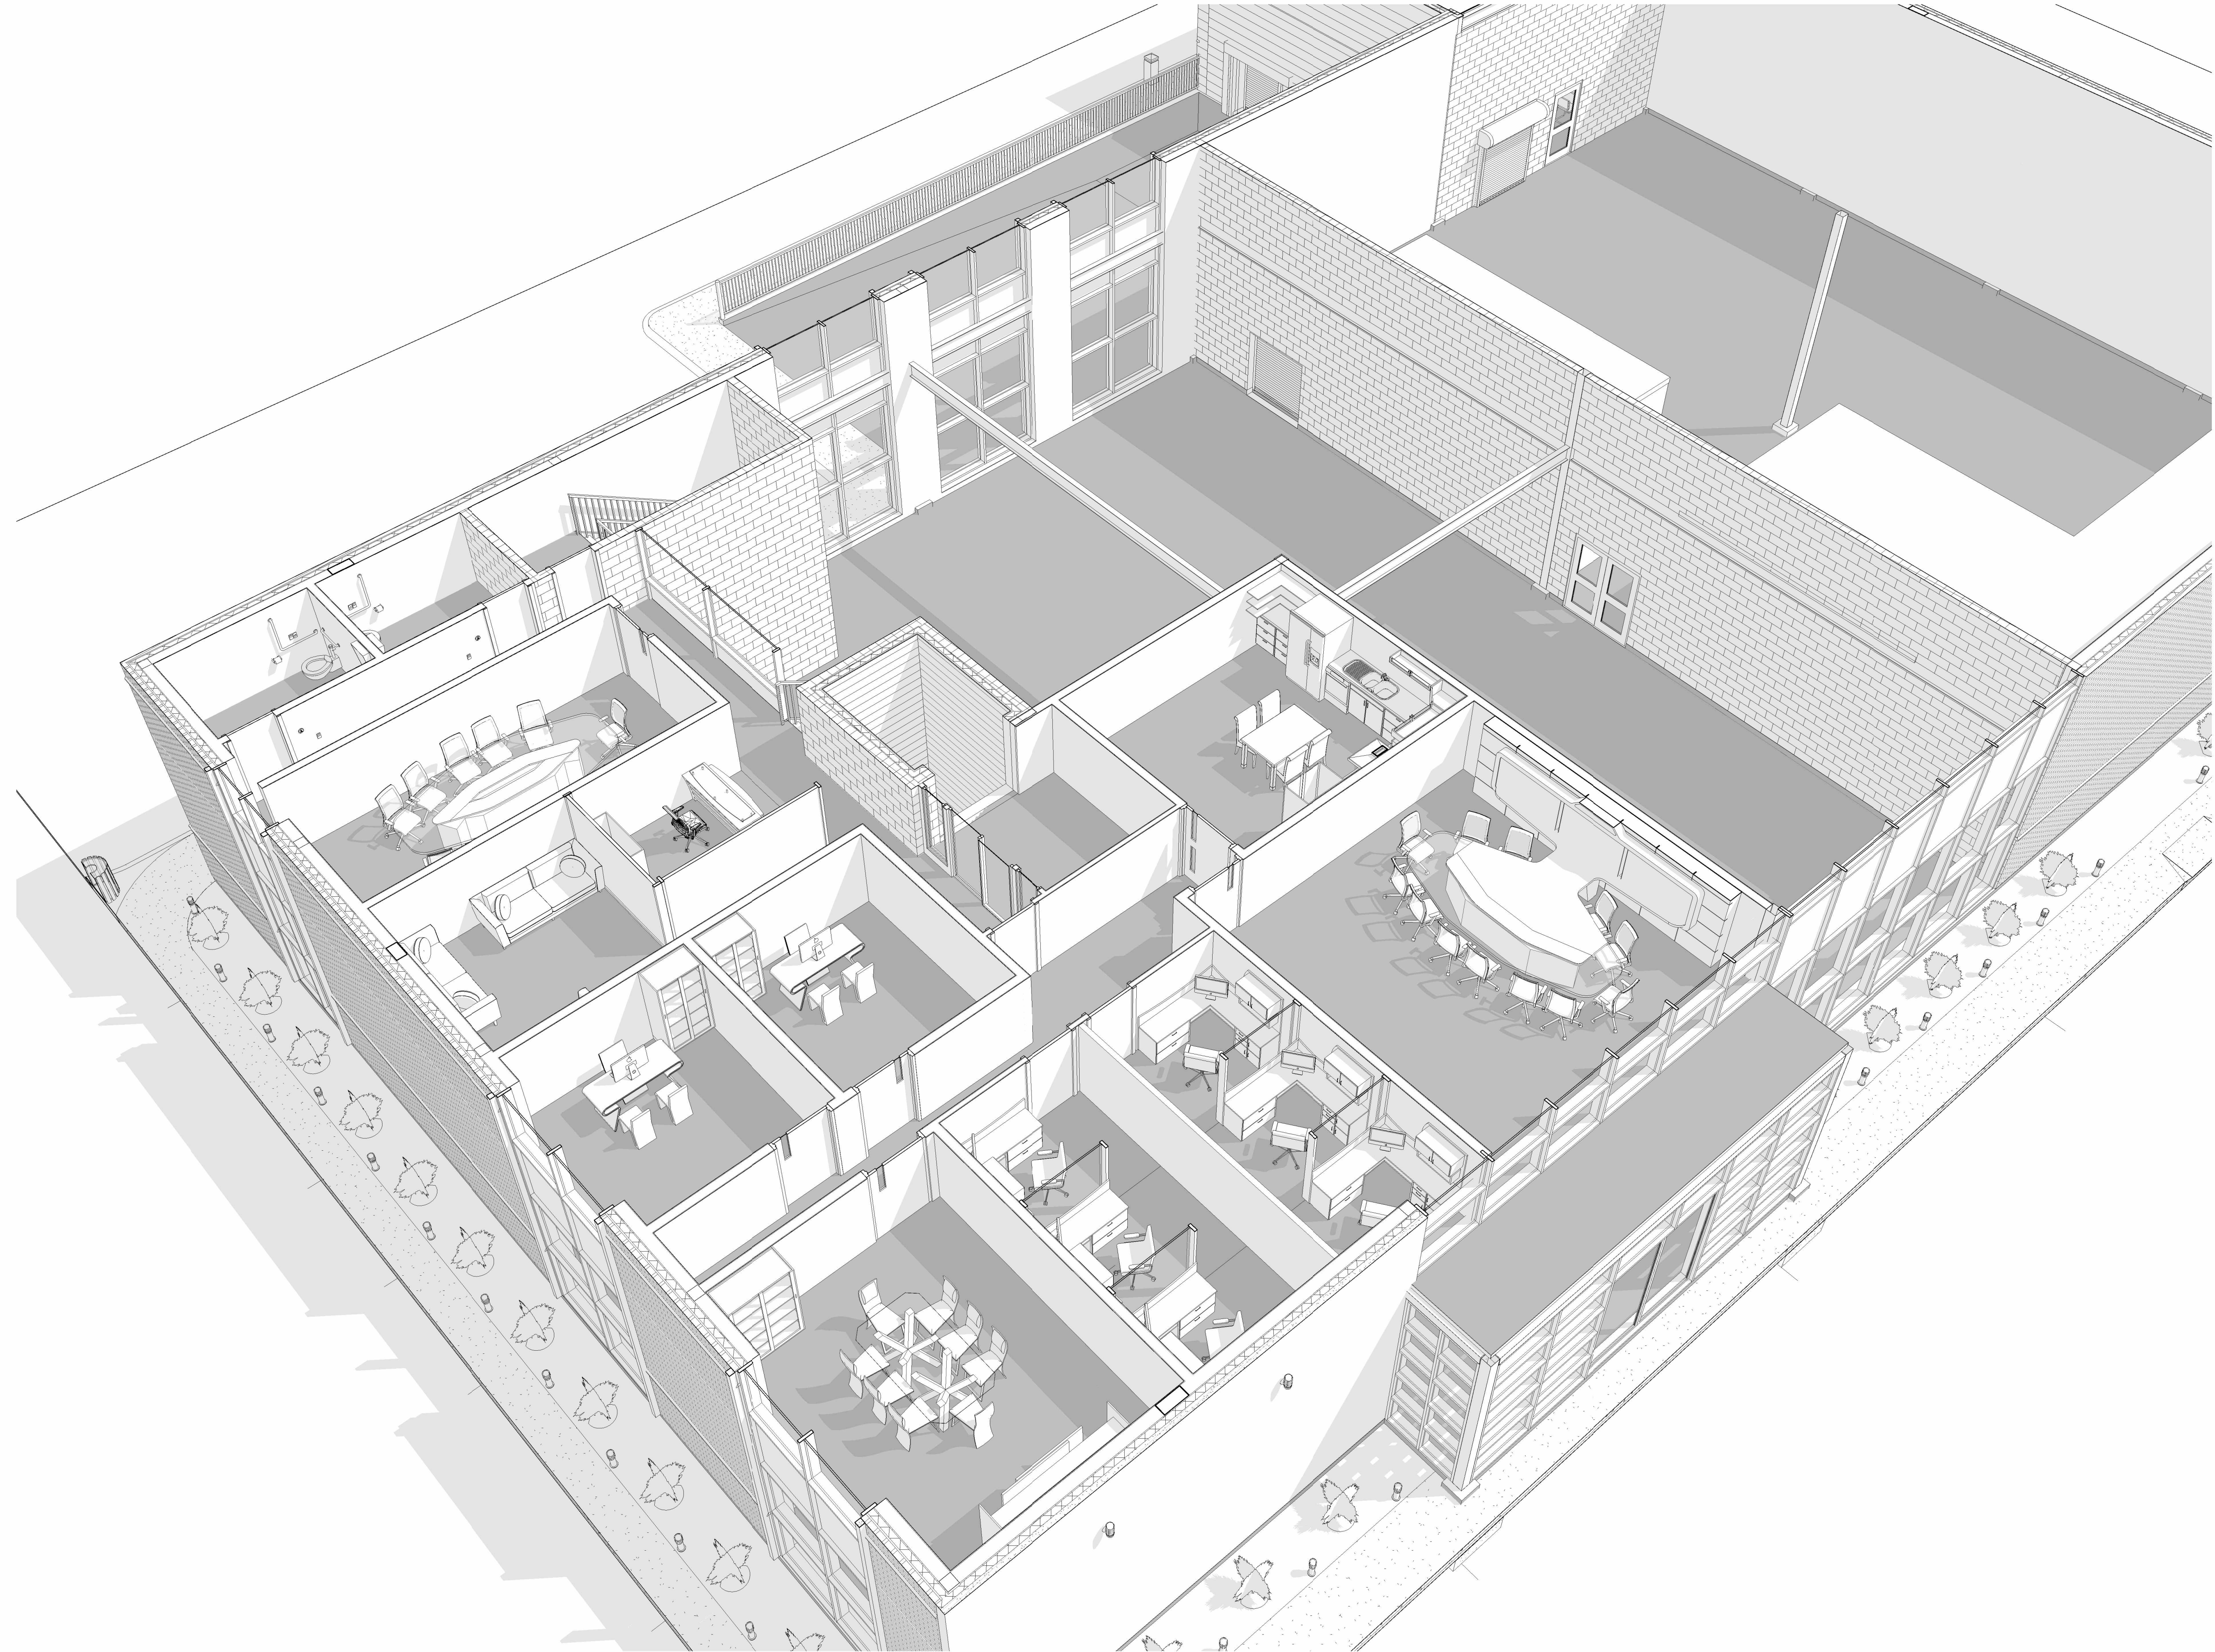

2401-RO1-1156DUNDASSTREET-LONDON-PROJECT03-AN
1156DUNDASSTREET-LONDON

LEVEL 2 FLOOR ISO

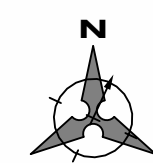

TWO STOREY COMMERCIAL



Architectural Technology



School of Building Technology

London Ontario Canada

AN 0001
D102-3

6/20/2024 6:22:40 PM

MATERIAL LEGENDS	
1	90 BRICK GRAY
2	CURTAIN WALL
3	BLACK ACP
4	GRAY METAL CLAD.

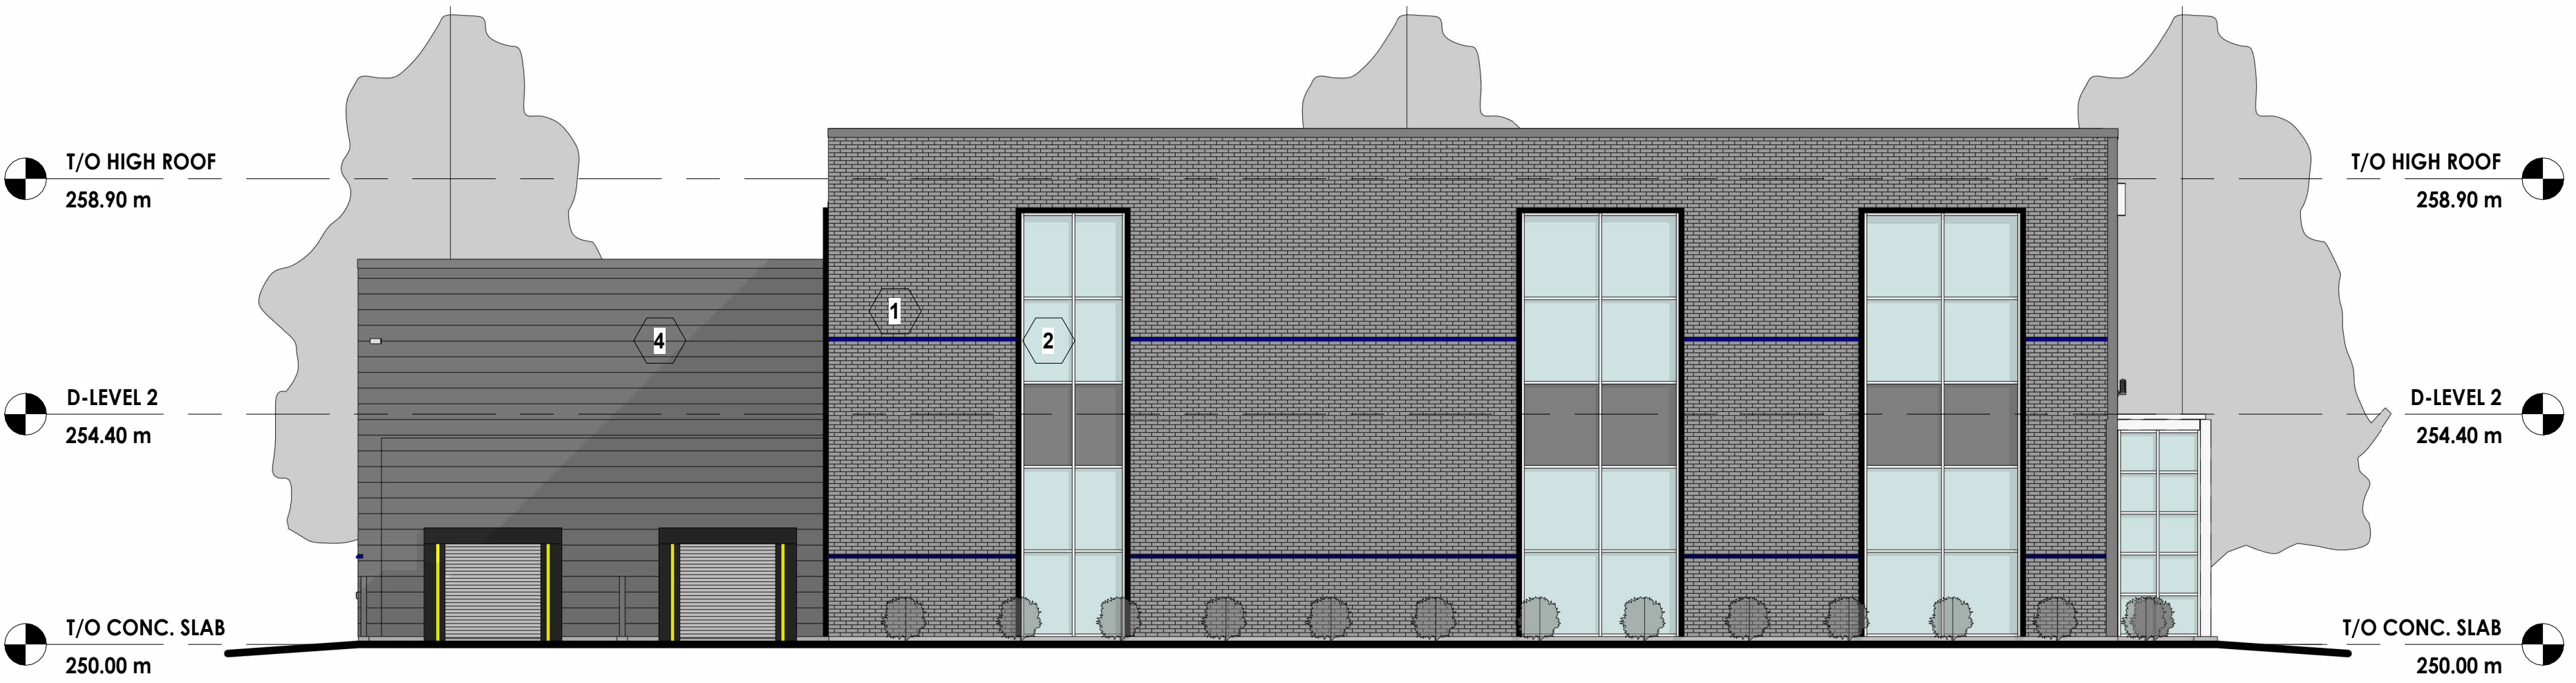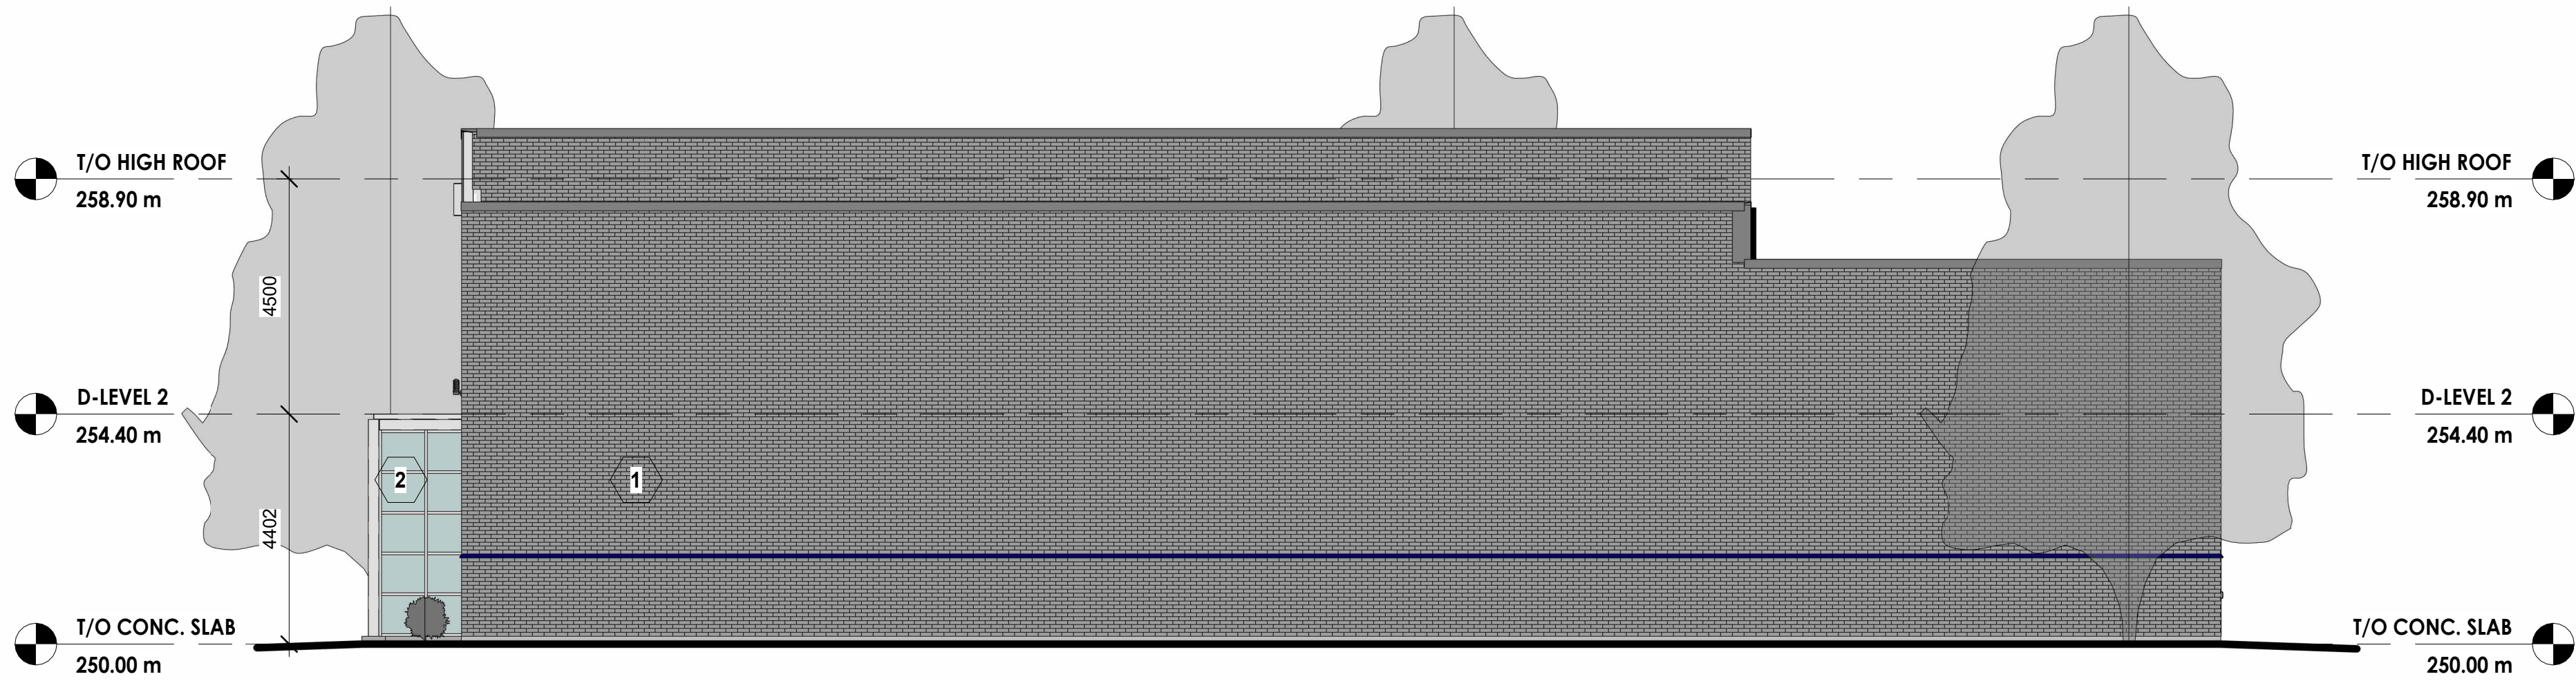

2401-RO1-1156DUNDASSTREET-LONDON-PROJECT03-AN
1156DUNDASSTREET-LONDON

ELEVATIONS

1 : 100



TWO STOREY COMMERCIAL



Architectural Technology


School of Building Technology

London Ontario Canada


AN 0001
D103

6/20/2024 6:22:54 PM

MATERIAL LEGENDS	
1	90 BRICK GRAY
2	CURTAIN WALL
3	BLACK ACP
4	GRAY METAL CLAD.

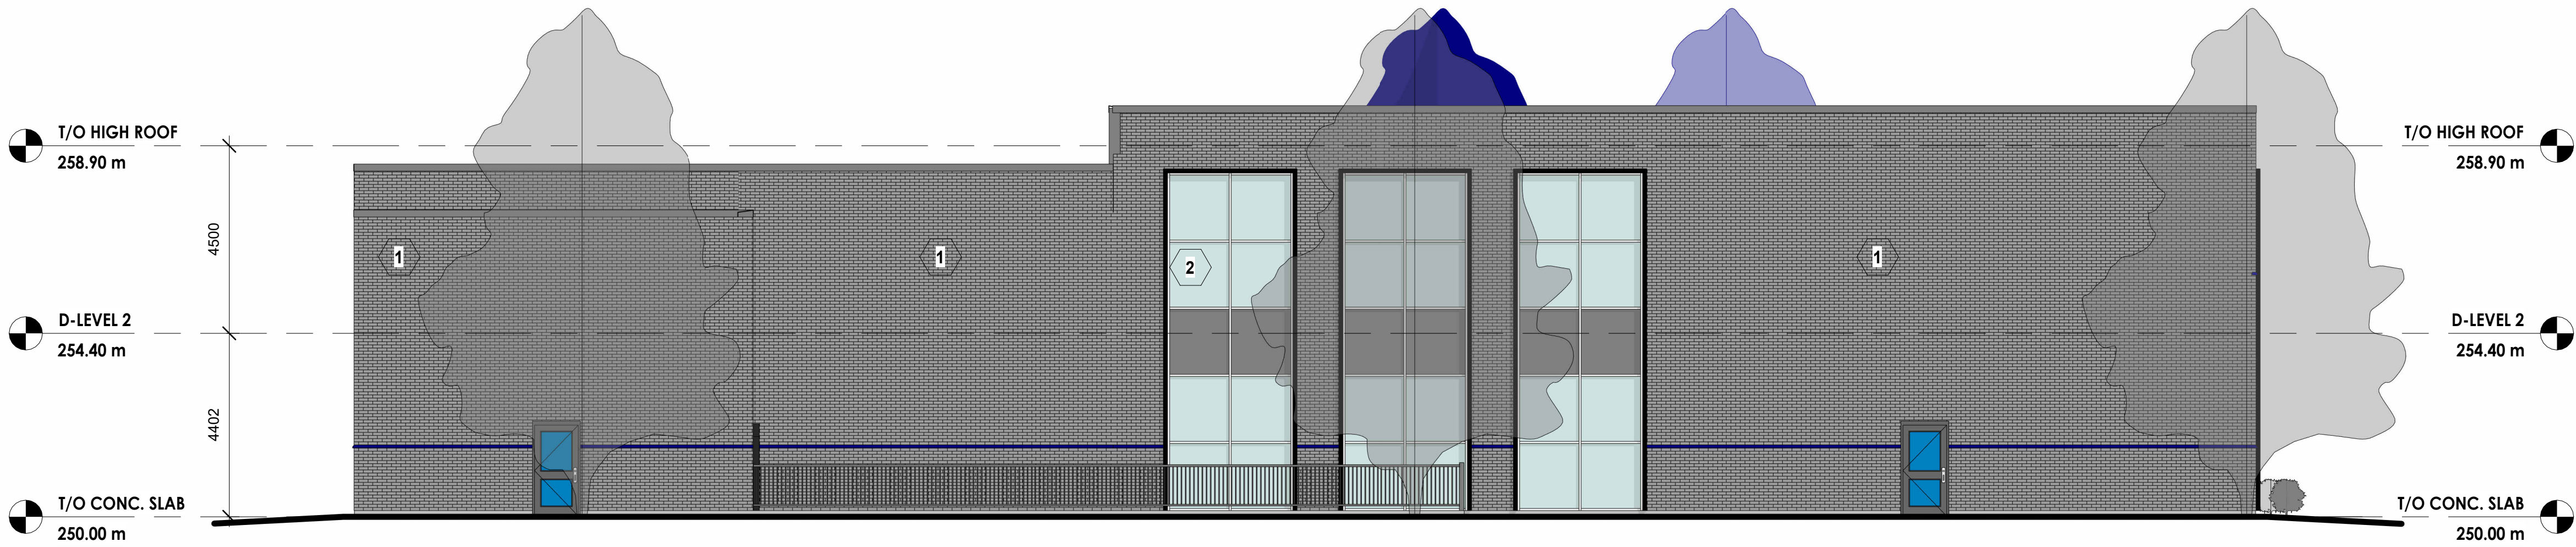

3 D-North
1 : 100

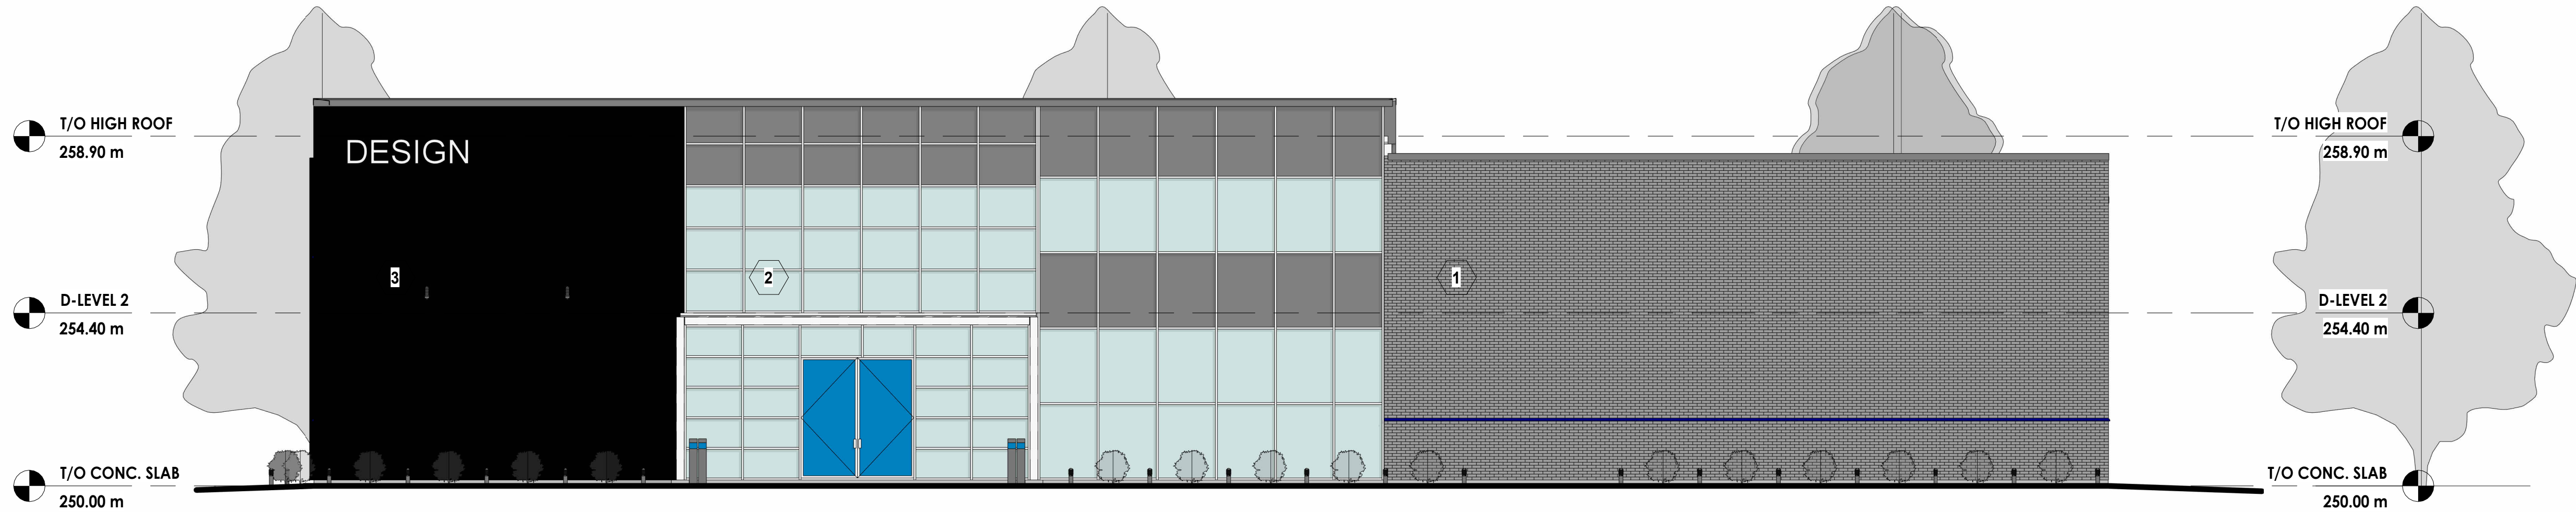

4 D-South
1 : 100

TWO STOREY COMMERCIAL

