



TWO STOREY COMMERCIAL
1156DUNDASSTREET-LONDON

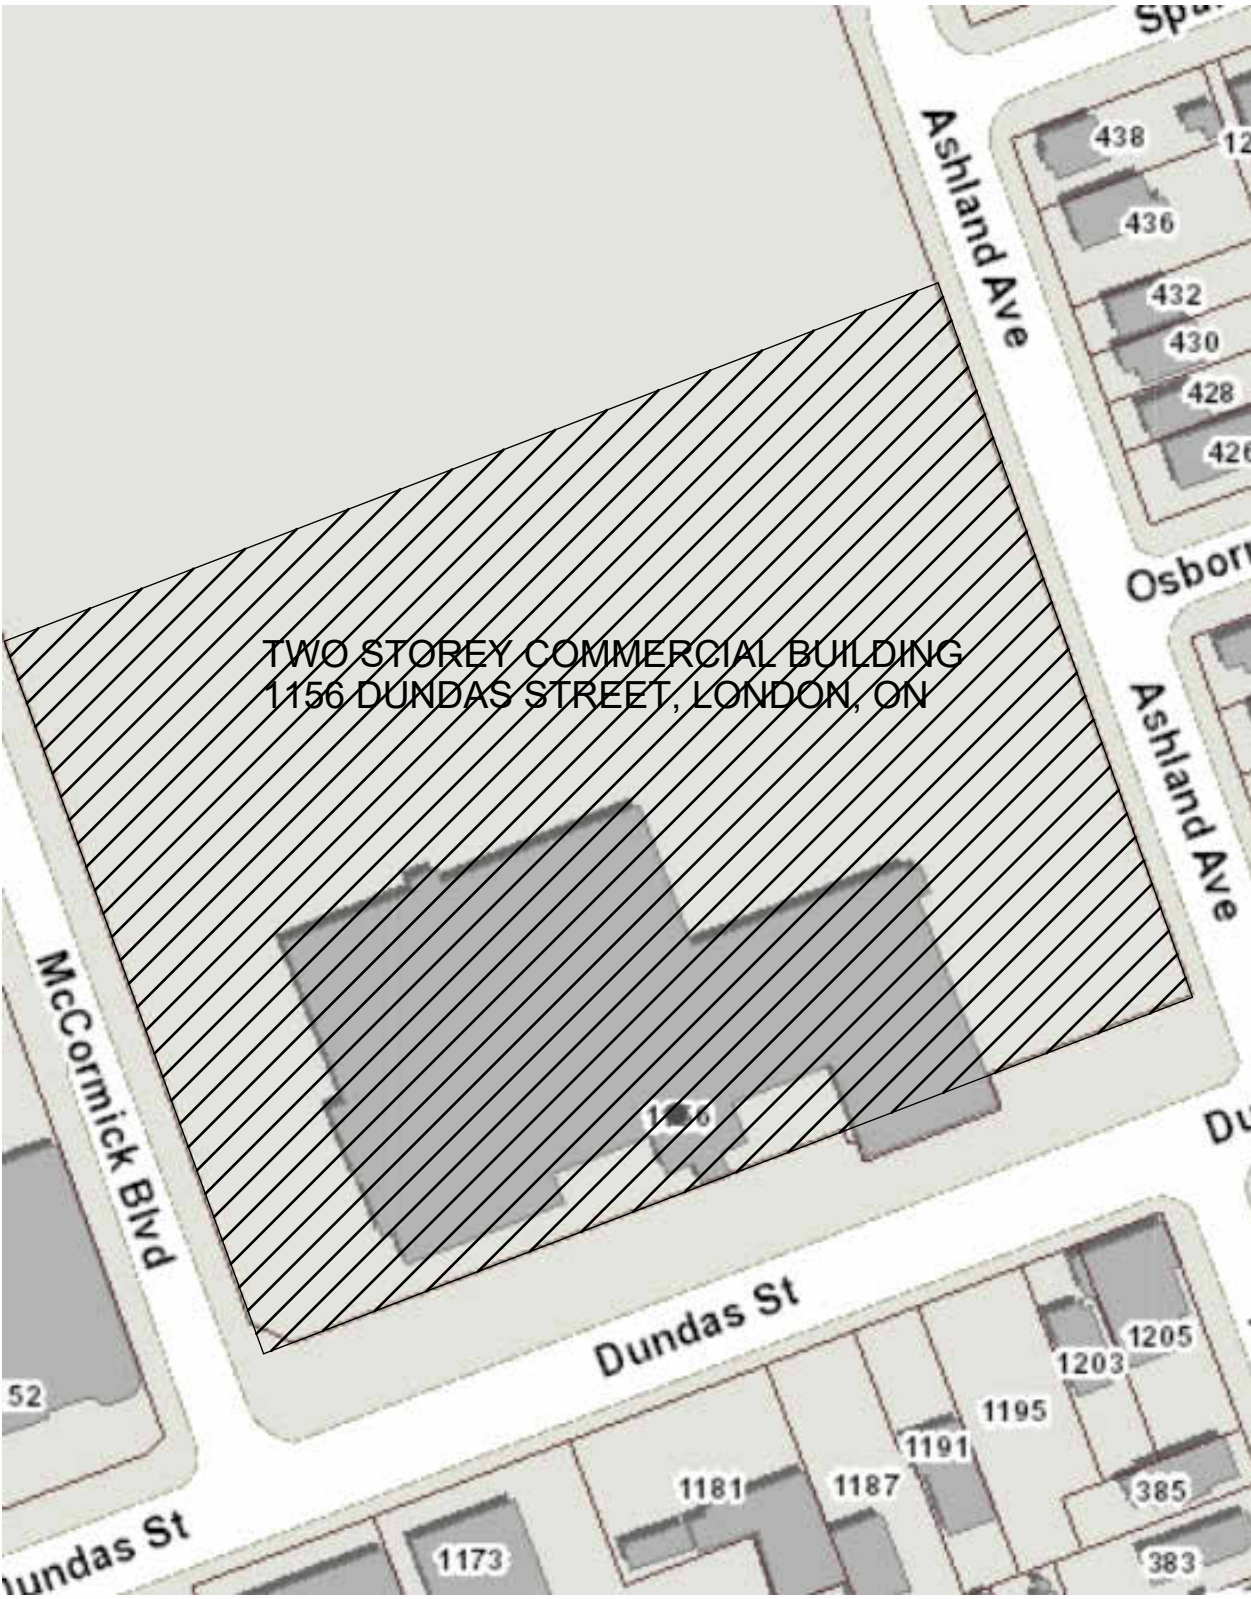

WD KEY PLAN
NTS.

WD Sheet List	
Sheet Name	Sheet Number
3D-ISO	A001
SITE PLAN	A100
MAIN FLOOR PLAN	A200
LEVEL 2 FLOOR PLAN	A201
ELEVATIONS	A300
ELEVATIONS	A301
ENLARGED STAIR PLAN & SECTION	A400
ENLARGED STAIR SECTION & 3D	A401
WALL SECTIONS	A500
DETAILS	A600









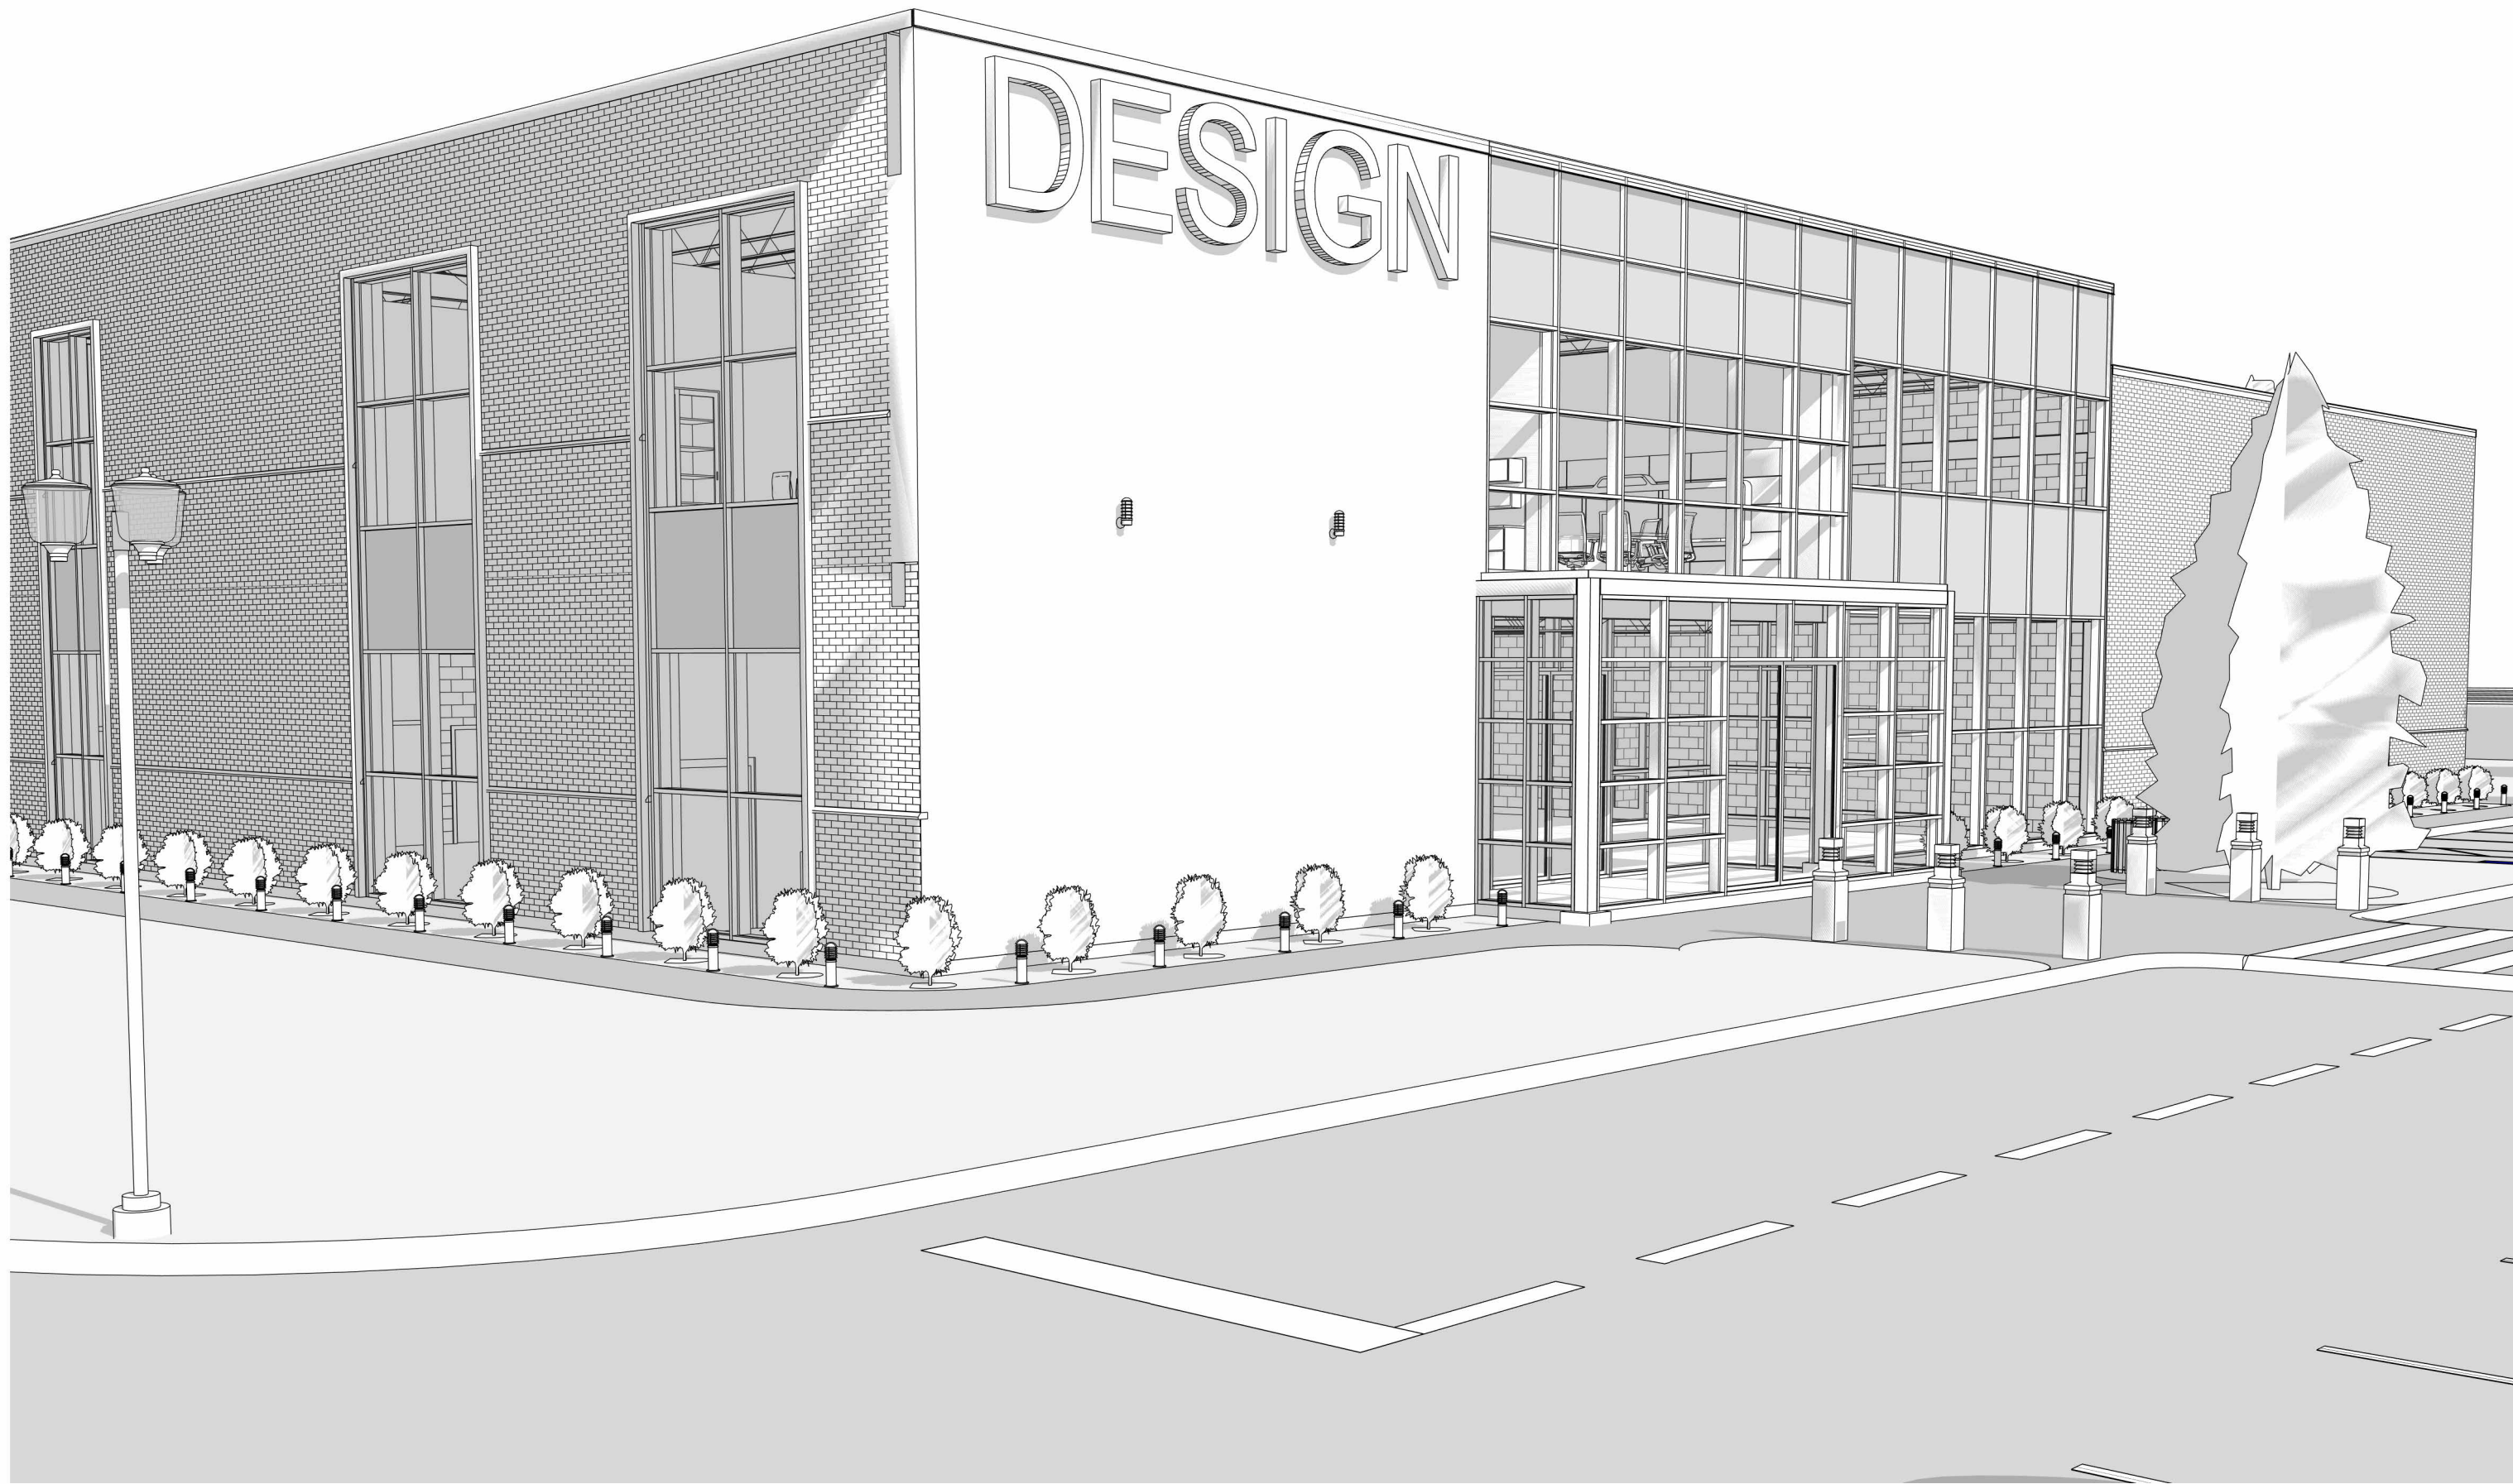


ABBREVIATIONS





CONC - CONCRETE	FOUND. - FOUNDATION	INT. - INTERIOR
C.I.P. - CAST IN PLACE	TYP. - TYPICAL	EXT. - EXTERIOR
hrs. - HOURS	hrs. - HOURS	COR. - CORNER
C/W - COMES WITH	C/W - COMES WITH	MASO. - MASONRY
ACP - ALUMINIUM COMPOSITE PANEL	PARA. - PARAPET	CONN. - CONNECTION
CMU - CONCRETE MASONRY UNIT	SEC. - SECTION	F.S. - FIRE SEPERATION
O/C - ON CENTRE	DET. - DETAIL	T.P.O. - THERMPLASTIC POLYOLEFIN

ASSEMBLIES

WALL ASSEMBLIES

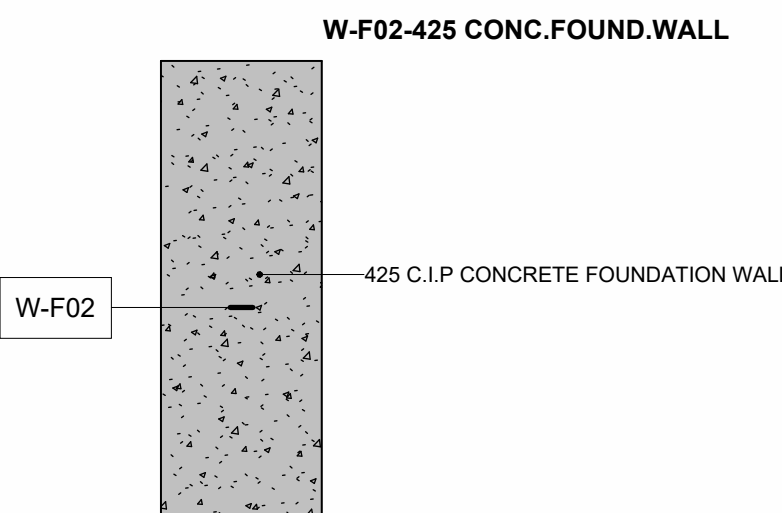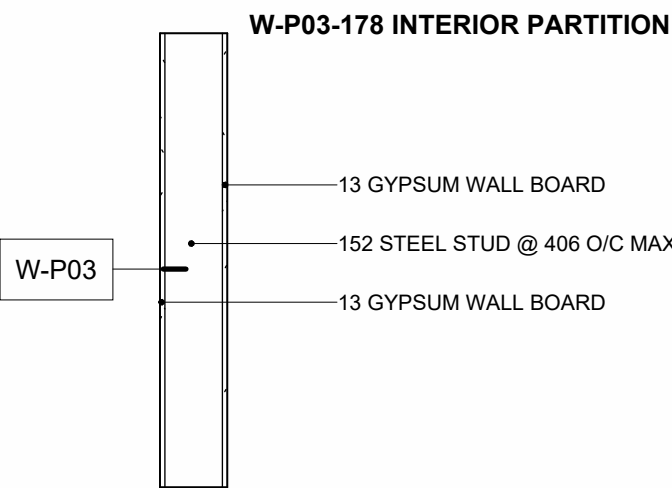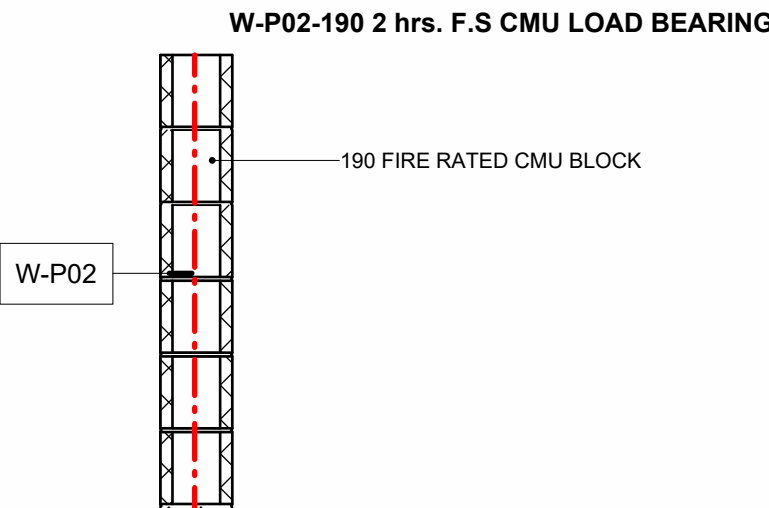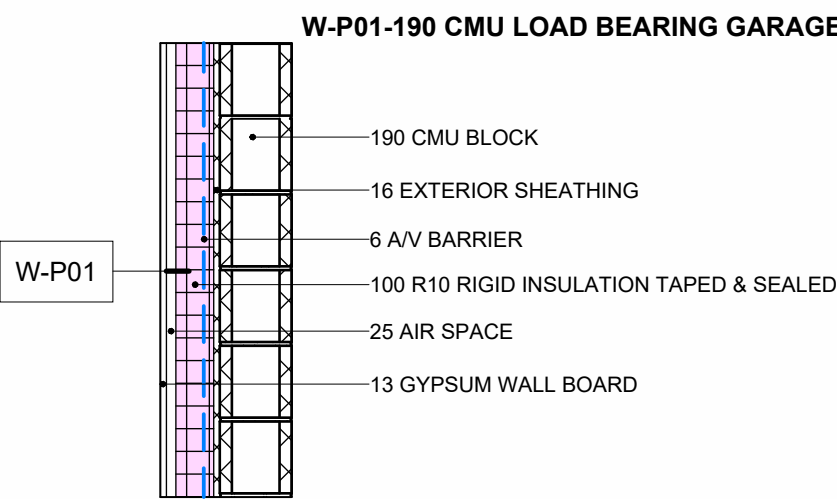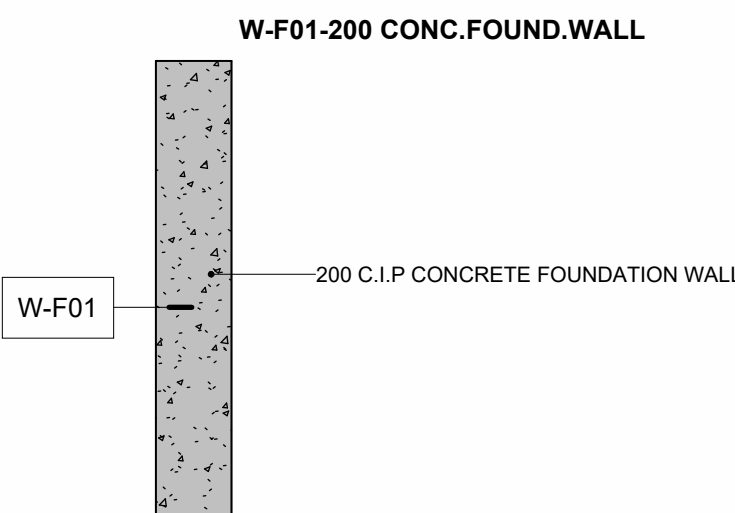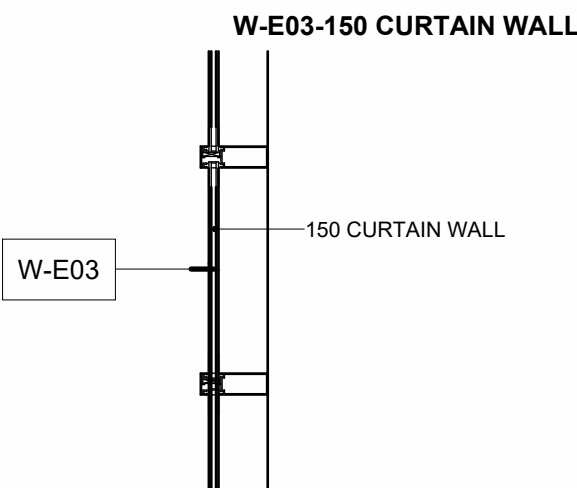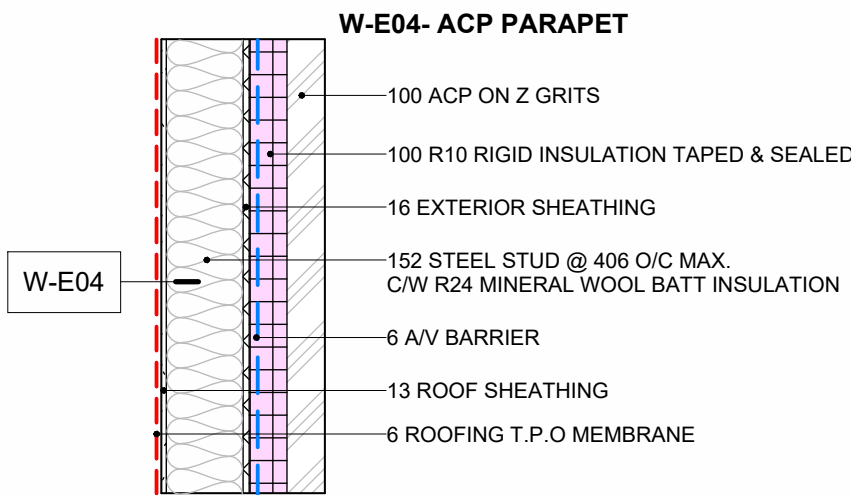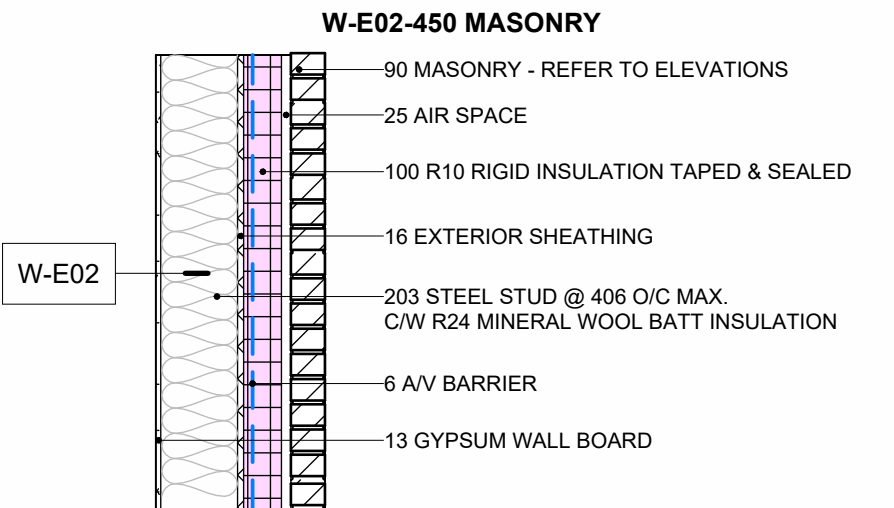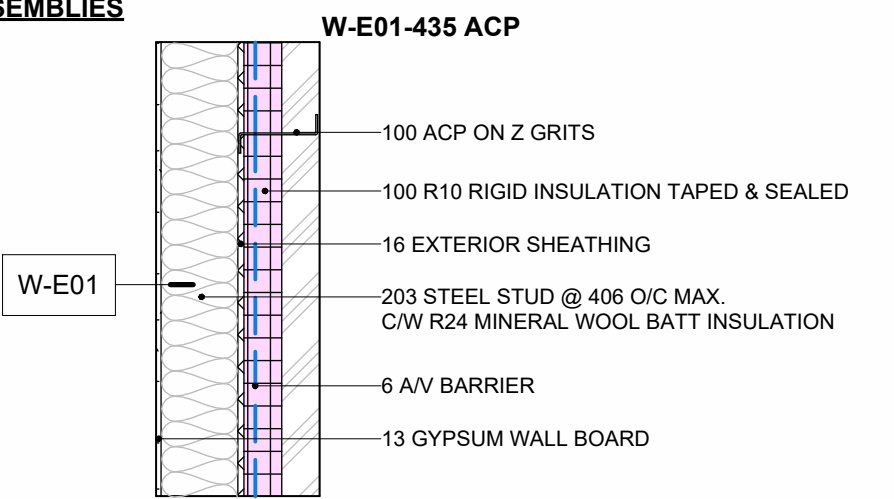

FLOOR ASSEMBLIES

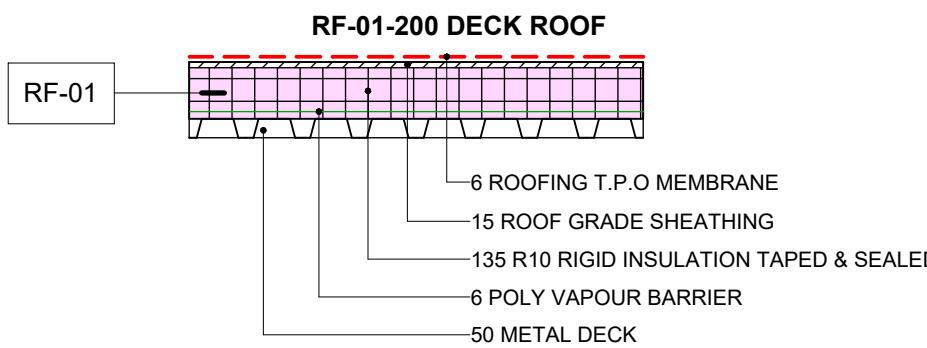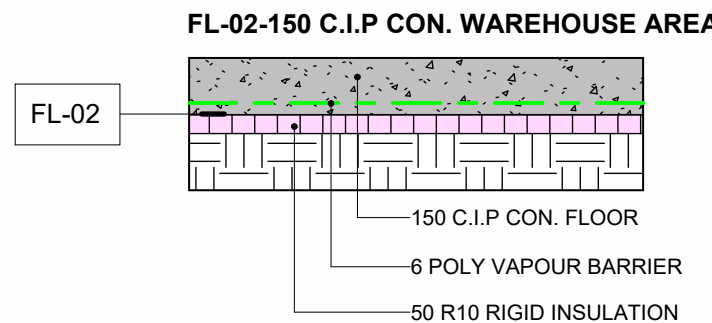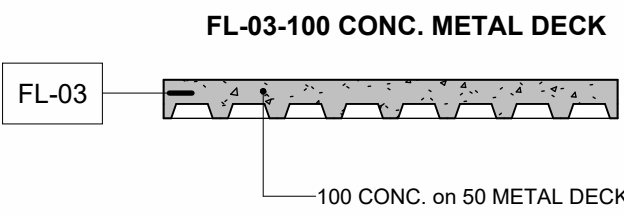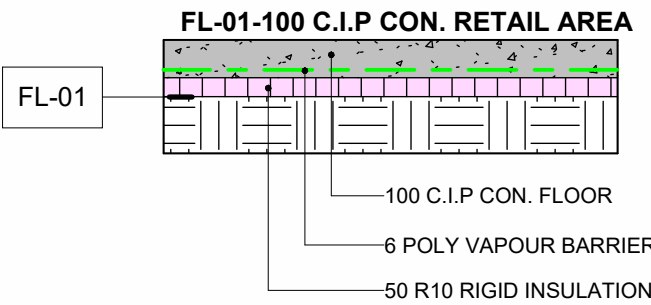

NOTES

VAPOUR BARRIER	---
A/V BARRIER	---
T.P.O ROOF MEMBRANE	---

PRELIMINARY
NOT FOR CONSTRUCTION



PROJECT TITLE
TWO STOREY COMMERCIAL BUILDING

CLIENT:
AFNM
PROJECT ADDRESS
1156DUNDASSTREET-LONDON

DRAWING TITLE
COVER PAGE

CHECKED LV | DRAWN AN | DATE 08/21/24

2401 PROJECT No. | A000 DRAWING

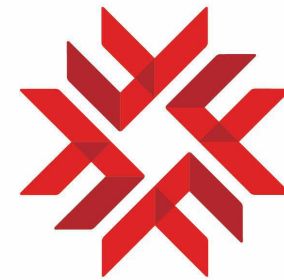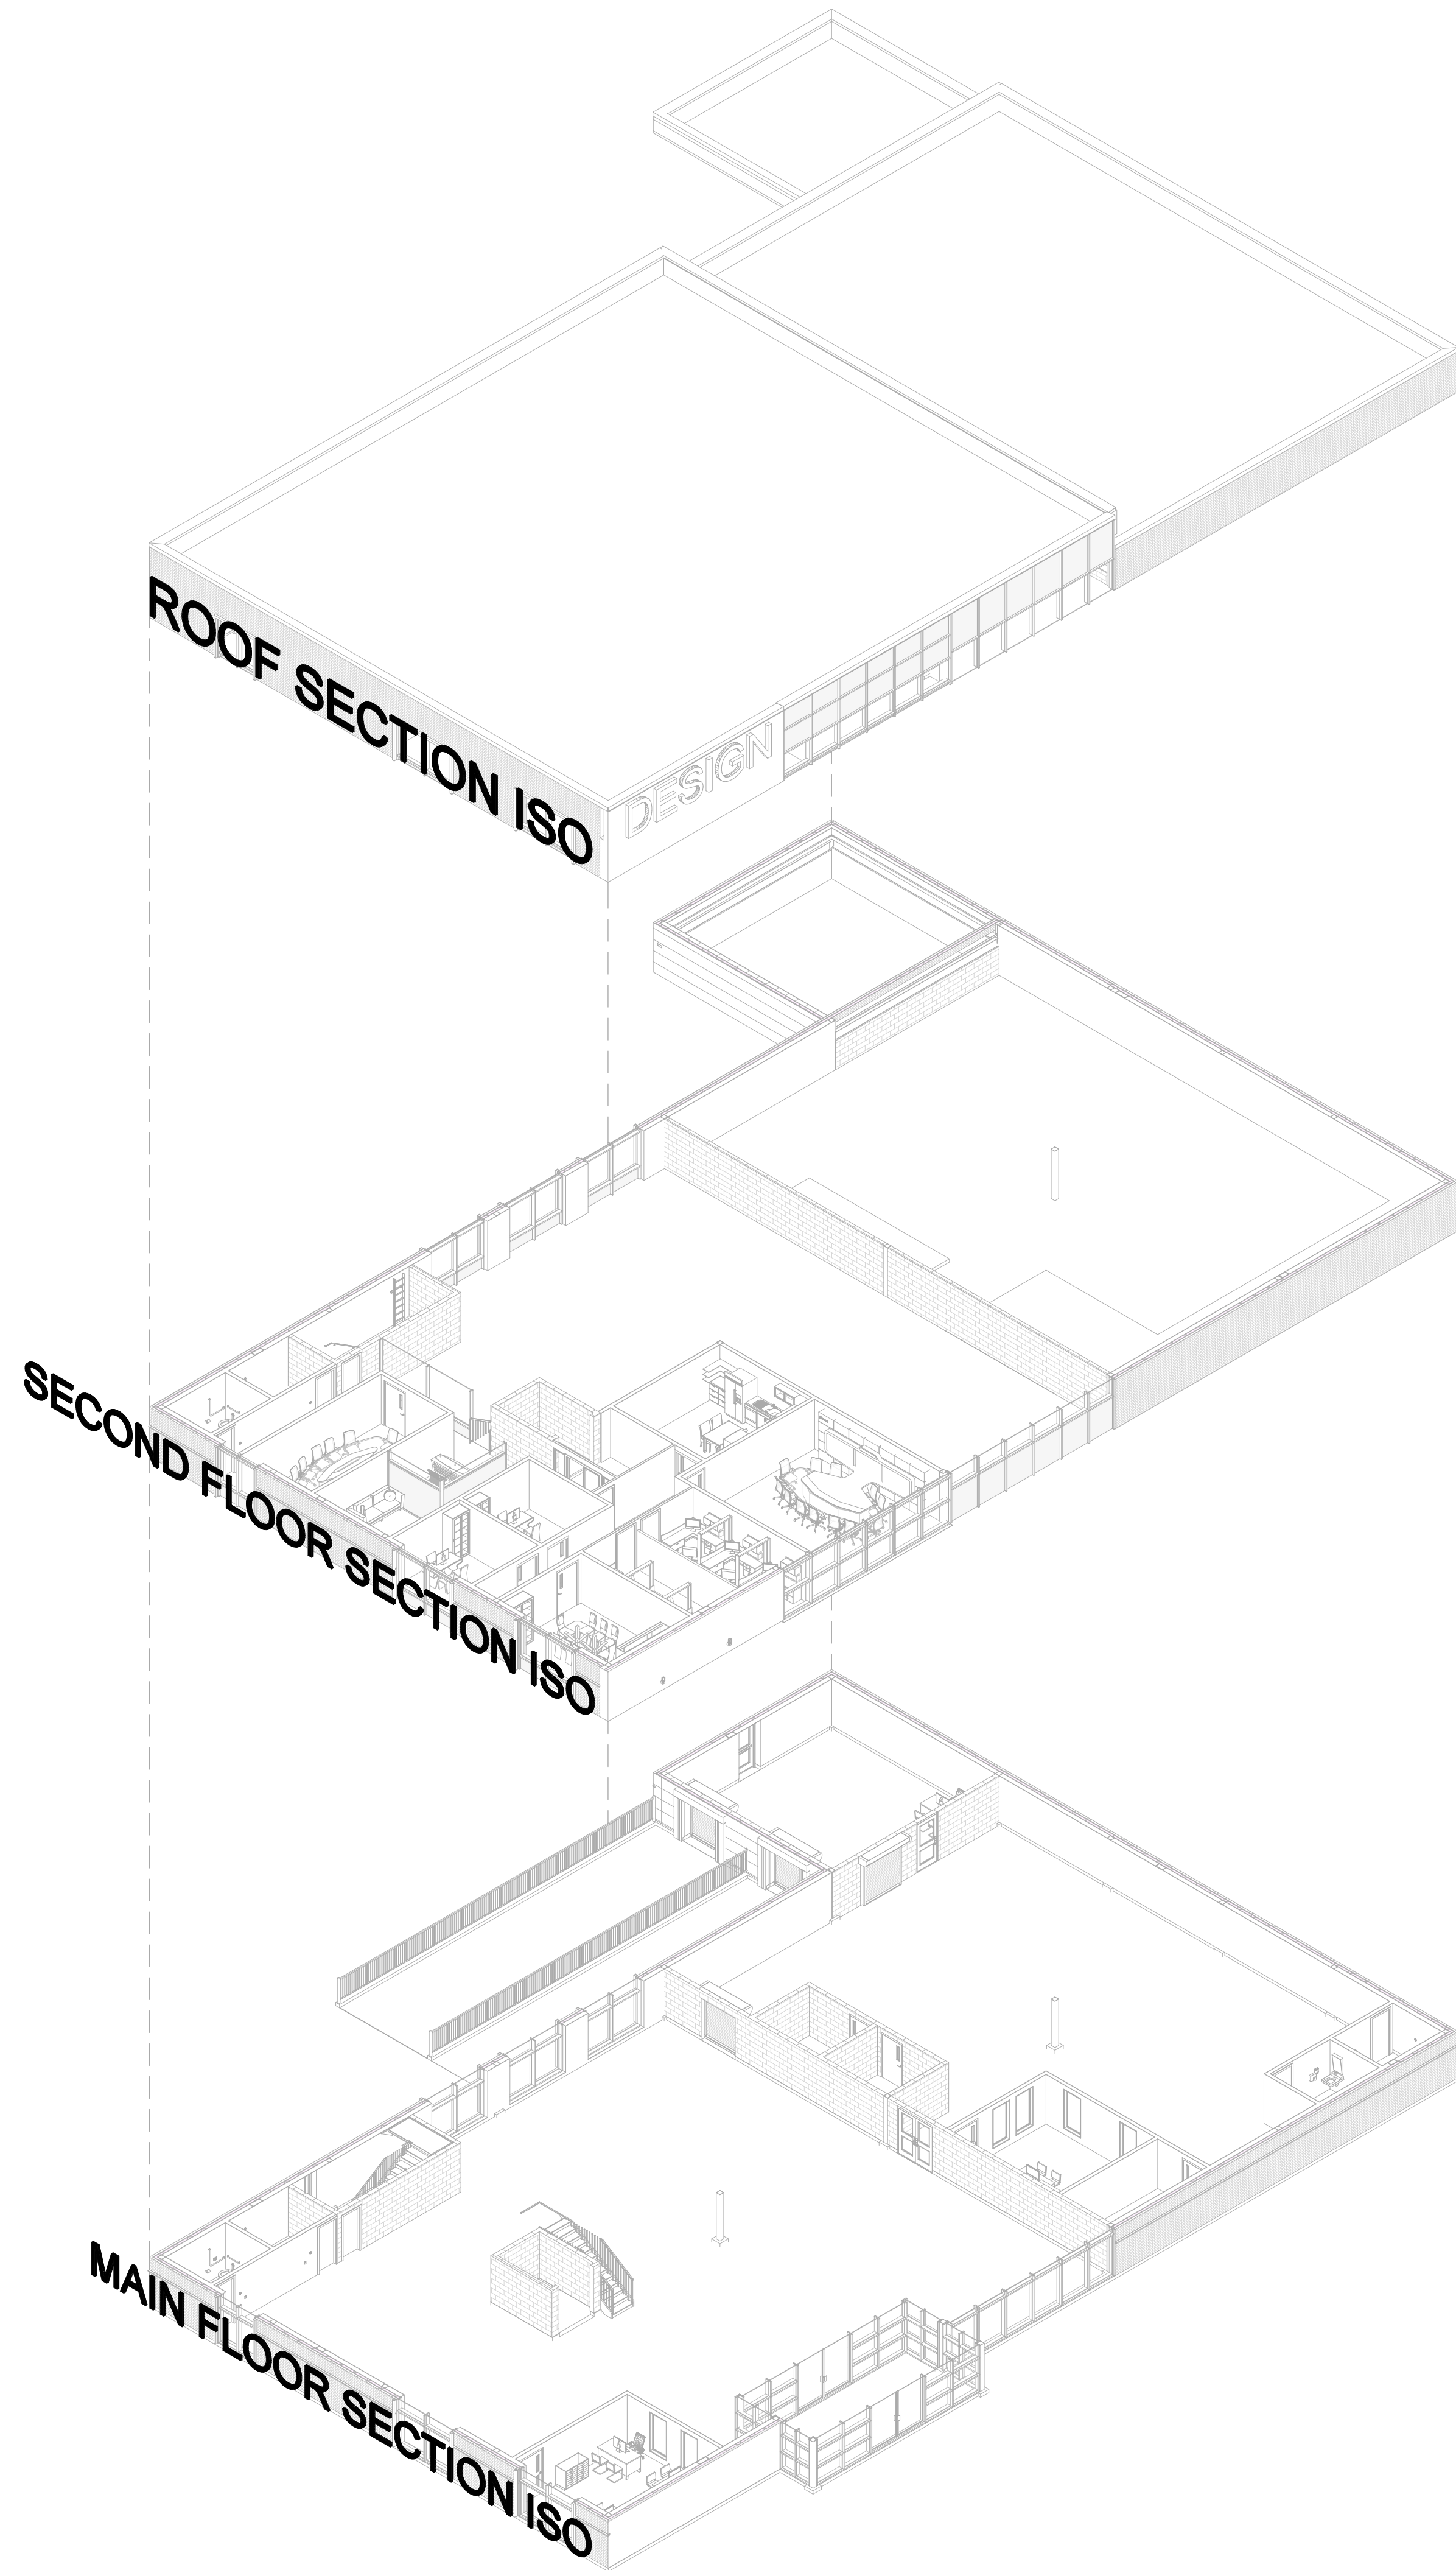

FANSHAWE
DONALD J. SMITH
SCHOOL OF BUILDING
TECHNOLOGY

NOTES

**PRELIMINARY
NOT FOR CONSTRUCTION**

PROJECT TITLE

**TWO STOREY
COMMERCIAL
BUILDING**

CLIENT:

AFNM

PROJECT ADDRESS

1156DUNDASSTREET-LONDON

DRAWING TITLE

3D-ISO

CHECKED | DRAWN
Checker Author

DATE
08/20/24

2401

PROJECT No.

A001


DRAWING

D:\SEM-3\DESIGN - 03\PROJECT
FILE\3\SUPERSEDED\WD-FINAL\2401-RO9-1156DUNDASSTREET-LONDON-PROJECT03-AN.rvt

8/20/2024 10:52:46 PM


ZONE: CSA2	ALLOWABLE	PROVIDED
LOT AREA (MIN):	17987.649 m²	17987.649 m²
LOT FRONTAGE (MIN):	30.0 m	176.4 m
LOT DEPTH (MIN):	30.0 m	102.0 m
FRONT & EXTERIOR SIDE YARD SETBACK (MIN):	8.0 m	8.0 m
REAR & INTERIOR SIDE YARD SETBACK (MIN):	8.0 m	8.0 m
LANDSCAPED AREA (MIN):	1798.7649 m²	13996.7 m²
LANDSCAPED AREA (MAX):	5396.2947 m²	1227.3 m²
BUILDING HEIGHT (MAX):	9.00 m	8.00 m
GROSS FLOOR AREA - GFA - (MAX):	10000 m²	1558 m²
GFA FOR OFFICE USE (MAX):	1500 m²	15%
GFA FOR COMMERCIAL AND PRIVATE SCHOOL USE (MAX):	1500 m²	15%
GFA FOR CINEMAS USE (MAX):	1000 m²	0 m²
PARKING REQUIREMENT:	0 SPACES	27 SPACES

SITE LEGENDS						
	PROPOSED TREE	FENSE	TRASH CAN	BOLLARD	STREET LIGHT	PLANTS
	EXISTING TREE	HYDRO POLE	STOP SIGN	BARRIER FREE	CONC. SIDEWALK	TREES
	DEMOLISH TREE	CROSSWALK	TRASH CAN	MAIN ENTRANCE	ASPHALT	TRUCK ROUTE
		MOLOK	FIRE ROUTE	SECONDARY ENTRY / EXIT	SOD	FIRE ROUTE

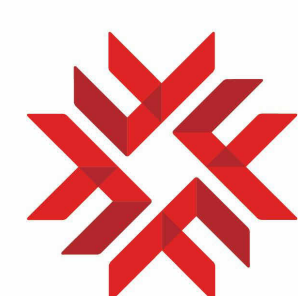

FANSHAWE
DONALD J. SMITH
SCHOOL OF BUILDING
TECHNOLOGY

NOTES

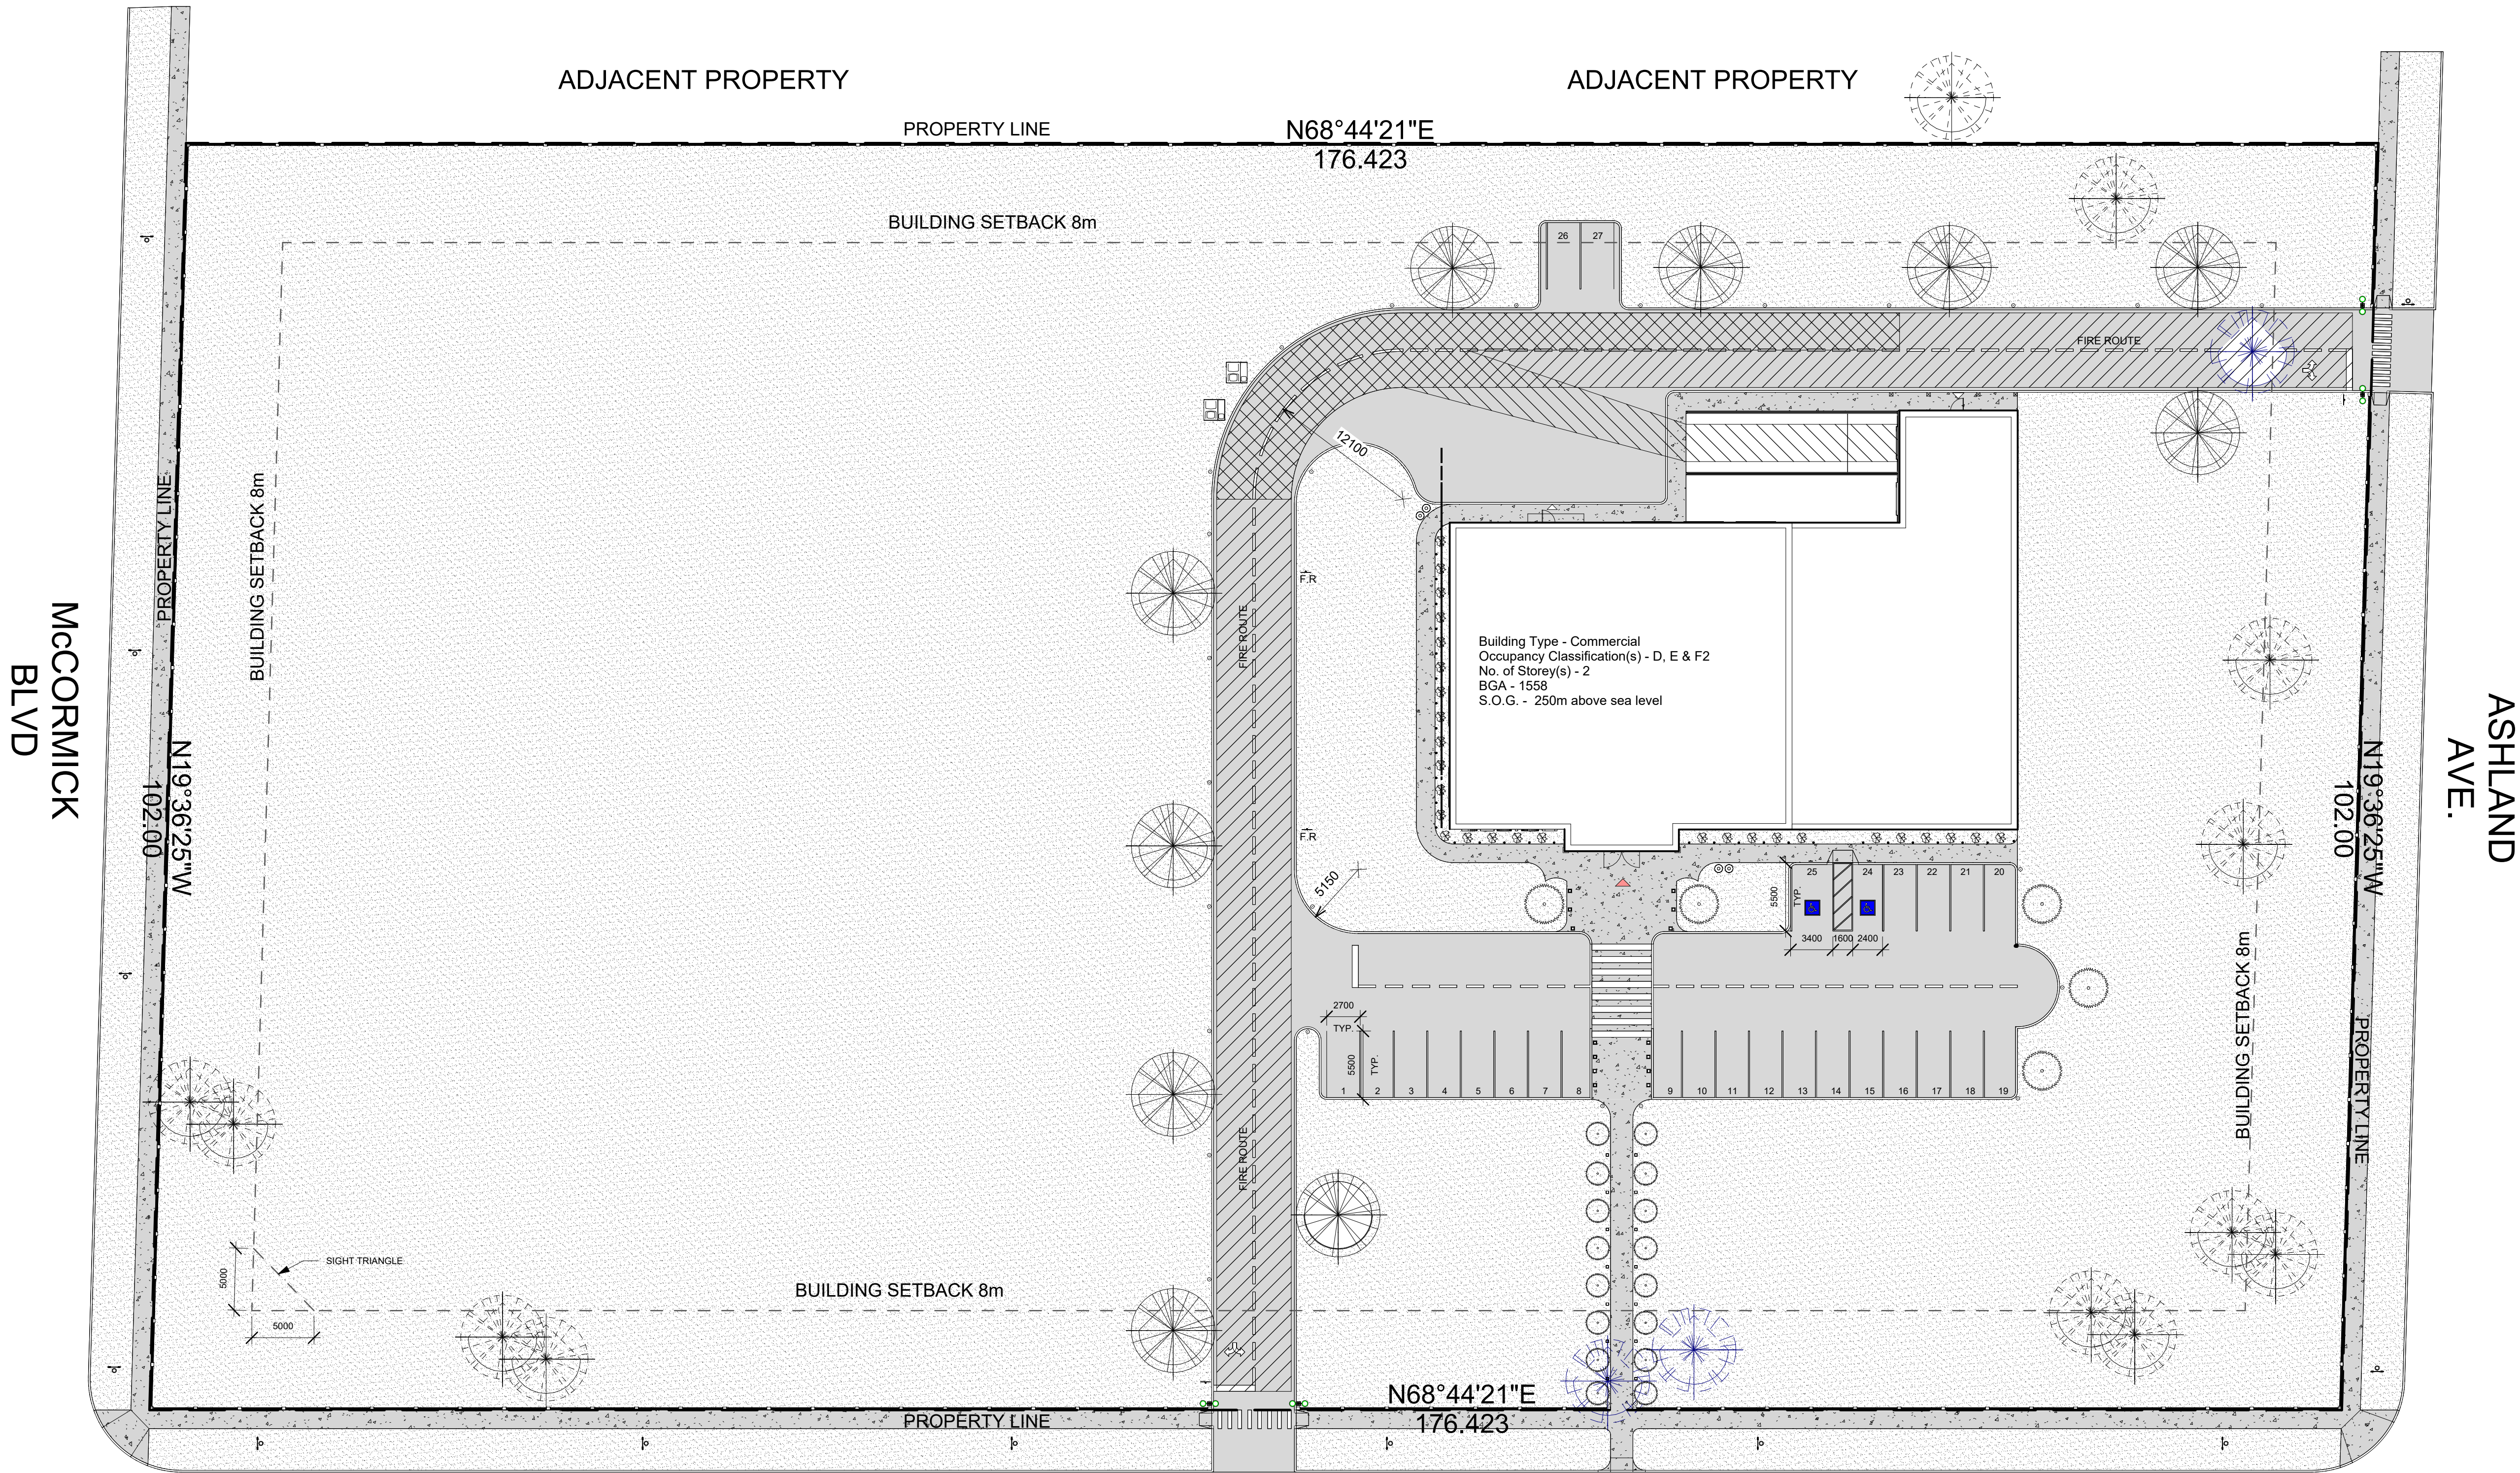

PRELIMINARY
NOT FOR CONSTRUCTION

PROJECT TITLE
**TWO STOREY
COMMERCIAL
BUILDING**

CLIENT:
AFNM

PROJECT ADDRESS
1156DUNDASSTREET-LONDON

DRAWING TITLE
SITE PLAN

CHECKED
LV

DRAWN
AN

DATE
08/21/24

PROJECT No.
2401

DRAWING
A100

NOTES

**PRELIMINARY
NOT FOR CONSTRUCTION**

PROJECT TITLE
**TWO STOREY
COMMERCIAL
BUILDING**

CLIENT:
AFNM


PROJECT ADDRESS
1156DUNDASSTREET-LONDON

DRAWING TITLE
MAIN FLOOR PLAN

CHECKED LV | DRAWN AN | DATE 08/21/24

2401
PROJECT No.

A200
DRAWING

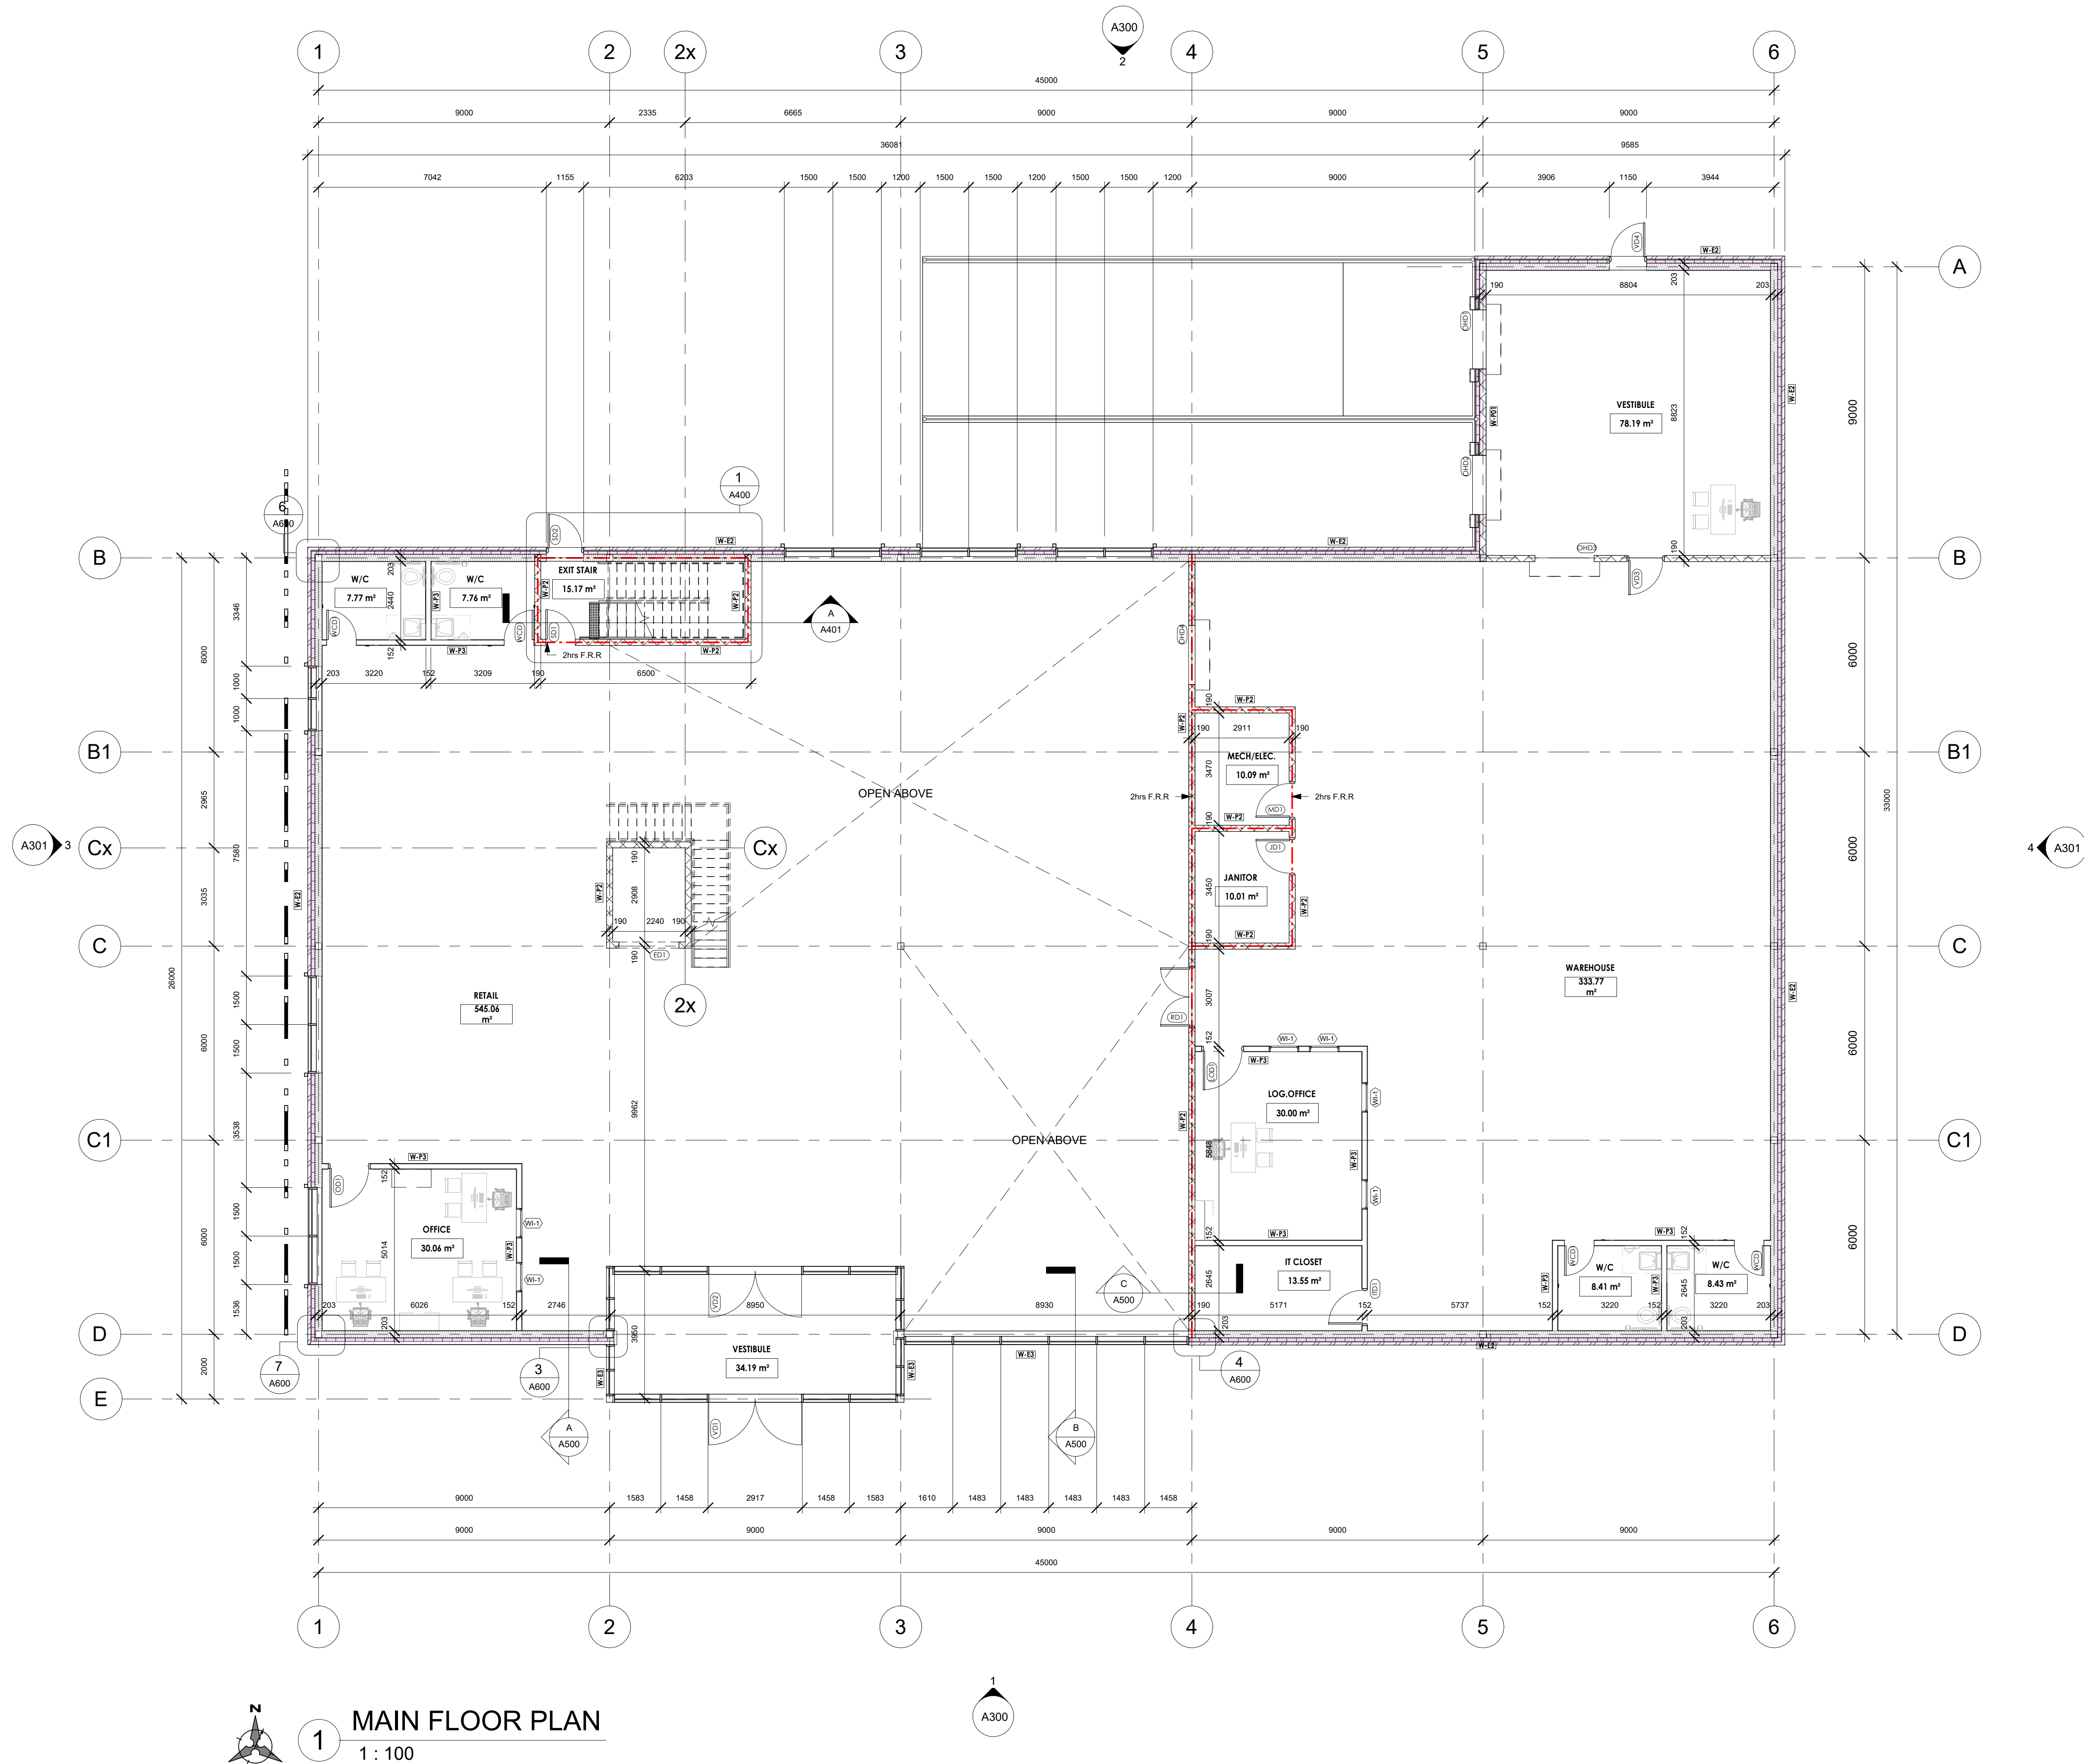

1 MAIN FLOOR PLAN
1 : 200

NOTES

PRELIMINARY
NOT FOR CONSTRUCTION

PROJECT TITLE
**TWO STOREY
COMMERCIAL
BUILDING**


CLIENT:
AFNM


PROJECT ADDRESS
1156DUNDASSTREET-LONDON

DRAWING TITLE
LEVEL 2 FLOOR PLAN

CHECKED | DRAWN | DATE
LV | AN | 08/21/24


2401 | A201
PROJECT No. | DRAWING

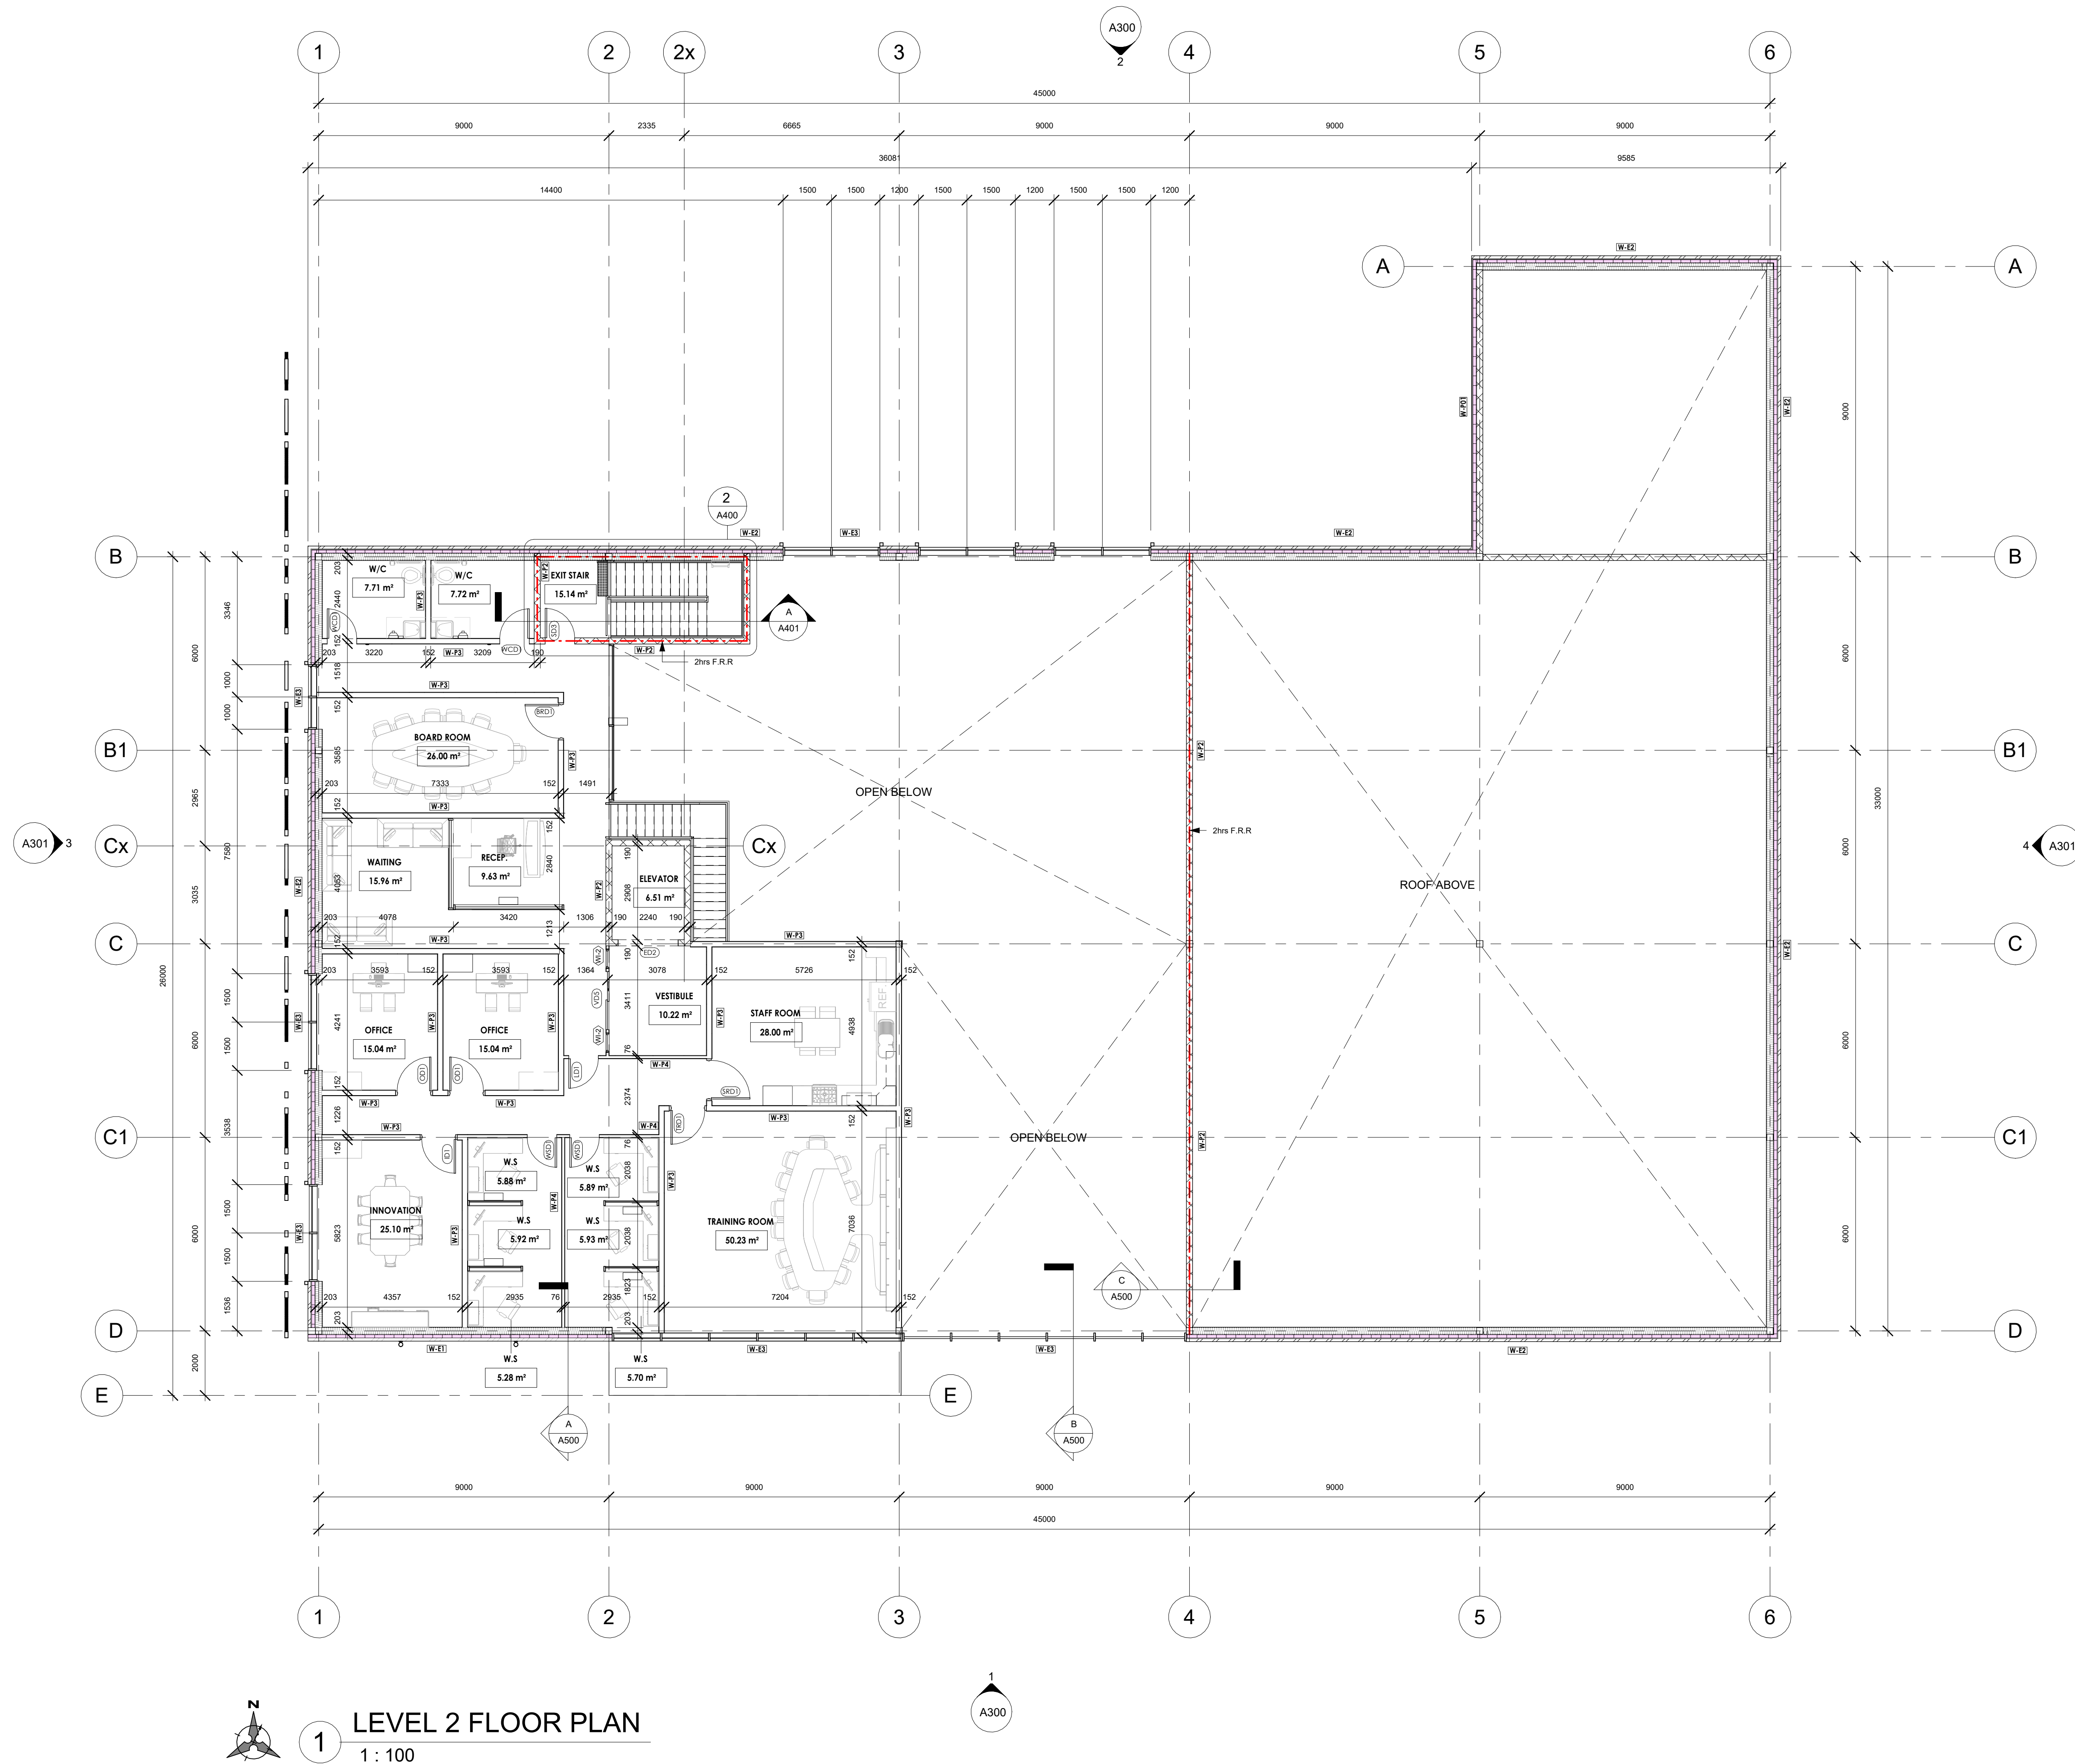

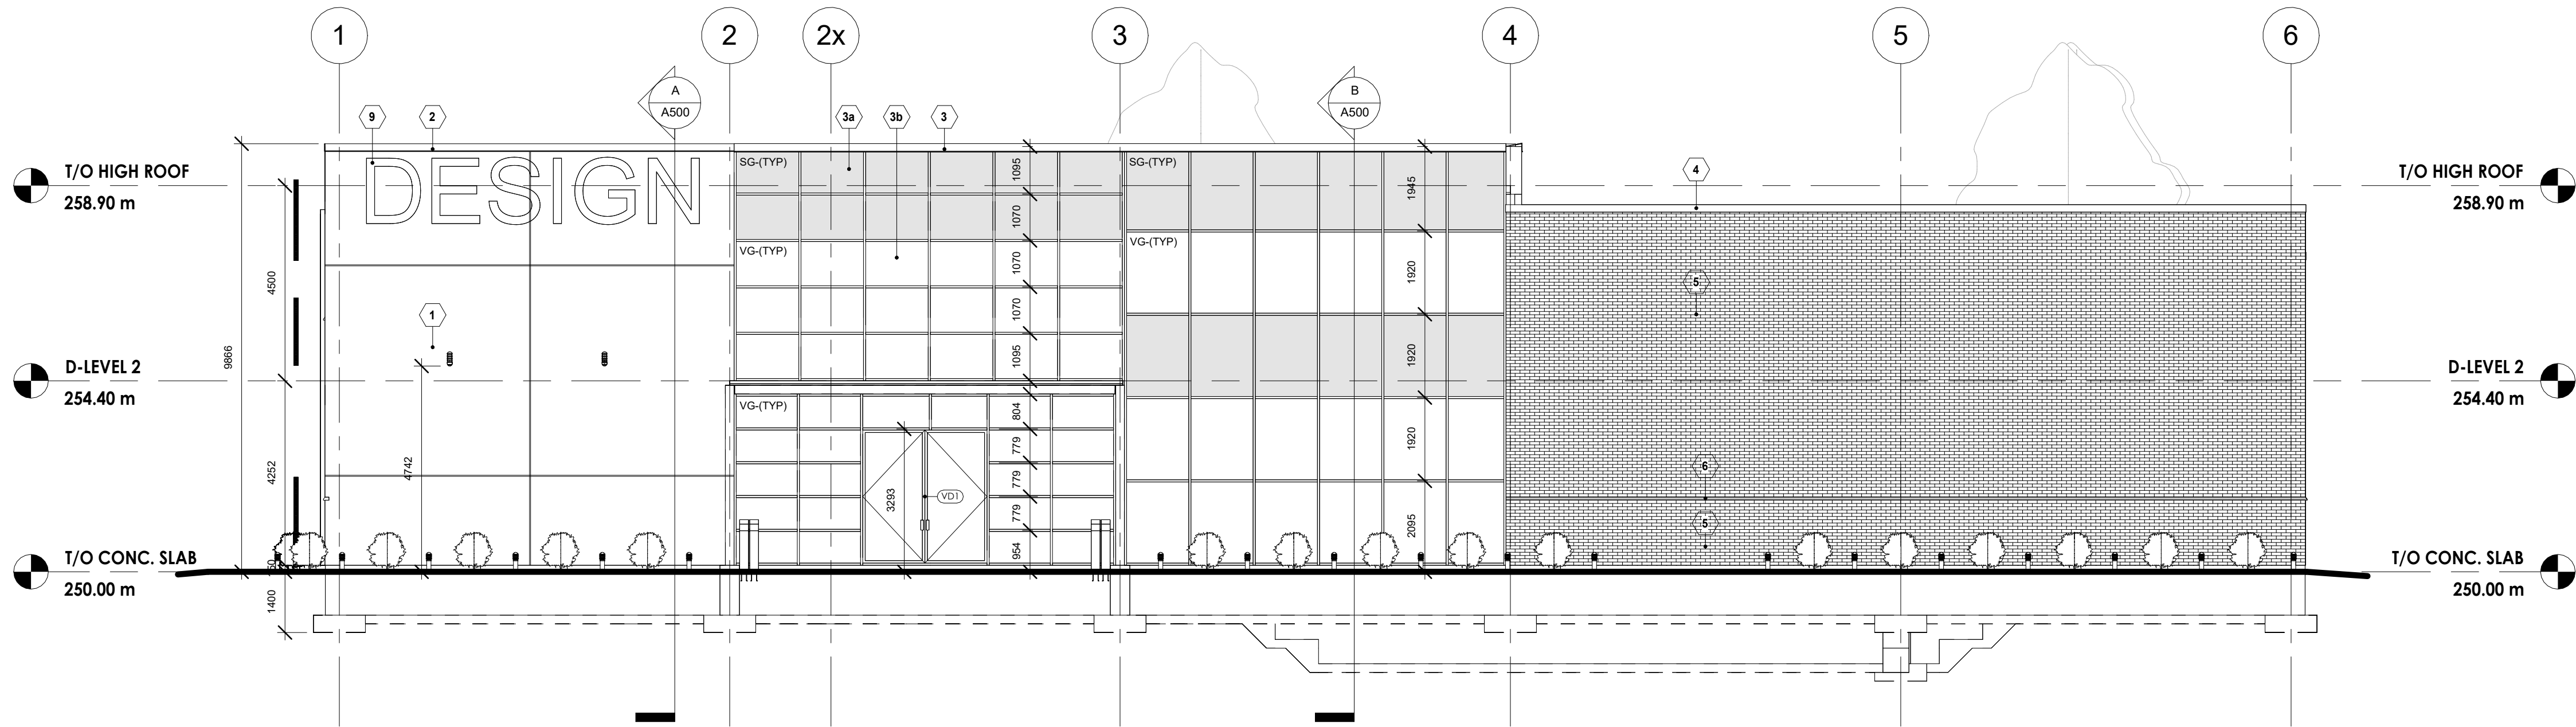


1 SOUTH ELEVATION
1 : 100

MATERIALS LEGEND	
1	ALUMINIUM COMPOSITE PANEL - BLACK
2	METAL FLASHING OVER ACP
3	METAL FLASHING OVER CURTAIN WALL
3a	SPANDREL GLASS - MEDIUM GREY
3b	VISION GLASS - LIGHT GREY
4	METAL FLASHING OVER MASONRY
5	90 LIGHT GREY BRICK - NON UNIFORM RUNNING
6	PRECAST CONCETE SILL - BLACK
7	METAL CLADDING - LIGHT GREY
8	METAL FLASHING OVER METAL CLADDING
9	ACRYLIC SIGNAGE BOARD
SG-(TYP)	SPANDREL GLASS - MEDIUM GREY
VG-(TYP)	VISION GLASS - LIGHT GREY

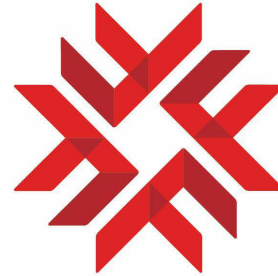

FANSHAW
DONALD J. SMITH
SCHOOL OF BUILDING
TECHNOLOGY

NOTES

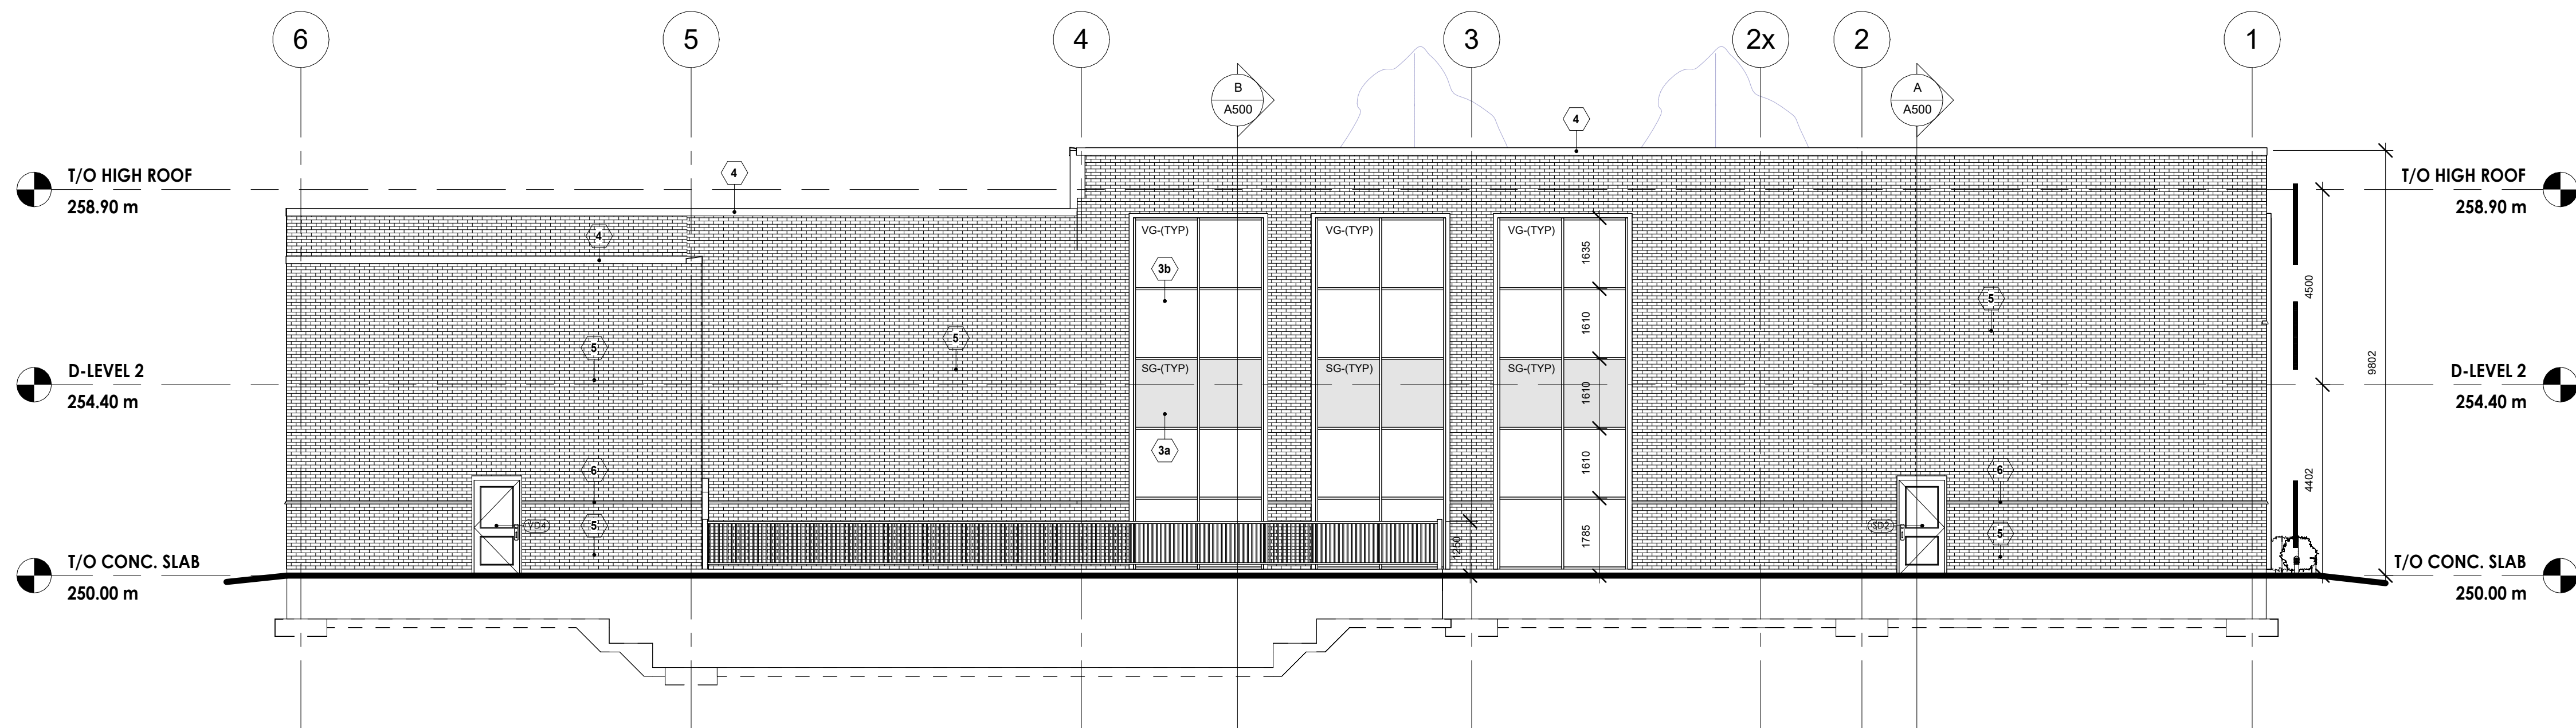

2 NORTH ELEVATION
1 : 100

**PRELIMINARY
NOT FOR CONSTRUCTION**



PROJECT TITLE
**TWO STOREY
COMMERCIAL
BUILDING**

CLIENT:
AFNM


PROJECT ADDRESS
1156DUNDASSTREET-LONDON

DRAWING TITLE
ELEVATIONS

CHECKED LV	DRAWN AN	DATE 08/08/24
2401 PROJECT No.	A300 DRAWING	

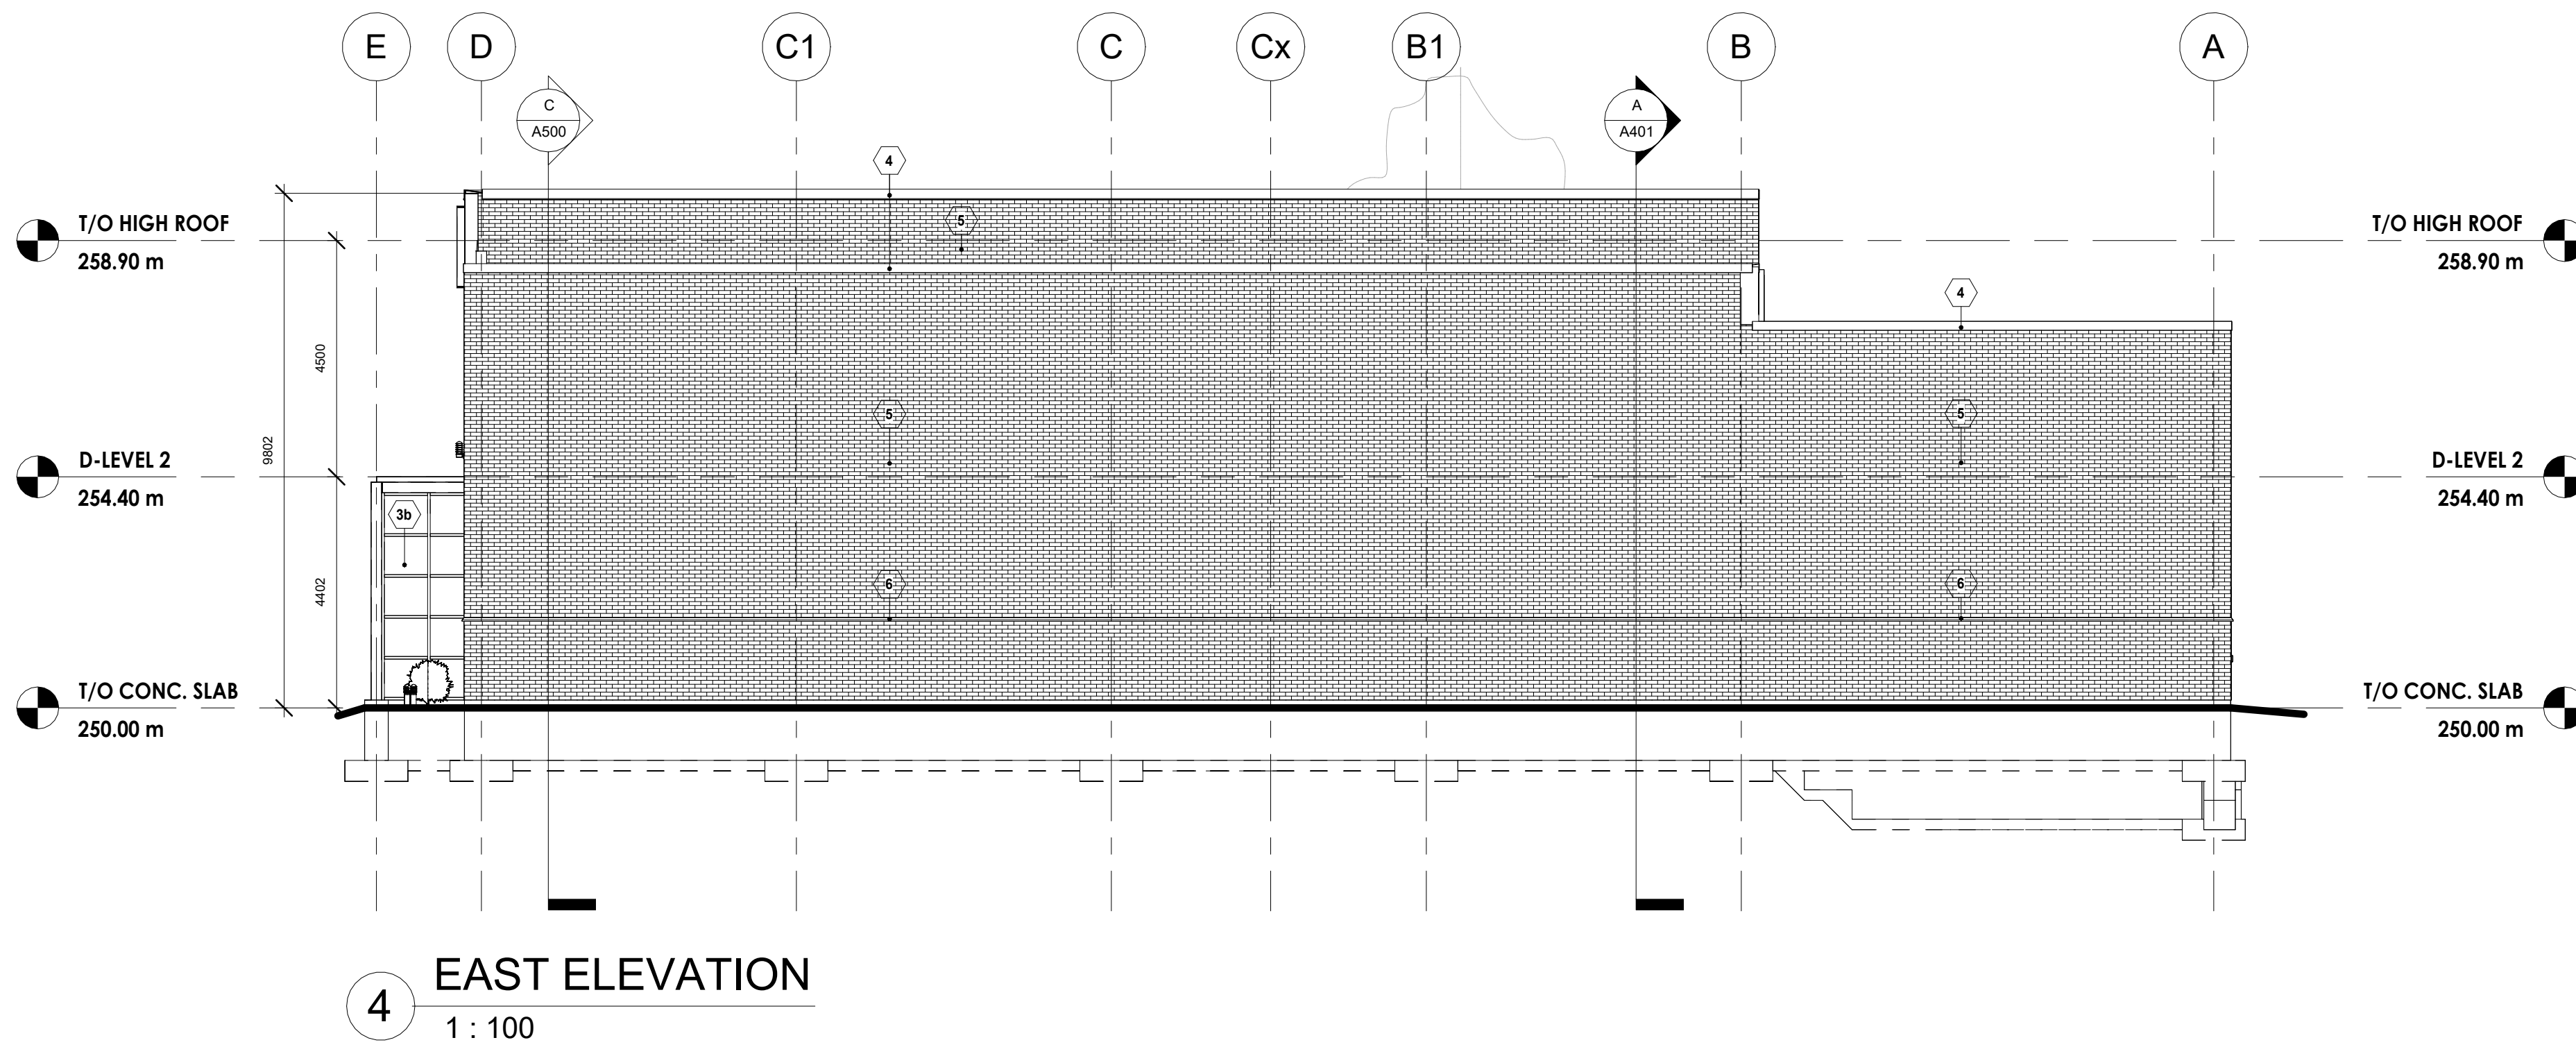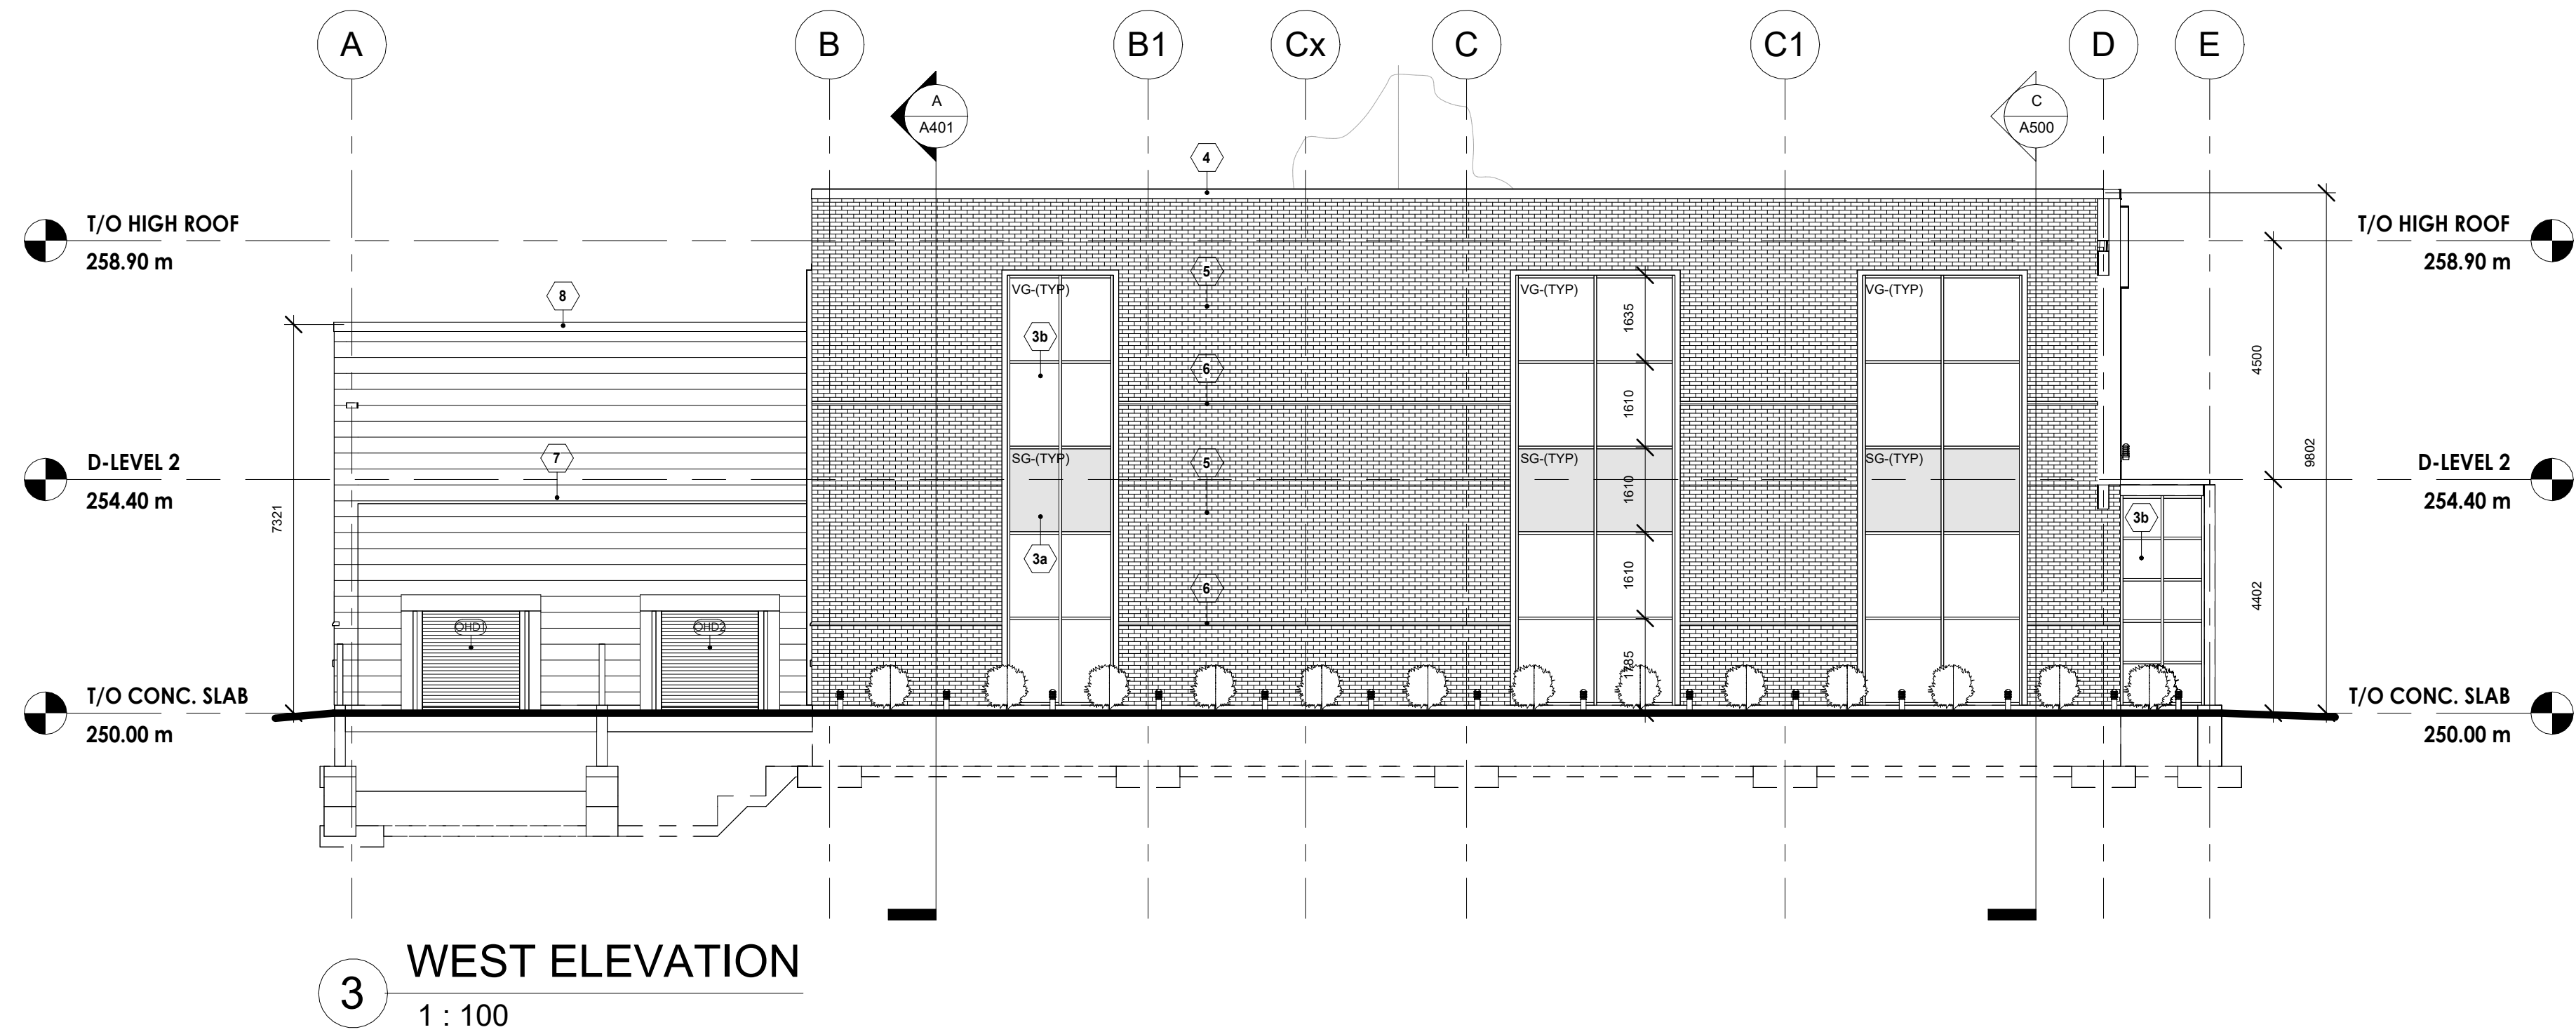

MATERIALS LEGEND	
1	ALUMINIUM COMPOSITE PANEL - BLACK
2	METAL FLASHING OVER ACP
3	METAL FLASHING OVER CURTAIN WALL
3a	SPANDREL GLASS - MEDIUM GREY
3b	VISION GLASS - LIGHT GREY
4	METAL FLASHING OVER MASONRY
5	90 LIGHT GREY BRICK - NON UNIFORM RUNNING
6	PRECAST CONCETE SILL - BLACK
7	METAL CLADDING - LIGHT GREY
8	METAL FLASHING OVER METAL CLADDING
9	ACRYLIC SIGNAGE BOARD
SG-(TYP)	SPANDREL GLASS - MEDIUM GREY
VG-(TYP)	VISION GLASS - LIGHT GREY

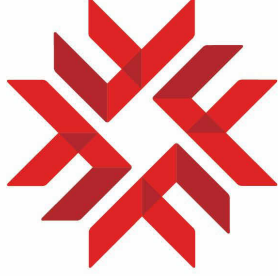

FANSHAW
DONALD J. SMITH
SCHOOL OF BUILDING
TECHNOLOGY

NOTES

**PRELIMINARY
NOT FOR CONSTRUCTION**

PROJECT TITLE
**TWO STOREY
COMMERCIAL
BUILDING**

CLIENT:
AFNM

PROJECT ADDRESS
1156DUNDASSTREET-LONDON

DRAWING TITLE
ELEVATIONS


CHECKED
LV

DRAWN
AN

DATE
08/08/24


2401
PROJECT No.

A301
DRAWING

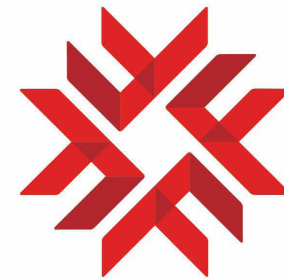


FANSHAW
DONALD J. SMITH
SCHOOL OF BUILDING
TECHNOLOGY

NOTES

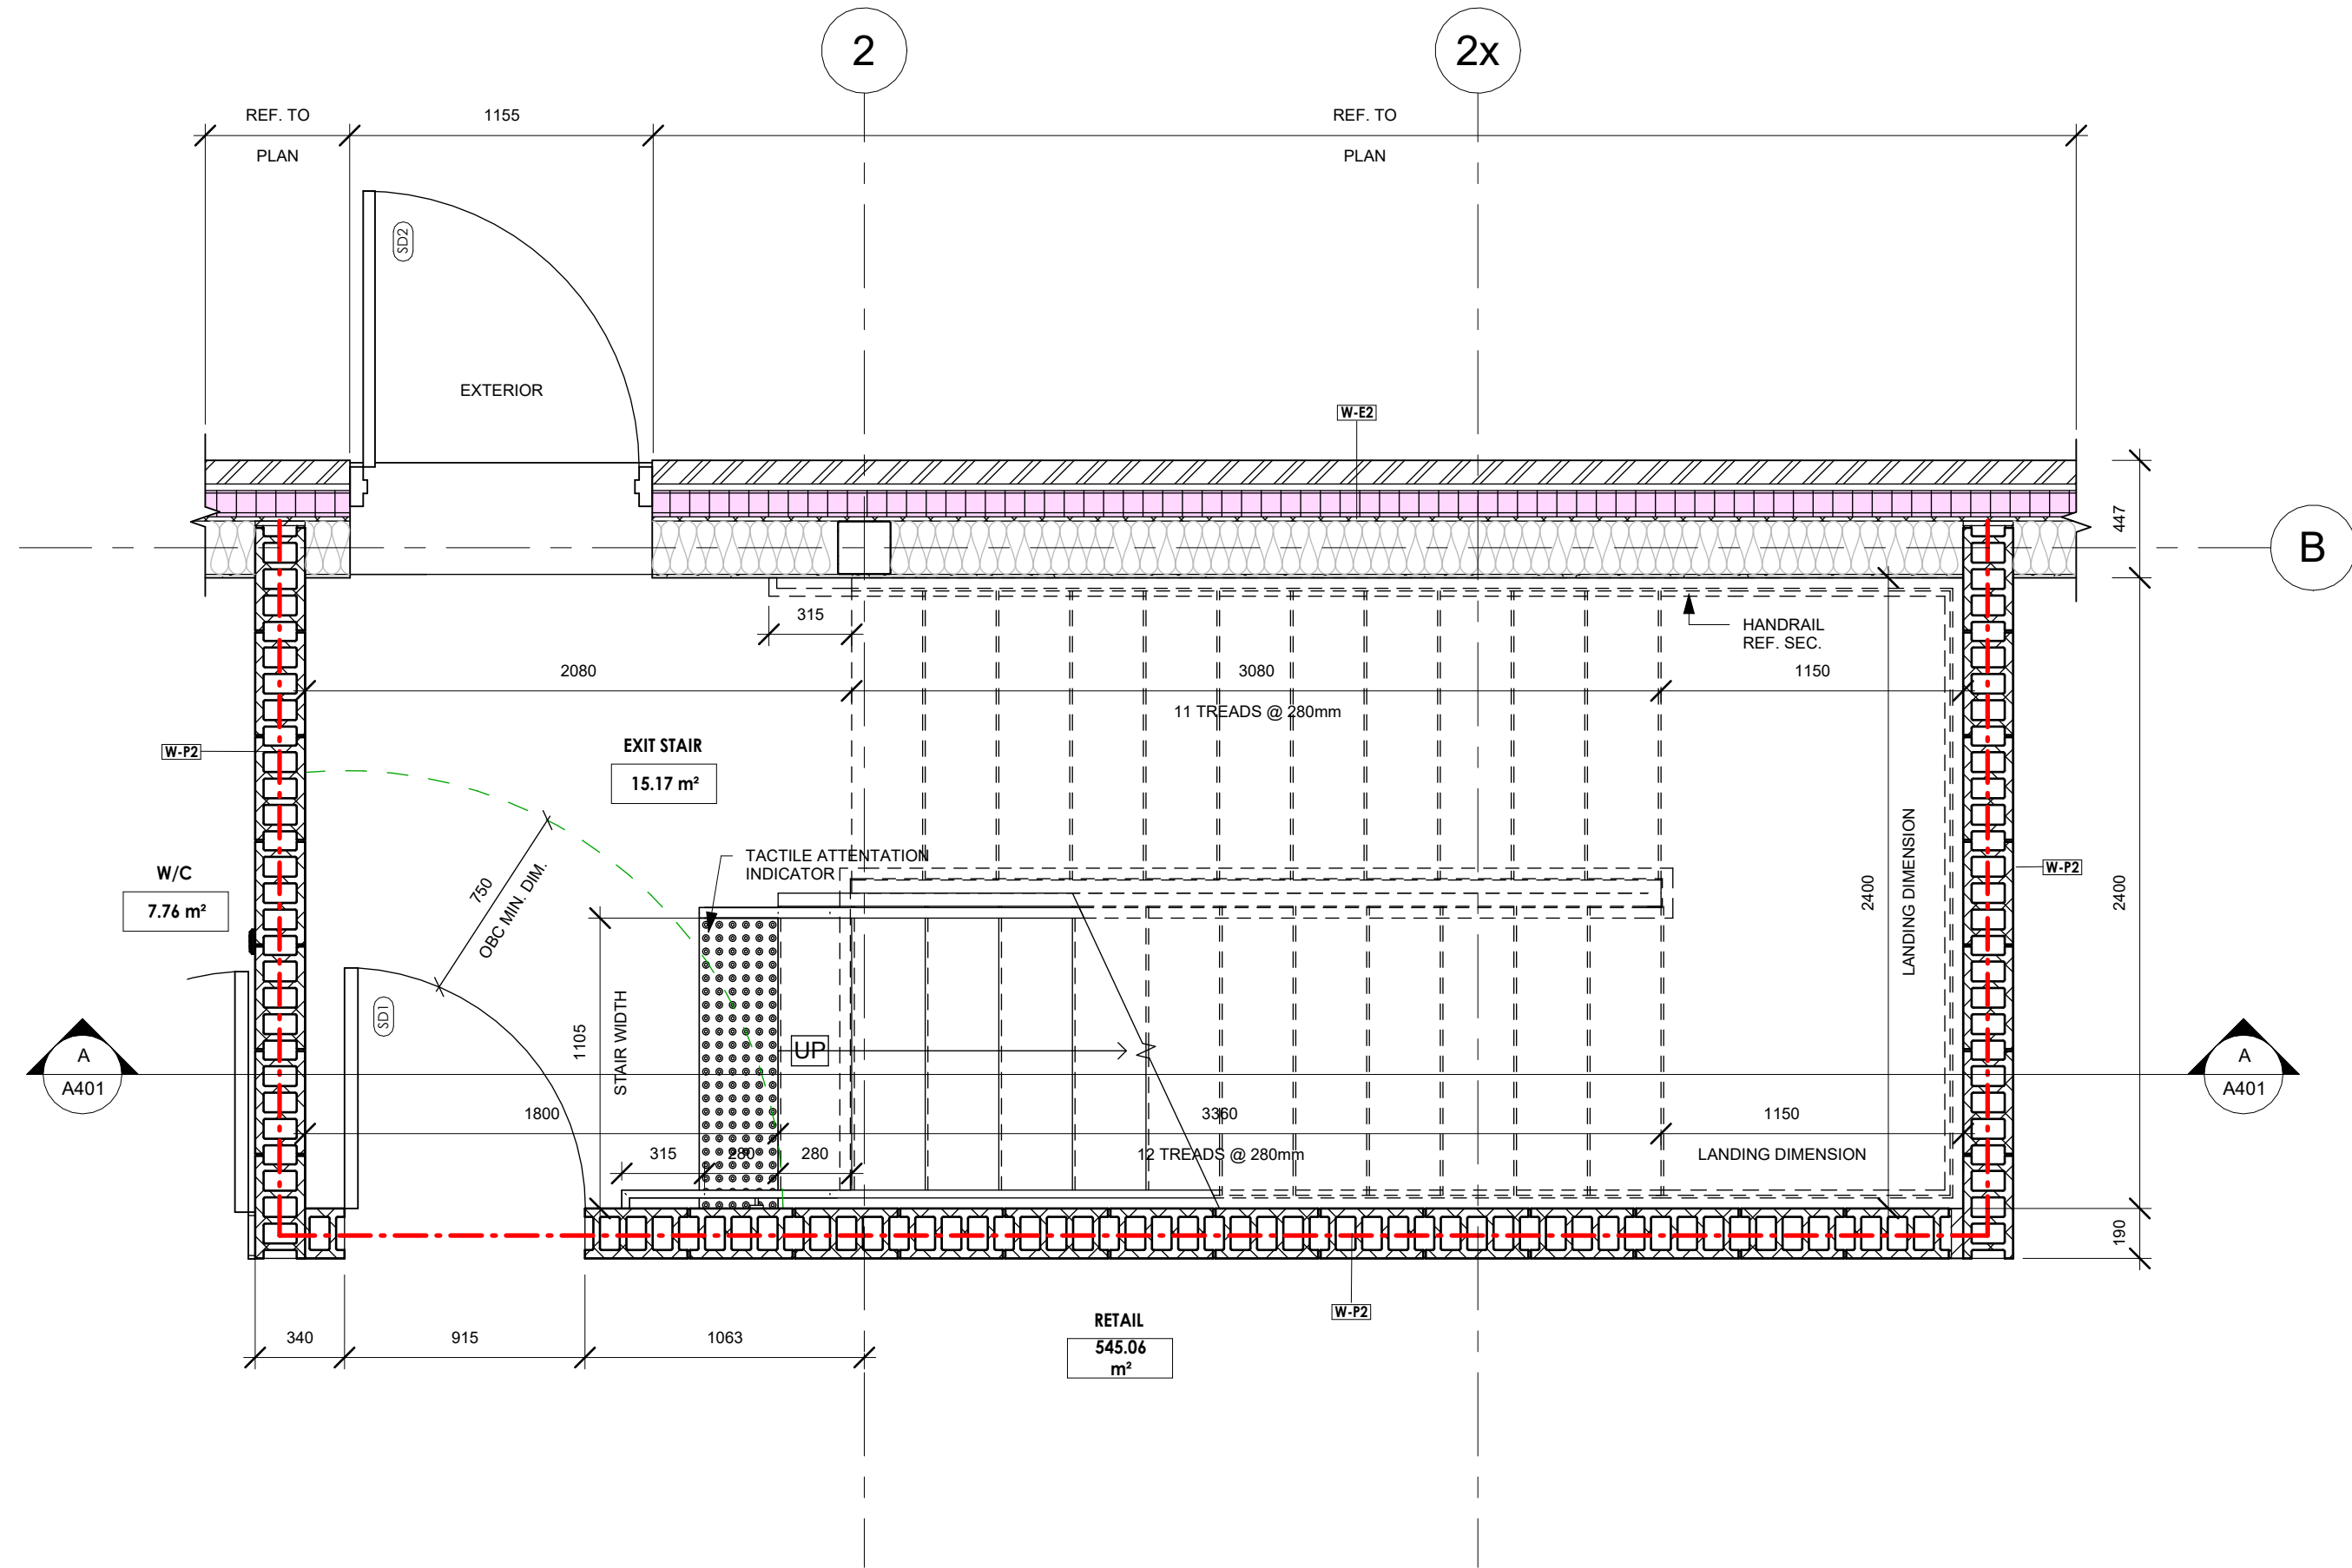

1
A400
ENLARGED MAIN FLOOR STAIR PLAN
1 : 25

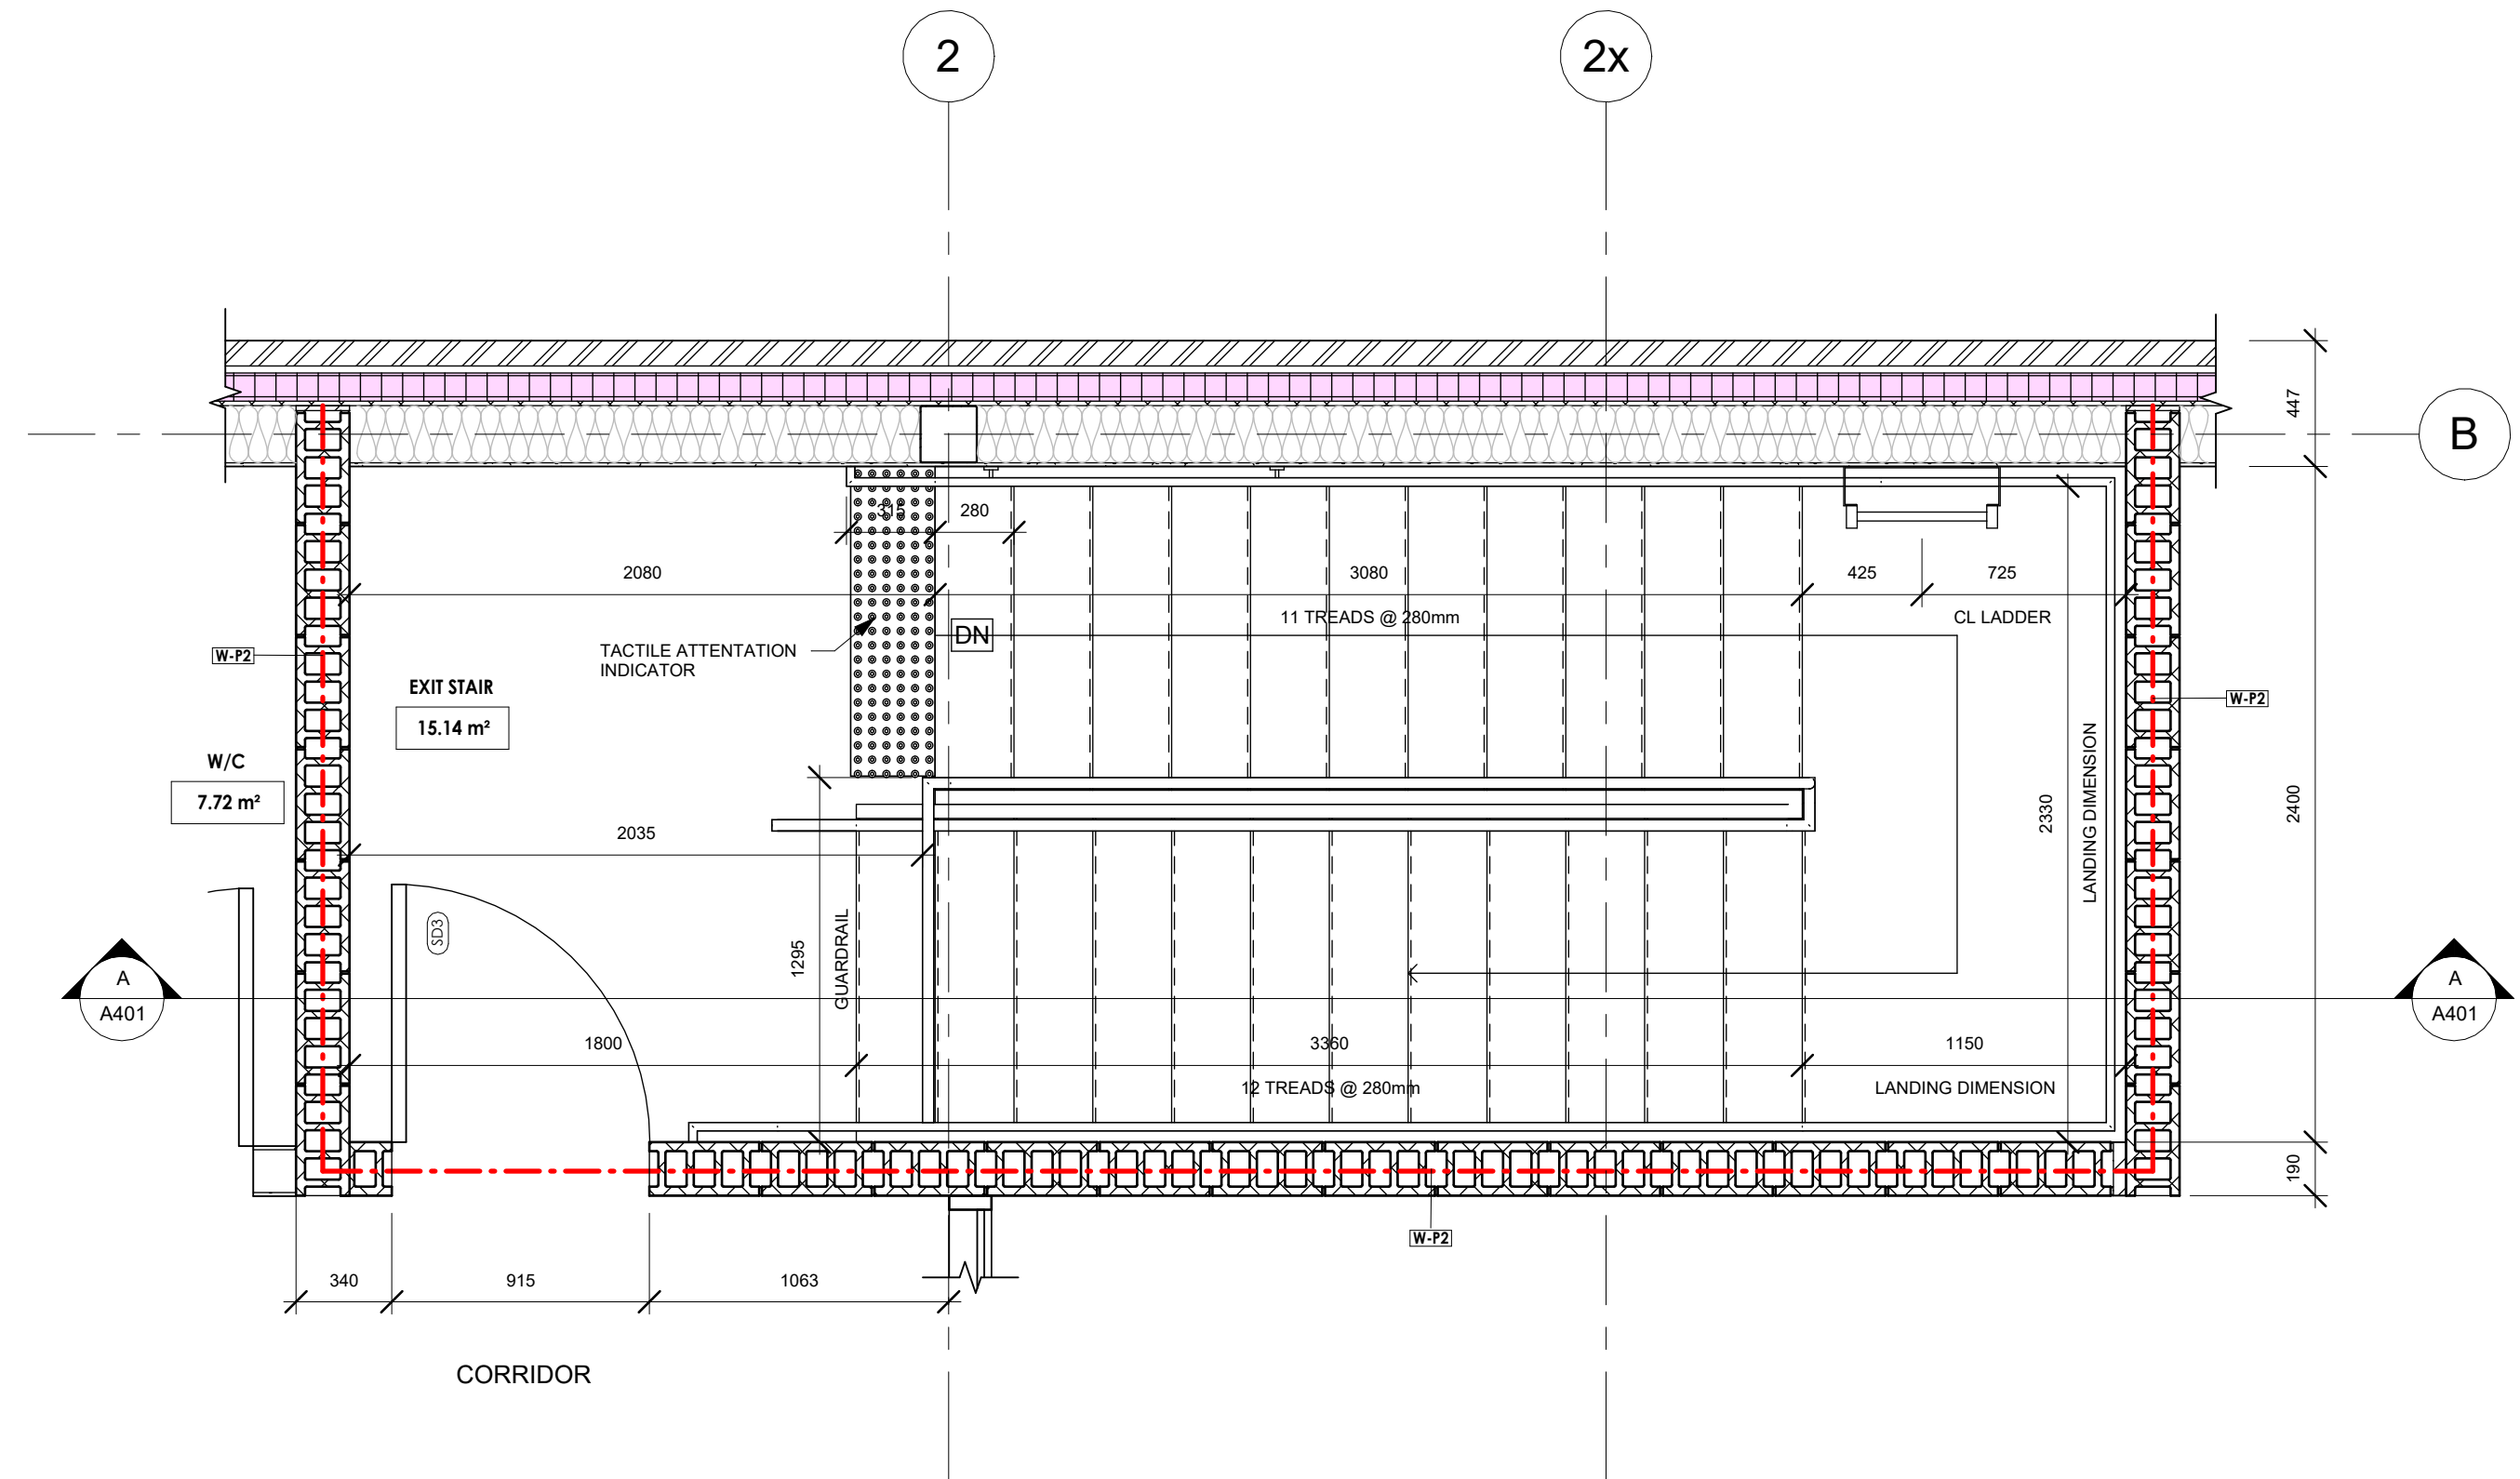

2
A400
ENLARGED LEVEL 2 STAIR PLAN
1 : 25


PRELIMINARY
NOT FOR CONSTRUCTION

PROJECT TITLE
TWO STOREY
COMMERCIAL
BUILDING
CLIENT:
AFNM
PROJECT ADDRESS
1156DUNDASSTREET-LONDON

DRAWING TITLE
ENLARGED STAIR PLAN & SECTION

CHECKED LV | DRAWN AN | DATE 07/31/24

2401
PROJECT No. | A400
DRAWING

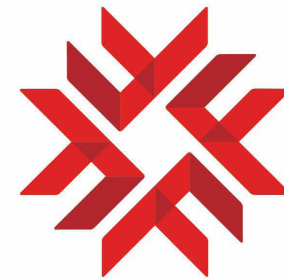

FANSHAWE
DONALD J. SMITH
SCHOOL OF BUILDING
TECHNOLOGY

NOTES

**PRELIMINARY
NOT FOR CONSTRUCTION**

PROJECT TITLE
**TWO STOREY
COMMERCIAL
BUILDING**

CLIENT:
AFNM


PROJECT ADDRESS
1156DUNDASSTREET-LONDON

DRAWING TITLE
ENLARGED STAIR SECTION & 3D

CHECKED LV | DRAWN AN | DATE 08/21/24


2401
PROJECT No.

A401
DRAWING

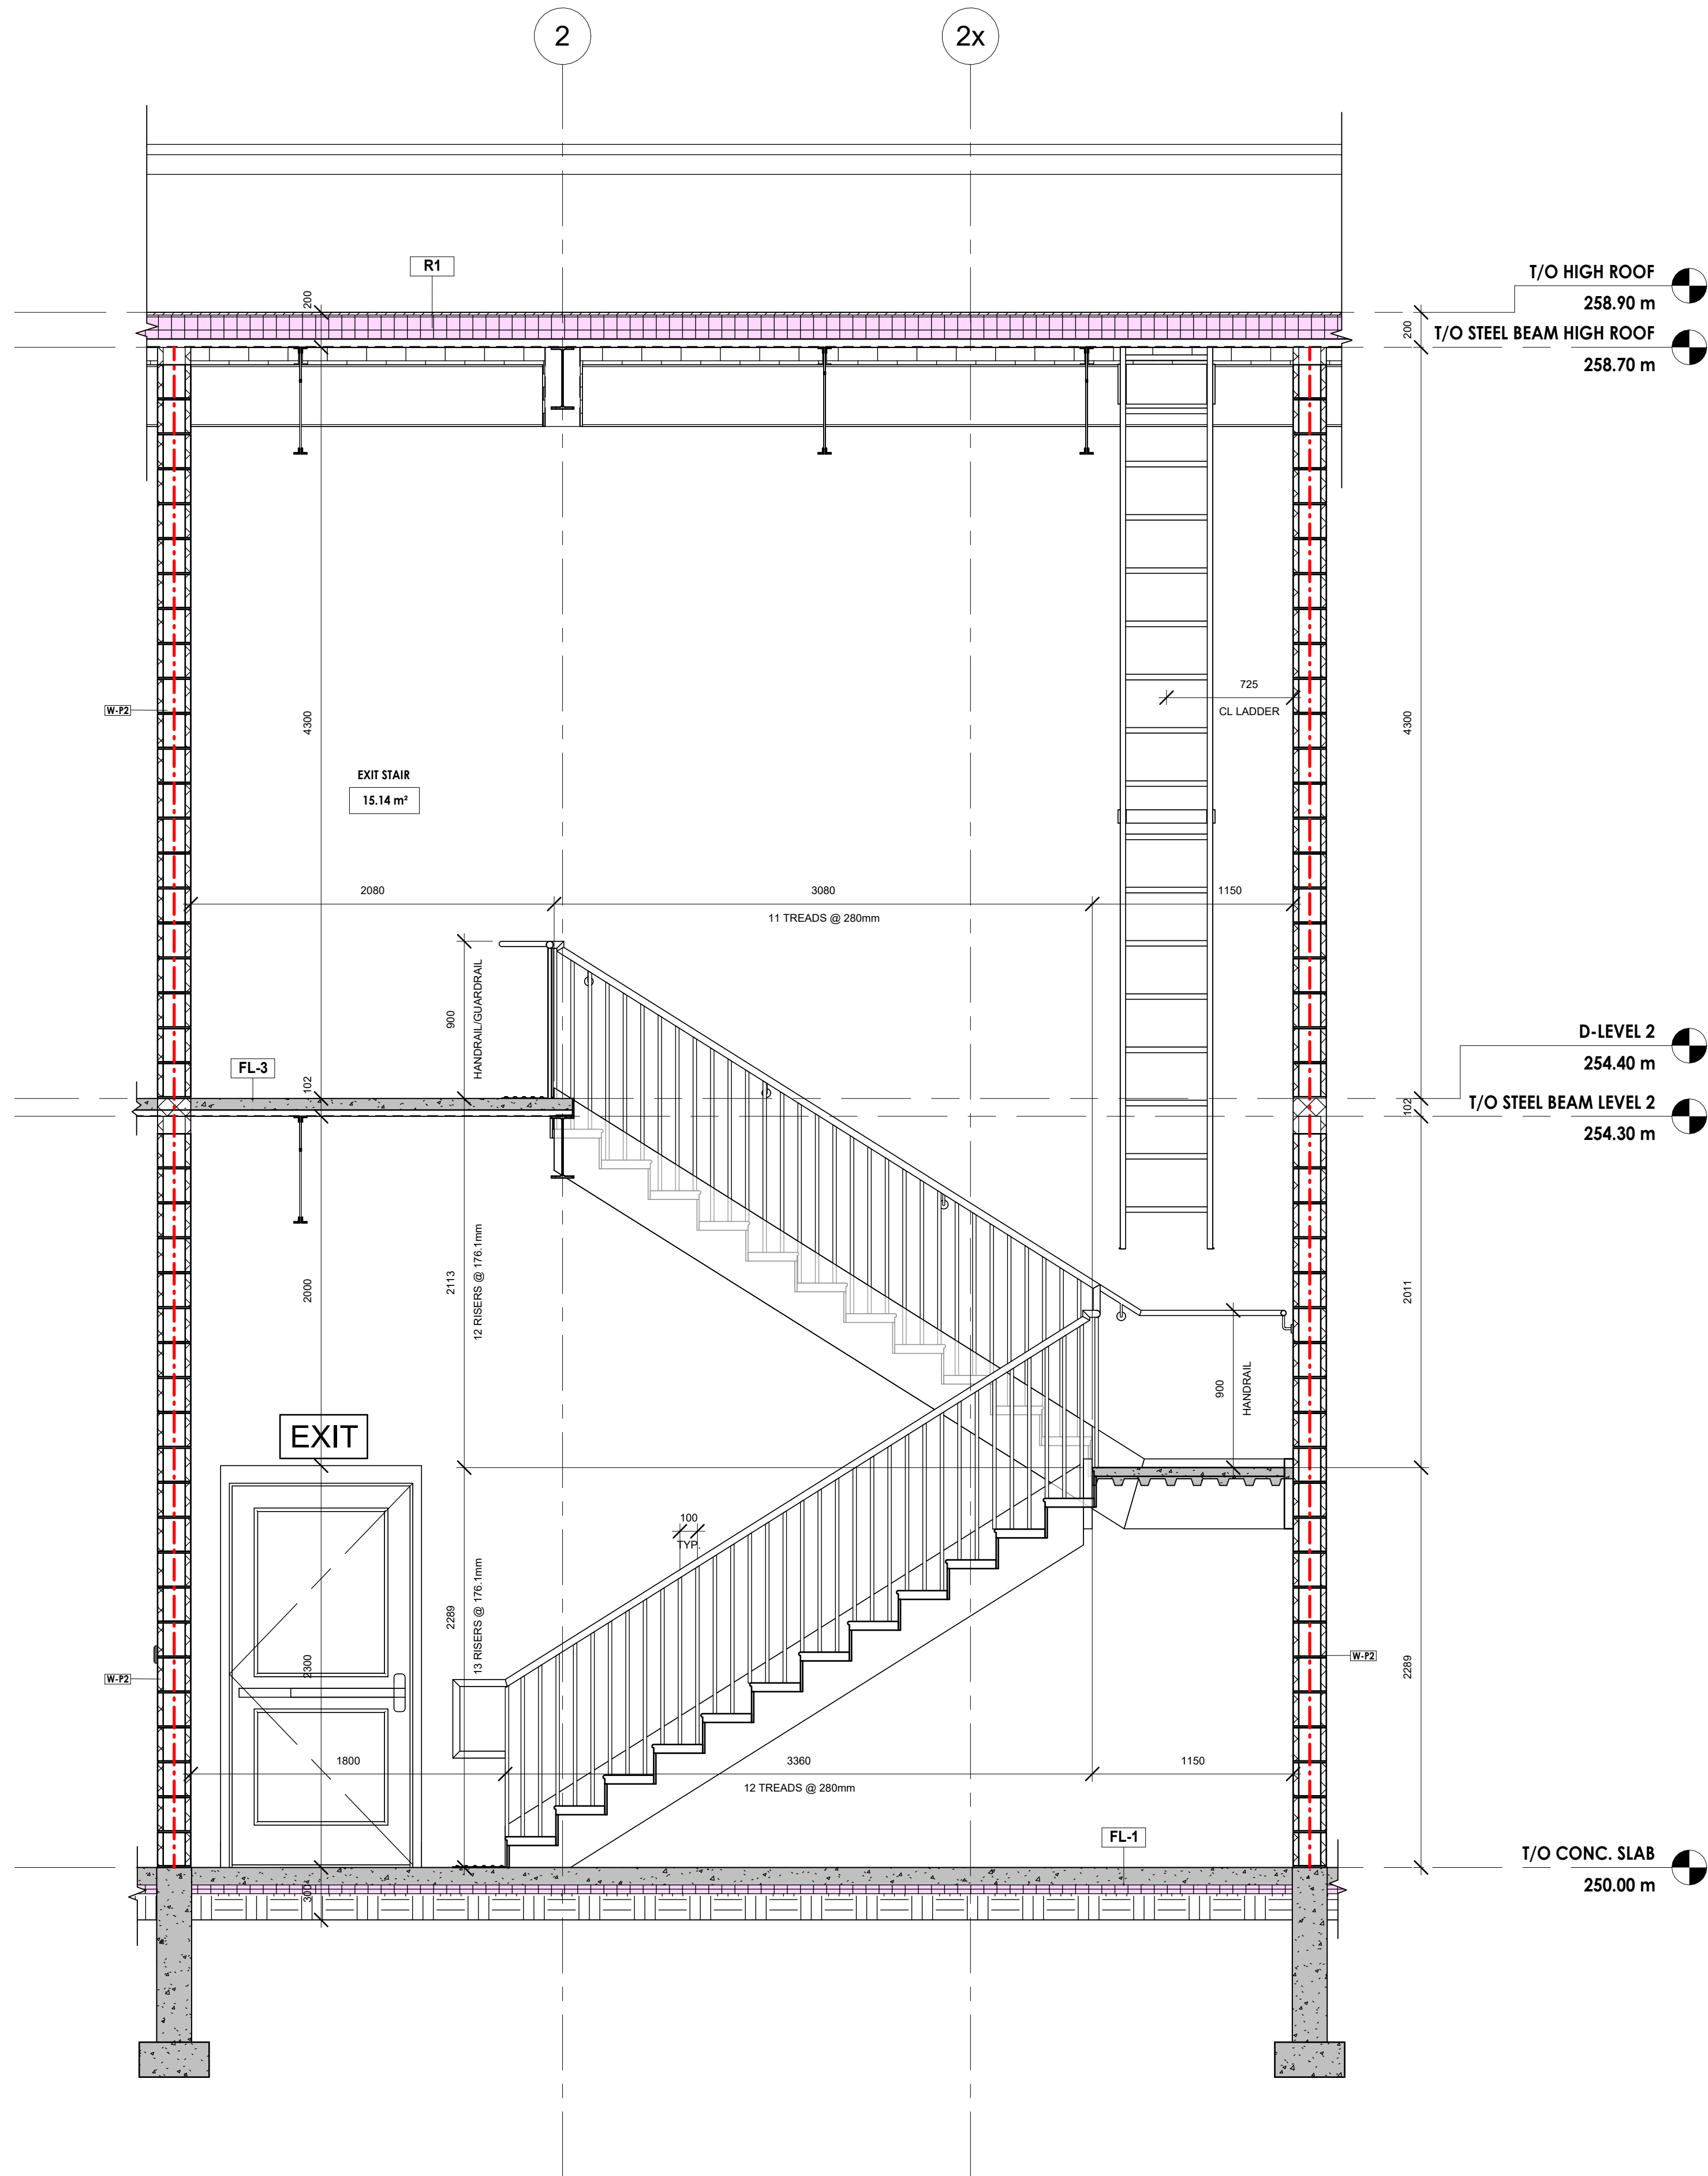


STAIR SECTION


1 : 25

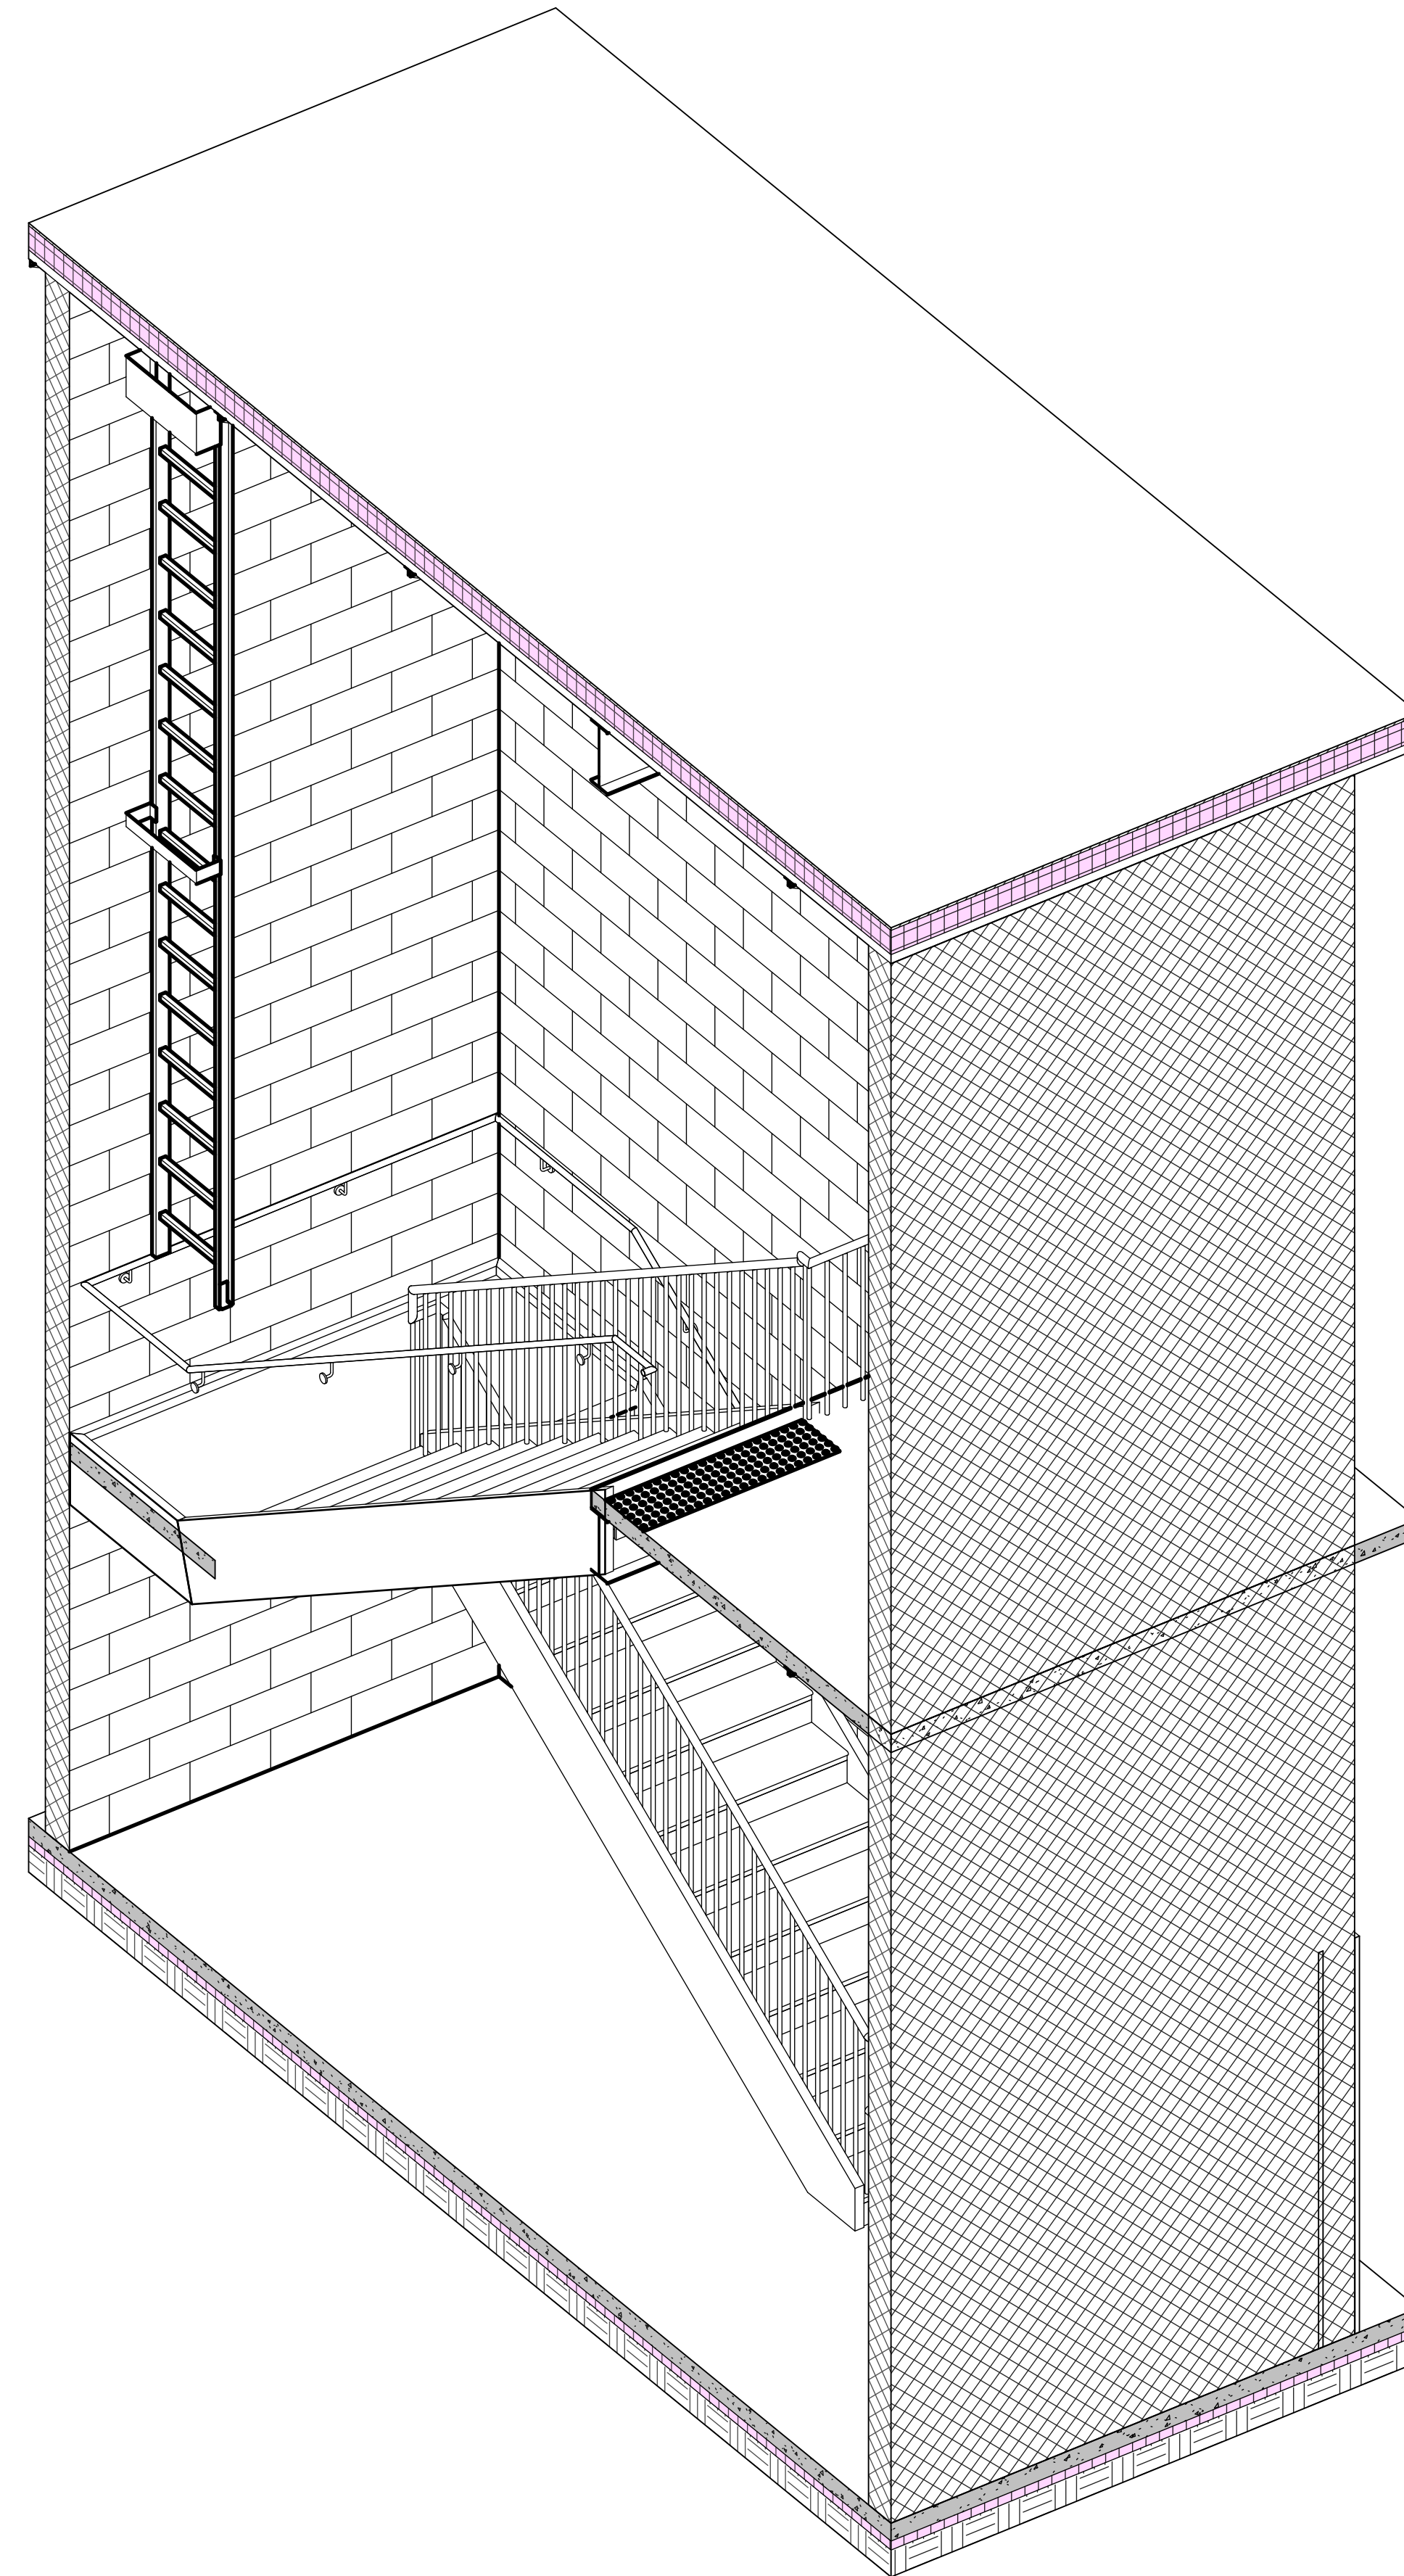


STAIR 3D

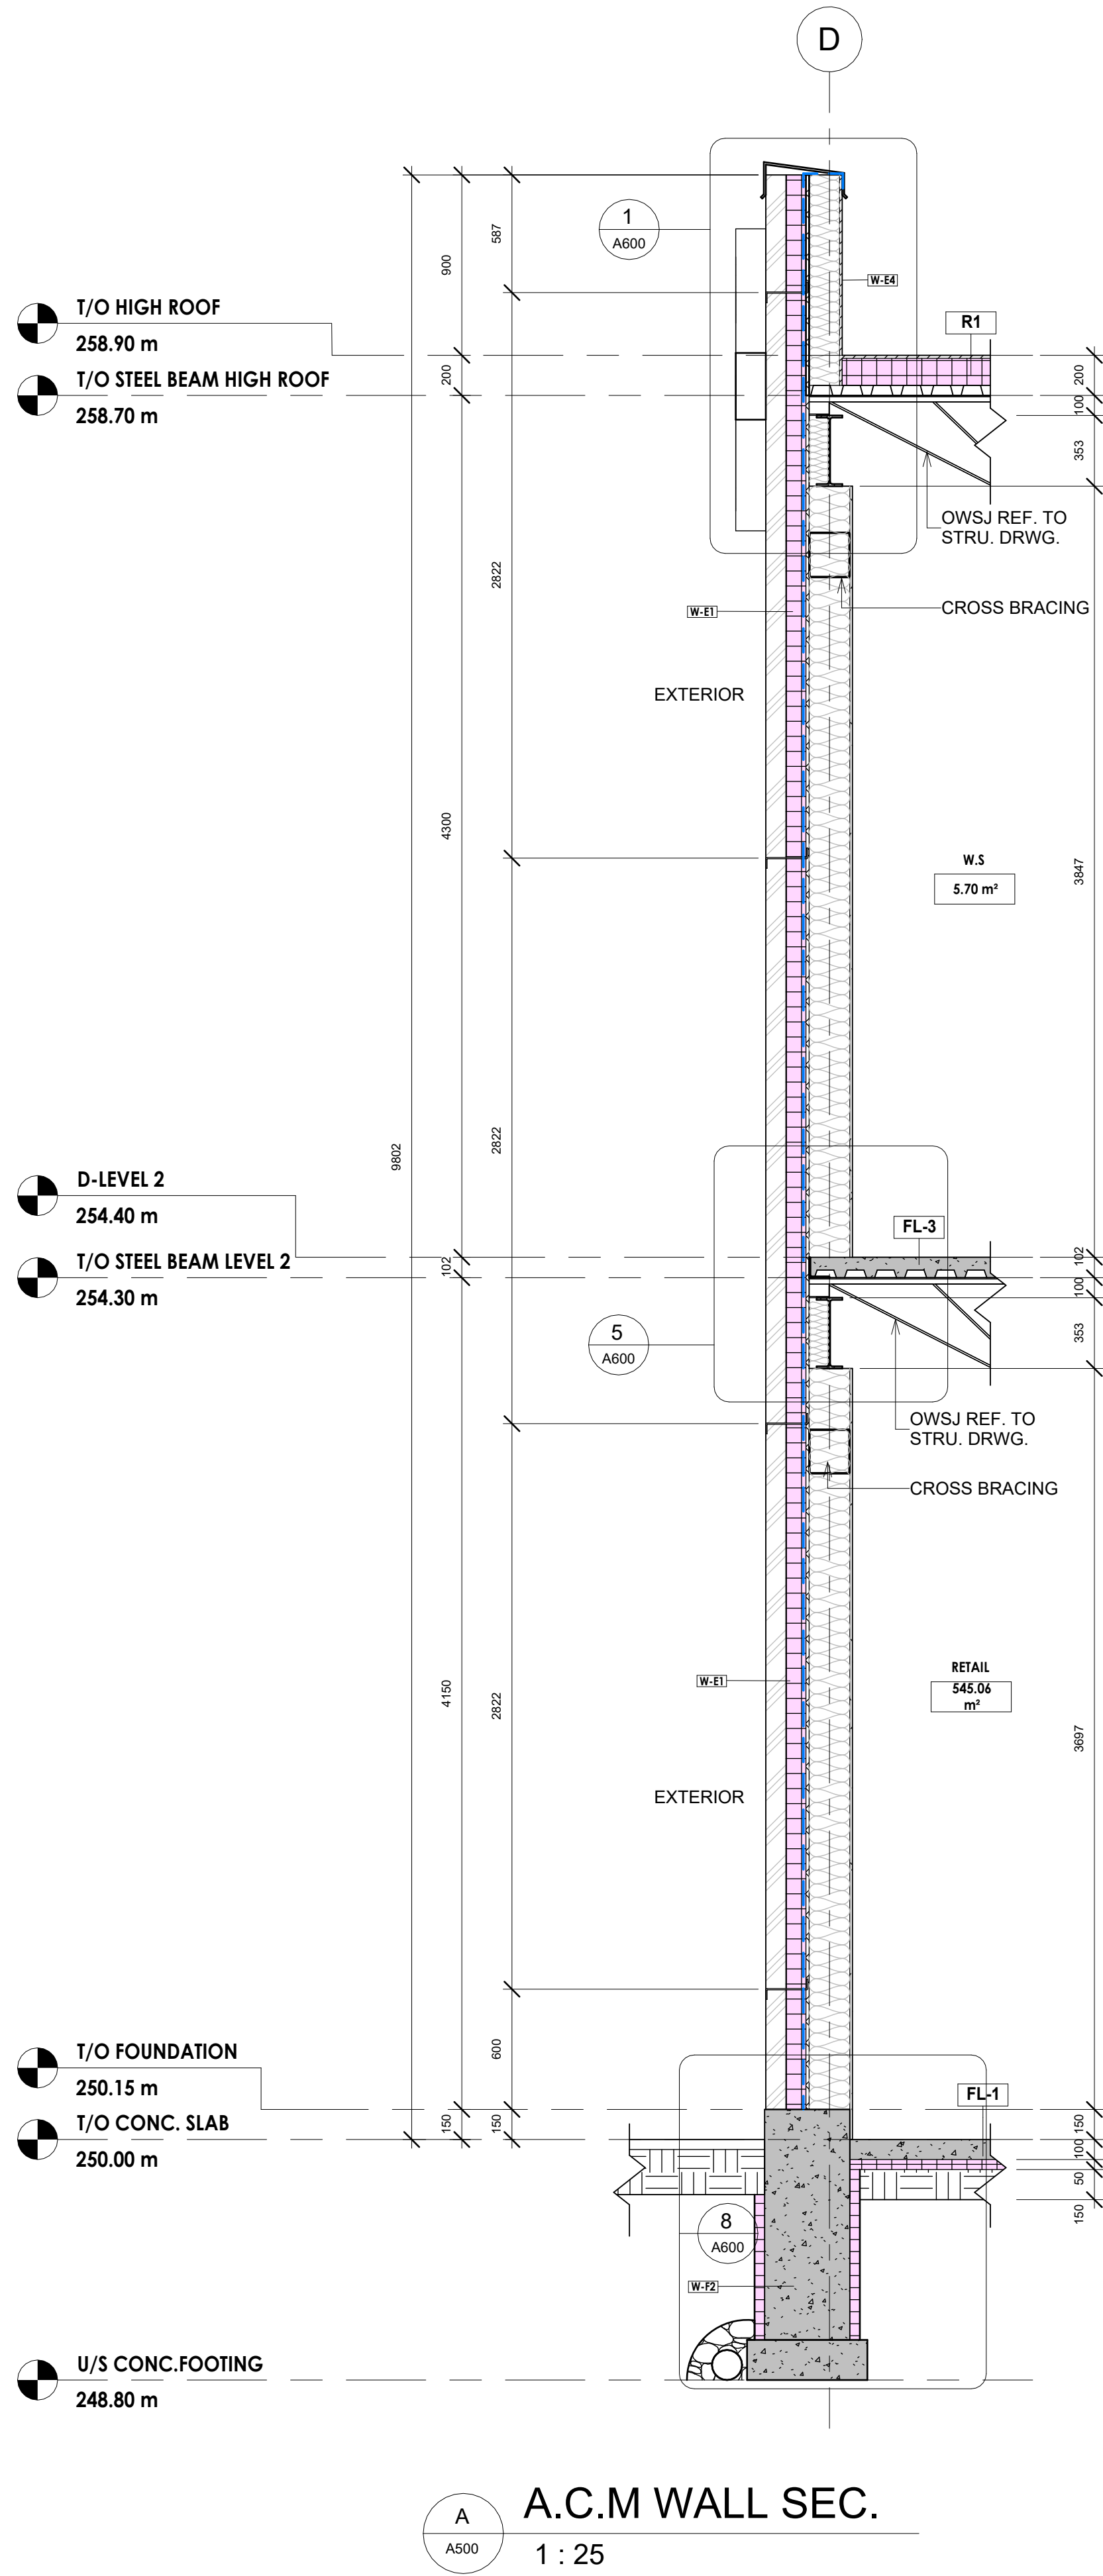


A
A500
A.C.M WALL SEC.
1 : 25

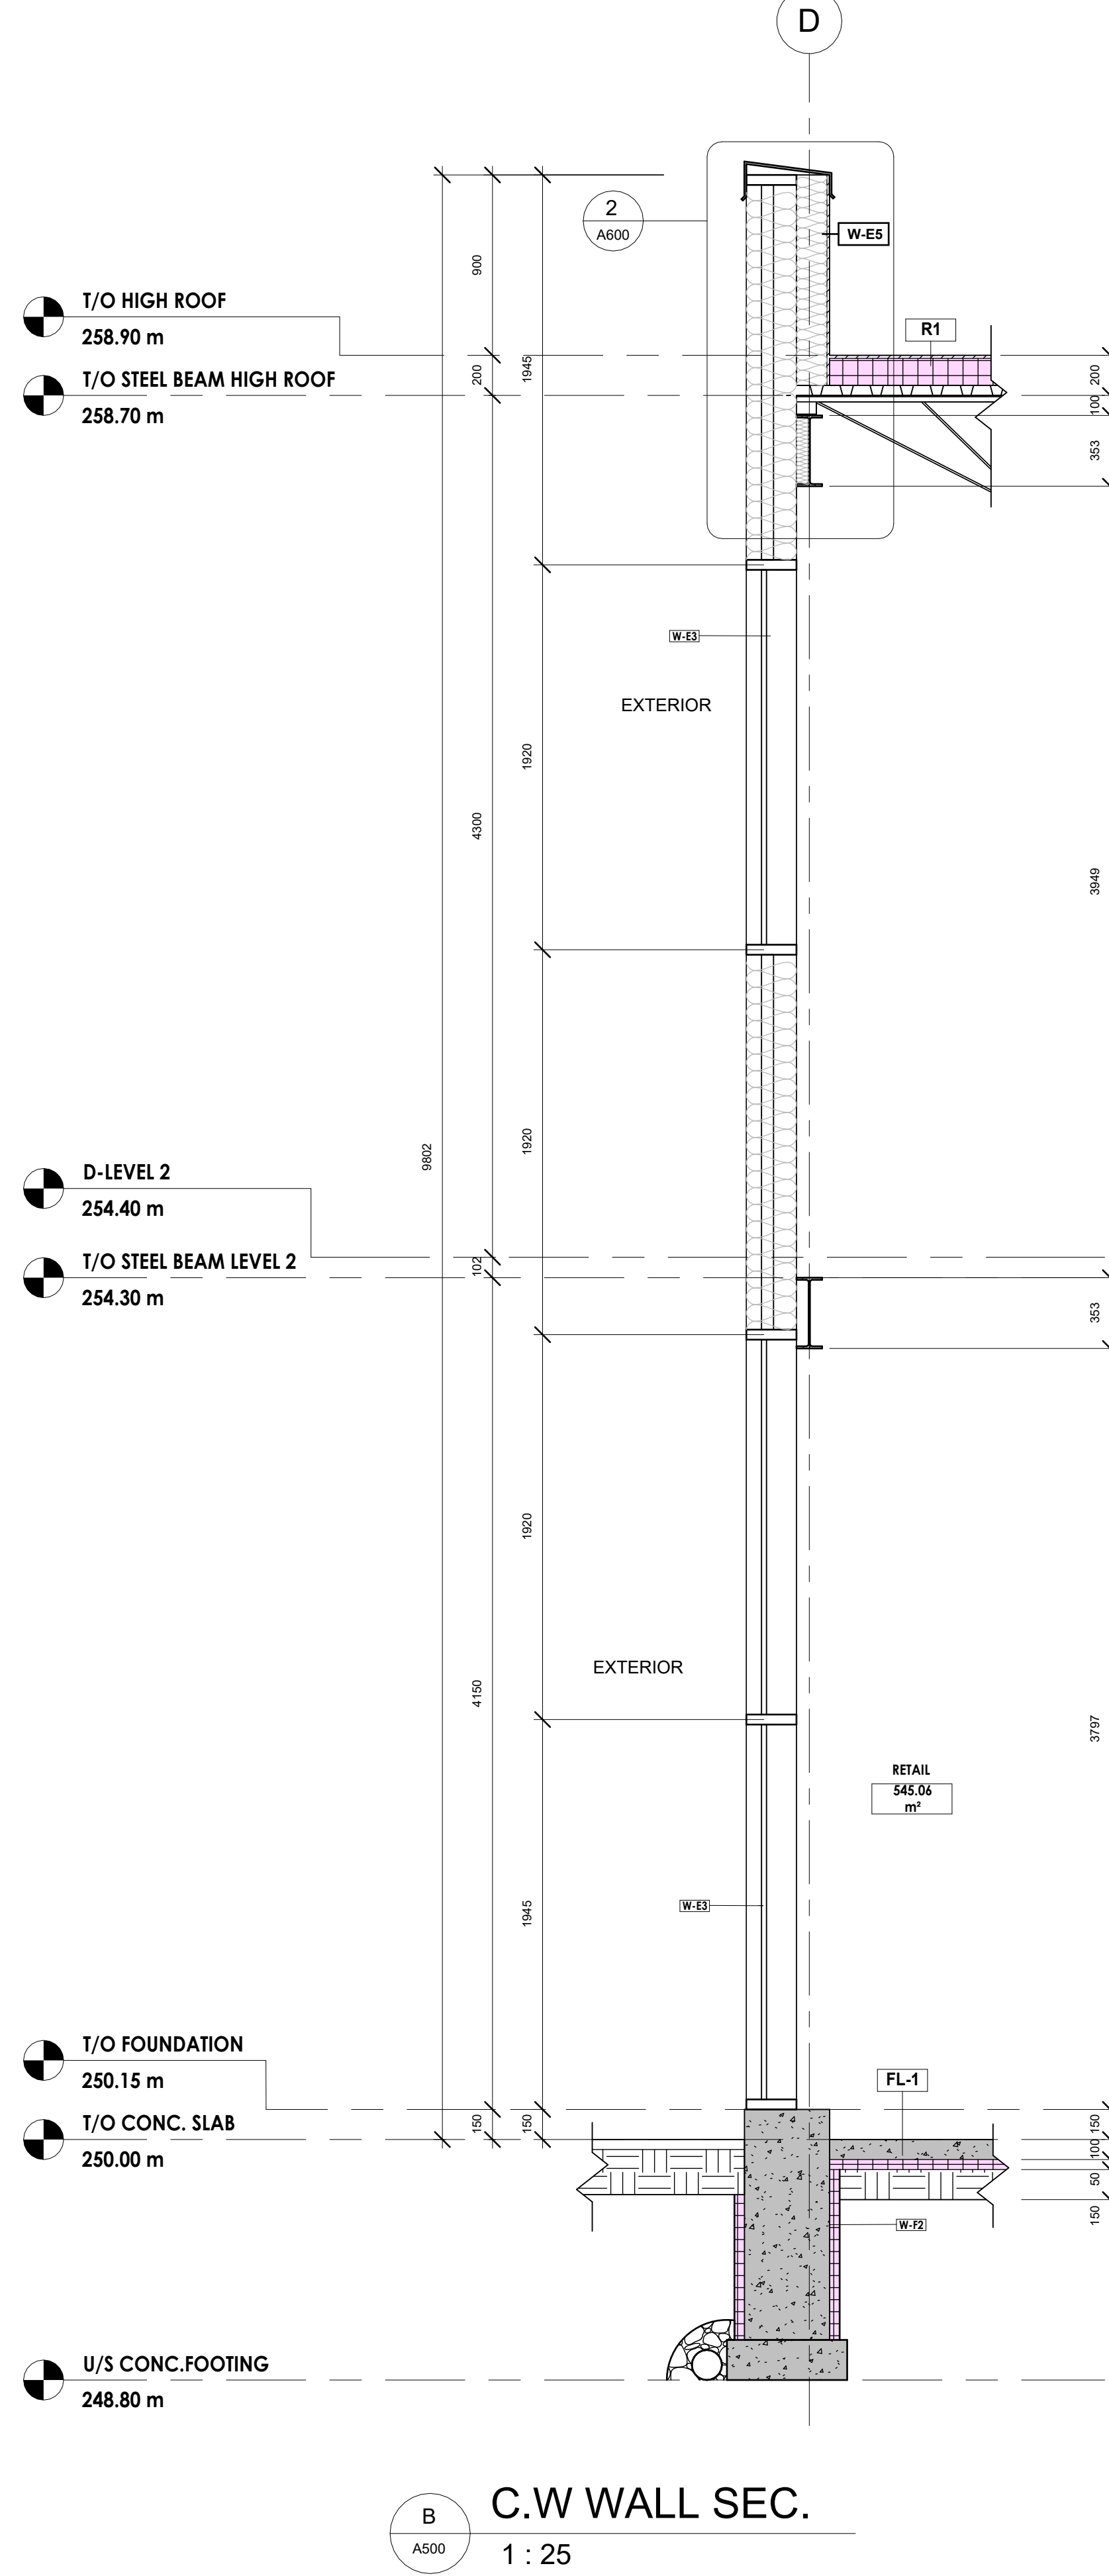

B
A500
C.W WALL SEC.
1 : 25

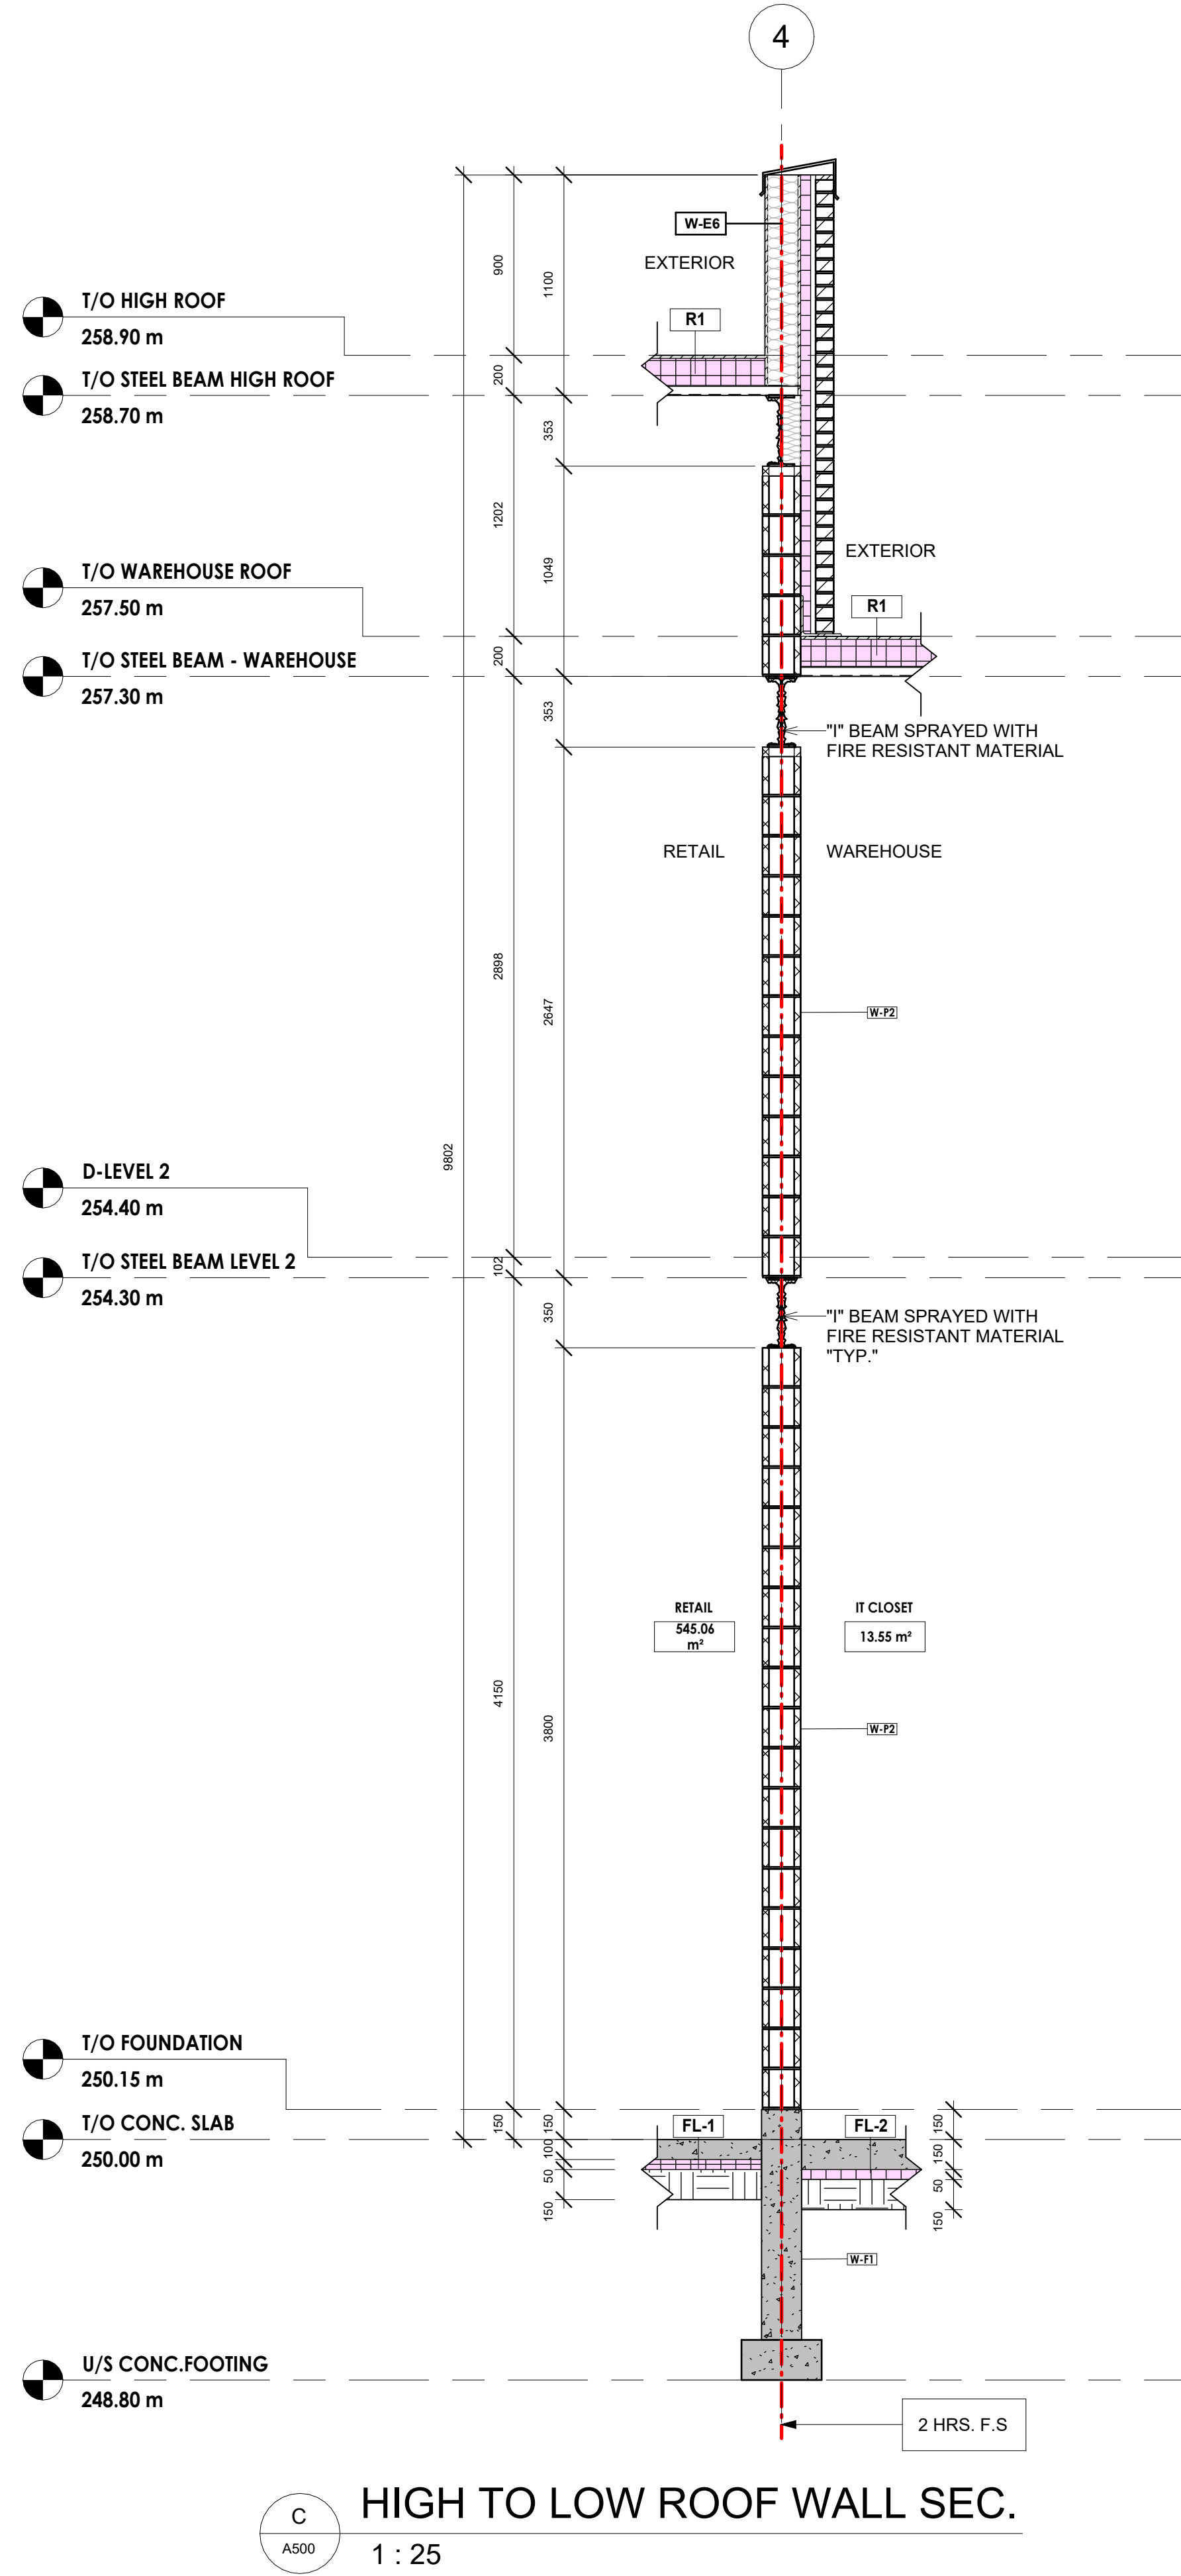

C
A500
HIGH TO LOW ROOF WALL SEC.
1 : 25

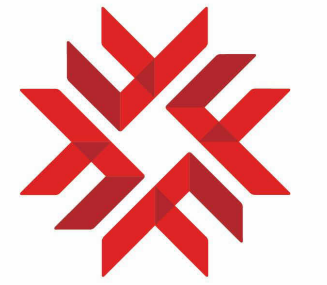

FANSHAW
DONALD J. SMITH
SCHOOL OF BUILDING
TECHNOLOGY

NOTES


VAPOUR BARRIER	---
A/V BARRIER	---
T.P.O ROOF MEMBRANE	---

PRELIMINARY
NOT FOR CONSTRUCTION

PROJECT TITLE
TWO STOREY
COMMERCIAL
BUILDING
CLIENT:
AFNM
PROJECT ADDRESS
1156DUNDASSTREET-LONDON
DRAWING TITLE
WALL SECTIONS

CHECKED
LV
DRAWN
AN
DATE
07/03/24

2401
PROJECT No.
A500
DRAWING

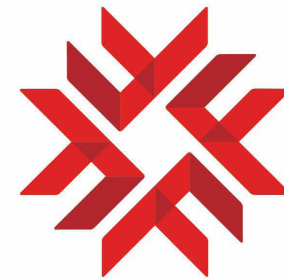

FANSHAWE
DONALD J. SMITH
SCHOOL OF BUILDING
TECHNOLOGY

NOTES

VAPOUR BARRIER	---
A/V BARRIER	---
T.P.O ROOF MEMBRANE	---

PRELIMINARY
NOT FOR CONSTRUCTION

PROJECT TITLE
**TWO STOREY
COMMERCIAL
BUILDING**

CLIENT:
AFNM

PROJECT ADDRESS
1156DUNDASSTREET-LONDON

DRAWING TITLE
DETAILS


CHECKED
LV

DRAWN
AN


DATE
07/03/24

2401
PROJECT No.


A600
DRAWING

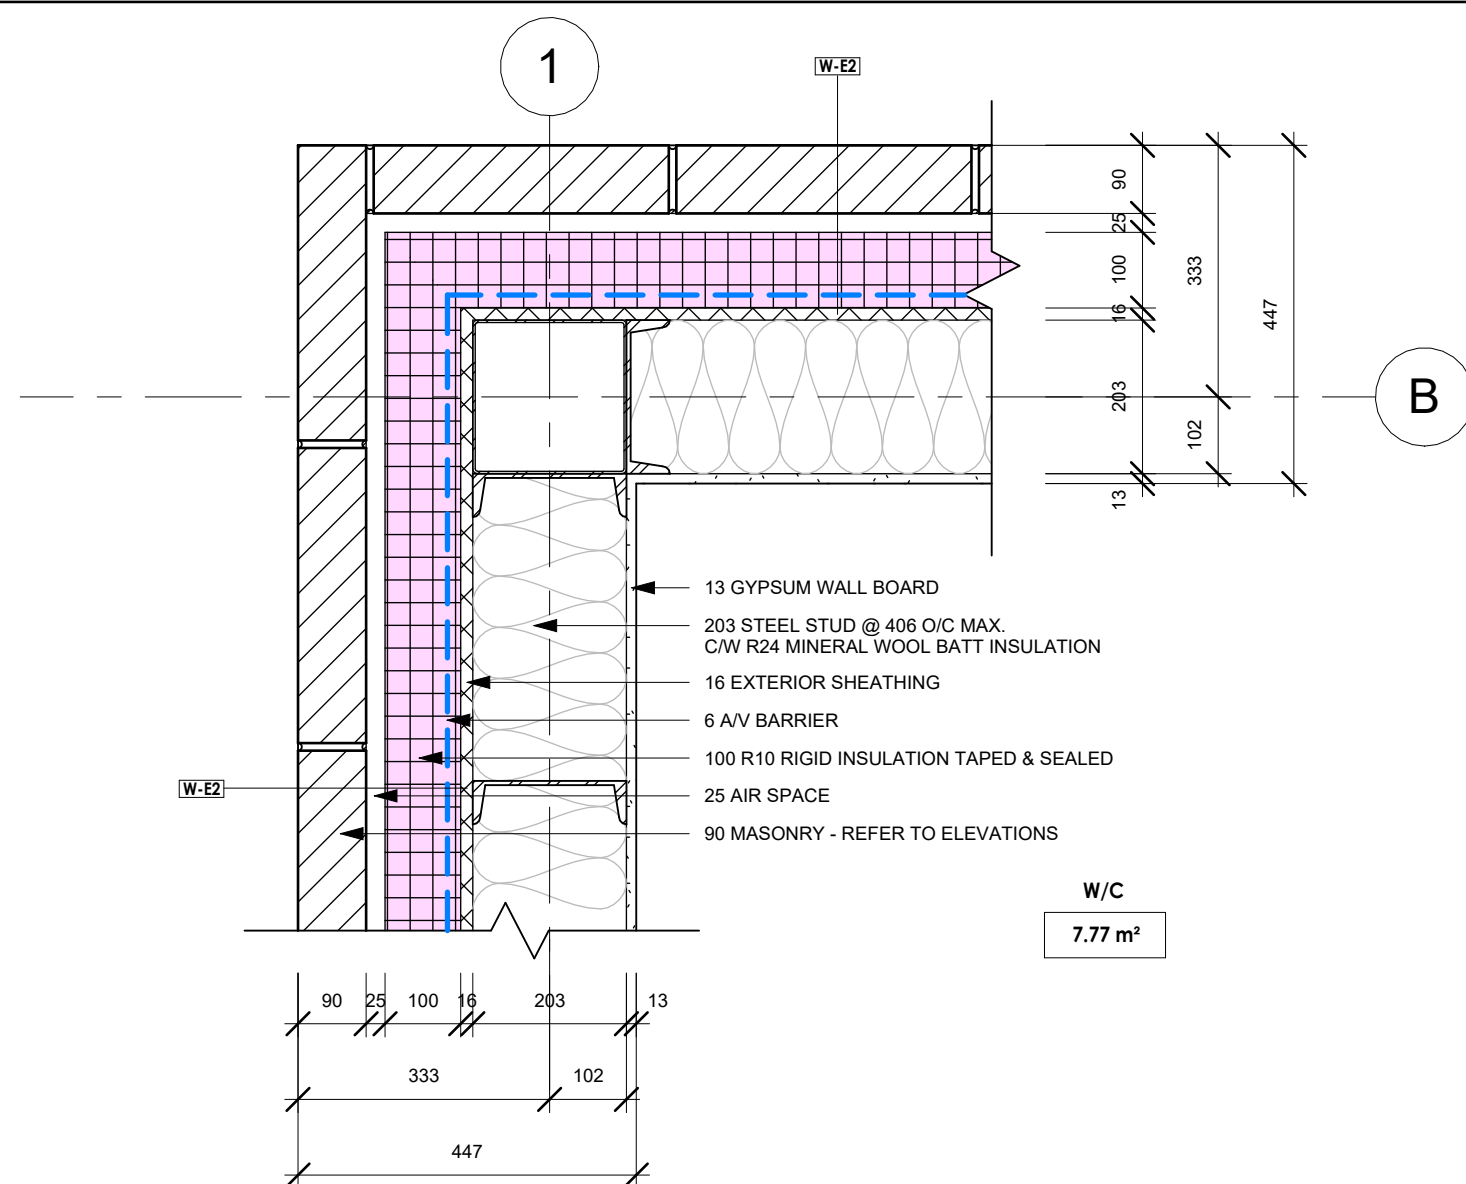


EXT. MASO. COR. PLAN DET.
1 : 10

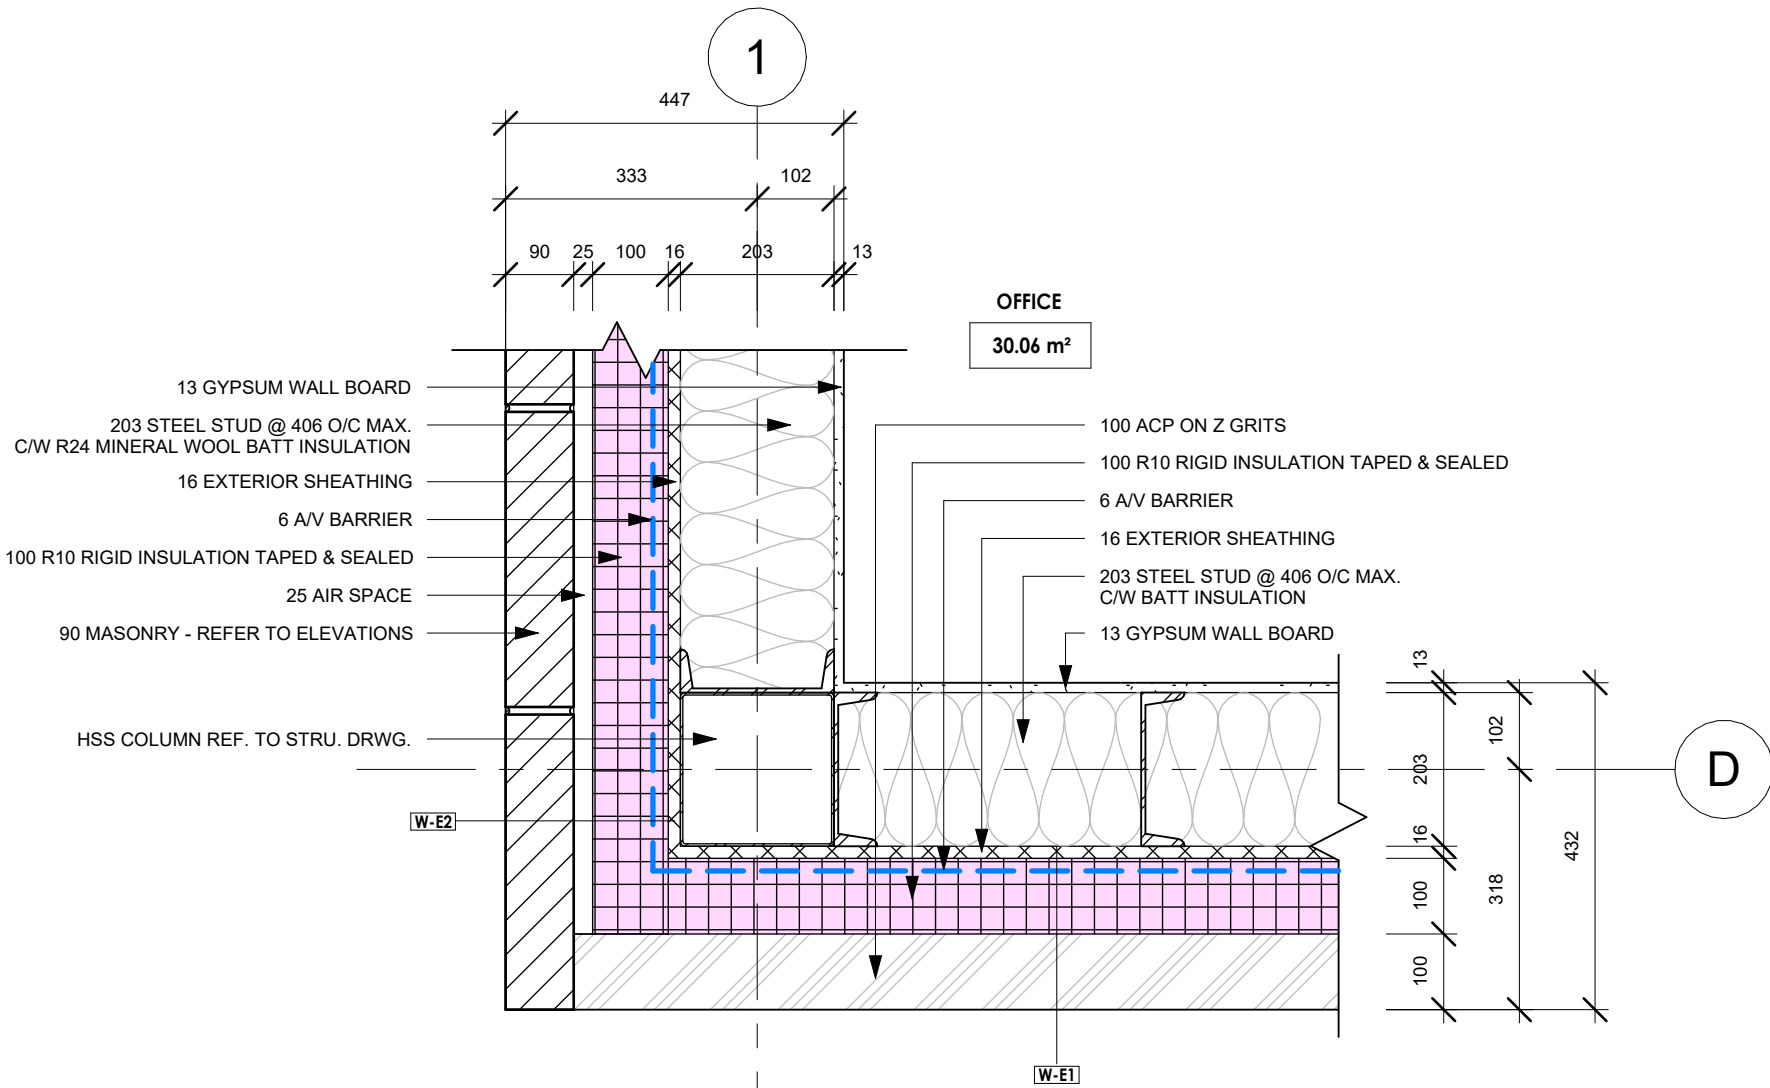


EXT. A.C.P COR. PLAN DET.
1 : 10

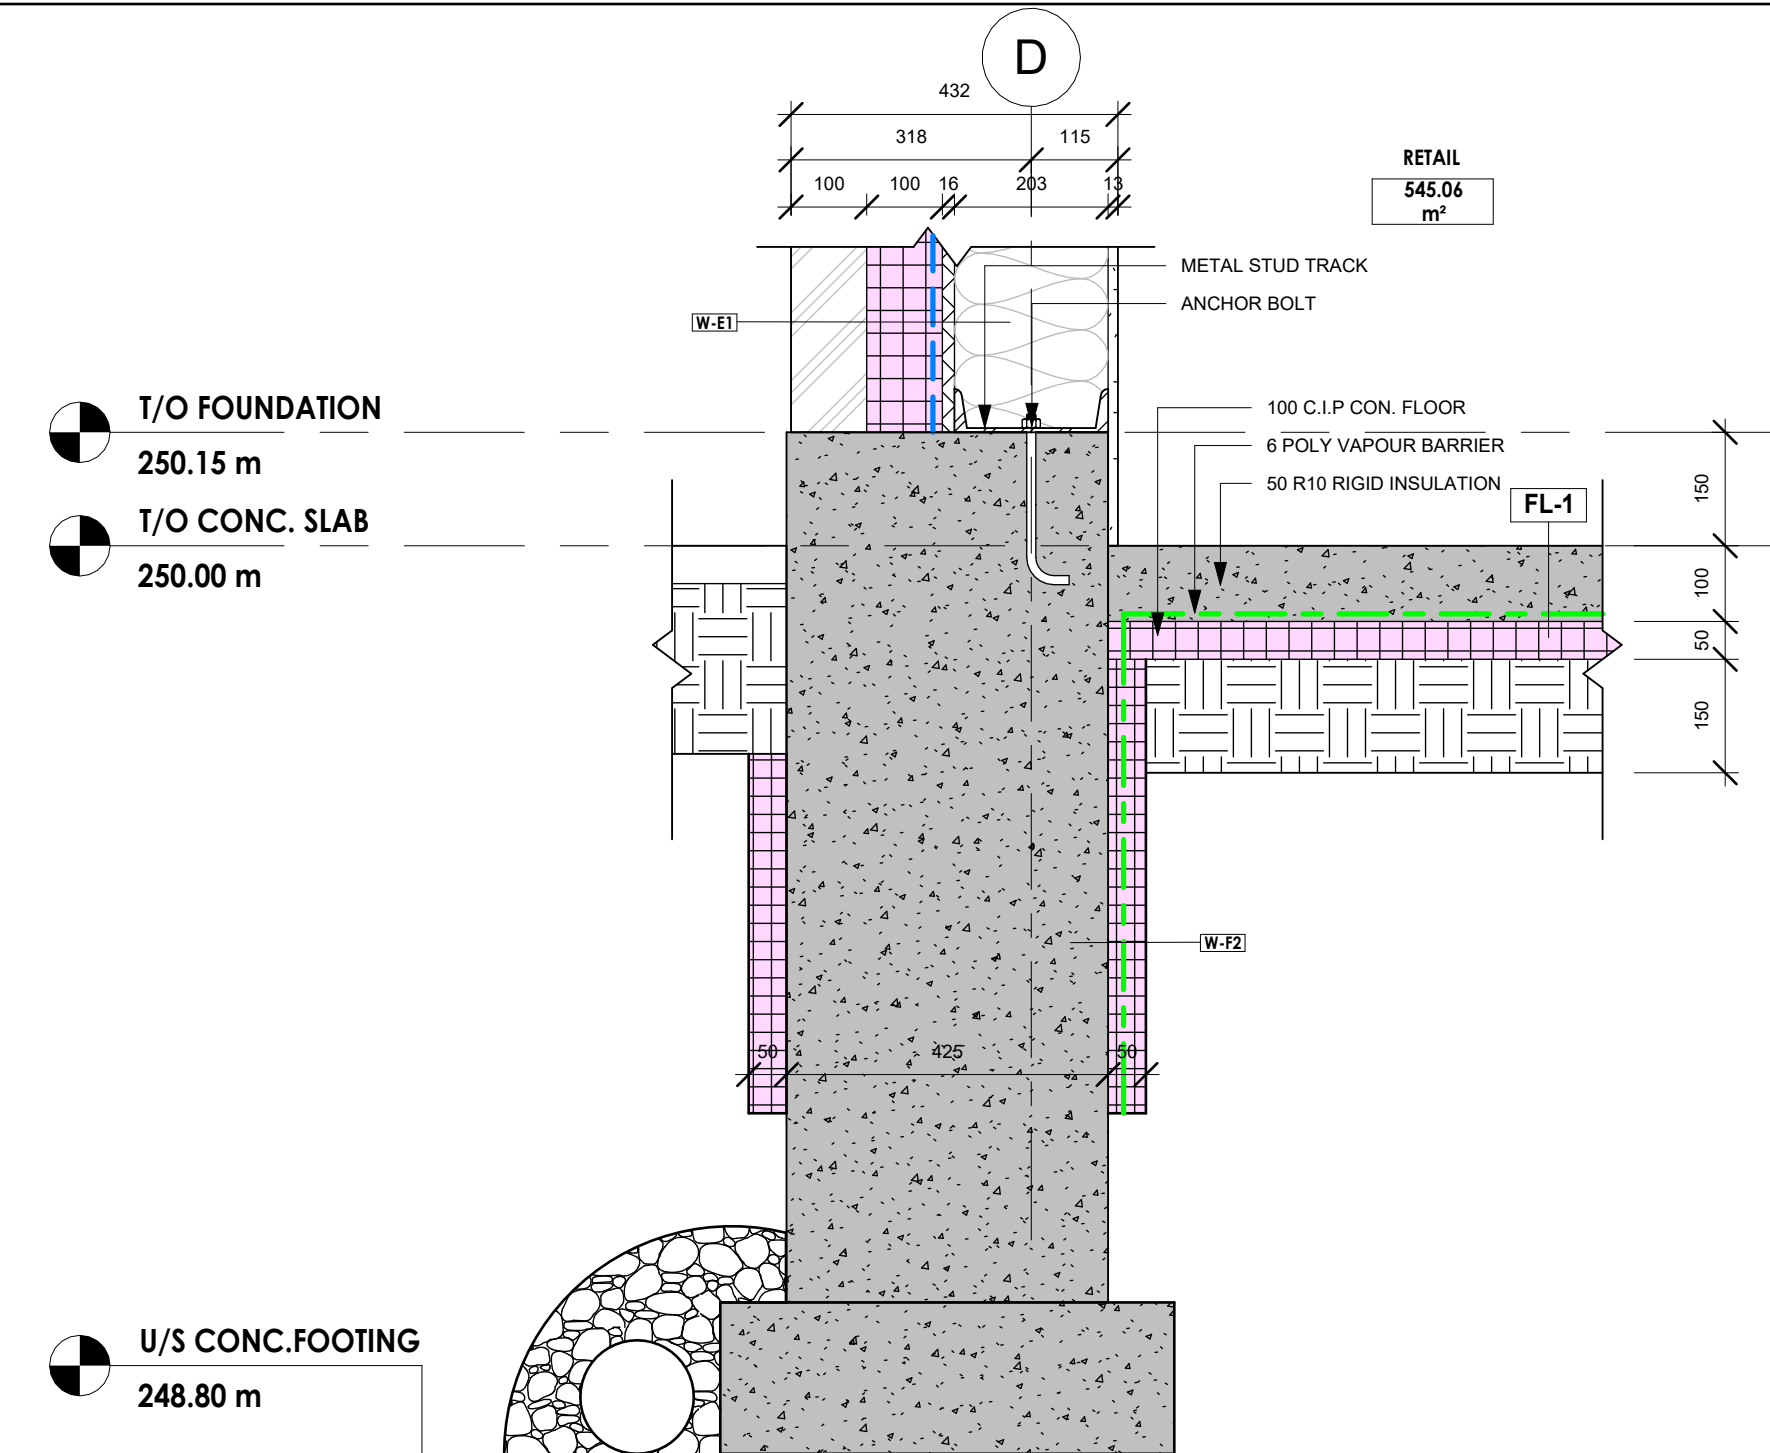


TYP. FOUND. DET.
1 : 10

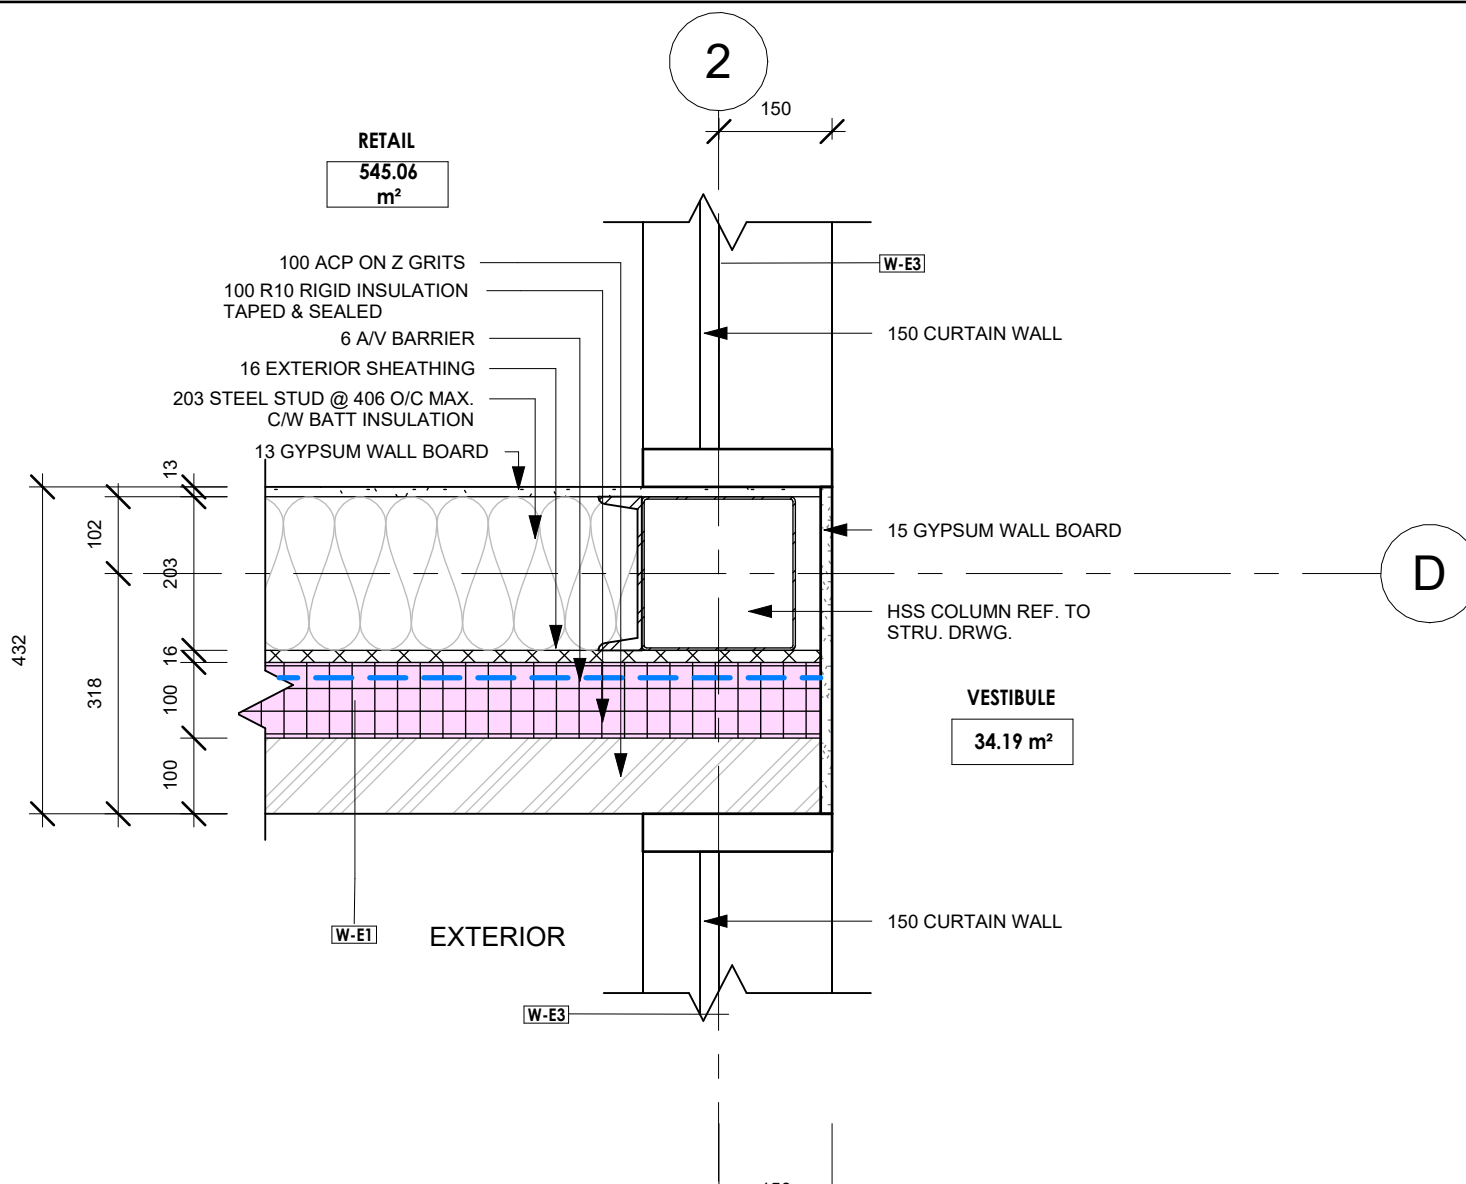


INT. COR. PLAN DET.
1 : 10

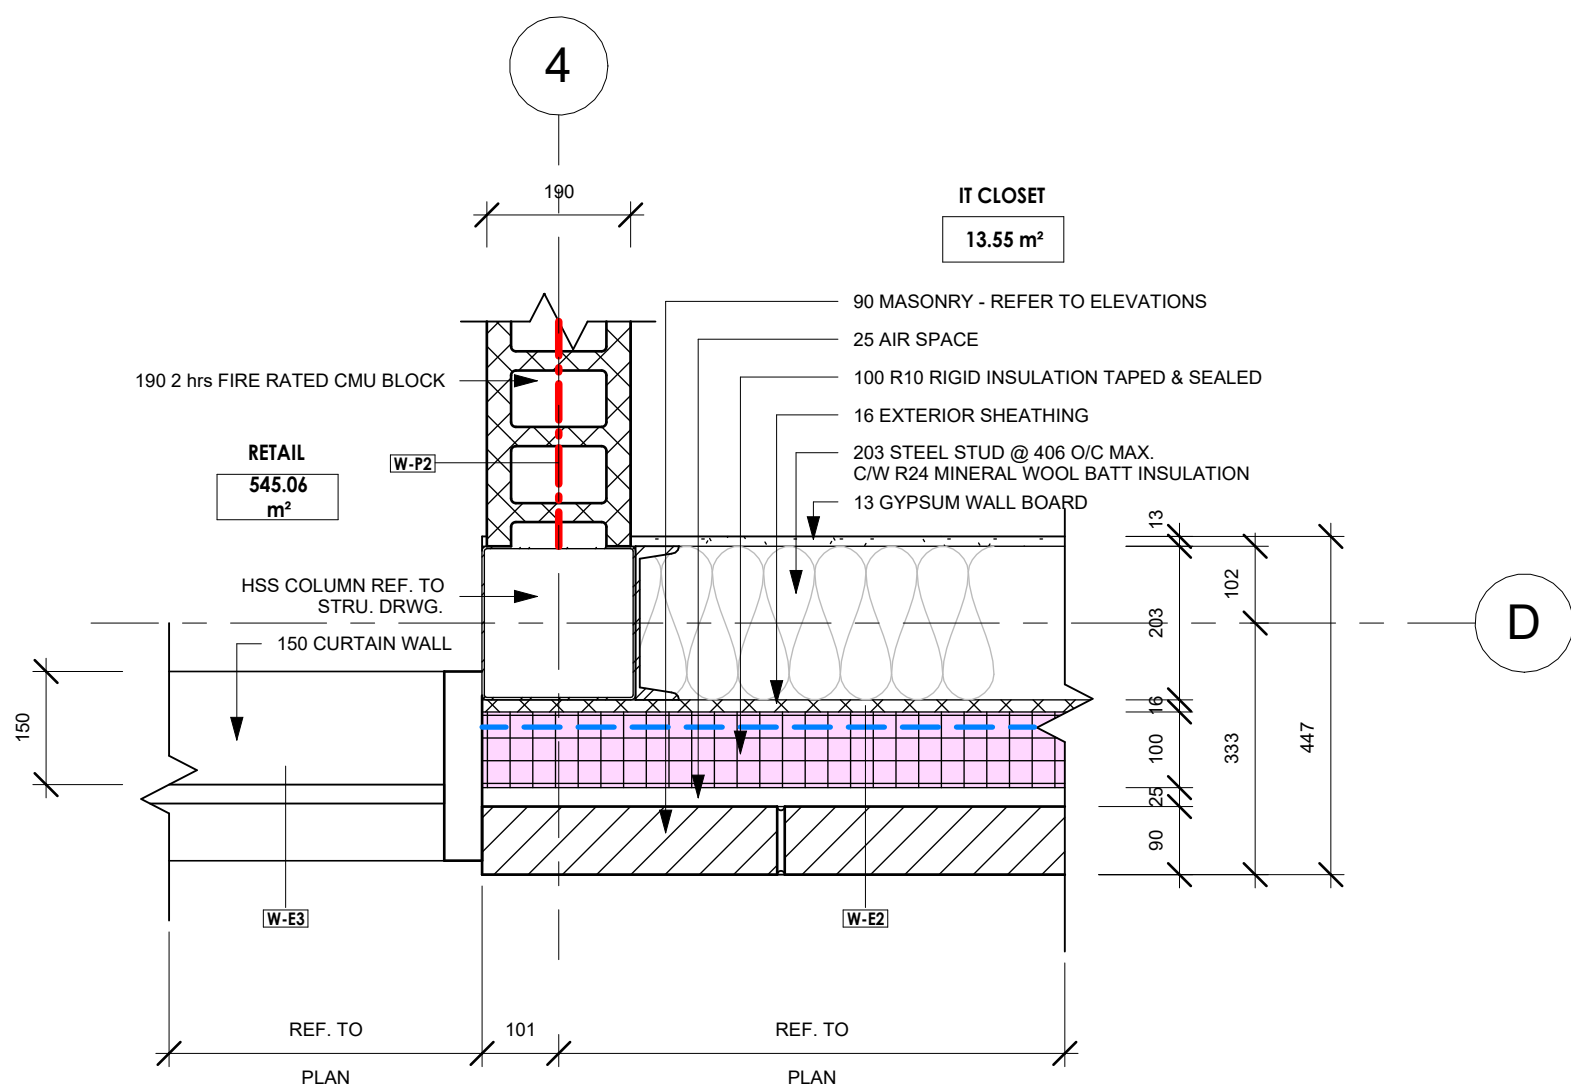


INT. COR. PLAN DET. 2
1 : 10

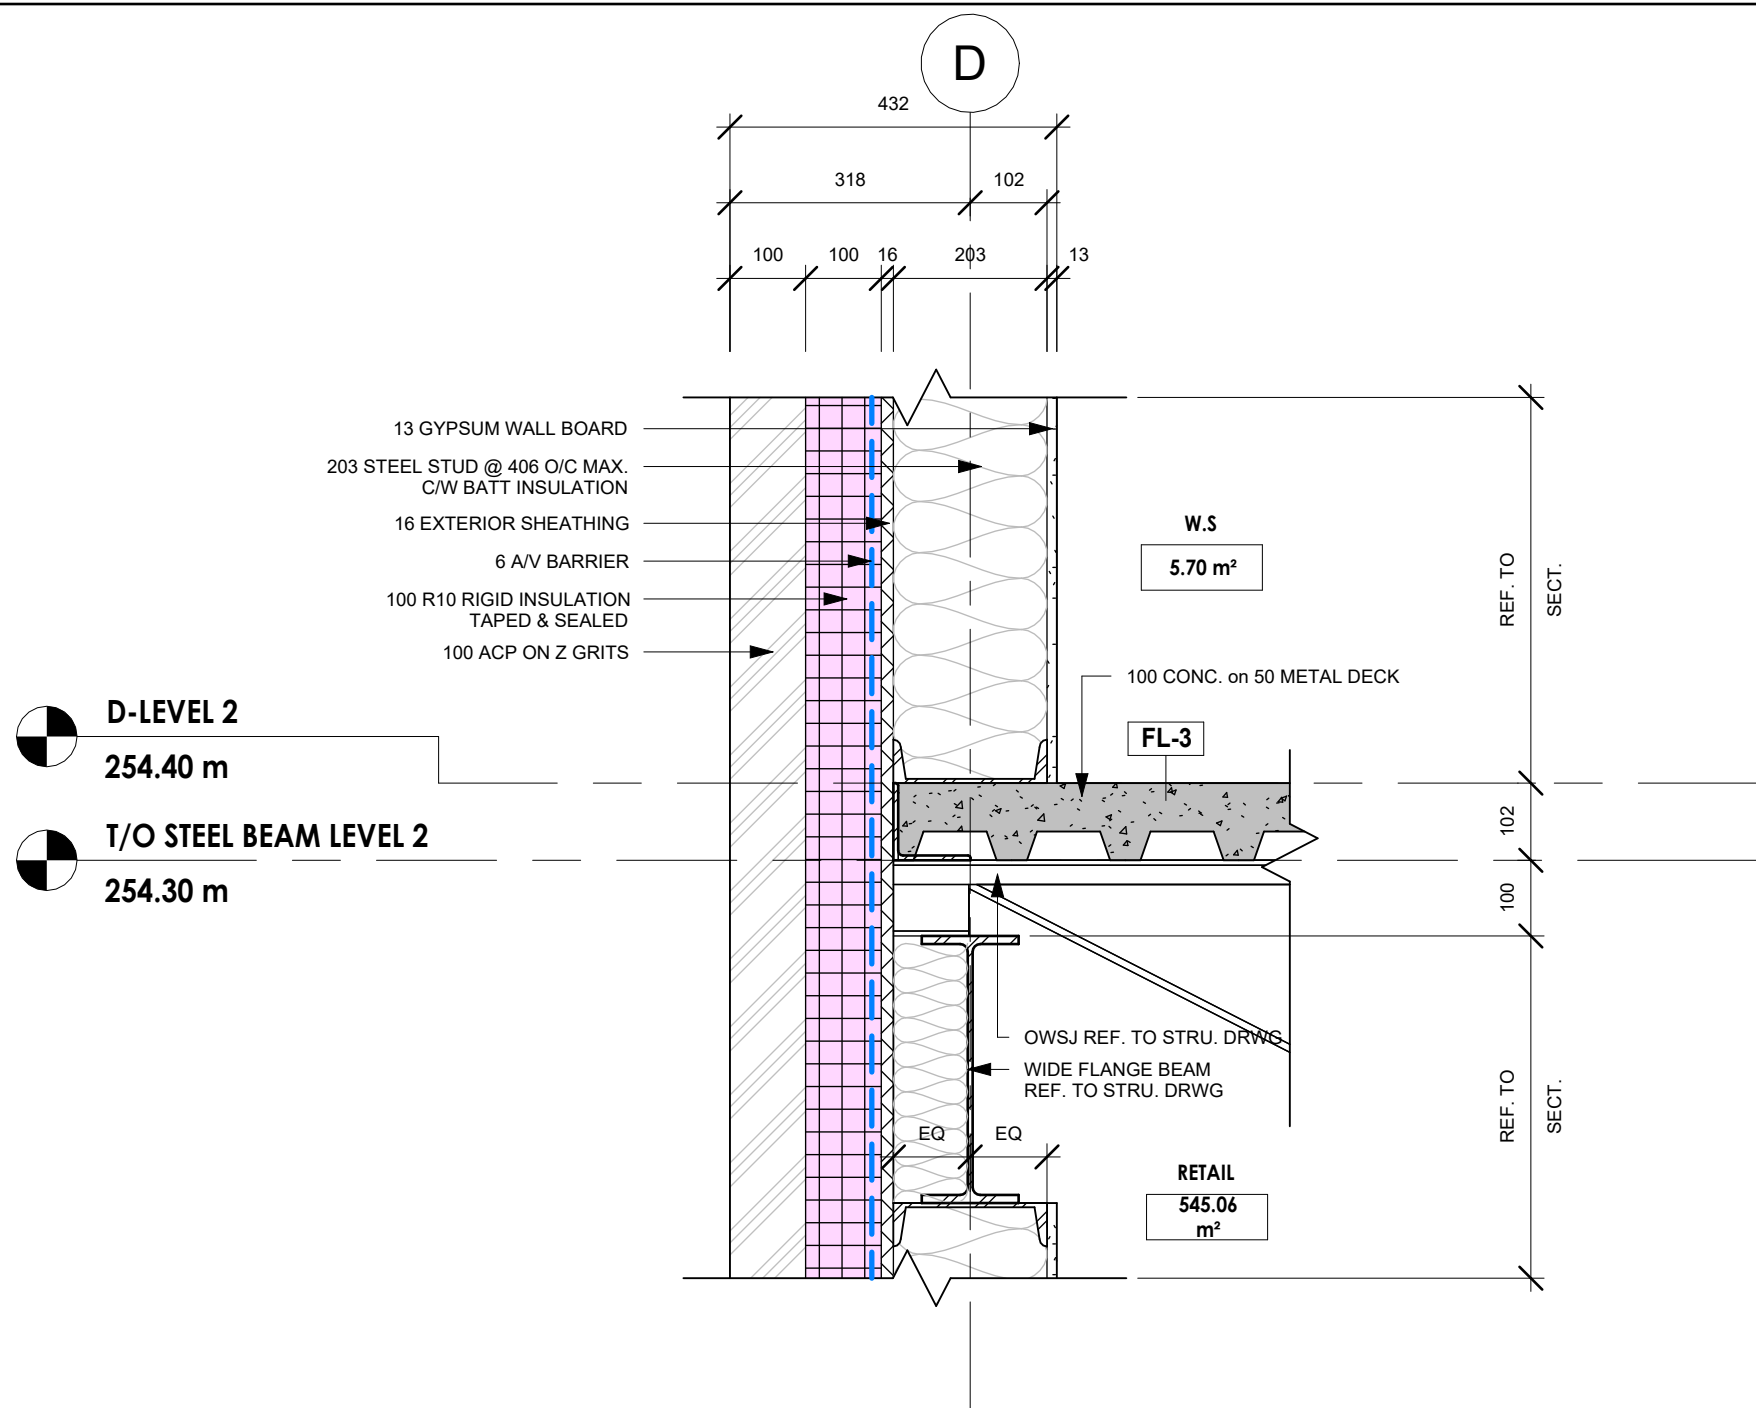

TYP. WALL TO FLOOR CONN.
1 : 10

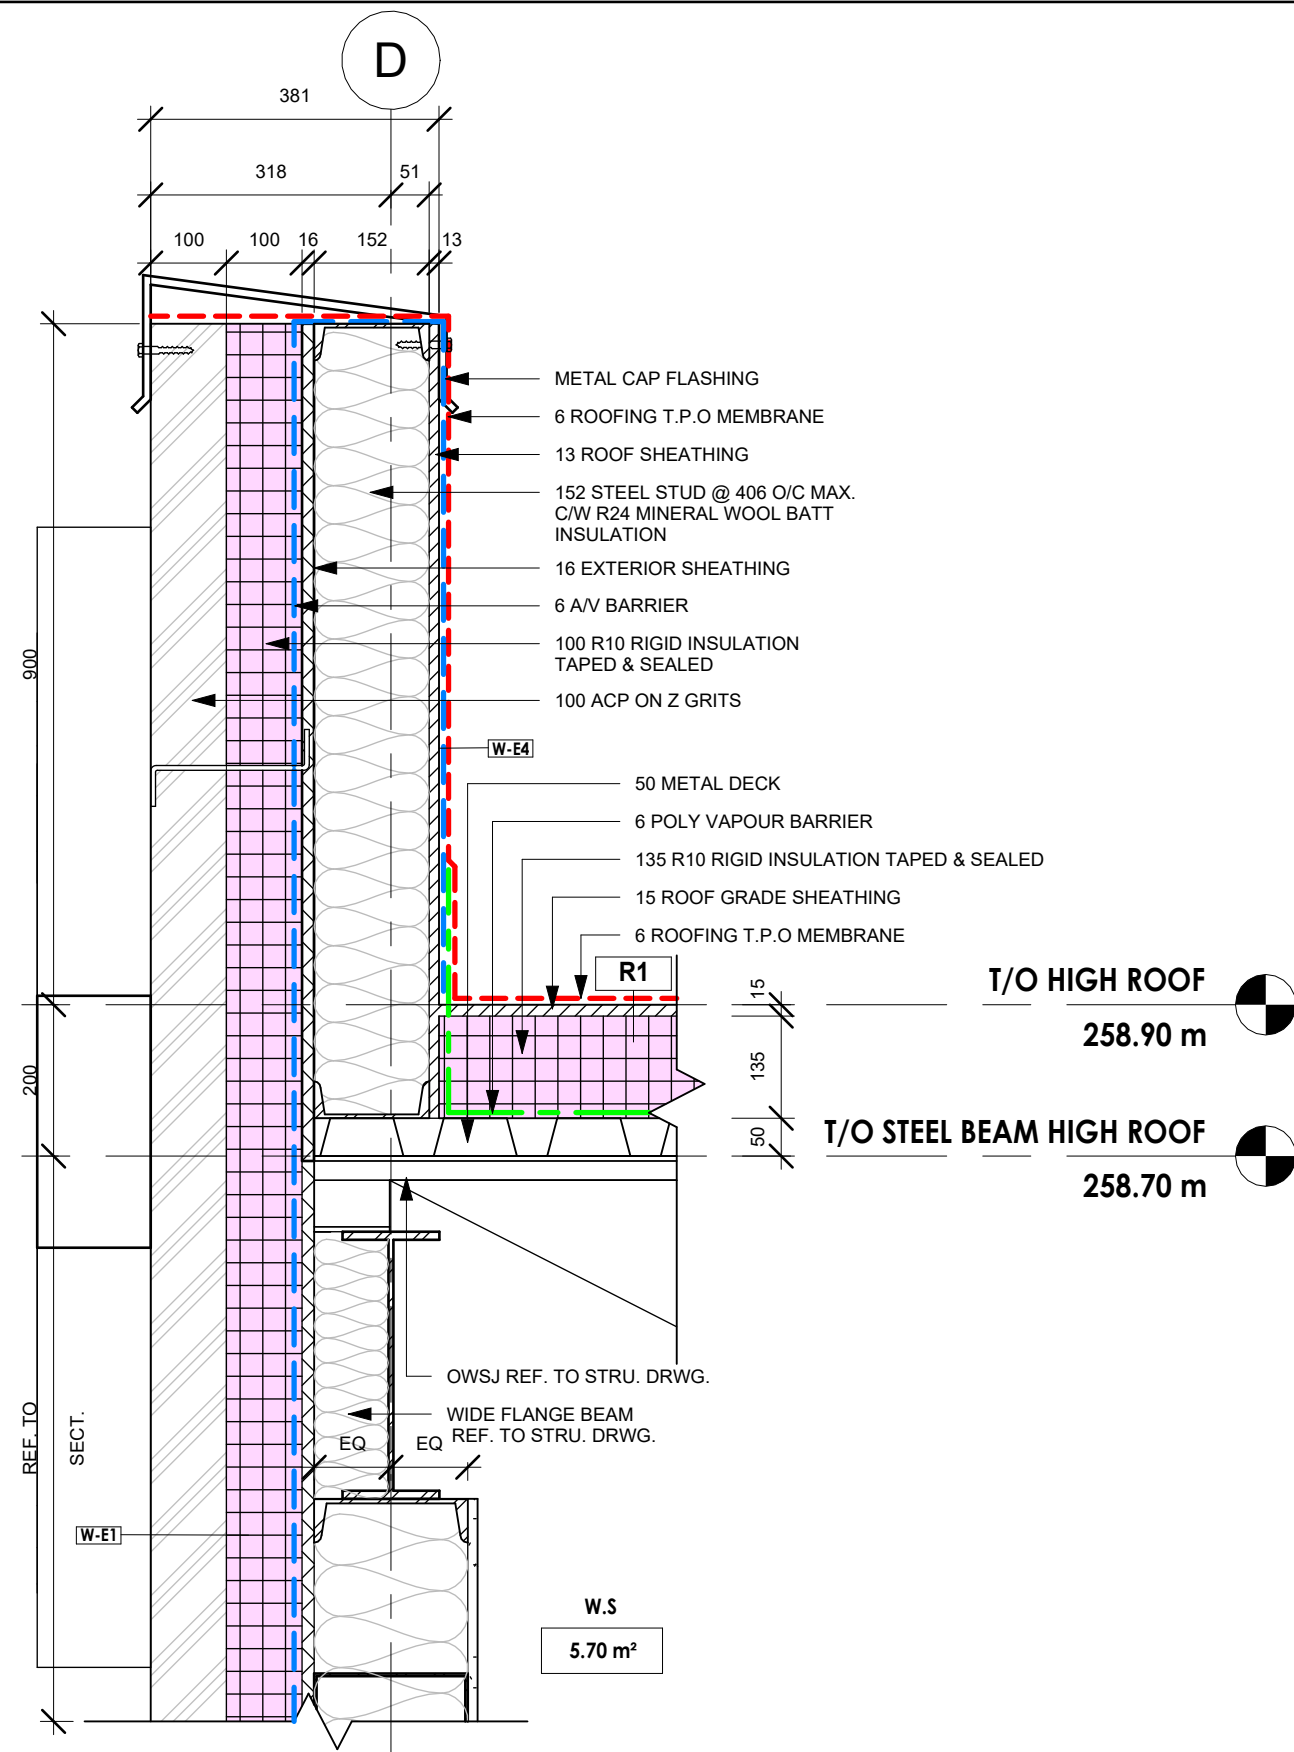

A.C.M PARA. SEC. DET.
1 : 10

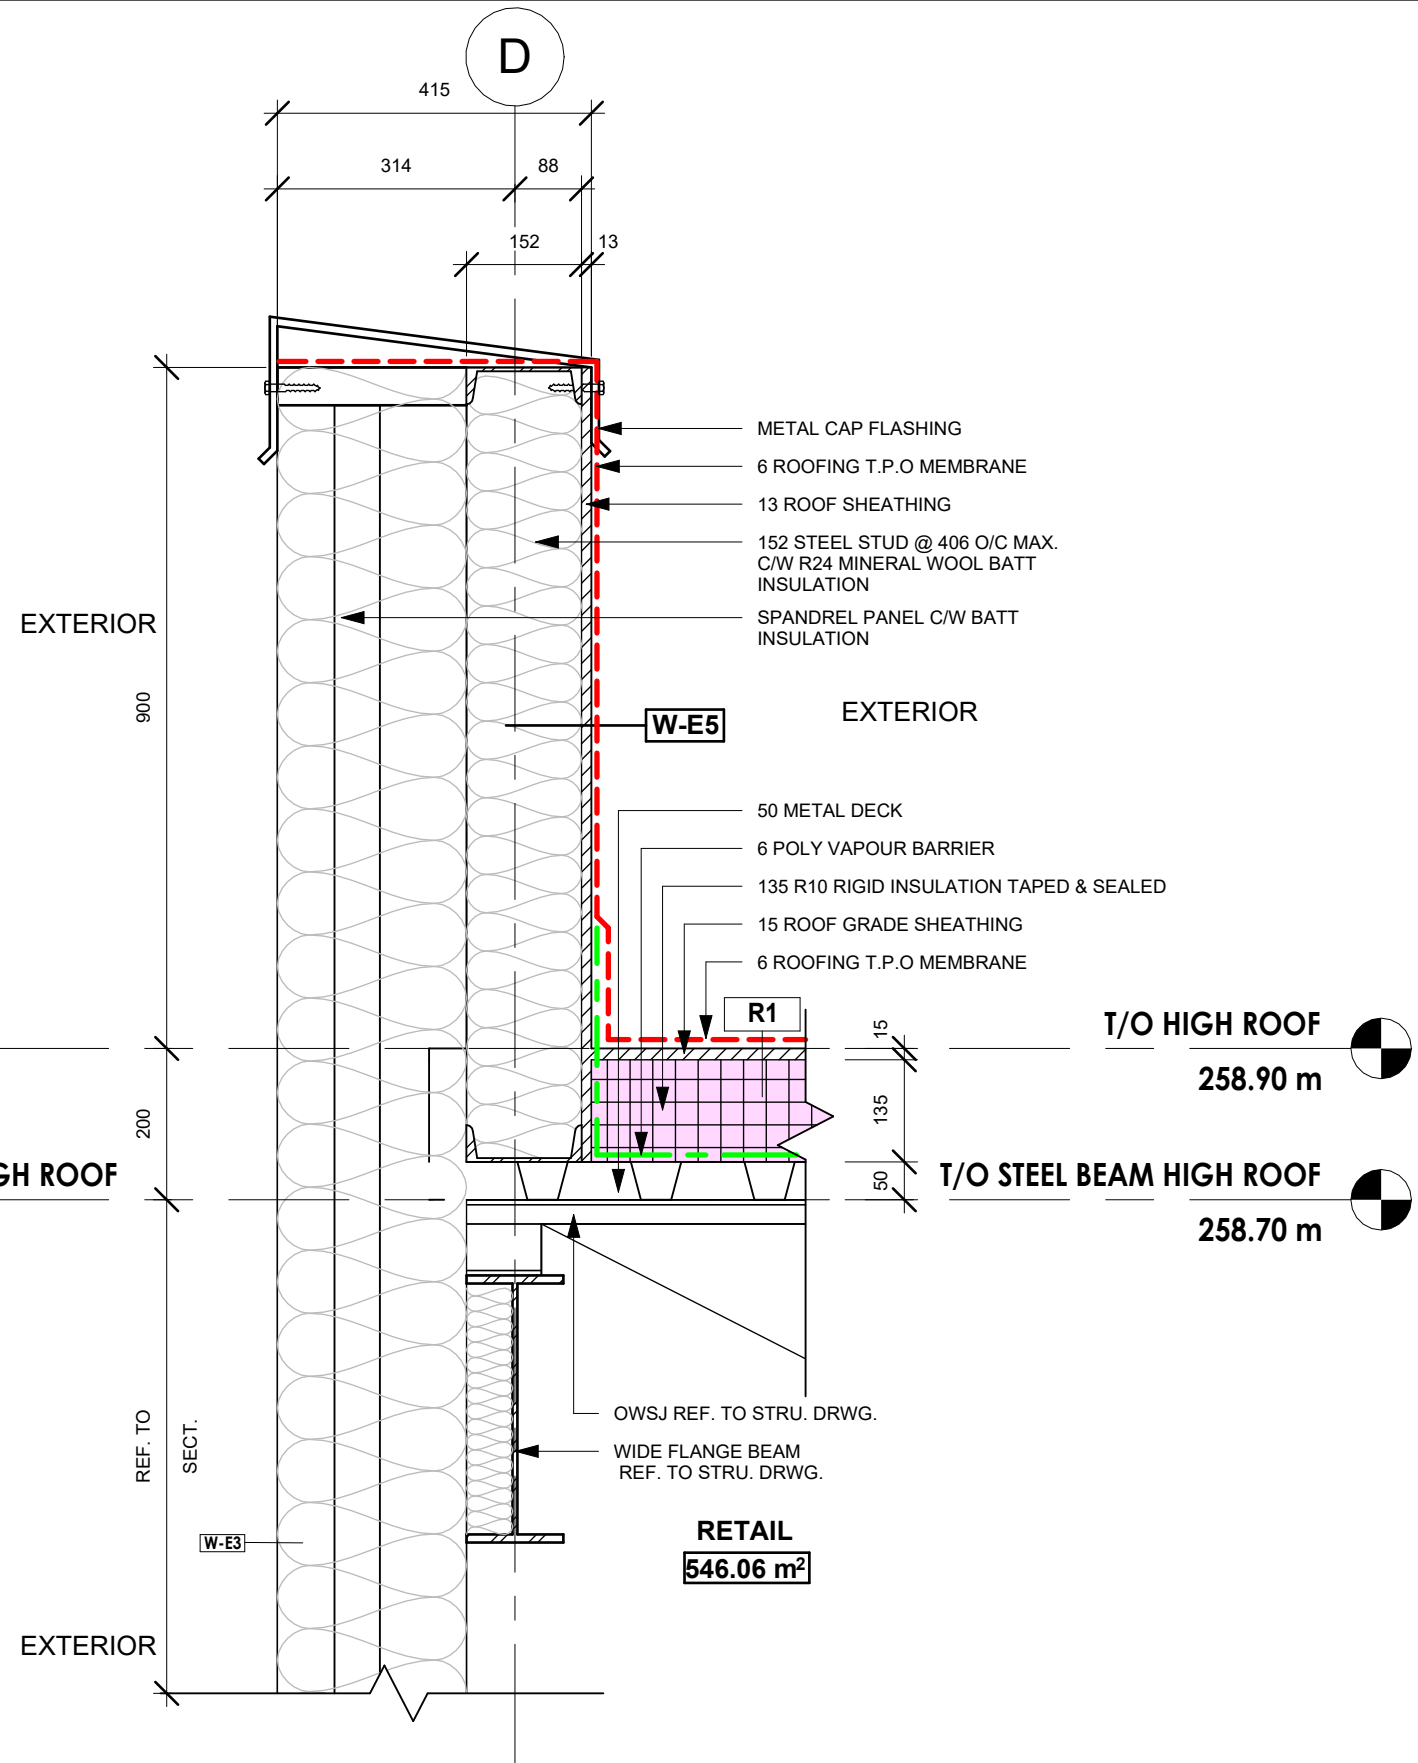

C.W PARA. SEC. DET.
1 : 10