

RICKETY RIDGE - LUXURY TOWNHOMES

Multi Unit Residential
Complex - Rental

PROJECT TEAM:

CONSULTANT:
ARCHITECTURE

CONSULTANT:
STRUCTURAL ENGINEERING

Consultant:
Construction Management

CONSULTANT:
BUILDING SERVICES

CONSULTANT:
CIVIL ENGINEERING

CONSULTANT:
LANDSCAPE ARCHITECTURE




REVISIONS

NO. | DATE | REVISION | BY

Item	ONTARIO BUILDING CODE DATA MATRIX PARTS 3 AND 9										OBC REFERENCE	
1	PROJECT DESCRIPTION: ☒ New ☐ Addition ☐ Change of Use ☐ Alteration ☒ Part 11 ☐ Part 3 ☐ Part 9										2.1.1	9.10.1.3	
2	MAJOR OCCUPANCY(S): GROUP C RESIDENTIAL										3.1.2.1.(1)	9.10.2	
3	BUILDING AREA (M2): Existing: _____ New: _____ Total: _____										1.1.3.2	1.1.3.2	
4	GROSS AREA: Existing: _____ New: _____ Total: _____										1.1.3.2	1.1.3.2	
5	NUMBER OF STOREYS: Above Grade: <u>3</u> Below Grade: _____										3.2.1.18.1.3.2	2.1.1.3	
6	HEIGHT OF BUILDING: 3 STORY WITH ROOF											2.1.1.3	
7	NUMBER OF STREETS/ACCESS ROUTE(S): FACING 1/2 STREETS - SEE SITE										3.2.2.10&3.2.5.5	
8	BUILDING CLASSIFICATION: PART 9										3.2.2.20 - 83	9.10.4	
9	SPRINKLER SYSTEM PROPOSED: ☐ ENTIRE BUILDING ☐ BASEMENT ONLY ☐ IN LIEU OF ROOF RATING ☒ NOT REQUIRED										3.2.2.20 - 83	9.10.4	
10	STANDPIPE REQUIRED: ☒ Yes ☐ No										3.2.9	
11	FIRE ALARM REQUIRED: ☒ Yes ☐ No										3.2.4	9.10.7.2	
12	WATER SERVICE / ADEQUATE SUPPLY: ☒ Yes ☐ No	
13	HIGH BUILDING: ☒ Yes ☒ No										3.2.6	
14	PERMITTED CONSTRUCTION: ☒ Combustible ☐ Non-combustible ACTUAL CONSTRUCTION: ☒ Combustible ☐ Non-combustible										3.2.2.20 - 83	9.10.6	
15	MEZZANINE AREA (M2):										3.2.1.1.(3)-(8)	9.10.4.1	
16	OCCUPANT LOAD BASED ON: ☒ m2 / person ☒ Design of Building BASEMENT: Occupancy: _____ Load: _____ Persons 1ST FLOOR: Occupancy: _____ Load: _____ Persons 2ND FLOOR: Occupancy: _____ Load: _____ Persons 3RD FLOOR: Occupancy: _____ Load: _____ Persons 4TH FLOOR: Occupancy: _____ Load: _____ Persons										3.1.1.6	9.9.1.3	
17	BARRIER FREE: ☒ Yes ☒ No (Explain): _____										3.8	9.5.2	
18	HAZARDOUS SUBSTANCES: ☒ Yes ☒ No (Explain): _____										3.3.1.2(1) 3.3.1.18(1)	9.10.1.3	
19	REQUIRED FIRE RESISTANCE RATING (FRR) HORIZONTAL ASSEMBLIES (FRR - Hours) Floor(s): <u>1</u> Hours Roof: <u>0</u> Hours Mezzanine(s): _____ Hours FRR Supporting Member(s): _____ LISTED DESIGN NO. OR DESCRIPTION (SB-3 SG-2) Listed Design No. or Description (SG-2)										3.2.1.4 3.2.2.20 - 83	9.10.8 9.10.9	
20	SPATIAL SEPARATION - CONSTRUCTION OF EXTERIOR WALLS: <table><tr><th>Wall:</th><th>Area of EBF: (m2)</th><th>L.D.: (m)</th><th>L/H: or H/L</th><th>Permitted Max. % of Openings</th><th>Proposed Max. % of Openings</th><th>FRR (Hours)</th><th>Listed Design or Description</th><th>Comb. Const.</th><th>Comb. Const. Nonc. Cladding</th><th>Non Comb. Const.</th></tr><tr><td>North:</td><td></td><td></td><td></td><td></td><td></td><td></td><td></td><td></td><td></td><td></td></tr><tr><td>South:</td><td></td><td></td><td></td><td></td><td></td><td></td><td></td><td></td><td></td><td></td></tr><tr><td>East:</td><td></td><td></td><td></td><td></td><td></td><td></td><td></td><td></td><td></td><td></td></tr><tr><td>West:</td><td></td><td></td><td></td><td></td><td></td><td></td><td></td><td></td><td></td><td></td></tr></table>										Wall:	Area of EBF: (m2)	L.D.: (m)	L/H: or H/L	Permitted Max. % of Openings	Proposed Max. % of Openings	FRR (Hours)	Listed Design or Description	Comb. Const.	Comb. Const. Nonc. Cladding	Non Comb. Const.	North:											South:											East:											West:											3.2.3	9.10.14
Wall:	Area of EBF: (m2)	L.D.: (m)	L/H: or H/L	Permitted Max. % of Openings	Proposed Max. % of Openings	FRR (Hours)	Listed Design or Description	Comb. Const.	Comb. Const. Nonc. Cladding	Non Comb. Const.	
North:	
South:	
East:	
West:	

GENERAL NOTES:

- DRAWINGS ARE NOT TO BE SCALED.
- ALL DIMENSIONS AND INSTALLATIONS ARE TO BE VERIFIED ON SITE.
- CONTRACTOR TO COMPLY TO ONTARIO BUILDING CODE (OBC) 2024 IN ADDITION TO ANY AND ALL AUTHORITIES HAVING JURISDICTION DURING ALL PHASES OF WORK.
- IT IS THE CONTRACTOR'S RESPONSIBILITY TO BRING ALL OMISSIONS, DISCREPANCIES, INCLUDING DIMENSIONS, TO THE ATTENTION OF THE ARCHITECT PRIOR TO THE COMMENCING OF ANY WORK.
- ANY PATCHING, REPAIR, REFINISHING, RECONSTRUCTION AND REPAINTING WORK REQUIRED AS A RESULT OF PERFORMANCE OF WORK UNDER THIS CONTRACT SHALL BE PERFORMED WITH MATERIALS TO MATCH EXISTING AND SHALL MAINTAIN REQUIRED FIRE RATINGS.
- IT IS THE CONTRACTOR'S RESPONSIBILITY TO ENSURE THAT WHEREVER A FIRE SEPARATION IS REQUIRED AS INDICATED BY THE CONSTRUCTION DRAWINGS, ALL COMPONENTS OF THE ASSEMBLY ARE TO BE APPROVED MATERIALS WITHIN THE INSTALLATION/FABRICATION PROCEDURES PER DIRECTIONS OF THE U.L.C. NUMBER AND/OR REQUIREMENTS OF THE OBC 2025. ALL FIRE SEPARATIONS MUST BE CONTINUOUS WITHIN THEIR EXTENT, AND ALL JOINTS TO BE AIR TIGHT.
- DIMENSIONS INDICATED ON FLOOR PLANS ARE TO GRID LINE. EXTERIOR FACE OF SHEATHING FOR EXTERIOR WALLS, OR CENTERLINE OF INTERIOR PARTITIONS. SEE FLOOR PLANS FOR ADDITIONAL DIMENSION NOTES.
- WHERE TYPE "X" GYPSUM BOARD IS NOTED ON DRAWINGS, PROVIDE FIRE-RESISTANT GYPSUM BOARD C/W U.L.C. LABEL.
- WHEN A PARTITION OCCURS ALONG A CONTROL JOINT, FASTEN THE TRACK TO ONE SIDE ONLY.
- GYPSUM BOARD CONTROL JOINTS ARE TO BE AT 900mm O.C. MAXIMUM, OR AS OTHERWISE SPECIFIED OR SHOWN.
- PROVIDE 19mm PLYWOOD BACKING AT TELEPHONE AND SURFACE MOUNTED ELECTRICAL PANEL LOCATIONS. PAINT PRIOR TO INSTALLATION WITH FIRE-RETARDANT PAINT.
- PROVIDE SHEET STEEL BACKING IN STUD PARTITIONS BEHIND GYPSUM BOARD AT ALL RECESSED OR SURFACE MOUNTED EQUIPMENT, MILLWORK, AND ACCESSORIES AT ALL ANCHOR POINTS. BACKING TO BE 19ga. GALVANIZED METAL IN 300mm WIDE STRIPS FASTENED TO 3 STUDS MINIMUM.
- IT IS THE CONTRACTOR'S RESPONSIBILITY TO COORDINATE HIS OWN FORCES AND HIS SUB TRADES TO ENSURE THAT HOLES CUT FOR PENETRATIONS THROUGH THE EXTERIOR WALL SYSTEMS ARE NOT OVERSIZED. AFTER INSTALLATION OF ANY PENETRATIONS, THE VOIDS BETWEEN THE PENETRATION OPENING AND THE PENETRATED MATERIALS SHALL BE COMPLETELY SEALED TO ENSURE THE INTEGRITY OF THE AIR/VAPOUR BARRIER.
- SEAL ALL ARCHITECTURAL, STRUCTURAL, MECHANICAL OR ELECTRICAL PENETRATIONS IN WALL AND/OR FLOOR ASSEMBLIES WITH AN APPROVED PRODUCT / SYSTEM TO MAINTAIN REQUIRED FIRE RATING AND ACOUSTICAL MINIMUMS.
- THESE ARCHITECTURAL DRAWINGS SHALL BE READ IN CONJUNCTION WITH SURVEY, STRUCTURAL, MECHANICAL AND ELECTRICAL DRAWINGS.
- ALL CEILING HEIGHTS SHOWN ON THE REFLECTED CEILING PLANS ARE RELATED TO A CLEAR DIMENSION ABOVE THE FLOOR LOCATED DIRECTLY BELOW THE CEILING.
- ALL INTERIOR FRAMED PARTITIONS ARE TO BE BRACED BACK TO THE STRUCTURE ABOVE THE SUSPENDED CEILING SYSTEM USING METAL STUD @ MAXIMUM 1200mm O.C. EACH SIDE OF WALL.
- WHERE FRAMED DRYWALL PARTITIONS ARE TO EXTEND UP TO THE UNDERSIDE OF ROOF OR FLOOR STRUCTURES PROVIDE A DOUBLE TOP TRACK ASSEMBLY TO ALLOW FOR A VERTICAL DEFLECTION OF 25mm. TYPICAL TRACK ASSEMBLY SHALL CONSIST OF A 50mm DEEP TRACK AND STANDARD TRACK IN COMBINATION WITH WALL BOARD FASTENED TO STUD ONLY. THE JOINTS OF THE TRACK TO STRUCTURE AND GYPSUM BOARD TO THE TRACK MUST BE CAULKED AIR TIGHT.
- IN EXTERIOR WALLS WHERE DISSIMILAR SUBSTRATES MEET LAP THE JOINT OF THE DISSIMILAR SUBSTRATES WITH AIRMOISTURE BARRIER (AM/AVB) MEMBRANE TO MINIMUM 150mm EACH SIDE OF THE JOINT. TYPICAL AT ALL HORIZONTAL AND VERTICAL JOINTS. REFER ALSO TO SECTION AND PLAN DETAILS, TYPICAL.

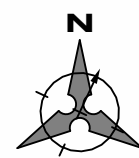

School of Building Technology
ARCHITECTURAL
TECHNOLOGY

PROJECT TITLE

RICKETY RIDGE -
LUXURY TOWNHOMES

CLIENT:

RICKETY DEVELOPMENT CORP.

PROJECT TITLE

539 PHILIP STREET
London ON.

DRAWING TITLE

COVER SHEET


CHECKED | DRAWN | DATE
GJG | AFNM | 04/15/24

00004

FILE

A0.1

DRAWING

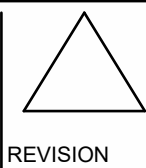



REVISION




Site Legend
1 : 750




 Zoning Cha
1 : 1

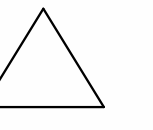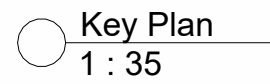

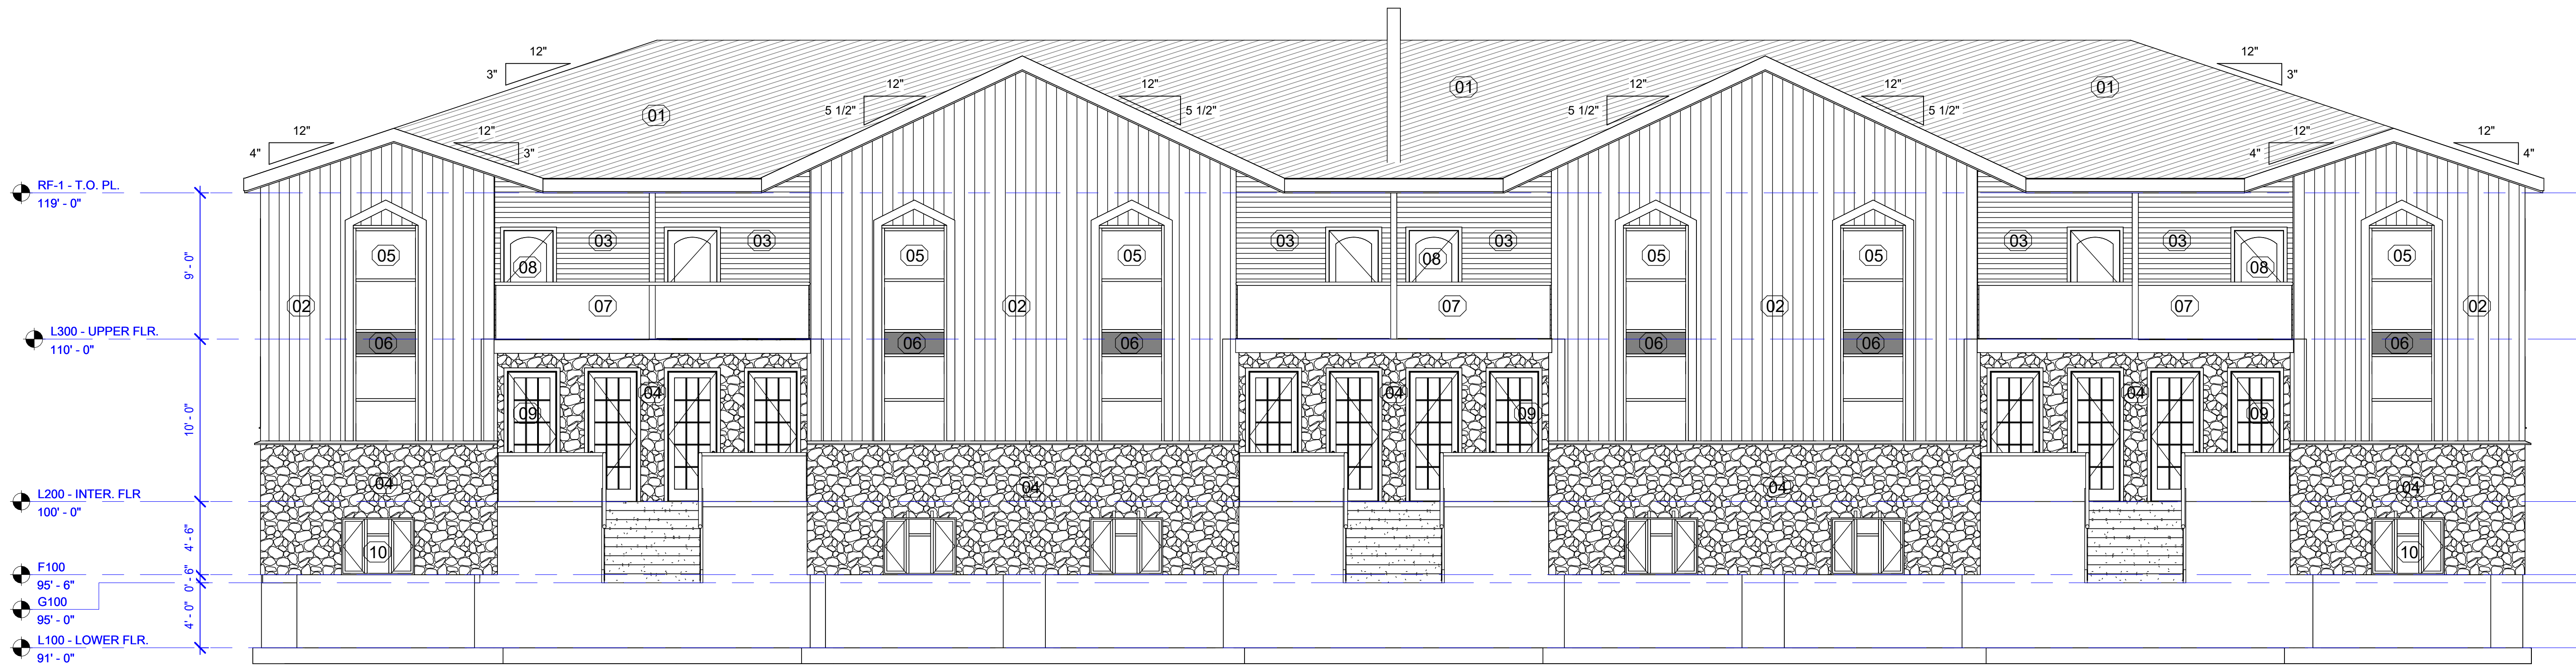


1 FRONT ELEVATION
3/16" = 1'-0"

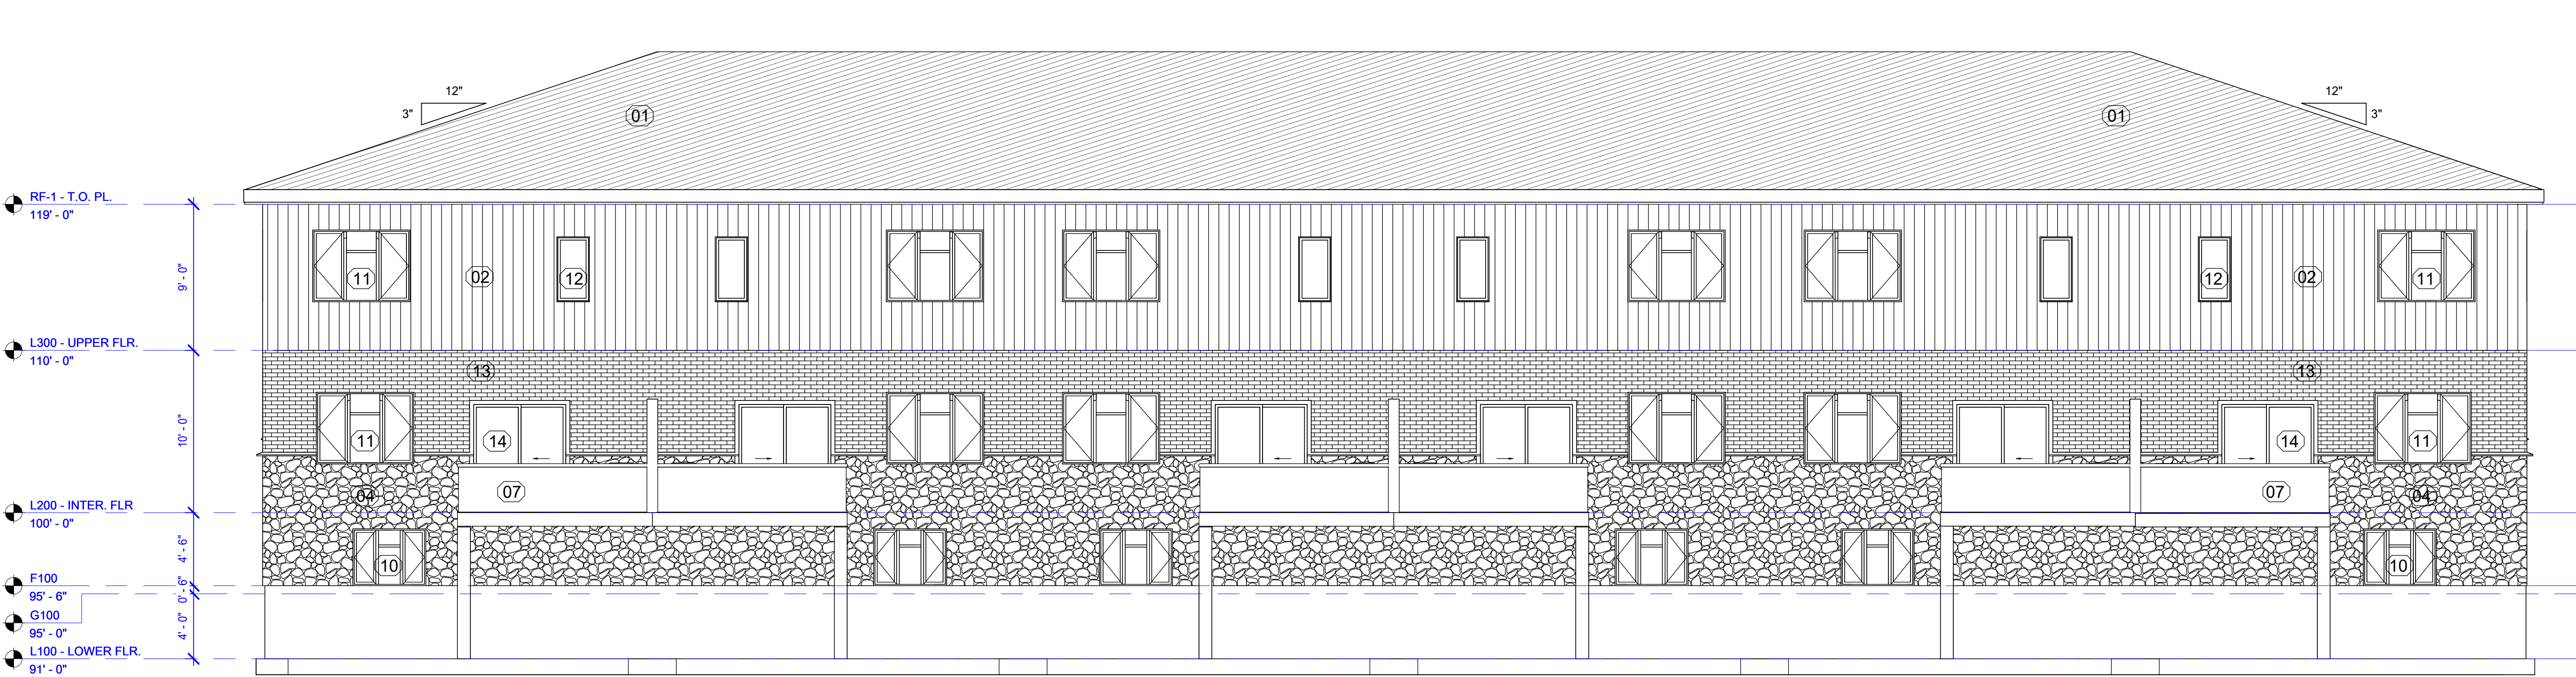


2 REAR ELEVATION
3/16" = 1'-0"

REVISIONS

NO. | DATE | REVISION | BY

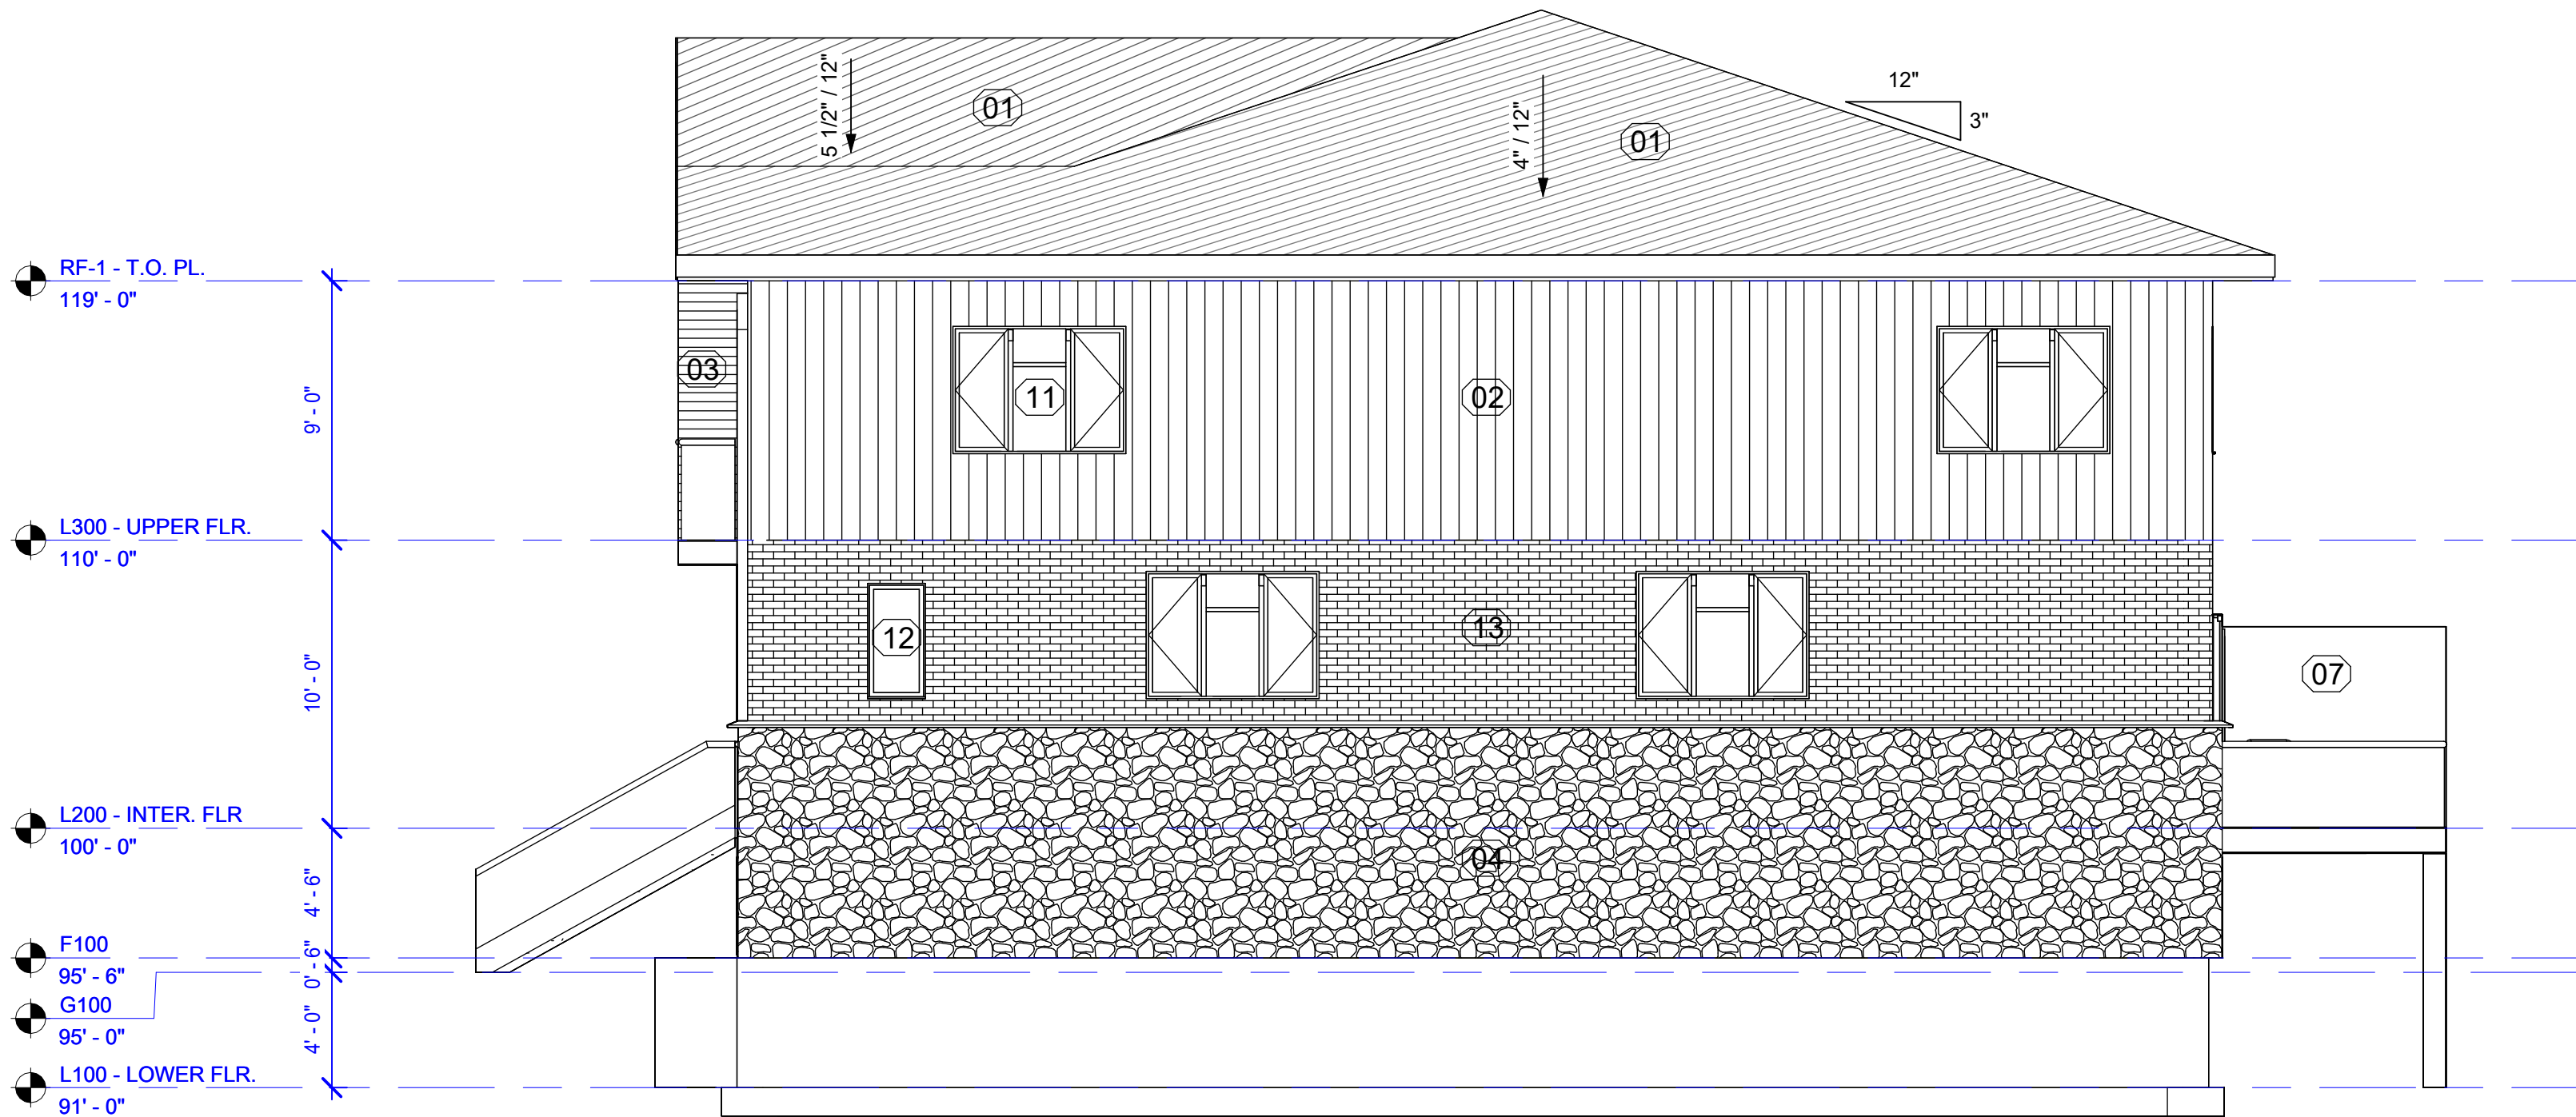

1 SIDE ELEVATION - LEFT
3/16" = 1'-0"

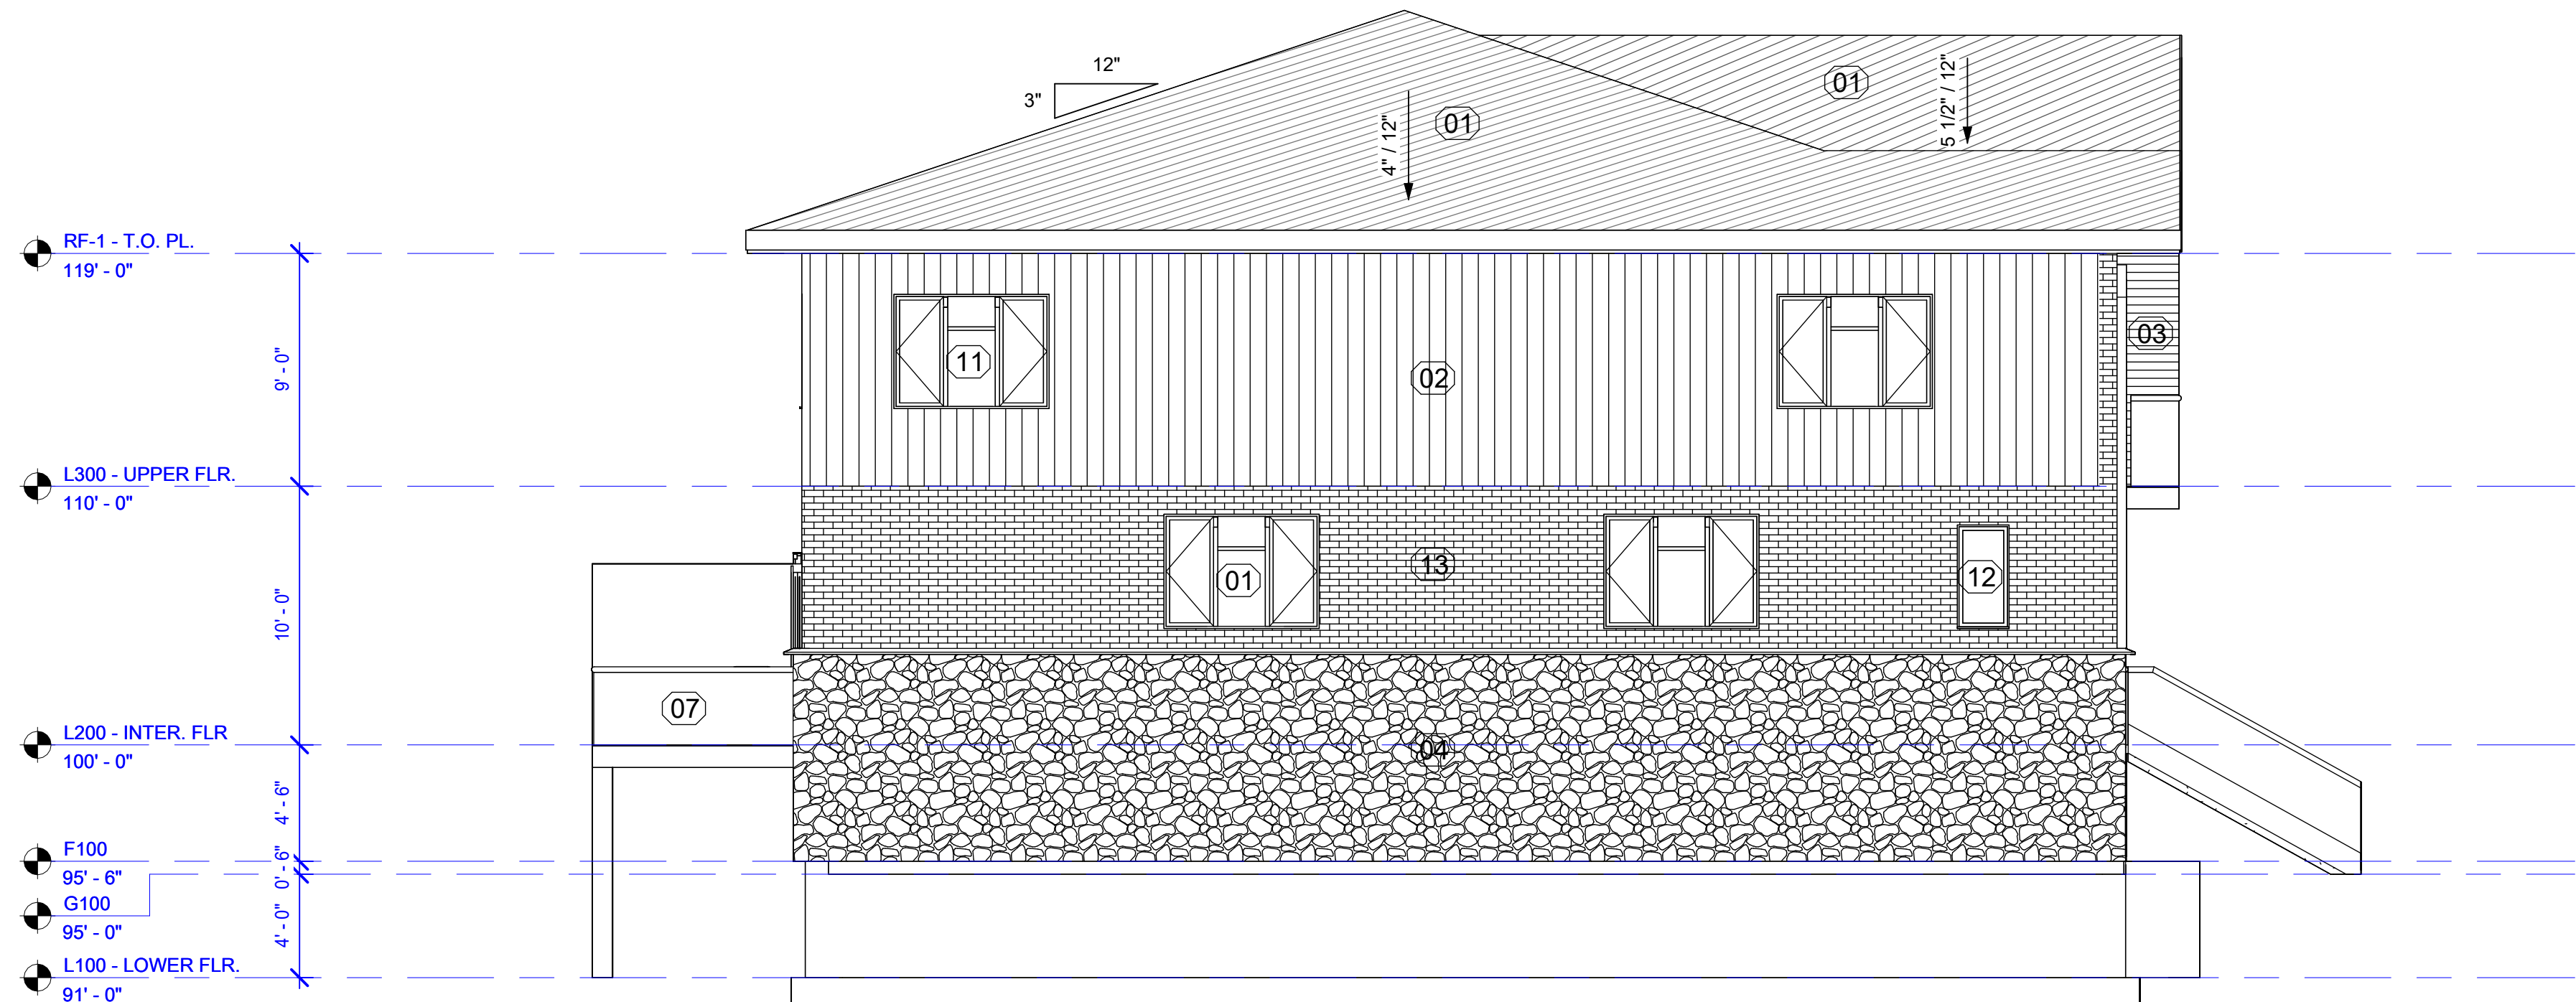

2 SIDE ELEVATION - RIGHT
3/16" = 1'-0"


DOOR SCHEDULE			
Type	Width	Height	Family and Type.
D2	3' - 0"	6' - 8"	Door-Exterior-Single-Entry-Half Arc Glass-Wood - 36" x 80"
D1	3' - 0"	8' - 0"	Door-Exterior-Single-Full Glass-Wood - 36" x 96"
D3	5' - 8"	6' - 8"	Door-Double-Sliding-68" x 80"

WINDOW SCHEDULE			
Type	Width	Height	Family and Type
W2448	2' - 0"	4' - 0"	Instance-Window-Fixed: 24" x 48"
W5442	4' - 6"	3' - 6"	Window-Casement-Triple-Middle-Transom: 54" x 42"
W7253	6' - 0"	4' - 5"	Window-Casement-Triple-Middle-Transom: 72" x 53"

MATERIAL LEGEND	
01	P.F METAL ROOFING
02	1/2" VERT. WOOD SIDING
03	1/2" HORI. WOOD SIDING
04	4" MASONRY VENEER - STONE
05	CURTAIN WALL CLEAR GLASS
06	CURTAIN WALL SPANDULAR PANEL
07	GLASS RAILING
08	EXTERIOR SINGLE DOOR 36"x86" - REFER SCHED.
09	EXTERIOR SINGLE DOOR 36"x96" - REFER SCHED.
10	EXTERIOR WINDOW 54"x42" - REFER SCHED.
11	EXTERIOR WINDOW 72"x53" - REFER SCHED.
12	FIXED WINDOW 24"x38" - REFER SCHED.
13	4" MASONRY VENEER - BRICK
14	EXT. DOU. SLIDING DOOR 64"x80" - REFER SCHED.

key plan

seal

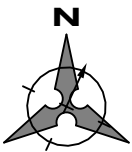

FANSHAWE

School of Building Technology
ARCHITECTURAL
TECHNOLOGY

PROJECT TITLE
RICKETY RIDGE - LUXURY
TOWNHOMES

CLIENT:
RICKETY DEVELOPMENT CORP.

PROJECT ADDRESS
539 PHILIP STREET
London ON.


DRAWING TITLE
BUILDING ELEVATIONS &
SCHEDULE

CHECKED | DRAWN | DATE
GJG | AFNM | 04/15/24


00004
FILE

A2.2
DRAWING


REVISION
1

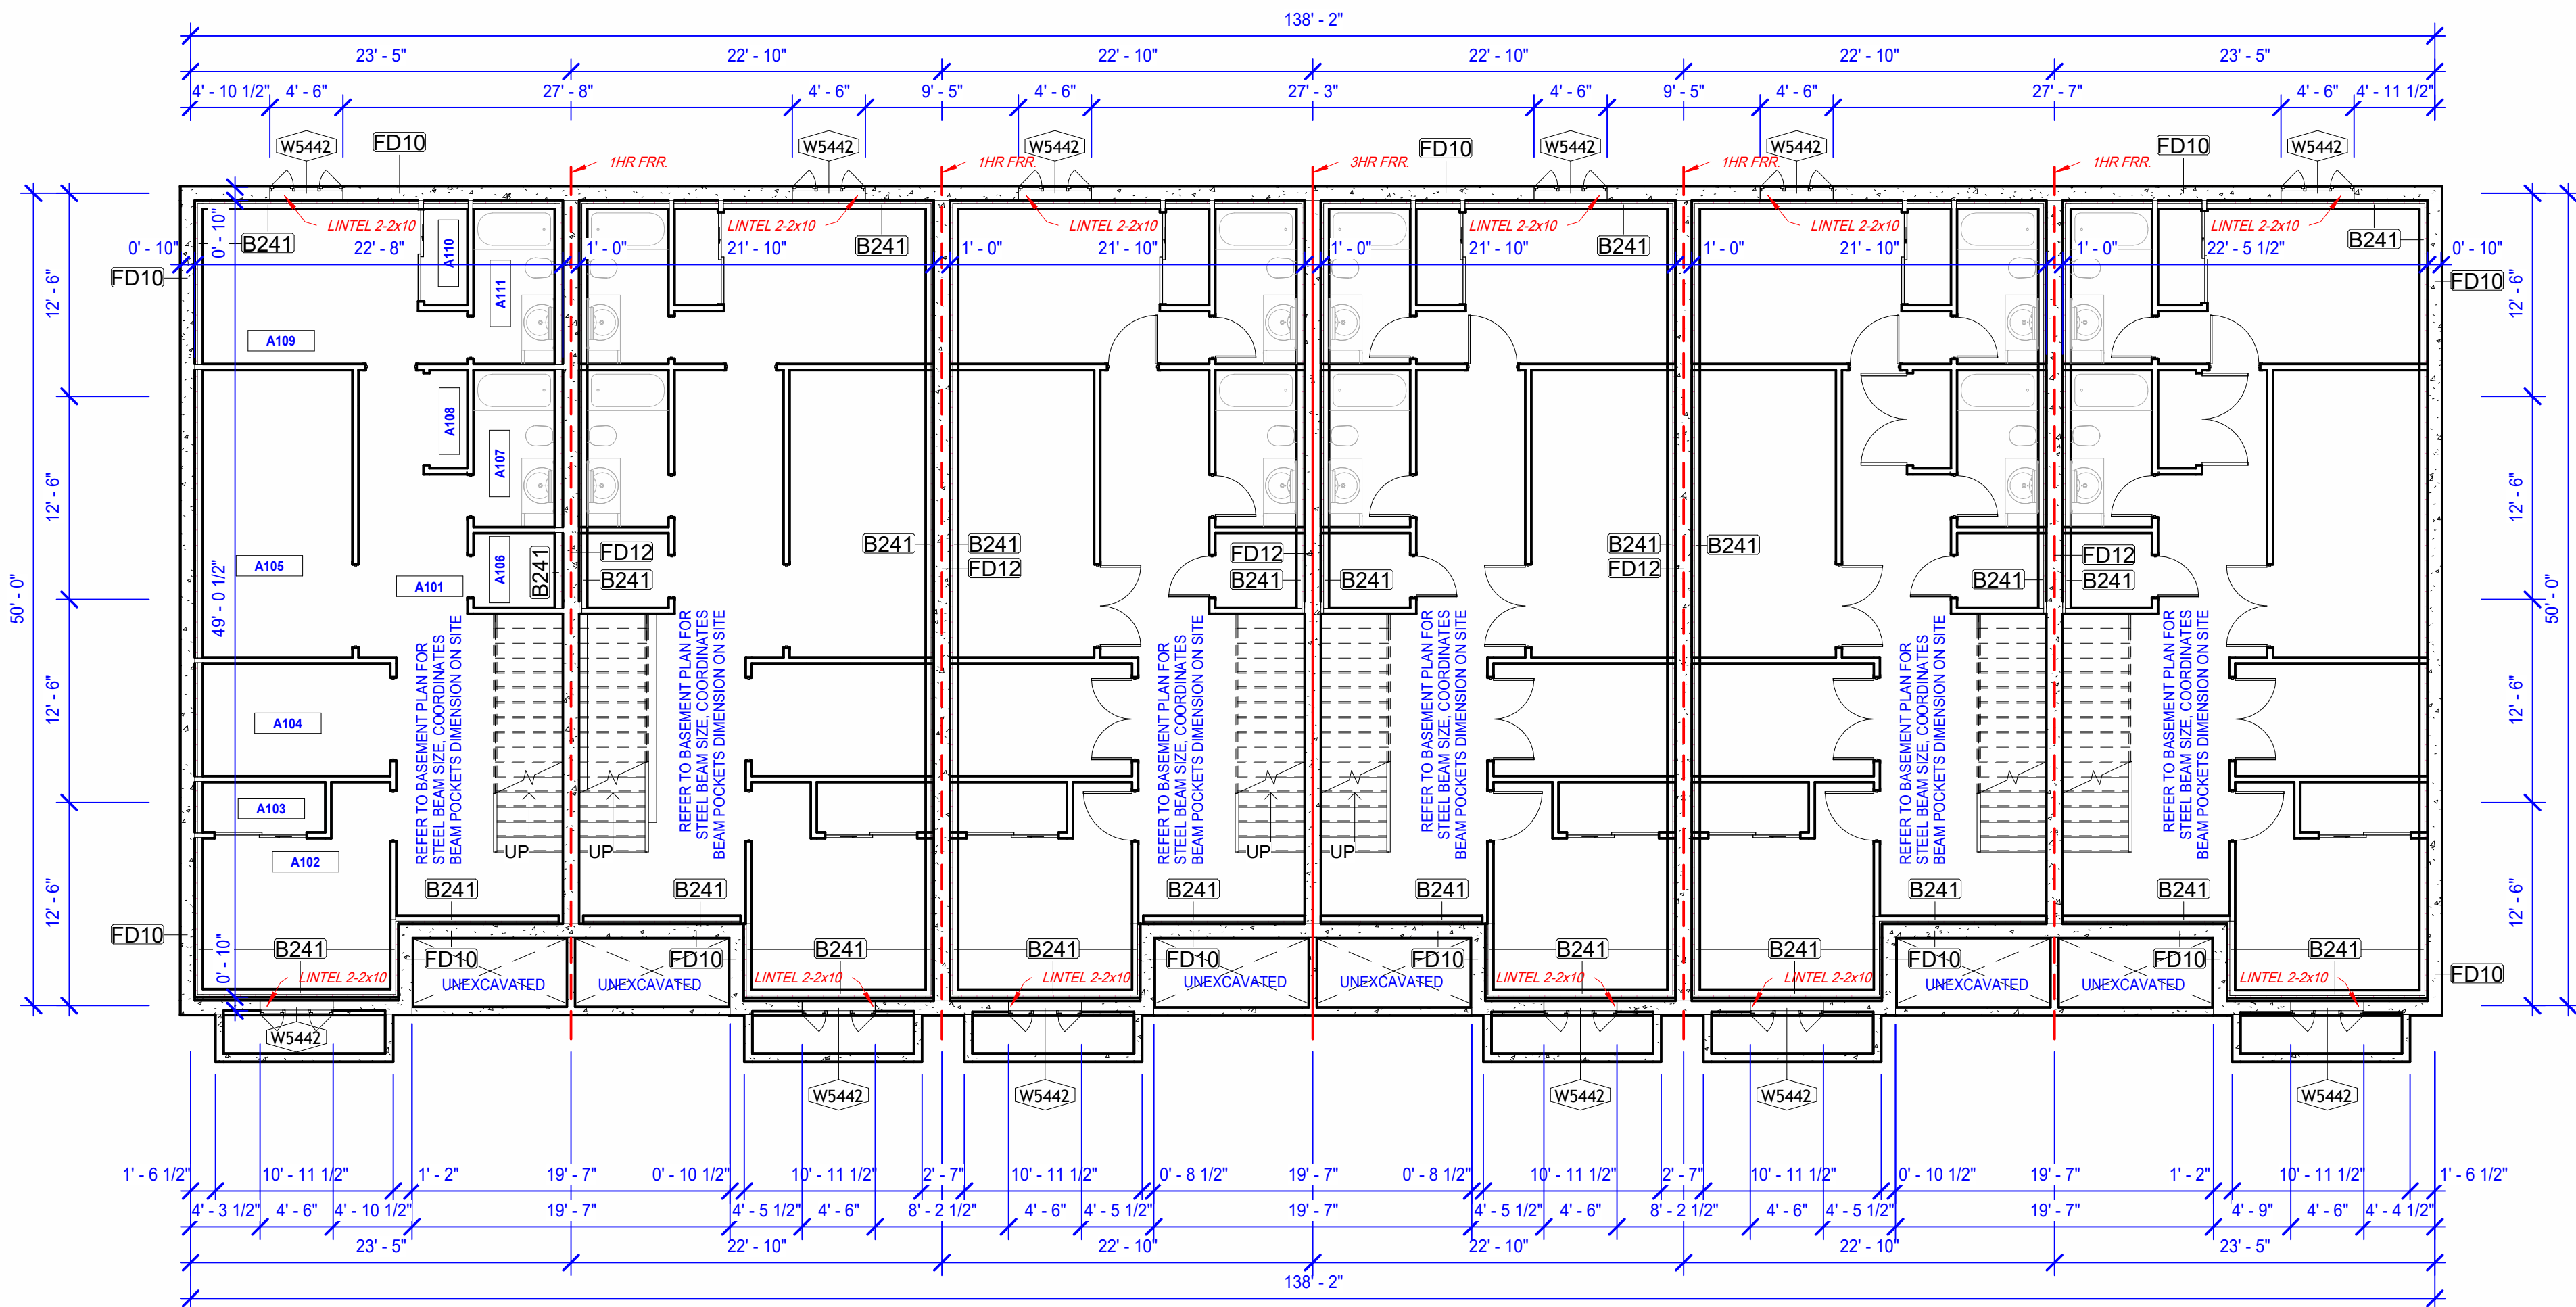


1 L100 - LOWER FLR.
1/8" = 1'-0"

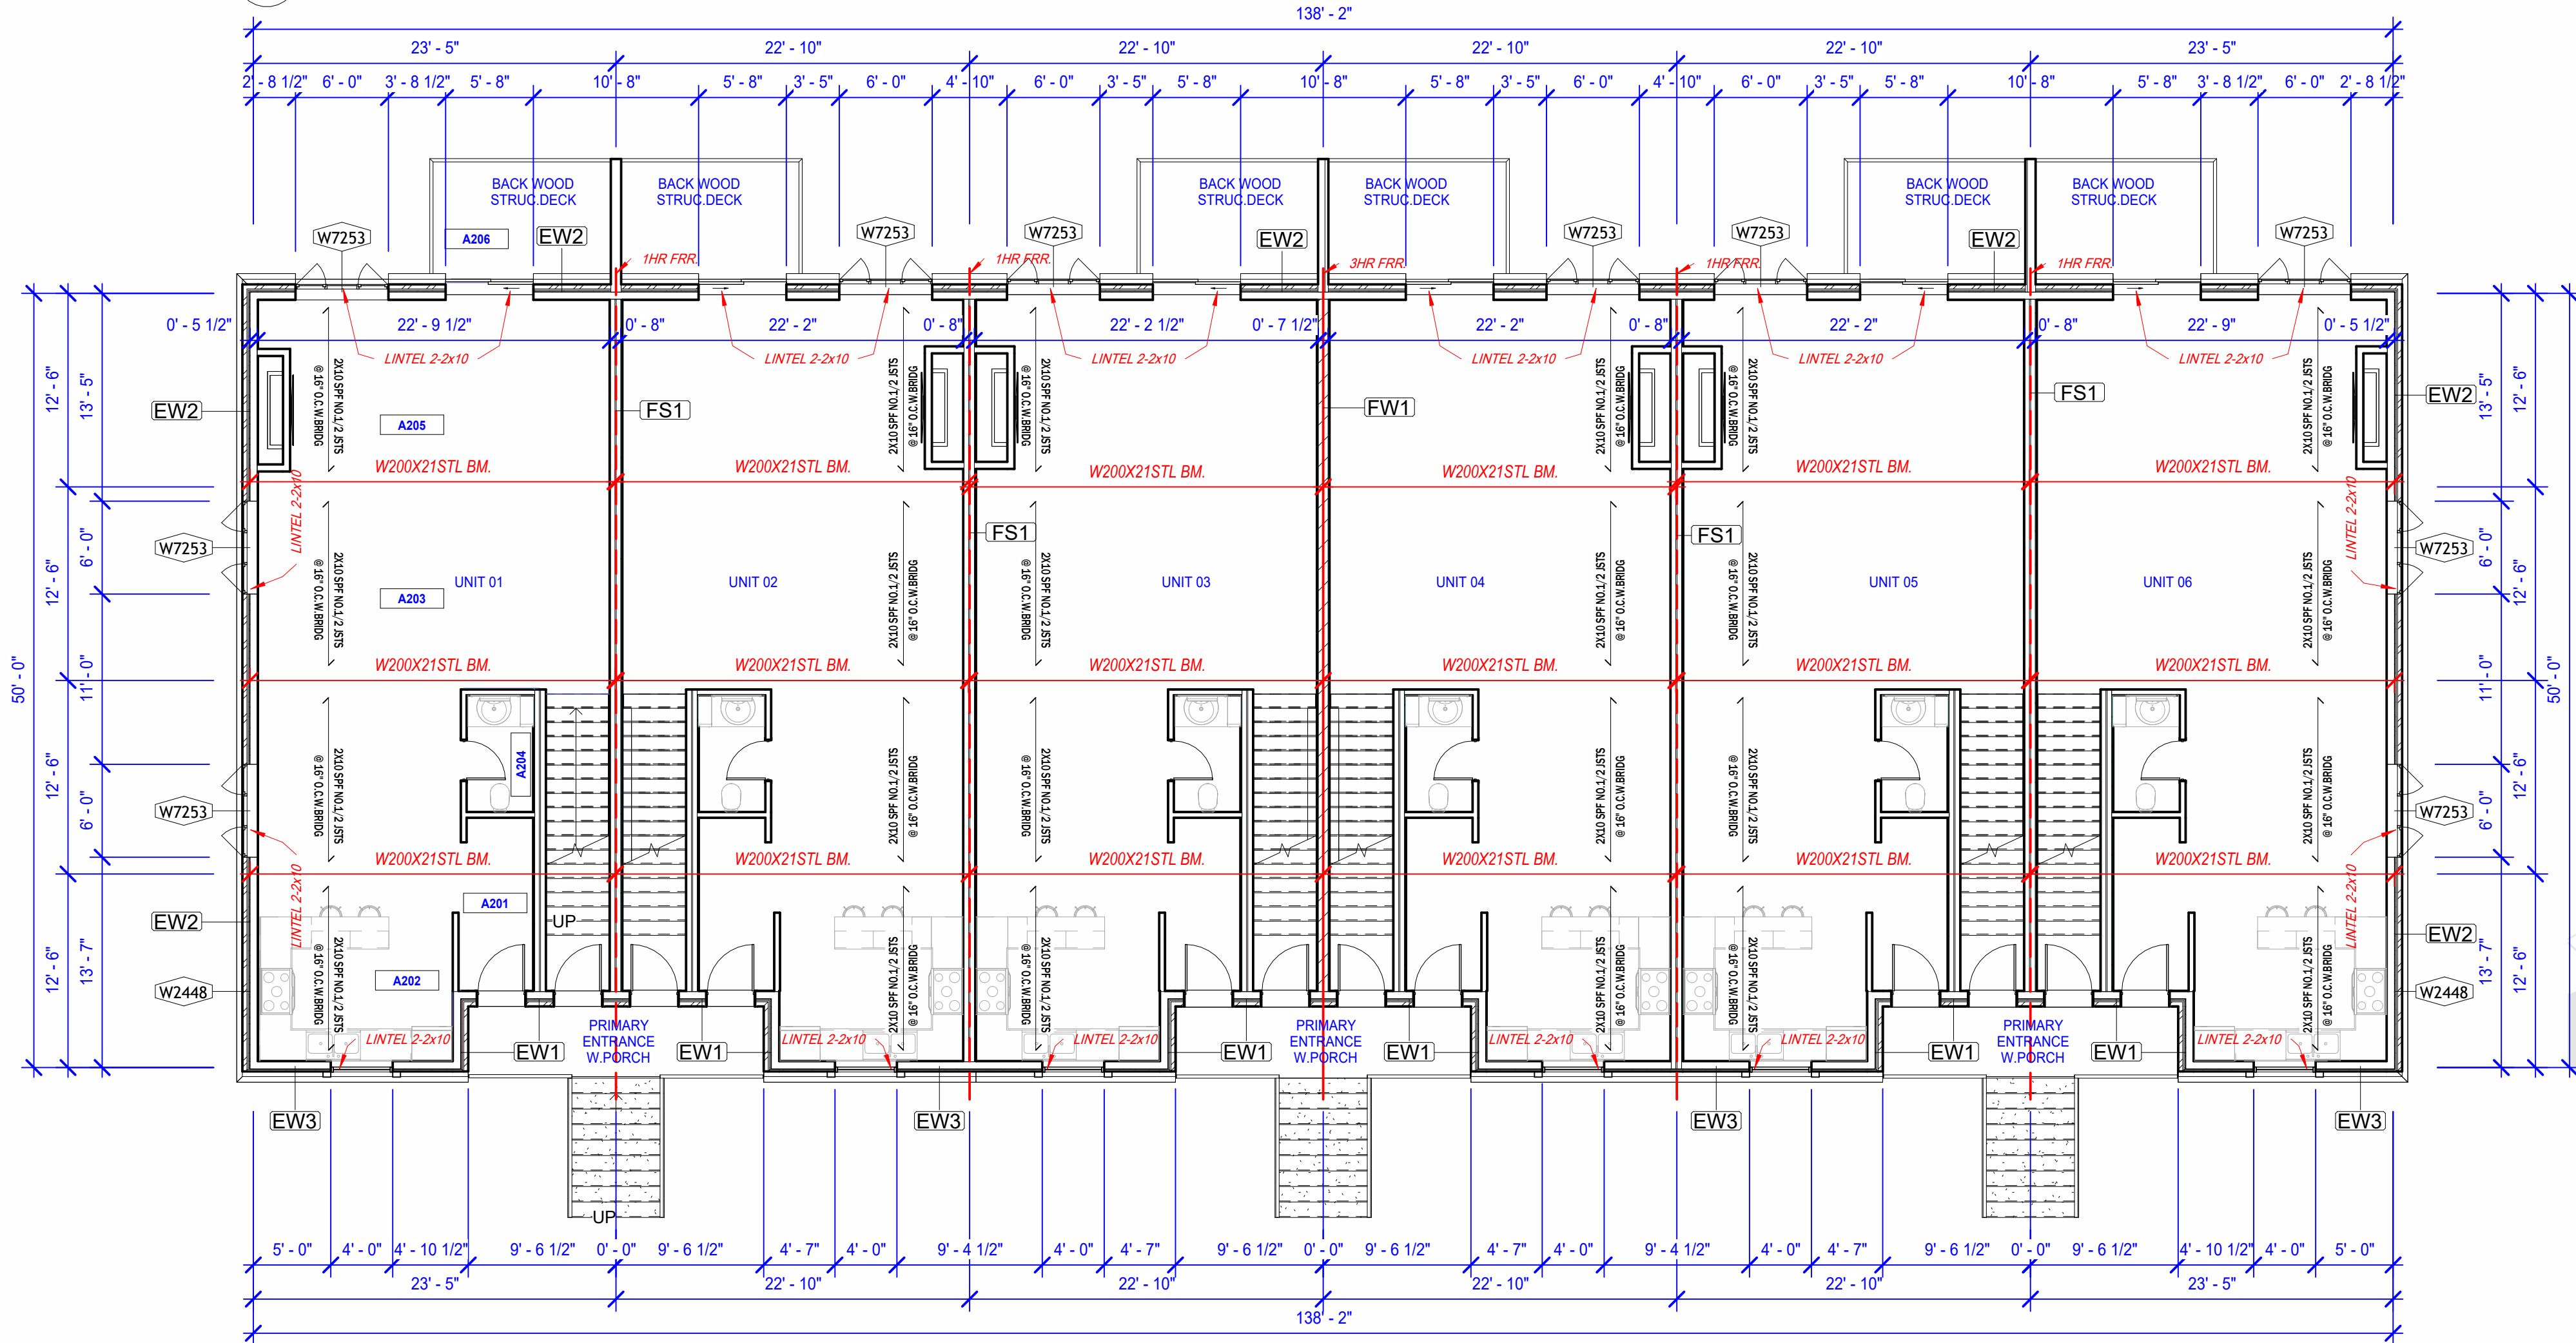


2 L200 - INTER. FLR.
1/8" = 1'-0"

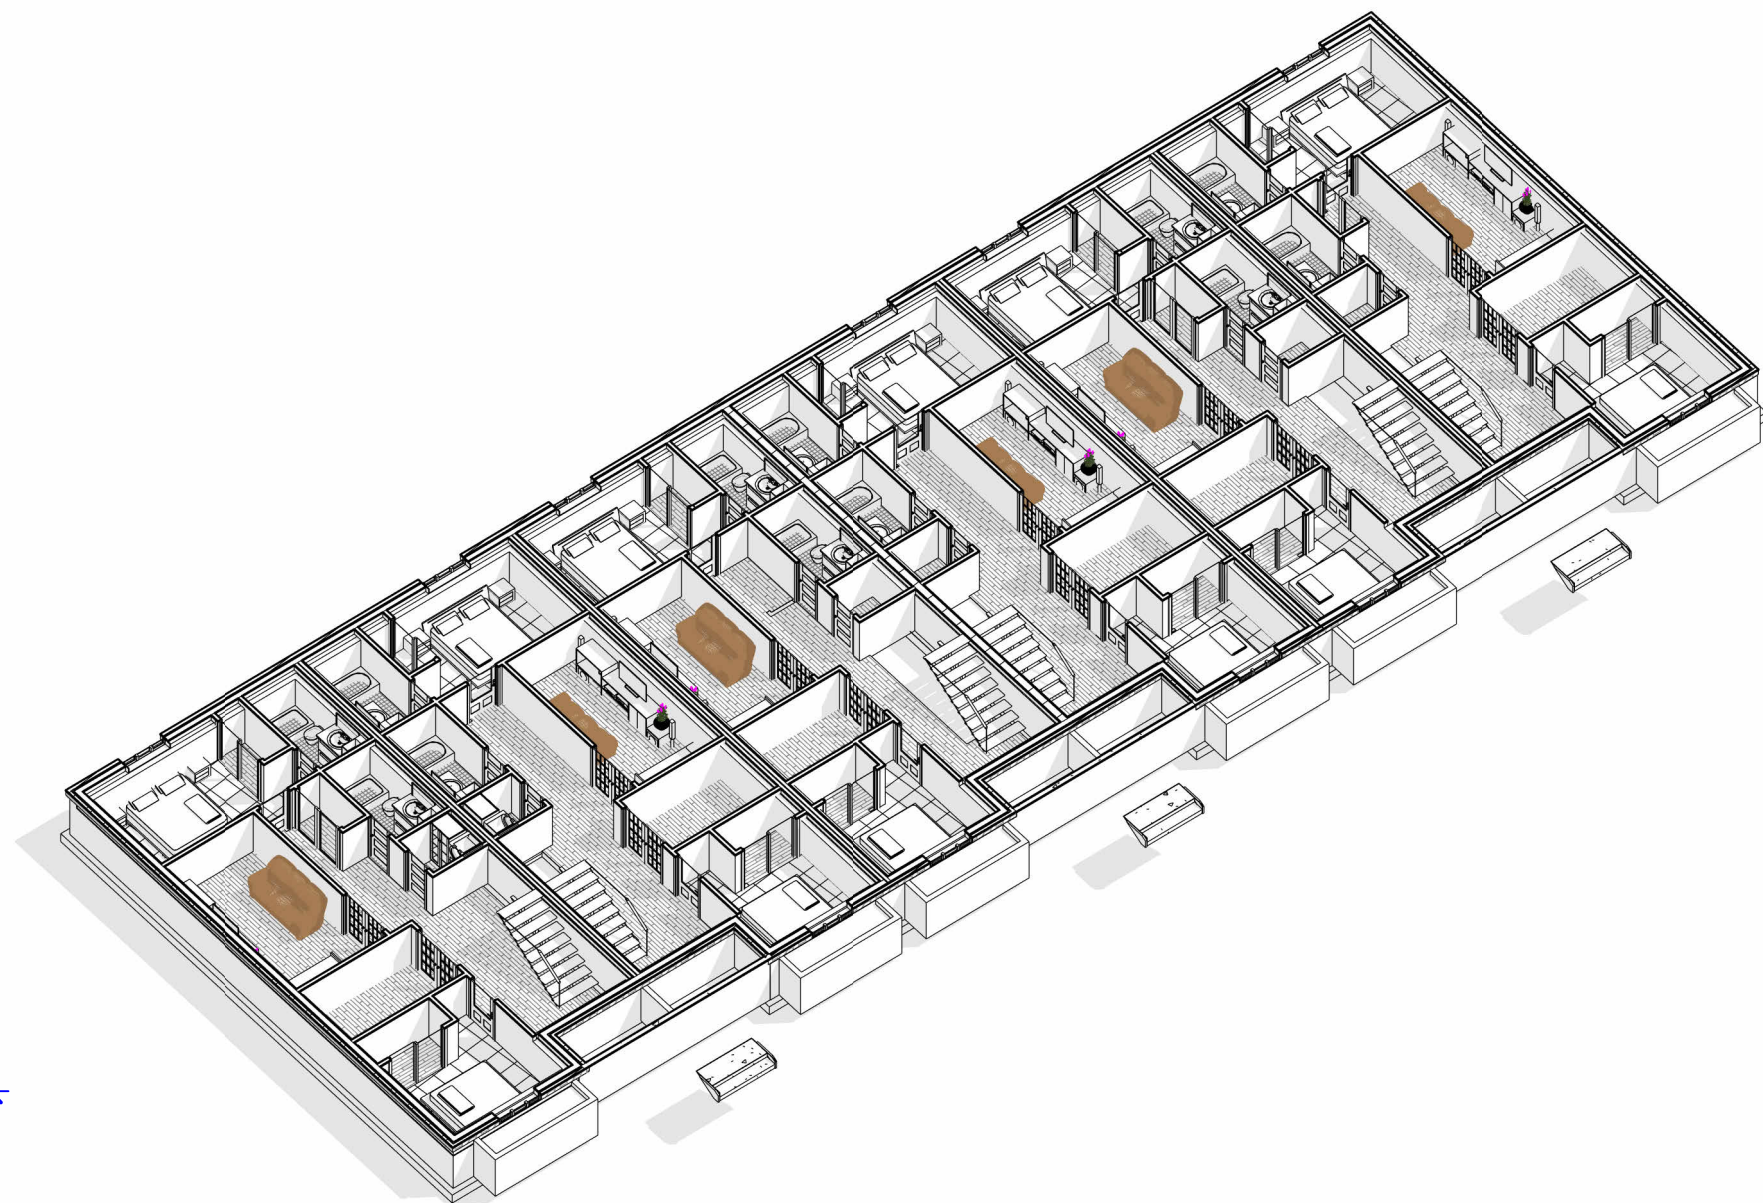

3 3D ISO L1

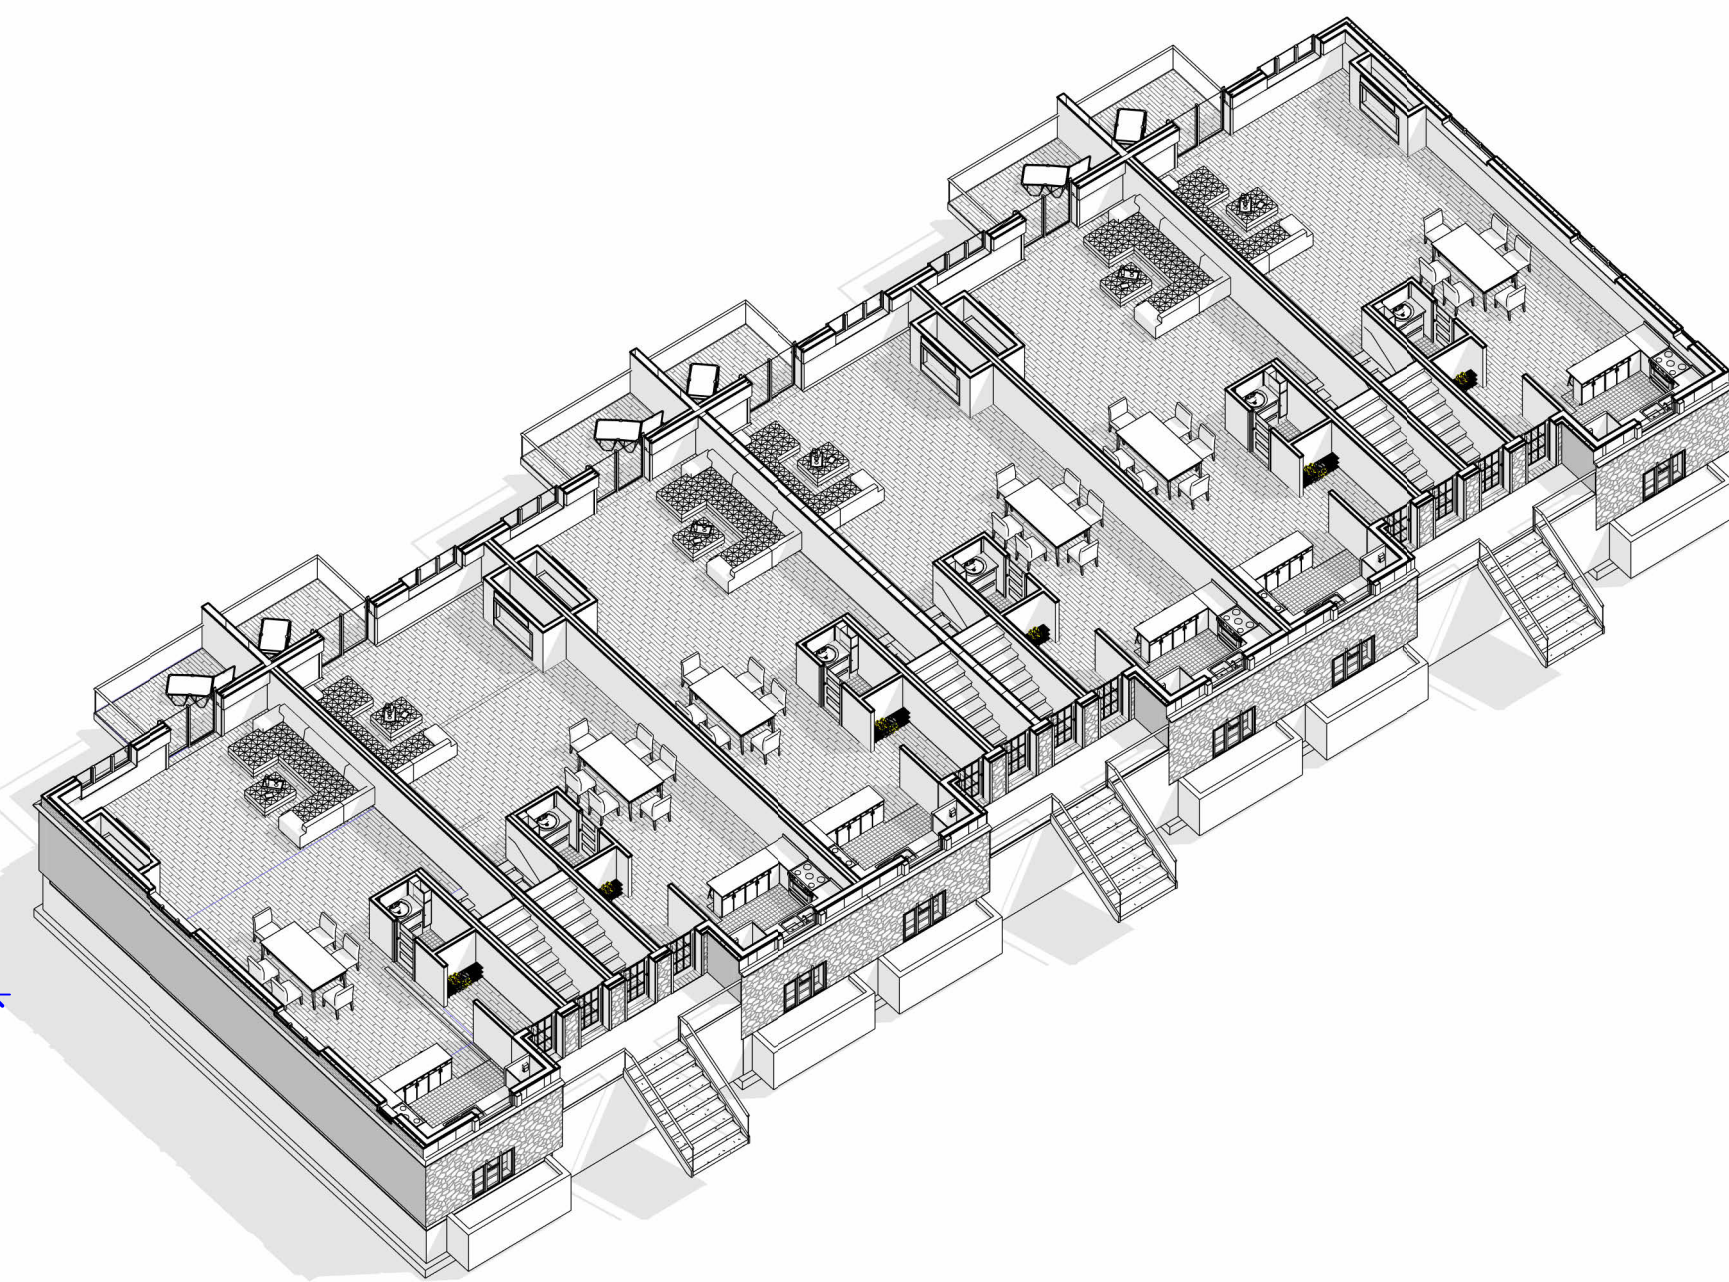

4 3D ISO L2

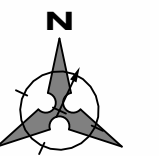

School of Building Technology
ARCHITECTURAL
TECHNOLOGY

PROJECT TITLE
RICKETY RIDGE - LUXURY
TOWNHOMES



CLIENT:
RICKETY DEVELOPMENT CORP.

PROJECT ADDRESS
539 PHILIP STREET
London ON.


DRAWING TITLE
FLOOR PLAN - BLOCK

CHECKED | DRAWN | DATE
GJG | AFNM | 04/15/25

00004 | A3.1 |
FILE | DRAWING | REVISION

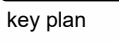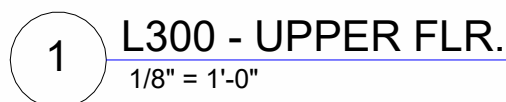

3 3D ISO L3

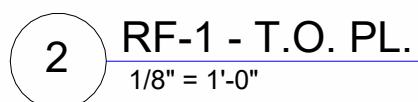

PROJECT TITLE

PROJECT ADDRESS
539 PHILIP STREET
London ON.

DRAWING TITLE
FLOOR PLAN - BLOCK




seal




DRAWING TITLE
FLOOR PLAN - UNITS

00004	A3.3	
FILE	DRAWING	REVISION

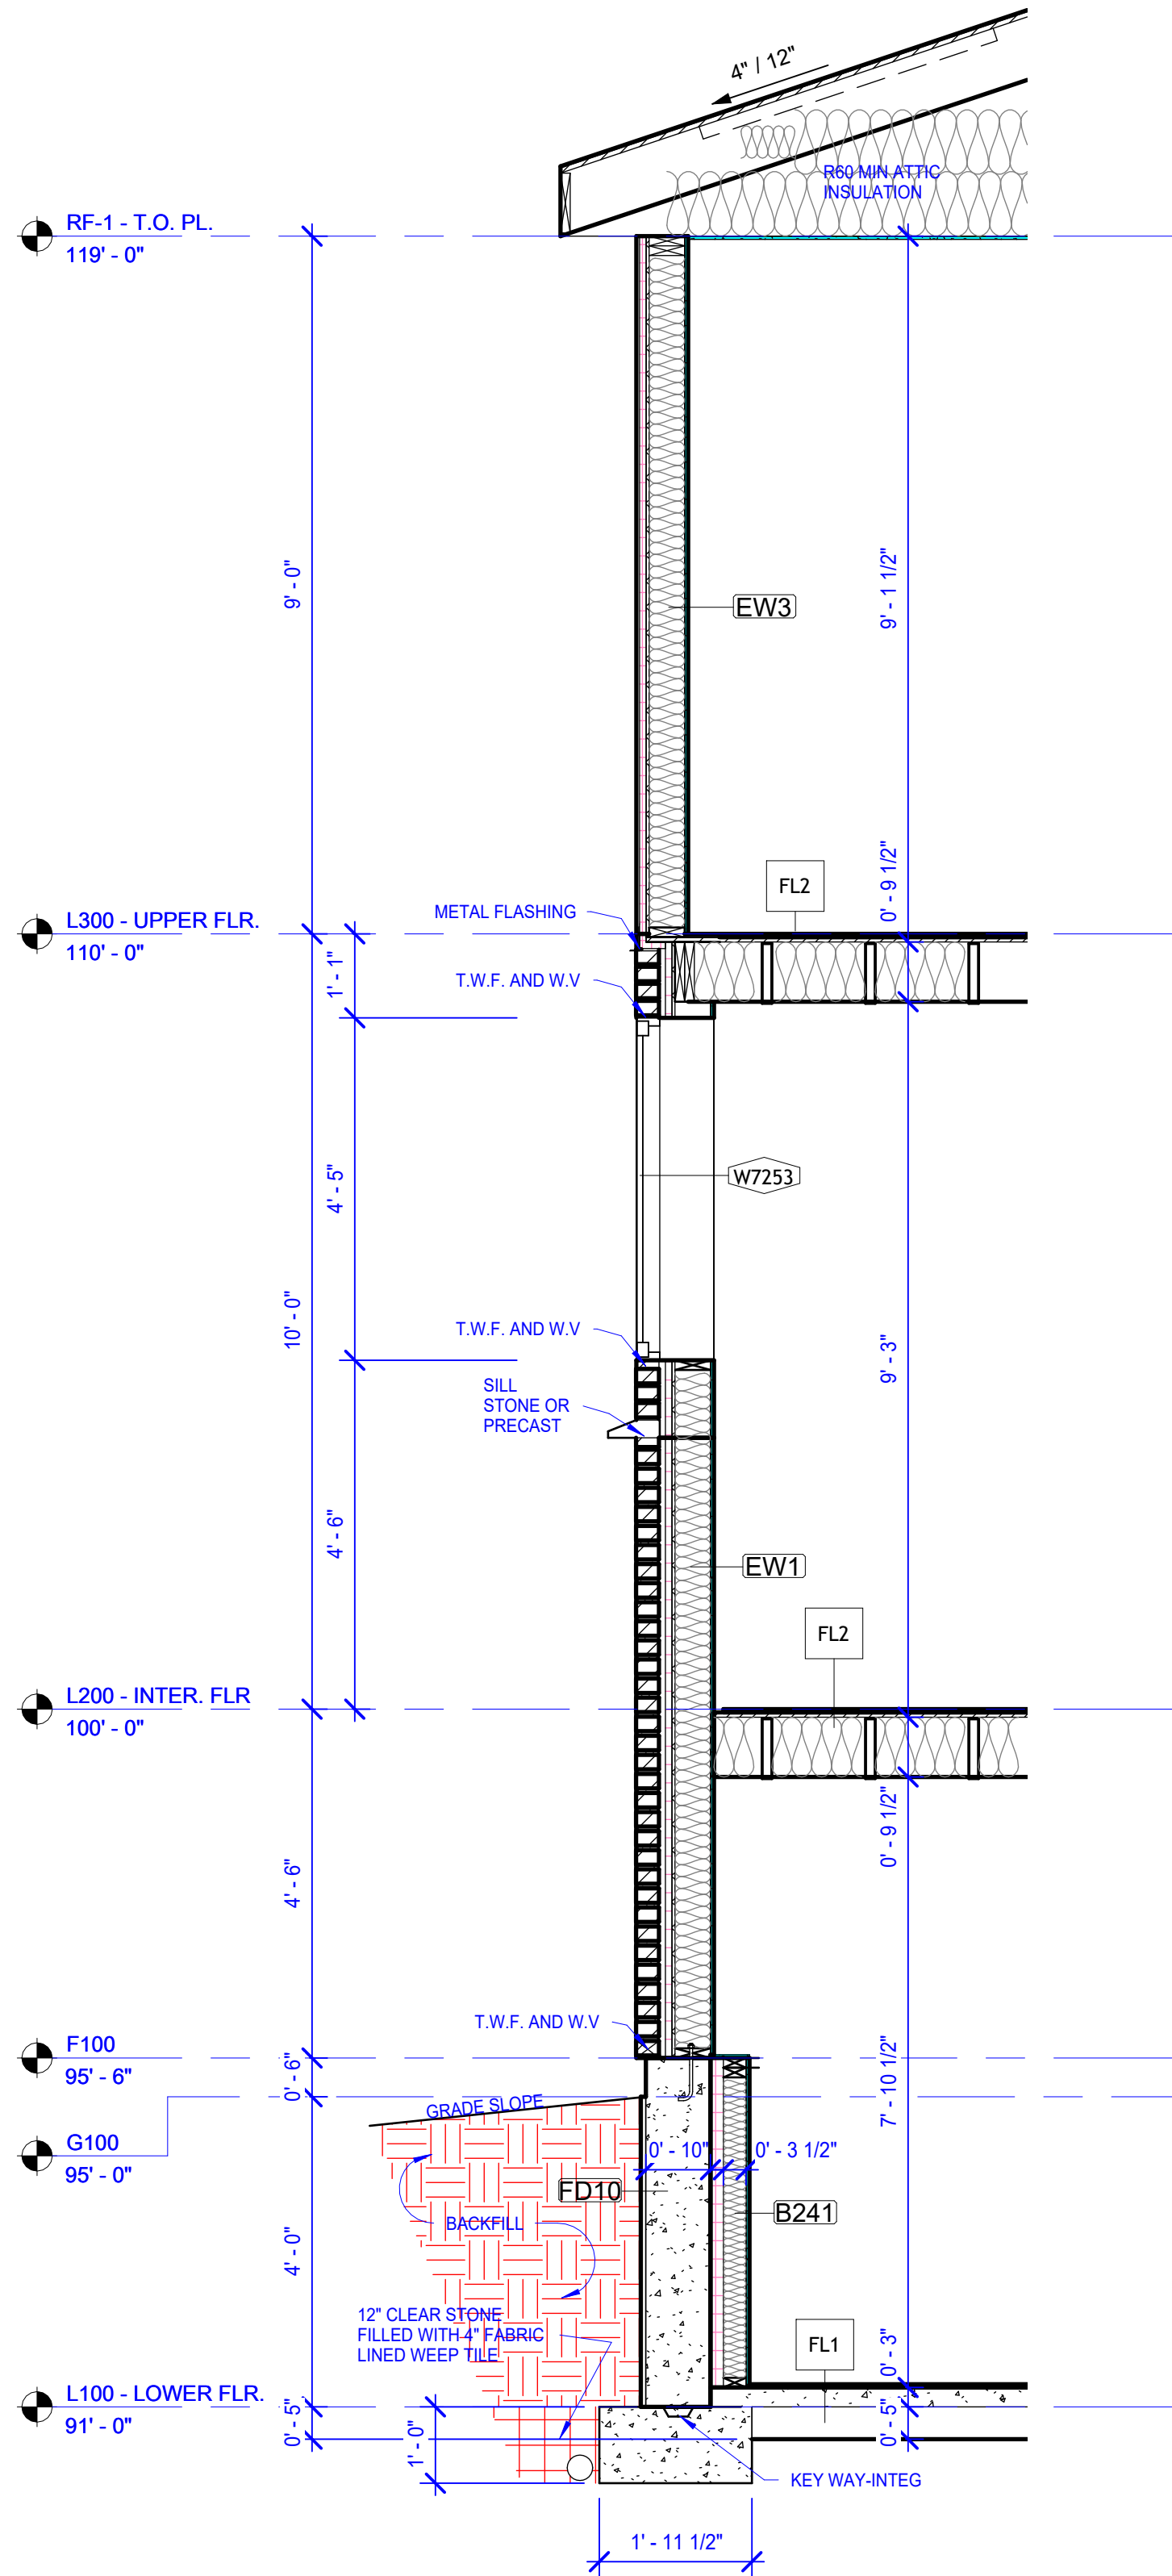

1 WALL SECTION 01
1/2" = 1'-0"

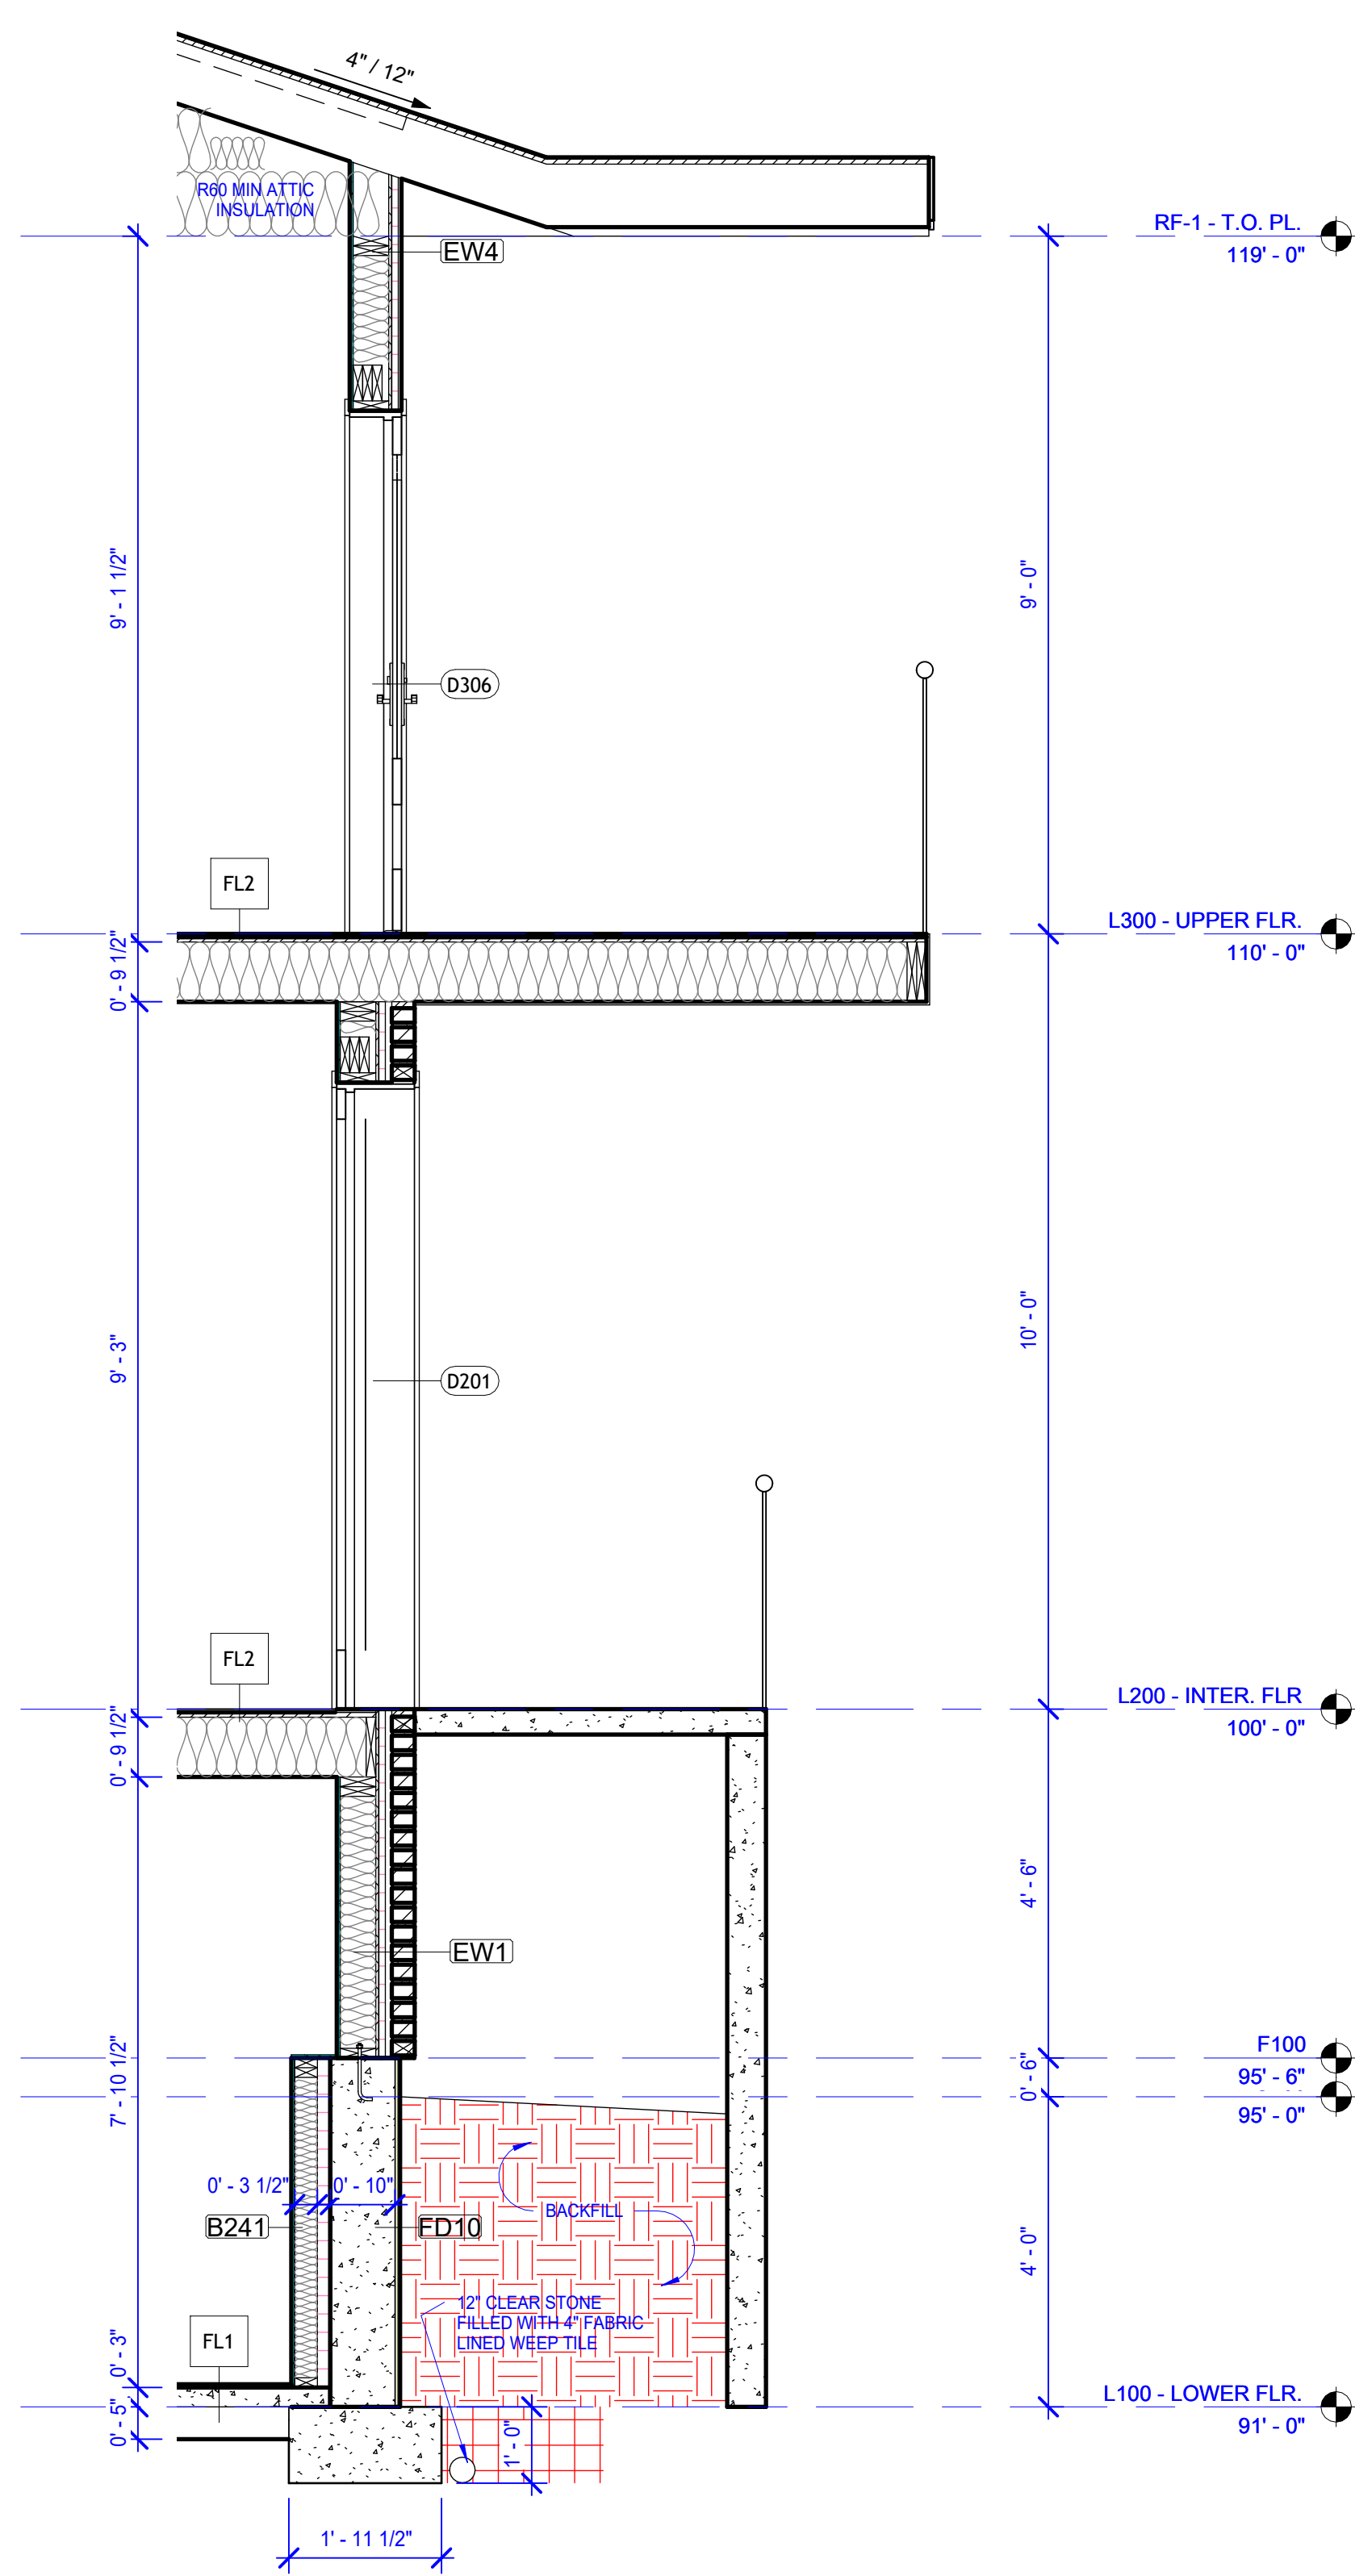


2 WALL SECTION 02
1/2" = 1'-0"

REVISIONS			
NO.	DATE	REVISION	BY

key plan

seal

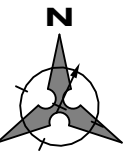

School of Building Technology
ARCHITECTURAL
TECHNOLOGY

PROJECT TITLE
RICKETY RIDGE - LUXURY
TOWNHOMES


CLIENT:
RICKETY DEVELOPMENT CORP.

PROJECT ADDRESS
539 PHILIP STREET
London ON.


DRAWING TITLE
SECTIONS

CHECKED	DRAWN	DATE
GJG	AFNM	04/15/25

00004	A4.1	
FILE	DRAWING	REVISION

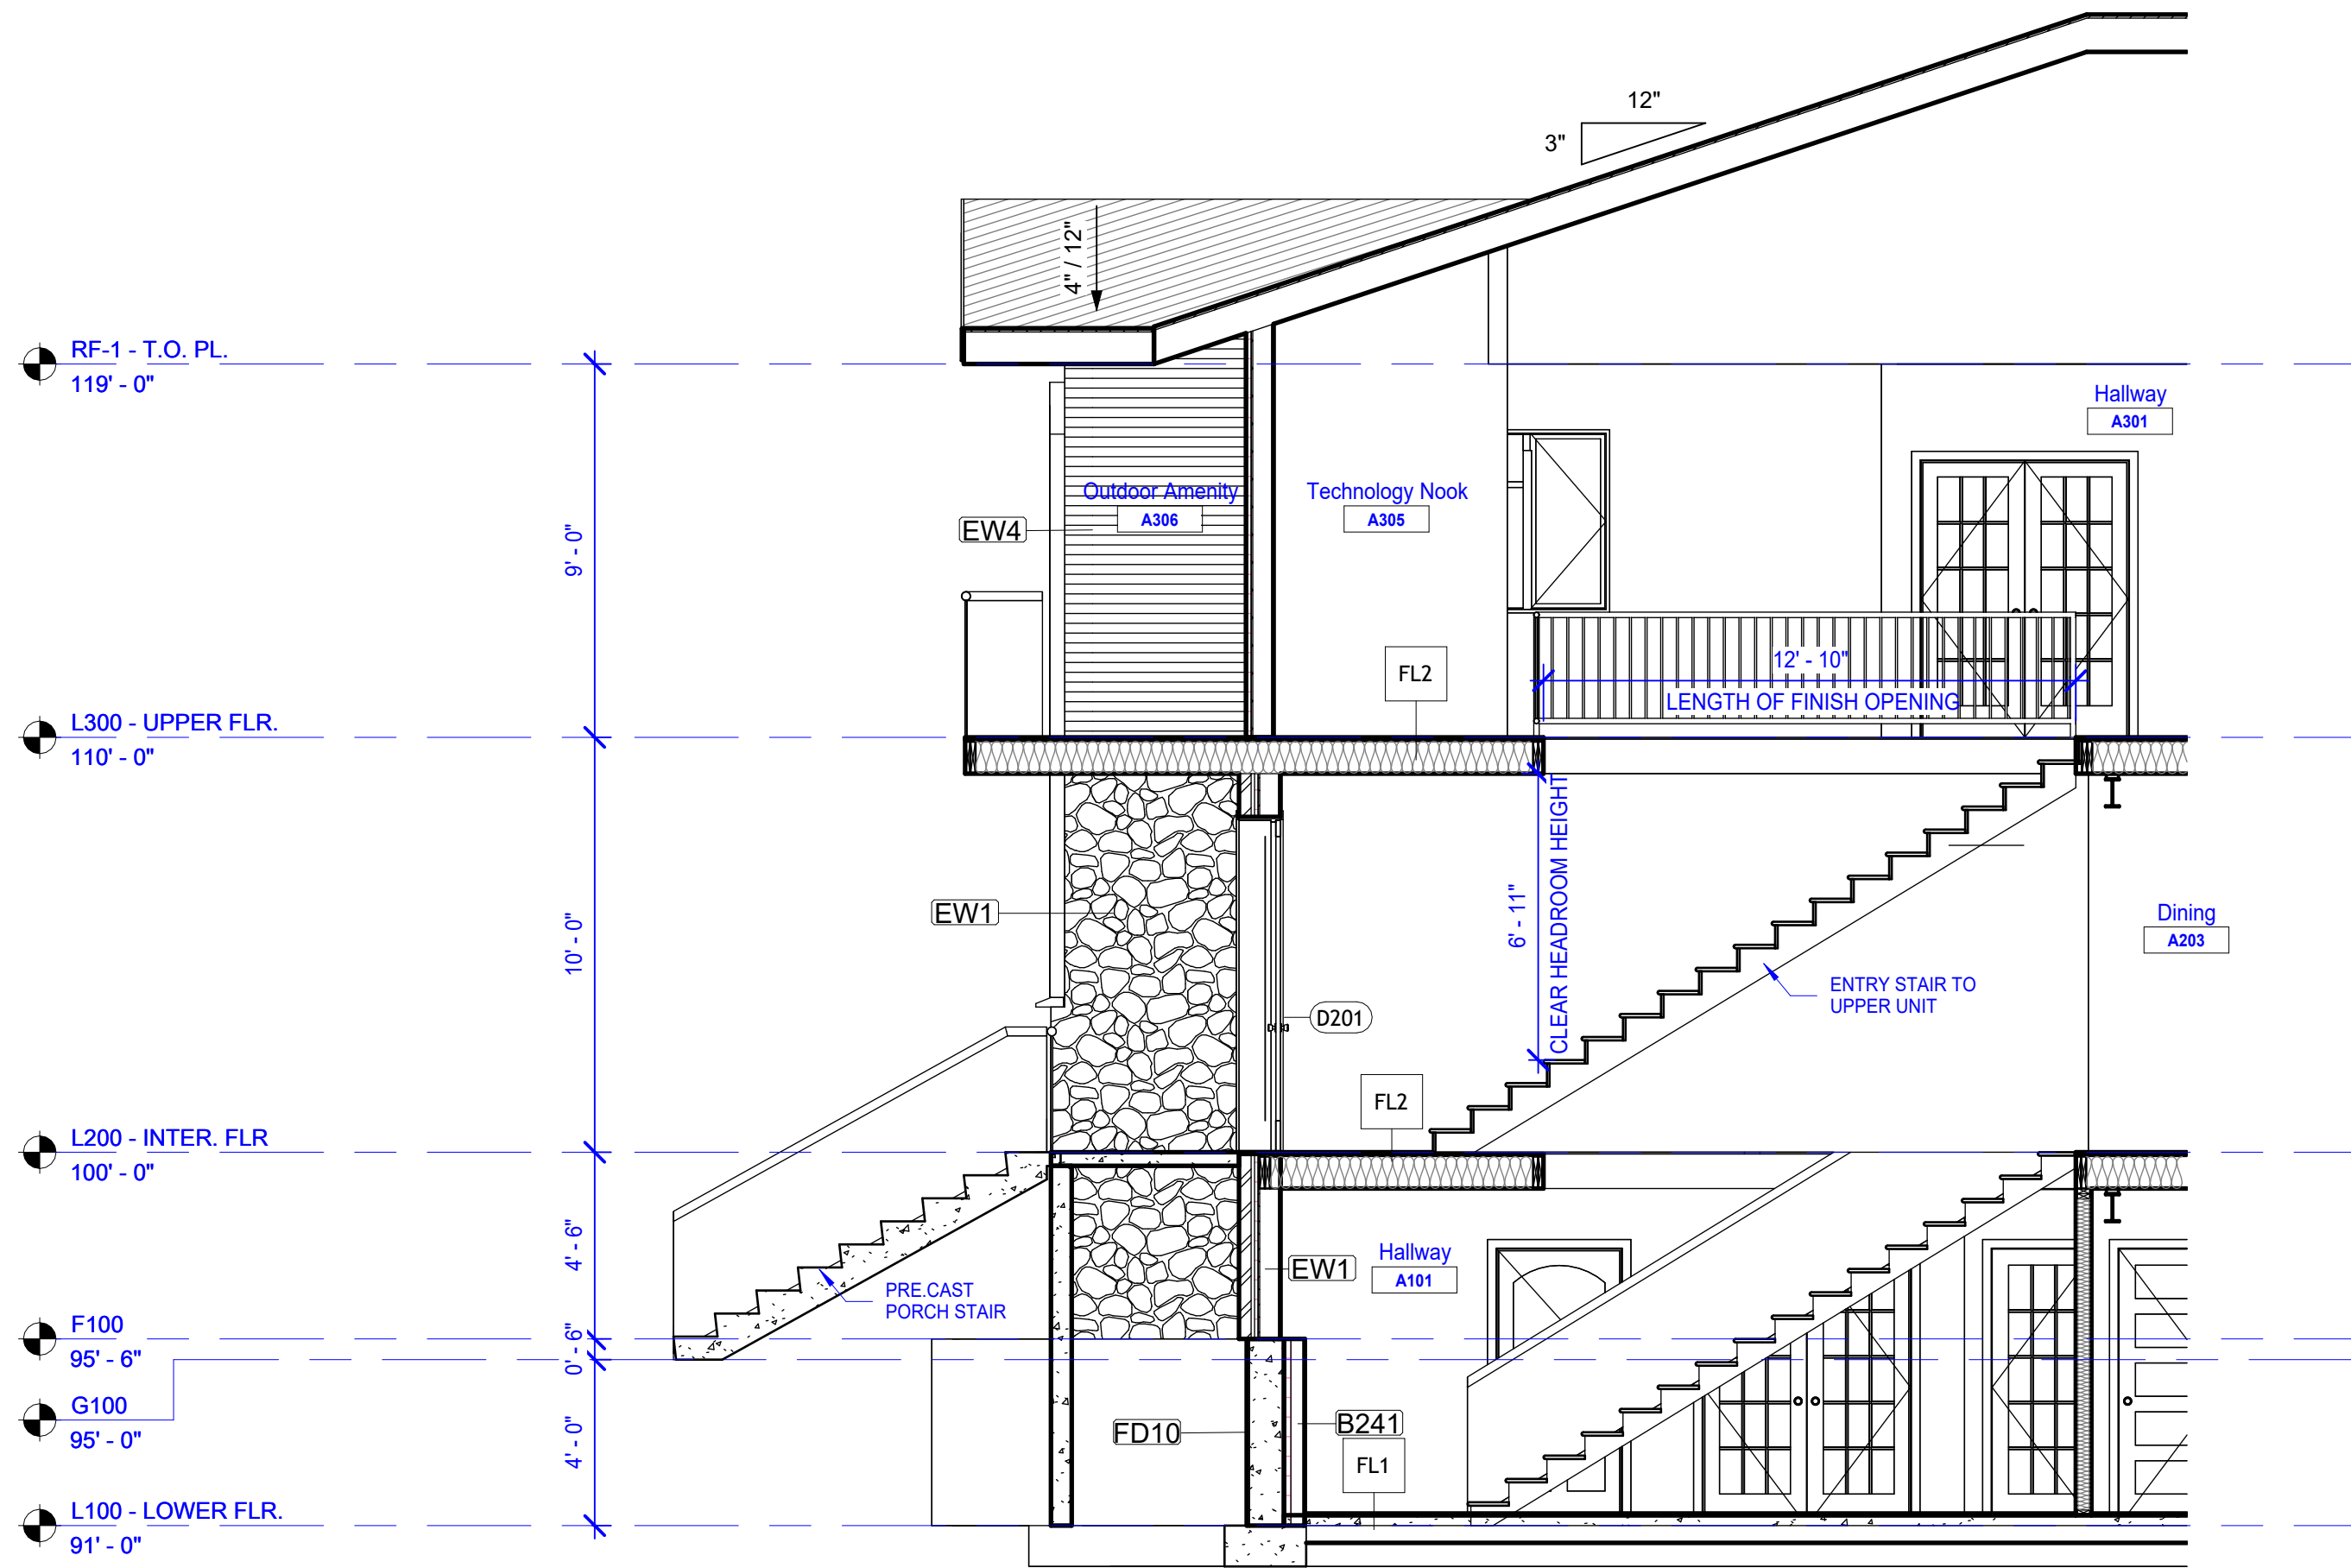



1 STAIR SECTION
1/4" = 1'-0"

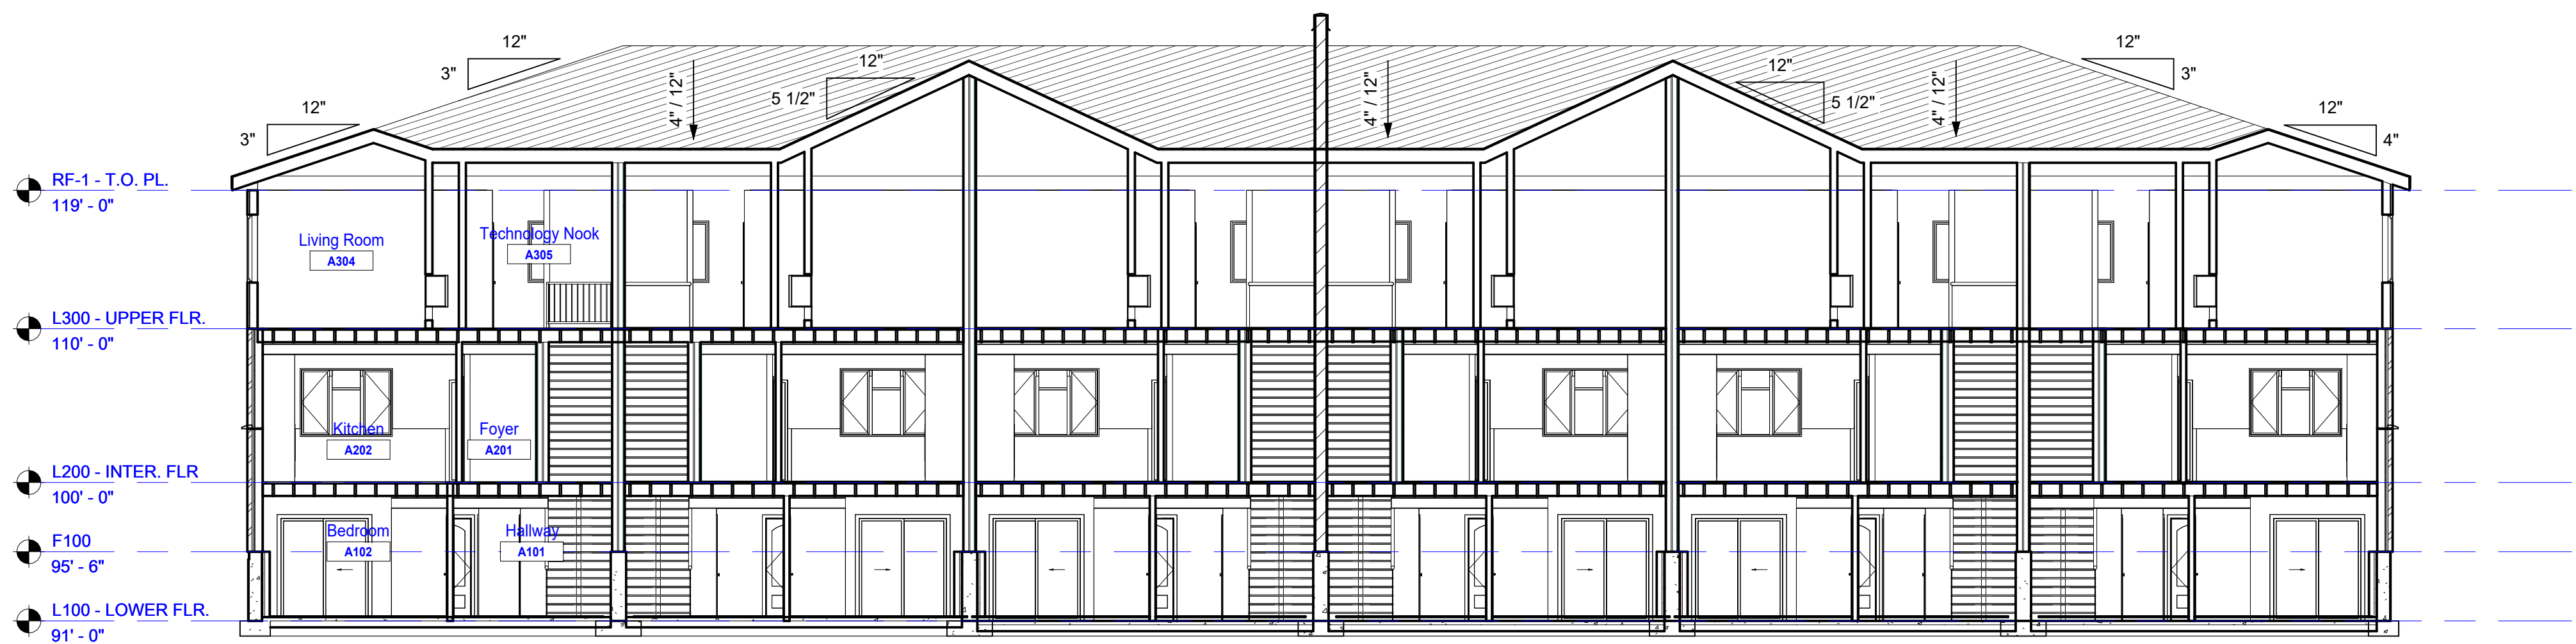

2 BUILDING SECTION
1/8" = 1'-0"

key plan

seal

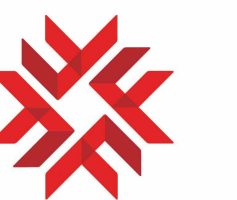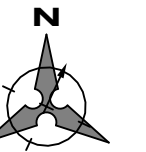

FANSHAWE

School of Building Technology
ARCHITECTURAL
TECHNOLOGY

PROJECT TITLE

RICKETY RIDGE - LUXURY
TOWNHOMES

CLIENT:

RICKETY DEVELOPMENT CORP.

PROJECT ADDRESS

539 PHILIP STREET
London ON.

DRAWING TITLE

SECTIONS


CHECKED	DRAWN	DATE
GJG	AFNM	04/15/25

00004	A4.2	
FILE	DRAWING	REVISION

REVISIONS		
NO.	DATE	REVISION

key plan

seal

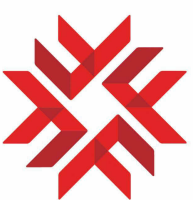

FANSHAWE

School of Building Technology
ARCHITECTURAL
TECHNOLOGY


PROJECT TITLE
**RICKETY RIDGE - LUXURY
TOWNHOMES**

CLIENT:
RICKETY DEVELOPMENT CORP.


PROJECT ADDRESS
539 PHILIP STREET
London ON.

DRAWING TITLE
DETAILS


CHECKED GJG	DRAWN AFNM	DATE 04/15/25
00004	A5.1	
FILE	DRAWING	REVISION

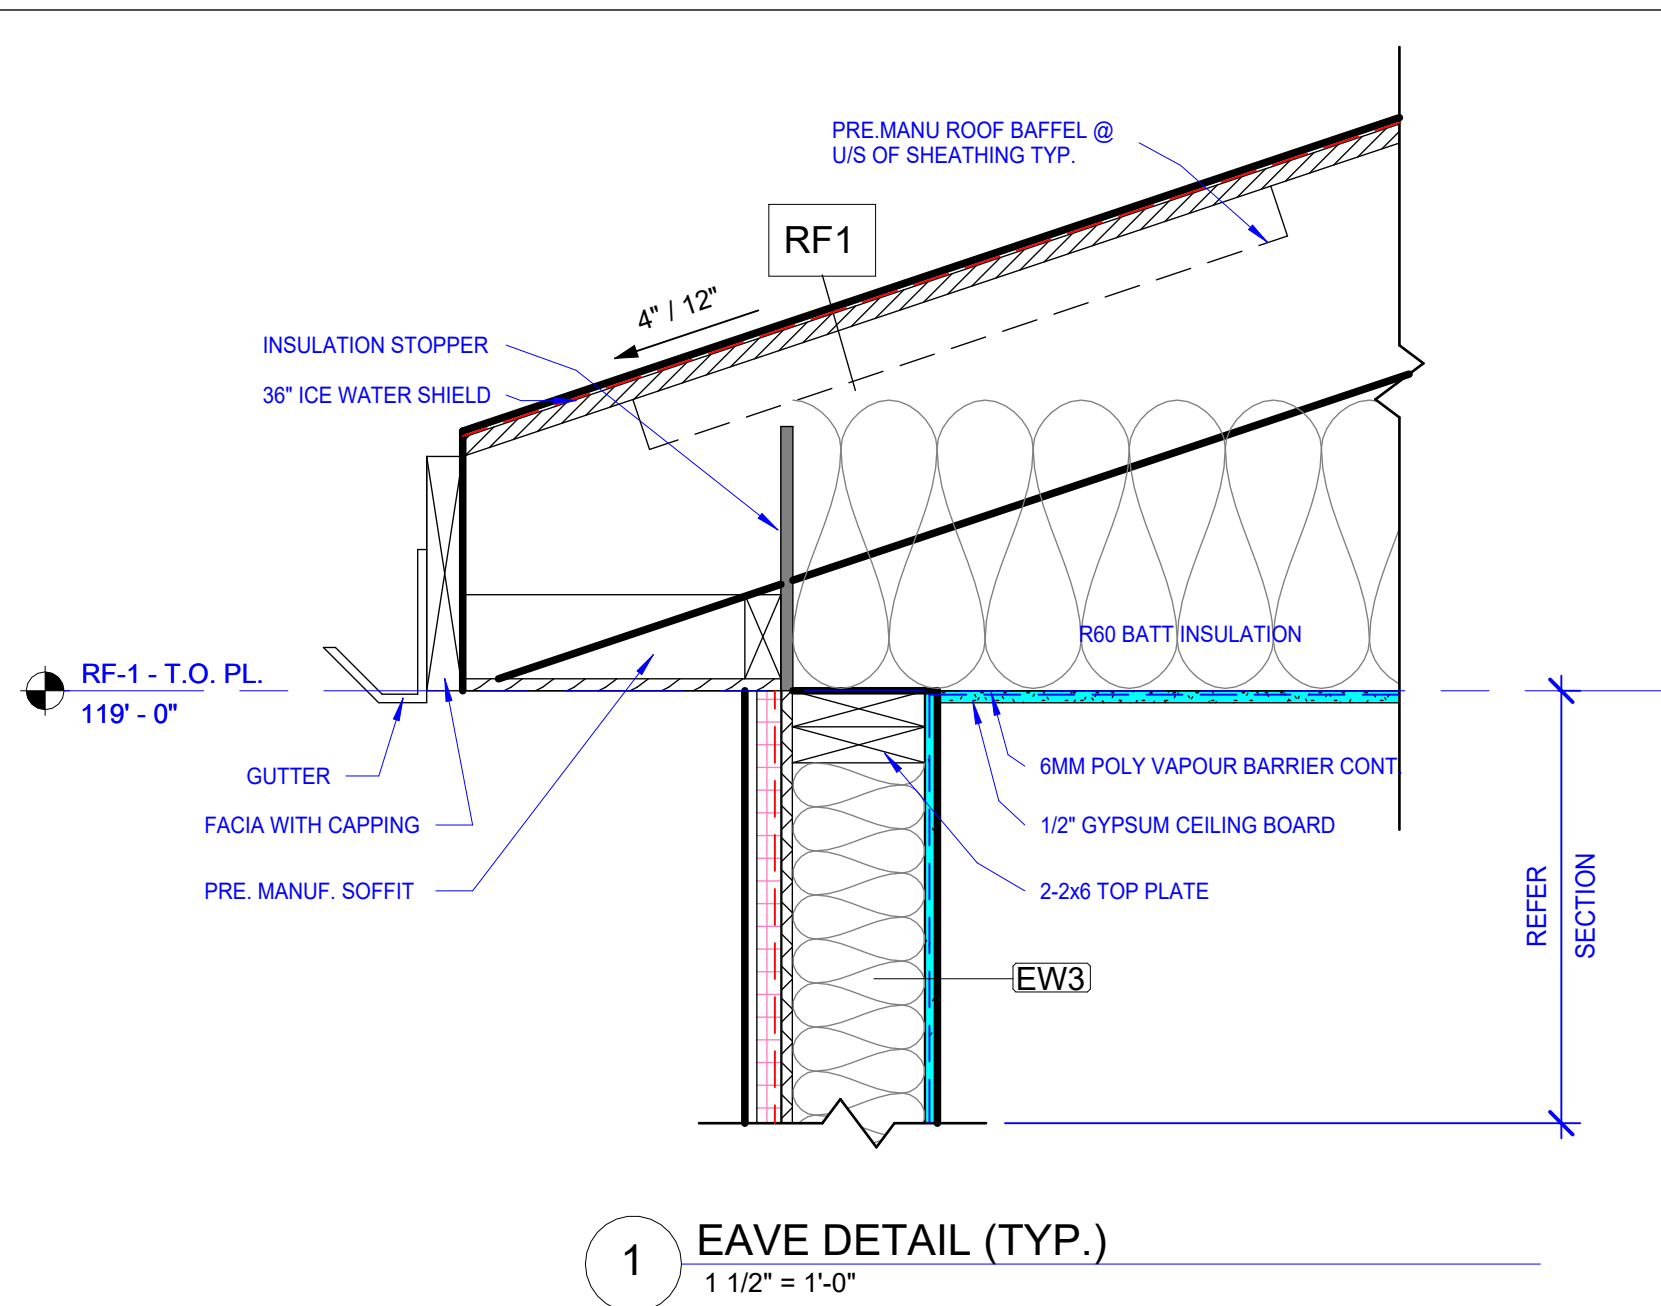


1 EAVE DETAIL (TYP.)
1 1/2" = 1'-0"

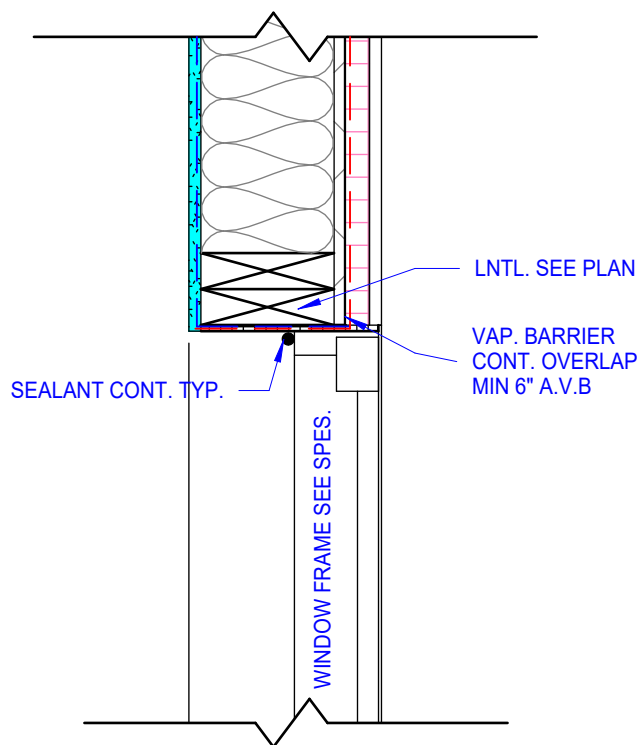


4 HEAD DETAIL
1 1/2" = 1'-0"

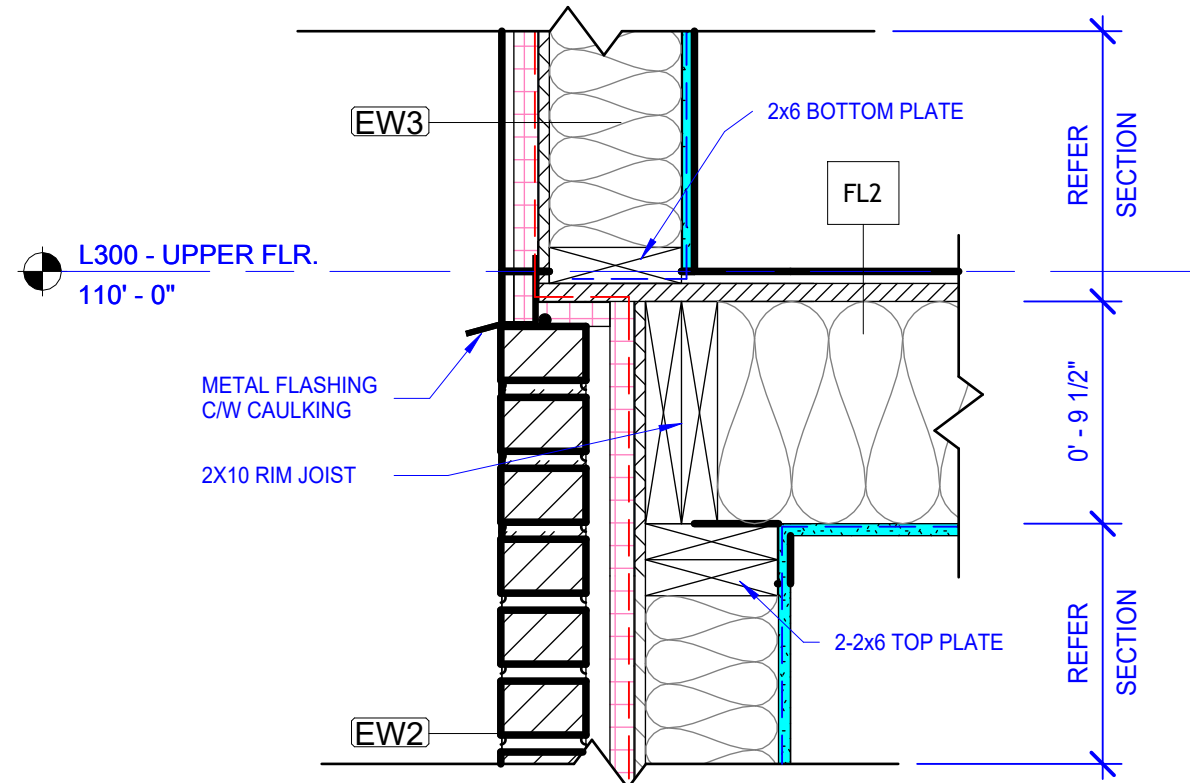


2 FLOOR INTERSECTION DETAIL (TYP.)
1 1/2" = 1'-0"

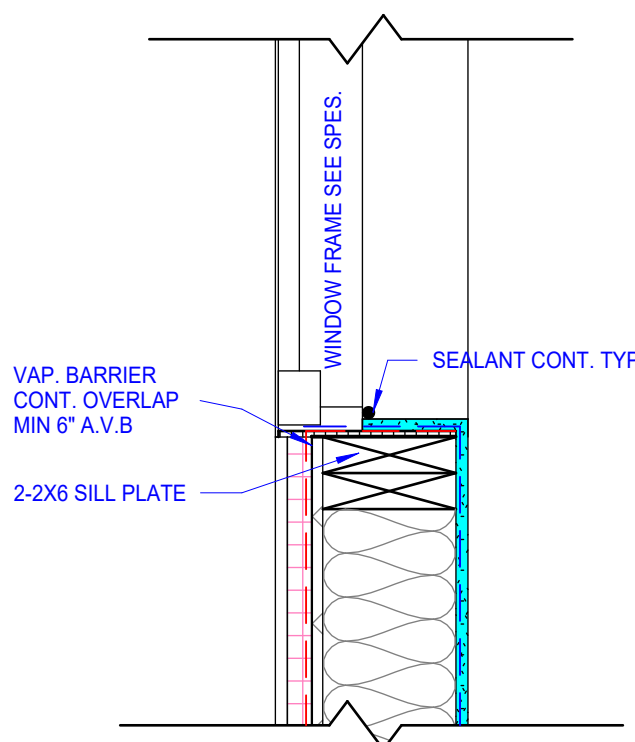

5 SILL DETAIL
1 1/2" = 1'-0"

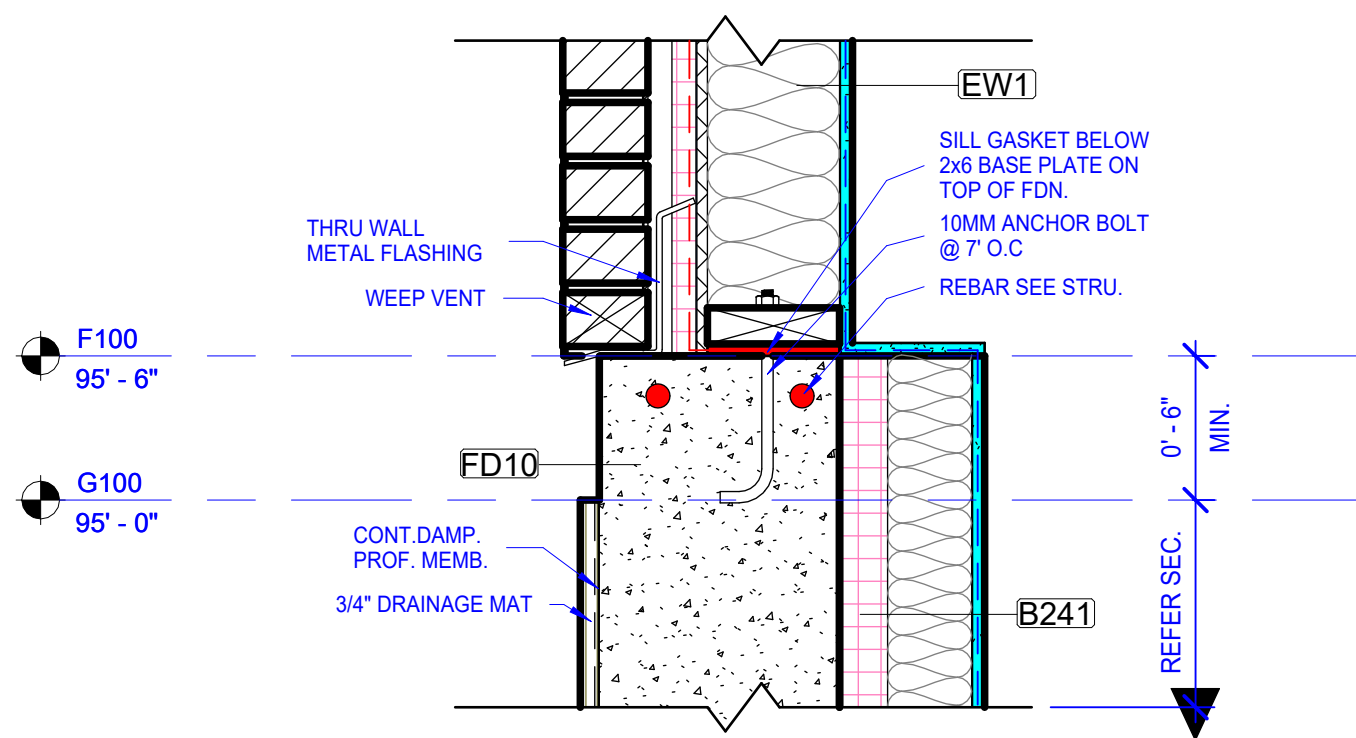

3 FDN. INTERSECTION DETAIL (TYP.)
1 1/2" = 1'-0"

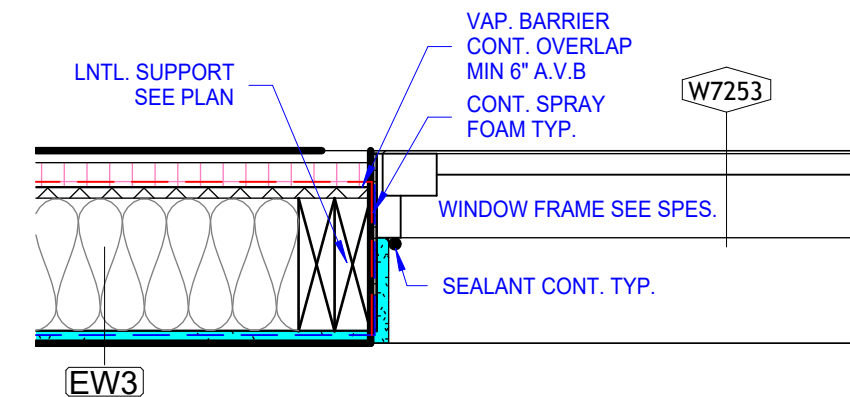

6 JAMB DETAIL
1 1/2" = 1'-0"