



Sheet List			
Sheet Number	Sheet Name	Drawn By	Checked By
A0.0	COVER PAGE	AFNM	GG
A0.1	ABBREVIATIONS & OBC MATRIX	AFNM	GG
A0.2	ASSEMBLIES SCHEDULE	AFNM	GG
A0.3	ASSEMBLIES SCHEDULE	AFNM	GG
A2.0	FOUNDATION PLAN	AFNM	GG
A2.1	LEVEL 0 - EXISTING BLD. PLAN	AFNM	GG
A2.2	LEVEL 1 - NEW BLD. PLAN	AFNM	GG
A2.3	LEVEL 2 - EXISTING BLD. PLAN	AFNM	GG
A2.4	LEVEL 3 - NEW & EXISTING BLD. PLAN	AFNM	GG
A2.5	LEVEL 4 - NEW & EXISTING BLD. PLAN	AFNM	GG
A2.6	LEVEL 5 - NEW & EXISTING BLD. PLAN	AFNM	GG
A3.1	NORTH AND SOUTH ELEVATION	AFNM	GG
A3.2	EAST AND WEST ELEVATION	AFNM	GG
A4.1	WALL SECTIONS	AFNM	GG
A5.1	PLAN DETAILS	AFNM	GG
A5.2	SECTION DETAILS	AFNM	GG
A6.1	STAIR PLANS & SECTION	AFNM	GG
A6.2	ELEVATOR PLANS & SECTIONS	AFNM	GG
A7.1	ENLARGED LEVEL 1 FLOOR & CEILING PLAN	AFNM	GG
A8.1	ROOF PLANS	AFNM	GG

NORTH ARROW



GENERAL NOTES

1. DO NOT SCALE DRAWINGS. WRITTEN DIMENSIONS SHALL HAVE PRECEDENCE OVER SCALED DIMENSIONS.
2. ALL WORK SHALL COMPLY WITH THE 2012 ONTARIO BUILDING CODE AND AMENDMENTS.
3. CONTRACTORS MUST CHECK AND VERIFY ALL DIMENSIONS AND SPECIFICATIONS AND REPORT ANY DISCREPANCIES TO THE ARCHITECT BEFORE PROCEEDING WITH THE WORK.
4. ALL CONTRACTORS AND SUB-CONTRACTORS SHALL HAVE A SET OF APPROVED CONSTRUCTION DOCUMENTS ON SITE AT ALL TIMES.
5. ALL DOCUMENTS REMAIN THE PROPERTY OF THE ARCHITECT. UNAUTHORIZED USE, MODIFICATION, AND/OR REPRODUCTION OF THESE DOCUMENTS IS PROHIBITED WITHOUT WRITTEN PERMISSION. THE CONTRACT DOCUMENTS WERE PREPARED BY THE CONSULTANT FOR THE ACCOUNT OF THE OWNER.
6. THE MATERIAL CONTAINED HEREIN REFLECTS THE CONSULTANT'S BEST JUDGMENT IN LIGHT OF THE INFORMATION AVAILABLE TO HIM/HER AT THE TIME OF PREPARATION. ANY USE WHICH A THIRD PARTY MAKES OF THE CONTRACT DOCUMENTS, OR ANY RELIANCE ON/OR DECISIONS TO BE MADE BASED ON THEM ARE THE RESPONSIBILITY OF SUCH THIRD PARTIES.
7. THE CONSULTANT ACCEPTS NO RESPONSIBILITY FOR DAMAGES, IF ANY, SUFFERED BY ANY THIRD PARTY AS A RESULT OF DECISIONS MADE OR ACTIONS BASED ON THE CONTRACT DOCUMENTS.

PRELIMINARY
NOT FOR CONSTRUCTION

PROJECT TITLE
THE EDEN PROJECT


CLIENT:
Eden Project
PROJECT ADDRESS
555 McCormick Street

DRAWING TITLE
COVER PAGE

CHECKED	DRAWN	DATE
GG	AFNM	15/08/25

0001	A0.0
PROJECT No.	DRAWING

NORTH ARROW

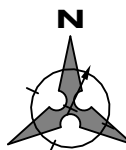

GENERAL NOTES

1. DO NOT SCALE DRAWINGS. WRITTEN DIMENSIONS SHALL HAVE PRECEDENCE OVER SCALED DIMENSIONS.
2. ALL WORK SHALL COMPLY WITH THE 2012 ONTARIO BUILDING CODE AND AMENDMENTS.
3. CONTRACTORS MUST CHECK AND VERIFY ALL DIMENSIONS AND SPECIFICATIONS AND REPORT ANY DISCREPANCIES TO THE ARCHITECT BEFORE PROCEEDINGS WITH THE WORK.
4. ALL CONTRACTORS AND SUB-CONTRACTORS SHALL HAVE A SET OF APPROVED CONSTRUCTION DOCUMENTS ON SITE AT ALL TIMES.
5. ALL DOCUMENTS REMAIN THE PROPERTY OF THE ARCHITECT. UNAUTHROIZED USE, MODIFICATION, AND/OR REPRODUCTION OF THESE DOCUMENTS IS PROHIBITED WITHOUT WRITTEN PERMISSION. THE CONTRACT DOCUMENTS WERE PREPARED BY THE CONSULTANT FOR THE ACCOUNT OF THE OWNER.
6. THE MATERIAL CONTAINED HEREIN REFLECTS THE CONSULTANTS BEST JUDEGMENT IN LIGHT OF THE INFORMATION AVAILABLE TO HIM/HER AT THE TIME OF PREPARATION. ANY USE WHICH A THIRD PARTY MAKES OF THE CONTRACT DOCUMENTS, OR ANY RELIANCE ON/OR DESCISIONS TO BE MADE BASED ON THEM ARE THE RESPONSIBILITY OF SUCH THIRD PARTIES.
7. THE CONSULTANT ACCEPTS NO RESPONSIBILITY FOR DAMAGES, IF ANY, SUFFERED BY ANY THIRD PARTY AS A RESULT OF DECISIONS MADE OR ACTIONS BASED ON THE CONTRACT DOCUMENTS

PRELIMINARY
NOT FOR CONSTRUCTION

PROJECT TITLE
THE EDEN PROJECT

CLIENT:
Eden Project
PROJECT ADDRESS
555 McCormick Street

DRAWING TITLE
ABBREVIATIONS & OBC MATRIX


CHECKED | DRAWN | DATE
GG | AFNM | 15/08/25

0001
PROJECT No.

A0.1
DRAWING

ABBREVIATIONS LEGEND		
GENERAL ABBREVIATIONS		MATERIAL LEGEND
AFF BD BF CCJ CHB CJ CM CONT CONC CS CW DCS DST DISP ECS EQ EK EXP EXIST FB FD F.D.C. FEC FLEX FL GALV GEN HDCP INSUL LPS MATL MIN NC NTS PB PJ PLYWD PS PT RRATG RCH RENF RD RM RWL SPEED STRUCT SW TB THERM TYP UC US VAP VF WI WIO	- ABOVE FINISHED FLOOR - BOARD - BARRIER FREE - COMPARTMENT CONTROL JOINT - CHALK BOARD - CONTROL JOINT - CONTROL MODULE - CONTINUOUS - CONCRETE - CLEAR STAIN - COMPLETE WITH - DROPPED CURB - DRAIN WATER DOWNSPOUT - DISTANCE - DISPLAY CASE - ELEVATOR CALL BUTTONS - EMERGENCY CALL SWITCH - EYE WASH STATION - EXISTING - EXPOSED - EXTERIOR - EXISTING - FIRE BLANKET - FIRE DEPARTMENT CONNECTION - FIRE EXTINGUISHER CABINET - FINISH - FLEXIBLE - FLOOR - GALVANIZED - GENERAL - HANDICAPPED - INSULATION - LOCK PUSH BUTTON - MATERIAL - MINIMAL / MINUTE - NOT IN CONTRACT - NOT TO SCALE - PUSH BUTTON (POWER DOOR OPERATOR) - ROCKET DOOR - PROJECTOR - PROJECTION SCREEN - PRESERVATIVE TREATED - RATING - RECESSED CAS HEATER - REINFORCED - ROOF DRAIN - ROOM - RAIN WATER LEADER - SPECIFIED - STRUCTURAL - SIDE WALK - TACK BOARD - THERMAL - TYPICAL - UNDER CUT - UNDER SIDE - VAPOUR - VERIFY IN FIELD - WITH - WITHOUT	ACT AL ALG ALP ALV AN AT BUR C CAR CART CB CJ CL CMB CONC C(S) CT EPC EMG EXP FD FG FLM FS GB GB2 GL GSS GWB GWG HDCP HM HMG HND HWG MC MFL MG MPR MR MSY MTD NAT P PC PS PLAM POS PS PREFN PTD QT R RG RM RS S SB SBC SC SF SG SP SPC SPNL S/S ST STF STGL S&V TB TEMP TS U VCT VF VR WB WBL WO WV WP
ACT AL ALG ALP ALV AN AT BUR C CAR CART CB CJ CL CMB CONC C(S) CT EPC EMG EXP FD FG FLM FS GB GB2 GL GSS GWB GWG HDCP HM HMG HND HWG MC MFL MG MPR MR MSY MTD NAT P PC PS PLAM POS PS PREFN PTD QT R RG RM RS S SB SBC SC SF SG SP SPC SPNL S/S ST STF STGL S&V TB TEMP TS U VCT VF VR WB WBL WO WV WP	- ACOUSTIC CEILING TILE - ALUMINUM - ALUMINUM GLAZING SYSTEM - ALUMINUM PLATES - ALUMINUM LOUVRES - ANODIZED - ACOUSTIC TILE - BUILT-UP ROOFING - CONCRETE - CARPET - CARPET TILE - CONCRETE BLOCK - CONTROL JOINT - CLEAR - CEMENT BOARD - CONCRETE - SEALED CONCRETE - CERAMIC TILE - EXPOSED PRECAST CONCRETE - EXPOSED - FLOOR DRAIN - FROSTED GLASS - GLAZING FILM - FLOOR SOCKET - GYPSUM BOARD - MOISTURE RESISTANT GYP. BD. - GLAZING / VISION GLASS - GALVANIZED STEEL SECTION - GYPSUM WALLBOARD - GEORGIAN WIRE GLAZING - HARDWARE (DOOR) - HOLLOW METAL - HOLLOW METAL GLAZING SYSTEM - HARDWOOD, CLEAR FINISH - HARDWOOD GLAZING SYSTEM - METAL GLADDING - METAL FLASHING (PRE-FINISHED) - METAL GATE - MAPRAIL - MIRROR - MASONRY - MOUNTING TRACK FOR DISPLAYS - NATURAL - PAINTED - PRECAST CONCRETE - PARTITION SYSTEM - PLASTIC LAMINATE - POINT OF SALE - CEILING MOUNTED PROJECTOR - PRE-FINISHED - PAINTED - QUARRY TILE - RUBBER - REFLECTIVE GLASS - ROOFING MEMBRANE - ROLLER SHADE - SEALED - STONE BASE - SAND-BLASTED POURED CONCRETE - SOLID CORE - SHEET FLOORING - STRUCTURAL GLAZING - SPECIAL COATING - STRUCTURAL PRECAST CONCRETE - SPANDREL PANEL - STAINLESS STEEL - STONE - STONE FLOOR TILE - STRUCTURAL GLAZING SYSTEM - STAINED & VARNISHED - TACKBOARD - TEMPERED GLAZING - TOP SOIL - POLY-URETHANE - VINYL COMPOSITE TILE - VENEER FACED - VENTED RUBBER BASE - WHITEBOARD MARKERBOARD - WINDOW BLIND - WOOD - WOOD VENEER - WOOD PANEL SYSTEM	- ACOUSTIC CEILING TILE - ALUMINUM - ALUMINUM GLAZING SYSTEM - ALUMINUM PLATES - ALUMINUM LOUVRES - ANODIZED - ACOUSTIC TILE - BUILT-UP ROOFING - CONCRETE - CARPET - CARPET TILE - CONCRETE BLOCK - CONTROL JOINT - CLEAR - CEMENT BOARD - CONCRETE - SEALED CONCRETE - CERAMIC TILE - EXPOSED PRECAST CONCRETE - EXPOSED - FLOOR DRAIN - FROSTED GLASS - GLAZING FILM - FLOOR SOCKET - GYPSUM BOARD - MOISTURE RESISTANT GYP. BD. - GLAZING / VISION GLASS - GALVANIZED STEEL SECTION - GYPSUM WALLBOARD - GEORGIAN WIRE GLAZING - HARDWARE (DOOR) - HOLLOW METAL - HOLLOW METAL GLAZING SYSTEM - HARDWOOD, CLEAR FINISH - HARDWOOD GLAZING SYSTEM - METAL GLADDING - METAL FLASHING (PRE-FINISHED) - METAL GATE - MAPRAIL - MIRROR - MASONRY - MOUNTING TRACK FOR DISPLAYS - NATURAL - PAINTED - PRECAST CONCRETE - PARTITION SYSTEM - PLASTIC LAMINATE - POINT OF SALE - CEILING MOUNTED PROJECTOR - PRE-FINISHED - PAINTED - QUARRY TILE - RUBBER - REFLECTIVE GLASS - ROOFING MEMBRANE - ROLLER SHADE - SEALED - STONE BASE - SAND-BLASTED POURED CONCRETE - SOLID CORE - SHEET FLOORING - STRUCTURAL GLAZING - SPECIAL COATING - STRUCTURAL PRECAST CONCRETE - SPANDREL PANEL - STAINLESS STEEL - STONE - STONE FLOOR TILE - STRUCTURAL GLAZING SYSTEM - STAINED & VARNISHED - TACKBOARD - TEMPERED GLAZING - TOP SOIL - POLY-URETHANE - VINYL COMPOSITE TILE - VENEER FACED - VENTED RUBBER BASE - WHITEBOARD MARKERBOARD - WINDOW BLIND - WOOD - WOOD VENEER - WOOD PANEL SYSTEM

Item	Ontario Building Code Data Matrix Parts 3 and 9				OBC Reference	
1	Project Description:	THE EDEN PROJECT	☒ New ☒ Addition ☐ Change of Use ☒ Alteration	☒ Part 11	☒ Part 3 ☐ Part 9	2.1.1 9.10.1.3
2	Major Occupancy(s):					3.1.2.1.(1) 9.10.2
3	Building Area (m2):	Existing: _____	New: _____	Total: _____		1.1.3.2 1.1.3.2
4	Gross Area:	Existing: _____	New: _____	Total: _____		1.1.3.2 1.1.3.2
5	Number of Storeys:	Above Grade: _____	Below Grade: _____			3.2.1.18 1.1.3.2
6	Height of Building:					2.1.1.3
7	Number of Streets/Access Route(s):					3.2.2.108 3.2.5.5
8	Building Classification:					3.2.2.20 - 83 9.10.4
9	Sprinkler System Proposed:		☒ Entire Building ☐ Basement Only ☐ In Lieu of Roof Rating ☐ Not Required			3.2.2.20 - 83 3.2.1.5 3.2.2.17 9.10.4
10	Standpipe Required:	☒ Yes ☐ No				3.2.9
11	Fire Alarm Required:	☒ Yes ☐ No				3.2.4 9.10.7.2
12	Water Service / Adequate Supply:	☒ Yes ☐ No				
13	High Building:	☐ Yes ☒ No				3.2.6
14	Permitted Construction:	☐ Combustible ☐ Non-combustible ☒ Both				3.2.2.20 - 83 9.10.6
15	Actual Construction:	☐ Combustible ☐ Non-combustible ☒ Both				3.2.1.1.(3)-(8) 9.10.4.1
16	Mezzanine Area (m2):					3.1.1.6 9.10.4.1
17	Occupant Load Based On:	☒ m2 / person ☐ Design of Building				3.1.1.6 9.10.4.1
18	Barrier Free:	☒ Yes ☐ No (Explain): _____				3.8 9.5.2
19	Hazardous Substances:	☐ Yes ☒ No (Explain): _____				3.3.1.2(1) 3.3.1.19.(1) 9.10.1.3
20	Horizontal Assemblies (FRR - Hours)					3.2.1.4 9.10.9
21	Listed Design No. or Description (SB-2)					
22	Floor(s):	01	Hours			N/A
23	Roof:	N/A	Hours			--
24	Mezzanine(s):	--	Hours			--
25	FRR Supporting Member(s)					
26	Listed Design No. or Description (SB-2)					
27	Floor(s):	1	Hours			--
28	Roof:	1	Hours			--
29	Mezzanine(s):	--	Hours			--
30	Spatial Separation - Construction of Exterior Walls:					3.2.3 9.10.14
31	Wall:	Area of EBF: (m2)	L.D.: (m) L/H: or H/L	Permitted Max. % of Openings	Proposed Max. % of Openings	FRR (Hours)
32	North:					
33	South:					
34	East:					
35	West:					

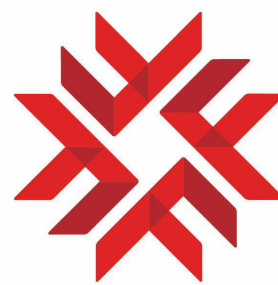

FANSHAWE
DONALD J. SMITH
SCHOOL OF BUILDING
TECHNOLOGY

NORTH ARROW



- GENERAL NOTES
1. DO NOT SCALE DRAWINGS. WRITTEN DIMENSIONS SHALL HAVE PRECEDENCE OVER SCALED DIMENSIONS.
 2. ALL WORK SHALL COMPLY WITH THE 2012 ONTARIO BUILDING CODE AND AMENDMENTS.
 3. CONTRACTORS MUST CHECK AND VERIFY ALL DIMENSIONS AND SPECIFICATIONS AND REPORT ANY DISCREPANCIES TO THE ARCHITECT BEFORE PROCEEDING WITH THE WORK.
 4. ALL CONTRACTORS AND SUB-CONTRACTORS SHALL HAVE A SET OF APPROVED CONSTRUCTION DOCUMENTS ON SITE AT ALL TIMES.
 5. ALL DOCUMENTS REMAIN THE PROPERTY OF THE ARCHITECT. UNAUTHORIZED USE, MODIFICATION, AND/OR REPRODUCTION OF THESE DOCUMENTS IS PROHIBITED WITHOUT WRITTEN PERMISSION. THE CONTRACT DOCUMENTS WERE PREPARED BY THE CONSULTANT FOR THE ACCOUNT OF THE OWNER.
 6. THE MATERIAL CONTAINED HEREIN REFLECTS THE CONSULTANT'S BEST JUDGMENT IN LIGHT OF THE INFORMATION AVAILABLE TO HIM/HER AT THE TIME OF PREPARATION. ANY USE WHICH A THIRD PARTY MAKES OF THE CONTRACT DOCUMENTS, OR ANY RELIANCE ON/OR DECISIONS TO BE MADE BASED ON THEM ARE THE RESPONSIBILITY OF SUCH THIRD PARTIES.
 7. THE CONSULTANT ACCEPTS NO RESPONSIBILITY FOR DAMAGES, IF ANY, SUFFERED BY ANY THIRD PARTY AS A RESULT OF DECISIONS MADE OR ACTIONS BASED ON THE CONTRACT DOCUMENTS.

PRELIMINARY
NOT FOR CONSTRUCTION

PROJECT TITLE
THE EDEN PROJECT

CLIENT:
Eden Project
PROJECT ADDRESS
555 McCormick Street

DRAWING TITLE
ASSEMBLIES SCHEDULE

CHECKED | DRAWN | DATE
GG | AFNM | 15/08/25


0001
PROJECT No. | A0.2
DRAWING

EXTERIOR & FOUNDATION WALL ASSEMBLIES


TAG: EXW-1	O.B.C./ULC NUMBER:	W605
	R-VALUE:	N/A
	F.R.R.:	1 HR
	STC RATING:	50 & 55
DESCRIPTION: ARCHITECTURAL BRICK WALL		




TAG: EXW-3	O.B.C./ULC NUMBER:	W605
	R-VALUE:	N/A
	F.R.R.:	1 HR
	STC RATING:	50 & 55
DESCRIPTION: VERTICAL WOOD SIDING COVER		

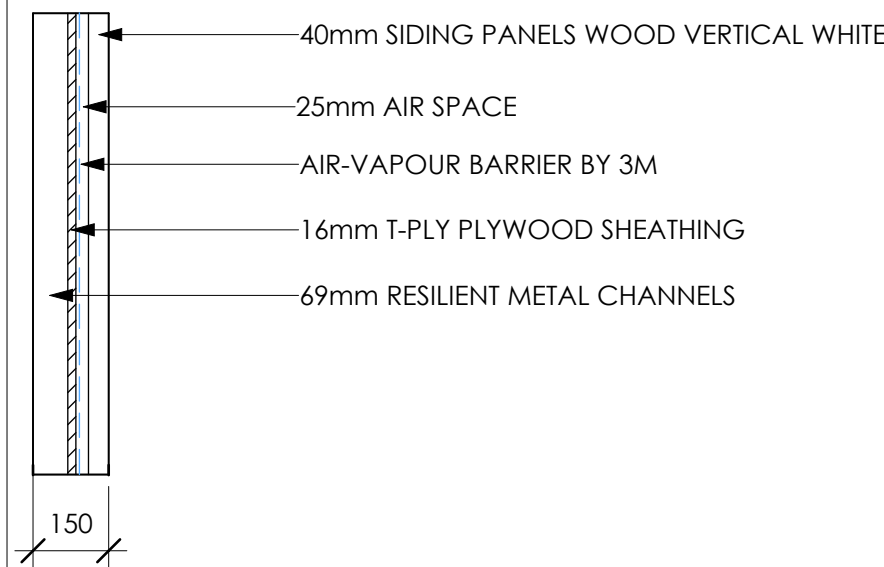


TAG: EXW-5	O.B.C./ULC NUMBER:	N/A
	R-VALUE:	N/A
	F.R.R.:	N/A
	STC RATING:	N/A
DESCRIPTION: CURTAIN WALL		

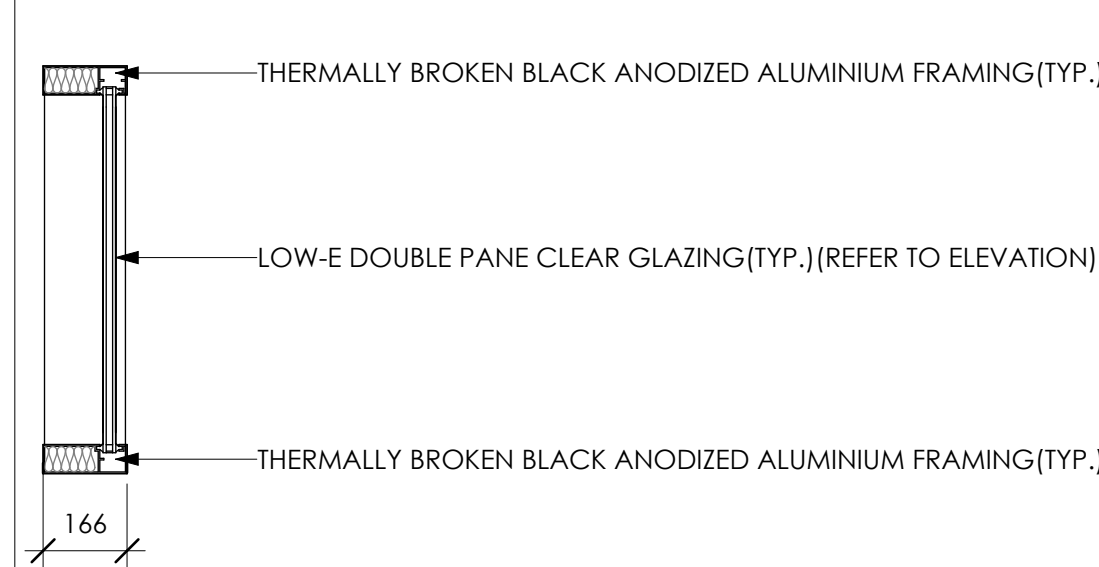


TAG: FDN-2	O.B.C./ULC NUMBER:	N/A
	R-VALUE:	N/A
	F.R.R.:	N/A
	STC RATING:	N/A
DESCRIPTION: FOUNDATION WALL		

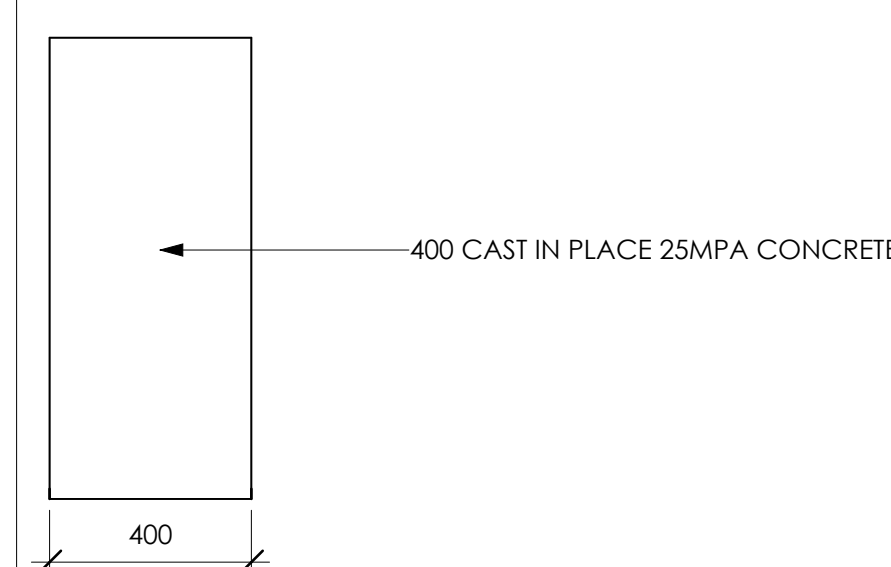

TAG: EXW-2	O.B.C./ULC NUMBER:	W605
	R-VALUE:	N/A
	F.R.R.:	1 HR
	STC RATING:	50 & 55
DESCRIPTION: VERTICAL WOOD SIDING WALL		

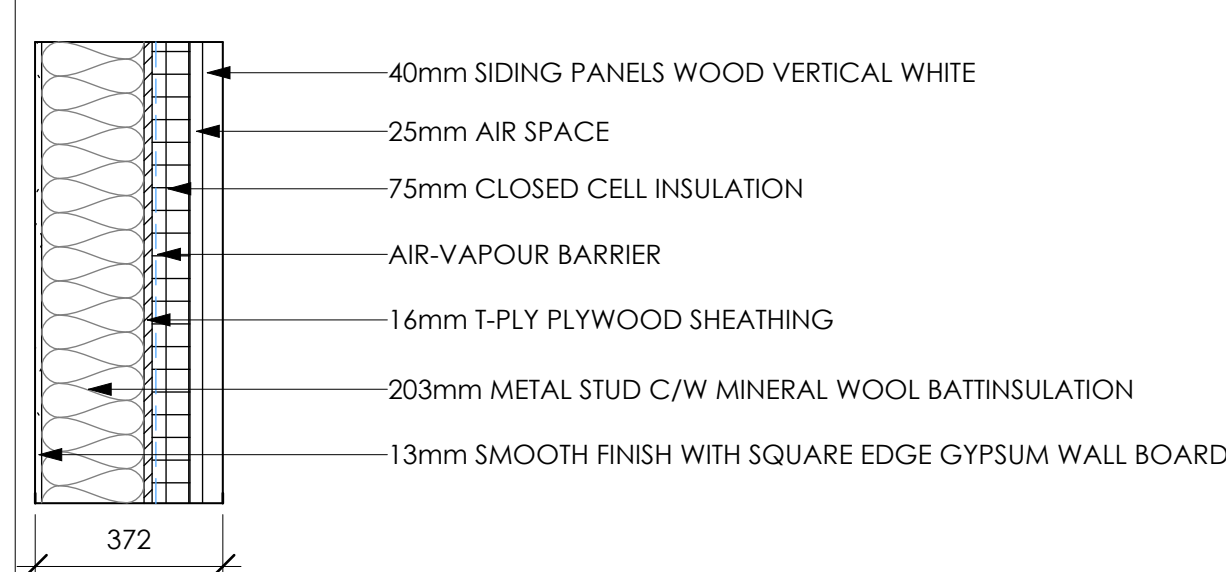


TAG: EXW-4	O.B.C./ULC NUMBER:	W605
	R-VALUE:	N/A
	F.R.R.:	1 HR
	STC RATING:	50 & 55
DESCRIPTION: EXISTING BRICK WALL		

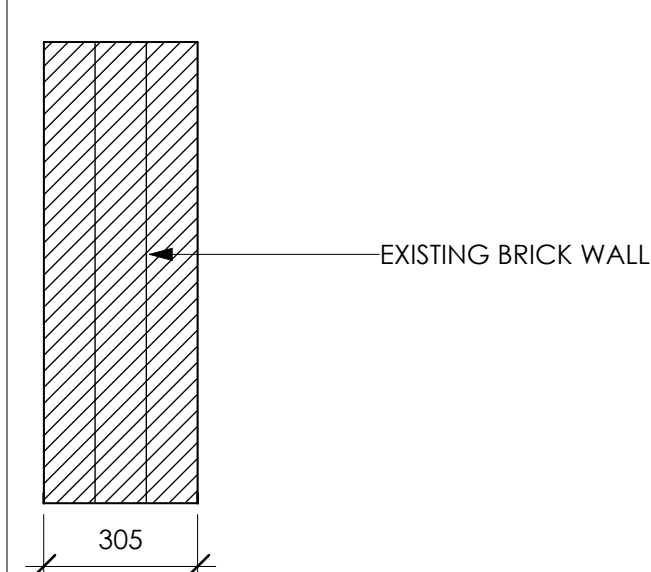

TAG: FDN-1	O.B.C./ULC NUMBER:	N/A
	R-VALUE:	N/A
	F.R.R.:	N/A
	STC RATING:	N/A
DESCRIPTION: FOUNDATION WALL		




TAG: FDN-3	O.B.C./ULC NUMBER:	N/A
	R-VALUE:	N/A
	F.R.R.:	N/A
	STC RATING:	N/A
DESCRIPTION: FOUNDATION WALL		

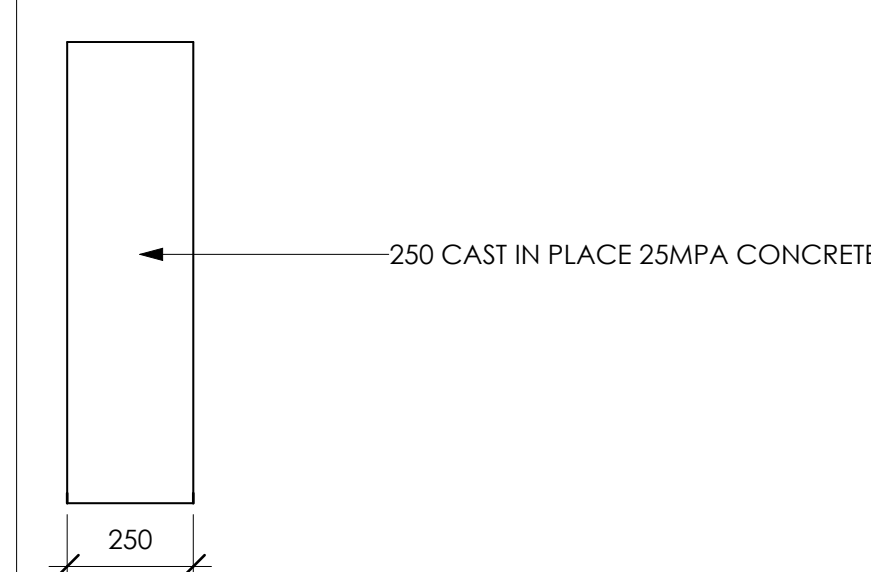


INTERIOR WALL ASSEMBLIES

TAG: INT-1	O.B.C./ULC NUMBER:	N/A
	R-VALUE:	N/A
	F.R.R.:	1 HR
	STC RATING:	N/A
DESCRIPTION: FIRE RATED WALL FOR COLUMN		

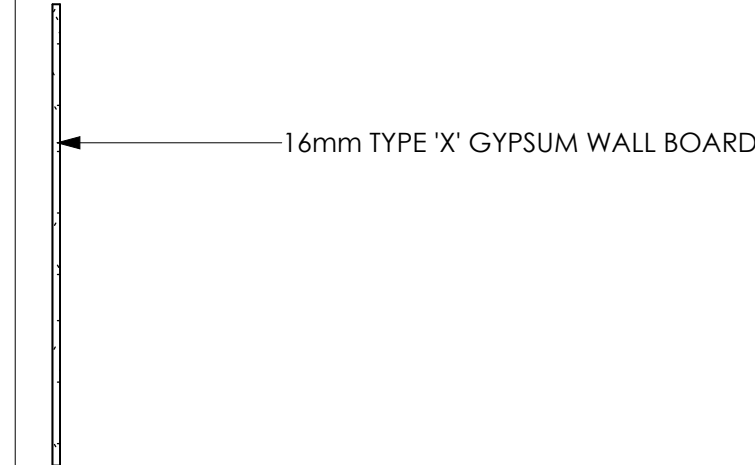


TAG: INT-3	O.B.C./ULC NUMBER:	N/A
	R-VALUE:	N/A
	F.R.R.:	1 HR
	STC RATING:	50 & 55
DESCRIPTION: PARTITION WALL		

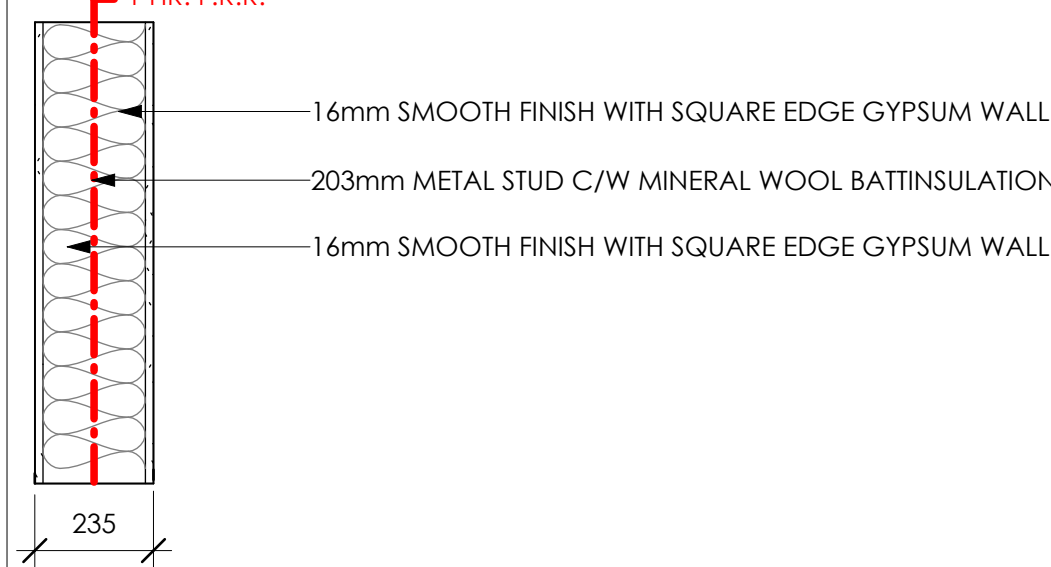


TAG: INT-5	O.B.C./ULC NUMBER:	W453
	R-VALUE:	N/A
	F.R.R.:	N/A
	STC RATING:	40
DESCRIPTION: SHAFT WALL		




TAG: INT-2	O.B.C./ULC NUMBER:	N/A
	R-VALUE:	N/A
	F.R.R.:	1 HR
	STC RATING:	50 & 55
DESCRIPTION: PARTITION WALL		

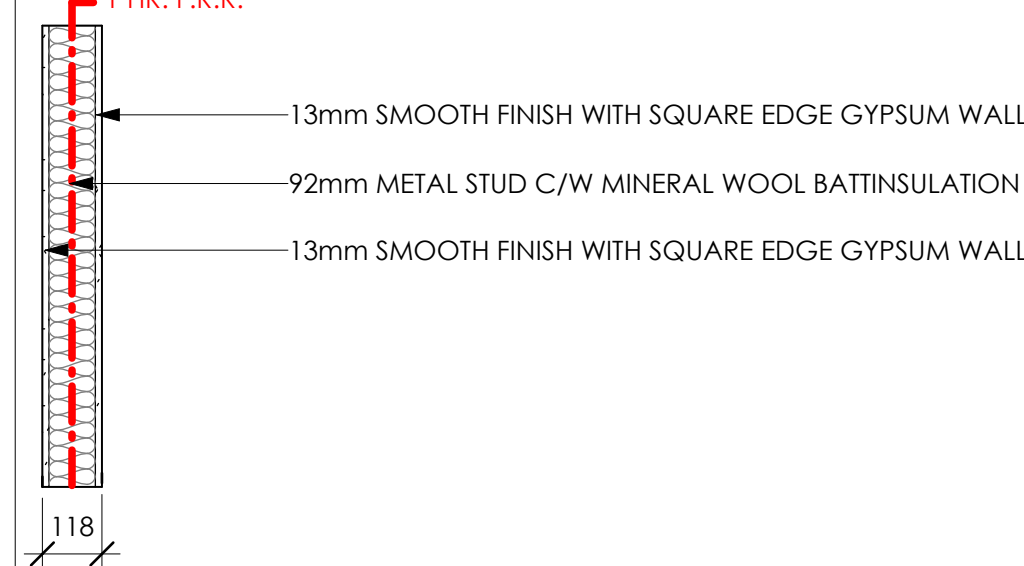


TAG: INT-4	O.B.C./ULC NUMBER:	N/A
	R-VALUE:	N/A
	F.R.R.:	1 HR
	STC RATING:	50 & 55
DESCRIPTION: PARTITION WALL		

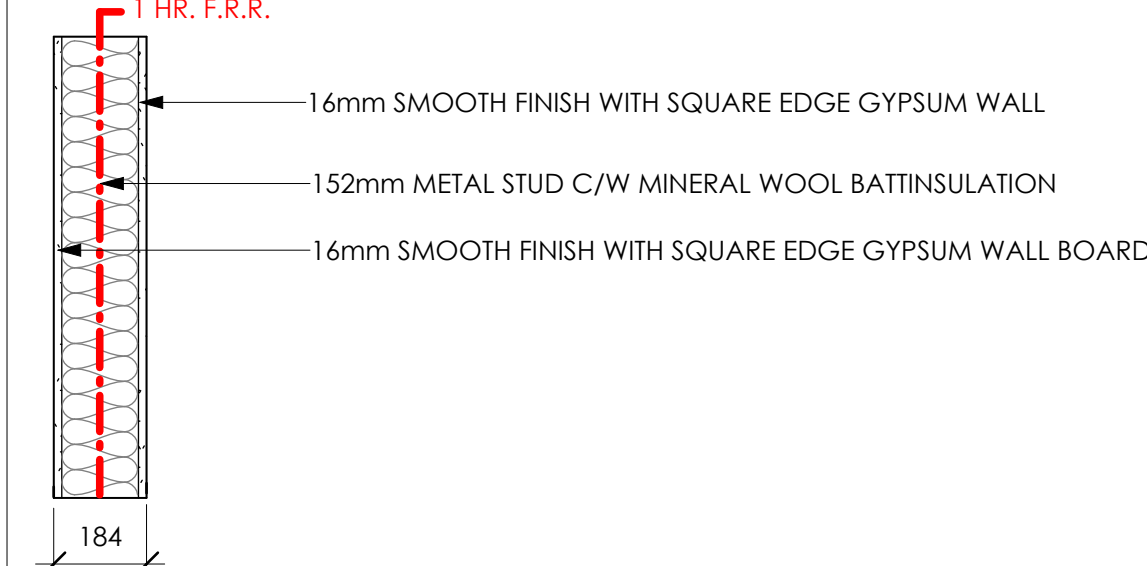

TAG: FRW-1	O.B.C./ULC NUMBER:	N/A
	R-VALUE:	N/A
	F.R.R.:	1 HR
	STC RATING:	N/A
DESCRIPTION: BLOCK WALL		

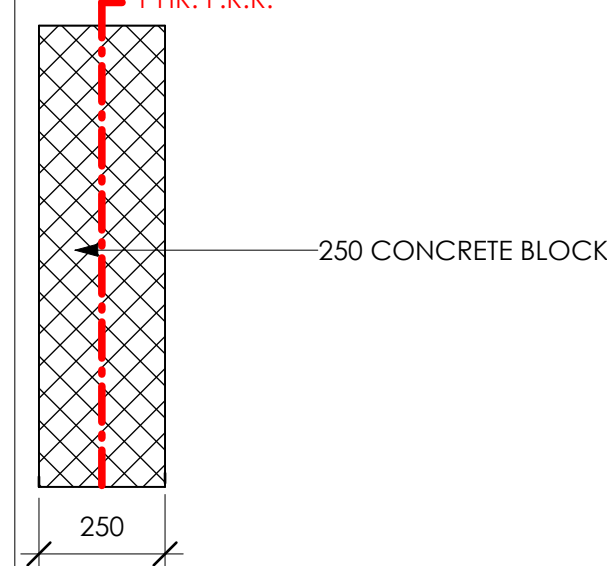

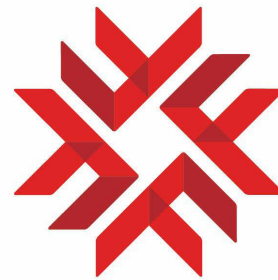

FANSHAW
DONALD J. SMITH
SCHOOL OF BUILDING
TECHNOLOGY

NORTH ARROW



GENERAL NOTES

1. DO NOT SCALE DRAWINGS. WRITTEN DIMENSIONS SHALL HAVE PRECEDENCE OVER SCALED DIMENSIONS.
2. ALL WORK SHALL COMPLY WITH THE 2012 ONTARIO BUILDING CODE AND AMENDMENTS.
3. CONTRACTORS MUST CHECK AND VERIFY ALL DIMENSIONS AND SPECIFICATIONS AND REPORT ANY DISCREPANCIES TO THE ARCHITECT BEFORE PROCEEDING WITH THE WORK.
4. ALL CONTRACTORS AND SUB-CONTRACTORS SHALL HAVE A SET OF APPROVED CONSTRUCTION DOCUMENTS ON SITE AT ALL TIMES.
5. ALL DOCUMENTS REMAIN THE PROPERTY OF THE ARCHITECT. UNAUTHORIZED USE, MODIFICATION, AND/OR REPRODUCTION OF THESE DOCUMENTS IS PROHIBITED WITHOUT WRITTEN PERMISSION. THE CONTRACT DOCUMENTS WERE PREPARED BY THE CONSULTANT FOR THE ACCOUNT OF THE OWNER.
6. THE MATERIAL CONTAINED HEREIN REFLECTS THE CONSULTANT'S BEST JUDGMENT IN LIGHT OF THE INFORMATION AVAILABLE TO HIM/HER AT THE TIME OF PREPARATION. ANY USE WHICH A THIRD PARTY MAKES OF THE CONTRACT DOCUMENTS, OR ANY RELIANCE ON/OR DECISIONS TO BE MADE BASED ON THEM ARE THE RESPONSIBILITY OF SUCH THIRD PARTIES.
7. THE CONSULTANT ACCEPTS NO RESPONSIBILITY FOR DAMAGES, IF ANY, SUFFERED BY ANY THIRD PARTY AS A RESULT OF DECISIONS MADE OR ACTIONS BASED ON THE CONTRACT DOCUMENTS

PRELIMINARY
NOT FOR CONSTRUCTION

PROJECT TITLE
THE EDEN PROJECT

CLIENT:
Eden Project
PROJECT ADDRESS
555 McCormick Street


DRAWING TITLE
ASSEMBLIES SCHEDULE

CHECKED
GG
DRAWN
AFNM
DATE
15/08/25


0001
PROJECT No.
A0.3
DRAWING

ROOF & CEILING ASSEMBLIES


TAG:	O.B.C./ULC NUMBER:	0
RF-1	R-VALUE:	35
DESCRIPTION:	F.R.R:	N/A
NEW ROOF	STC RATING:	N/A

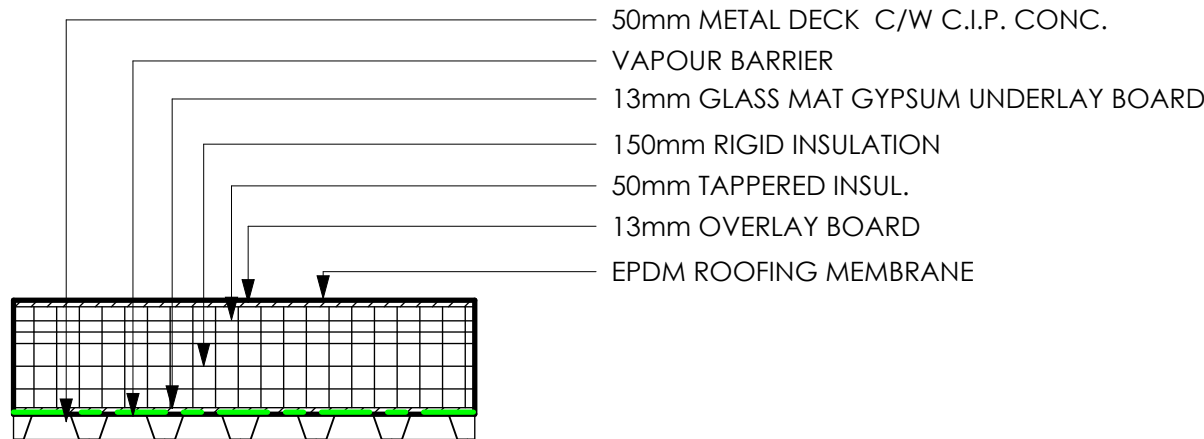


TAG:	O.B.C./ULC NUMBER:	N/A
RF-2	R-VALUE:	N/A
DESCRIPTION:	F.R.R:	N/A
EXISTING ROOF	STC RATING:	N/A

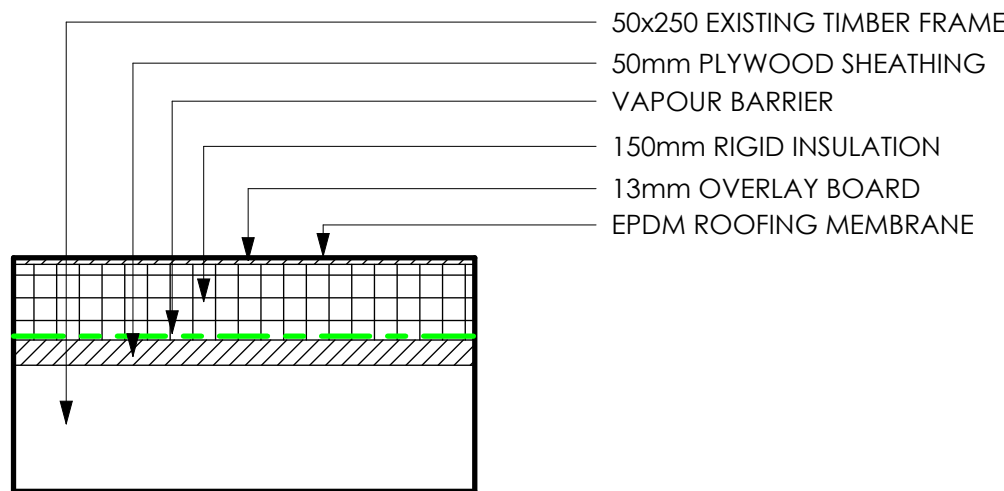


TAG:	O.B.C./ULC NUMBER:	N/A
CL-1	R-VALUE:	N/A
DESCRIPTION:	F.R.R:	N/A
CELLING	STC RATING:	N/A

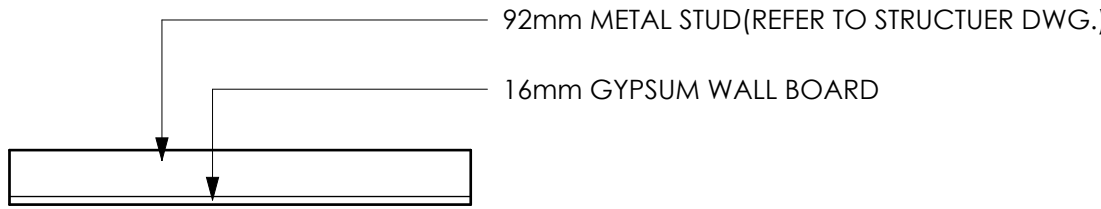


TAG:	O.B.C./ULC NUMBER:	N/A
CL-2	R-VALUE:	N/A
DESCRIPTION:	F.R.R:	N/A
CELLING	STC RATING:	N/A

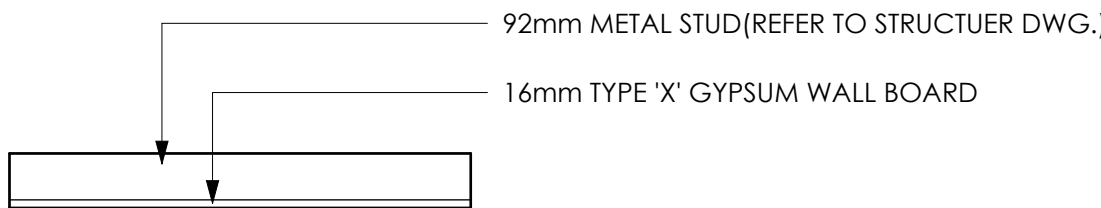


TAG:	O.B.C./ULC NUMBER:	N/A
-	R-VALUE:	N/A
DESCRIPTION:	F.R.R:	N/A
-	STC RATING:	N/A

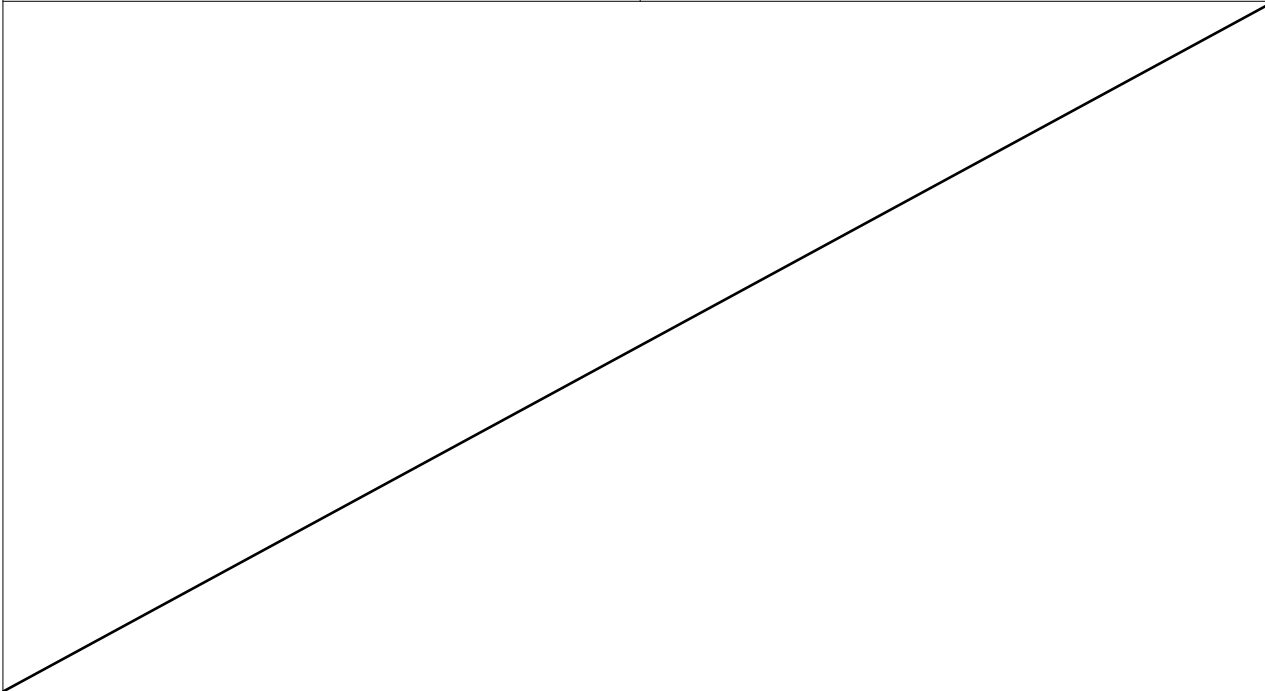


TAG:	O.B.C./ULC NUMBER:	N/A
-	R-VALUE:	N/A
DESCRIPTION:	F.R.R:	N/A
-	STC RATING:	N/A

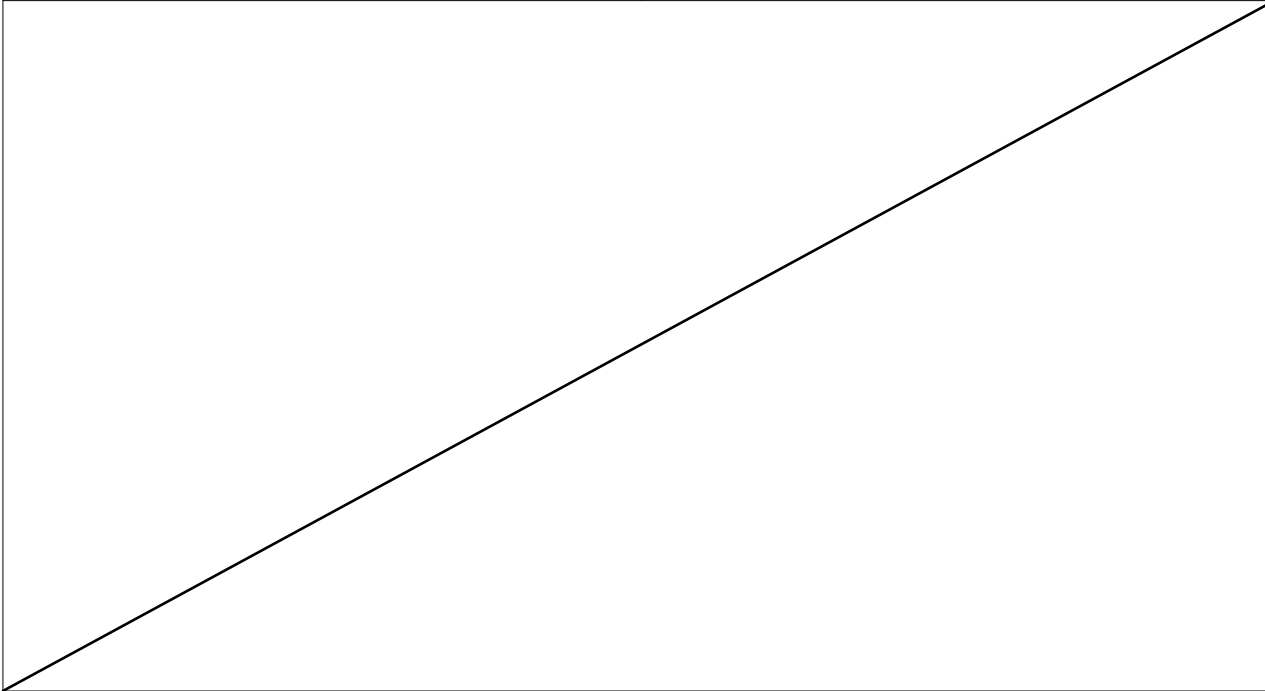

TAG:	O.B.C./ULC NUMBER:	N/A
-	R-VALUE:	N/A
DESCRIPTION:	F.R.R:	N/A
-	STC RATING:	N/A

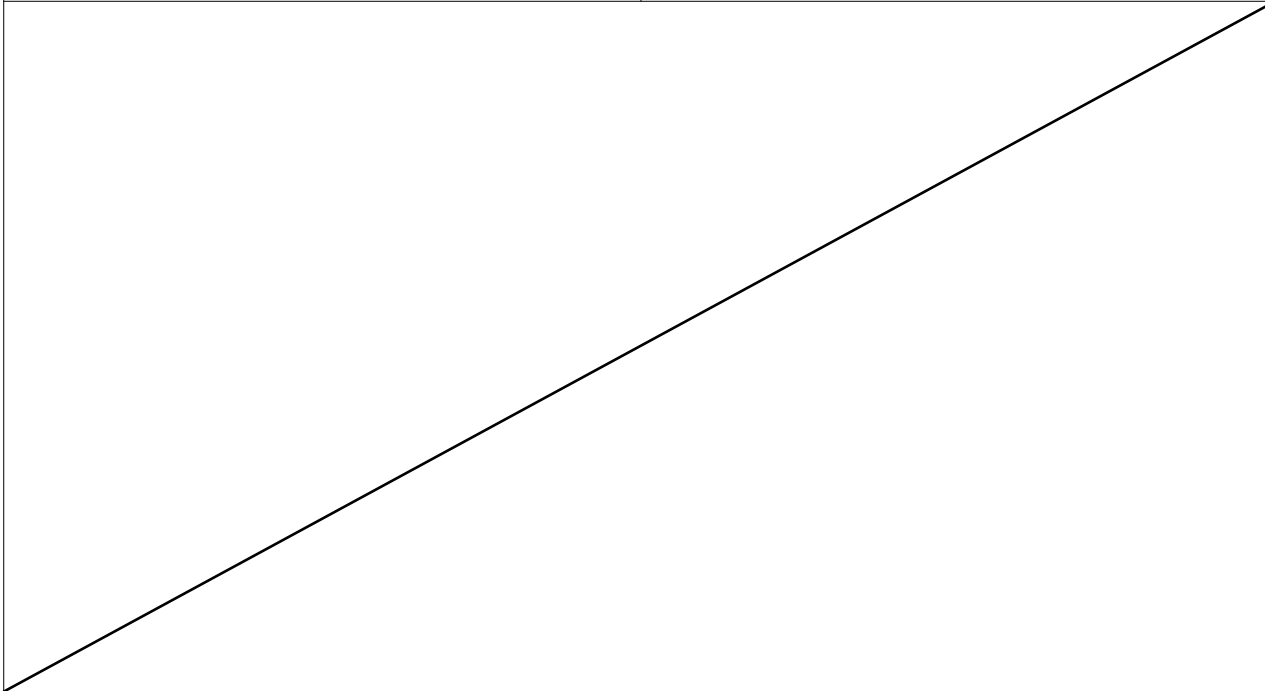


TAG:	O.B.C./ULC NUMBER:	N/A
-	R-VALUE:	N/A
DESCRIPTION:	F.R.R:	N/A
-	STC RATING:	N/A

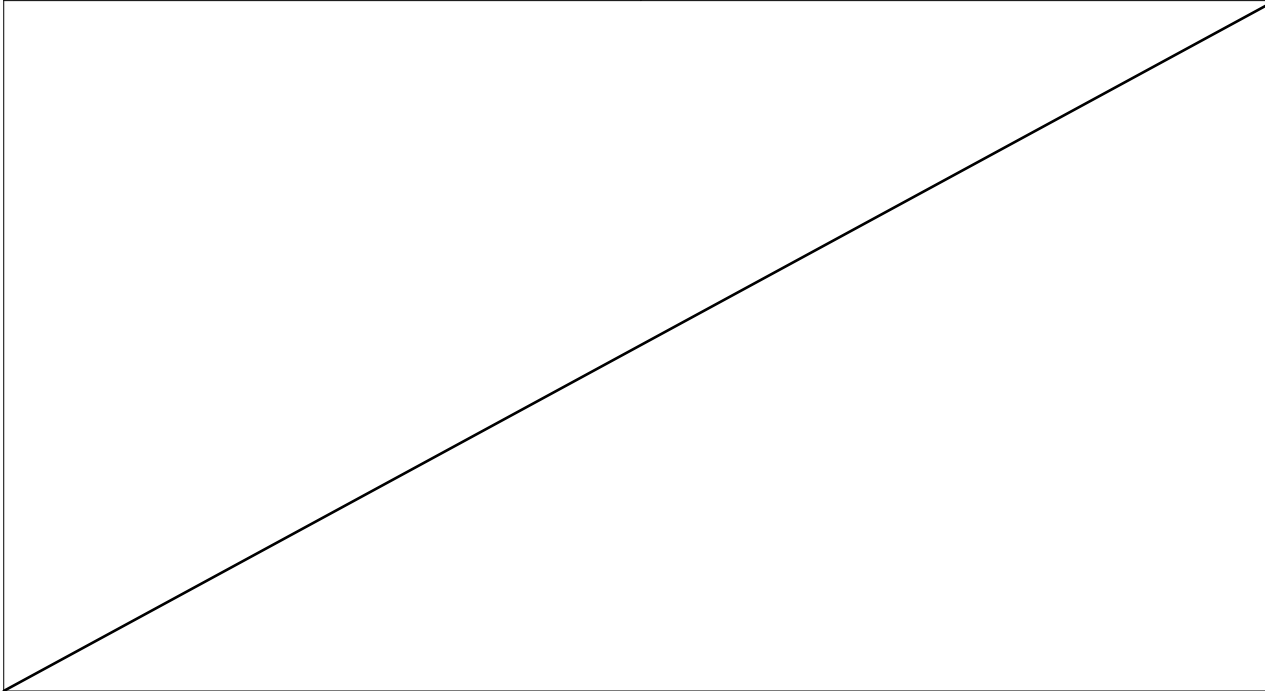


FLOOR ASSEMBLIES


TAG:	O.B.C./ULC NUMBER:	N/A
FLR-1	R-VALUE:	N/A
DESCRIPTION:	F.R.R:	N/A
100mm CONCRETE FLOOR	STC RATING:	N/A

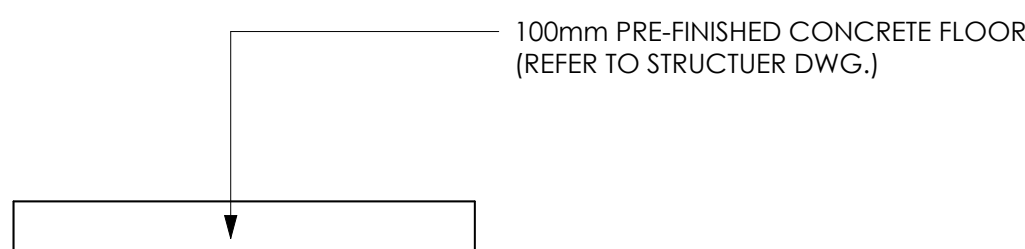


TAG:	O.B.C./ULC NUMBER:	N/A
FLR-2	R-VALUE:	N/A
DESCRIPTION:	F.R.R:	N/A
150mm CONCRETE FLOOR	STC RATING:	N/A

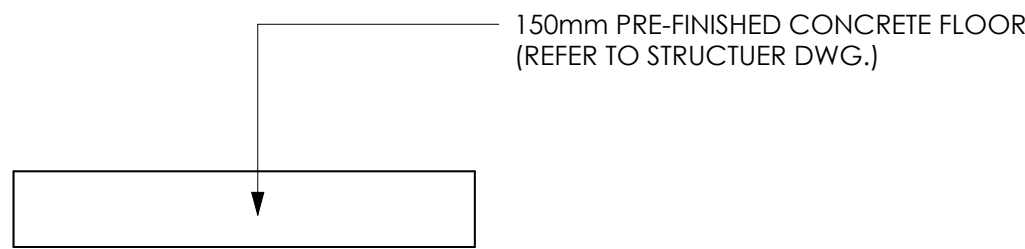


TAG:	O.B.C./ULC NUMBER:	N/A
FLR-3	R-VALUE:	N/A
DESCRIPTION:	F.R.R:	N/A
HOLLOWCORE FLOOR	STC RATING:	N/A

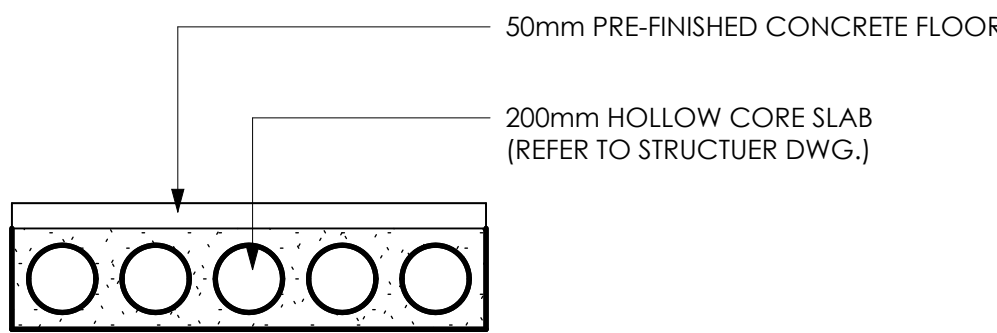


TAG:	O.B.C./ULC NUMBER:	N/A
FLR-4	R-VALUE:	N/A
DESCRIPTION:	F.R.R:	N/A
CONC. S.O.G. TYP	STC RATING:	N/A

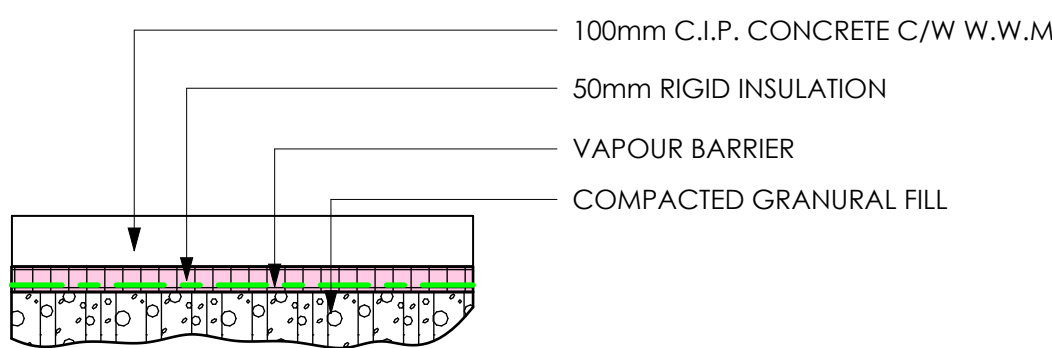


TAG:	O.B.C./ULC NUMBER:	N/A
-	R-VALUE:	N/A
DESCRIPTION:	F.R.R:	N/A
-	STC RATING:	N/A

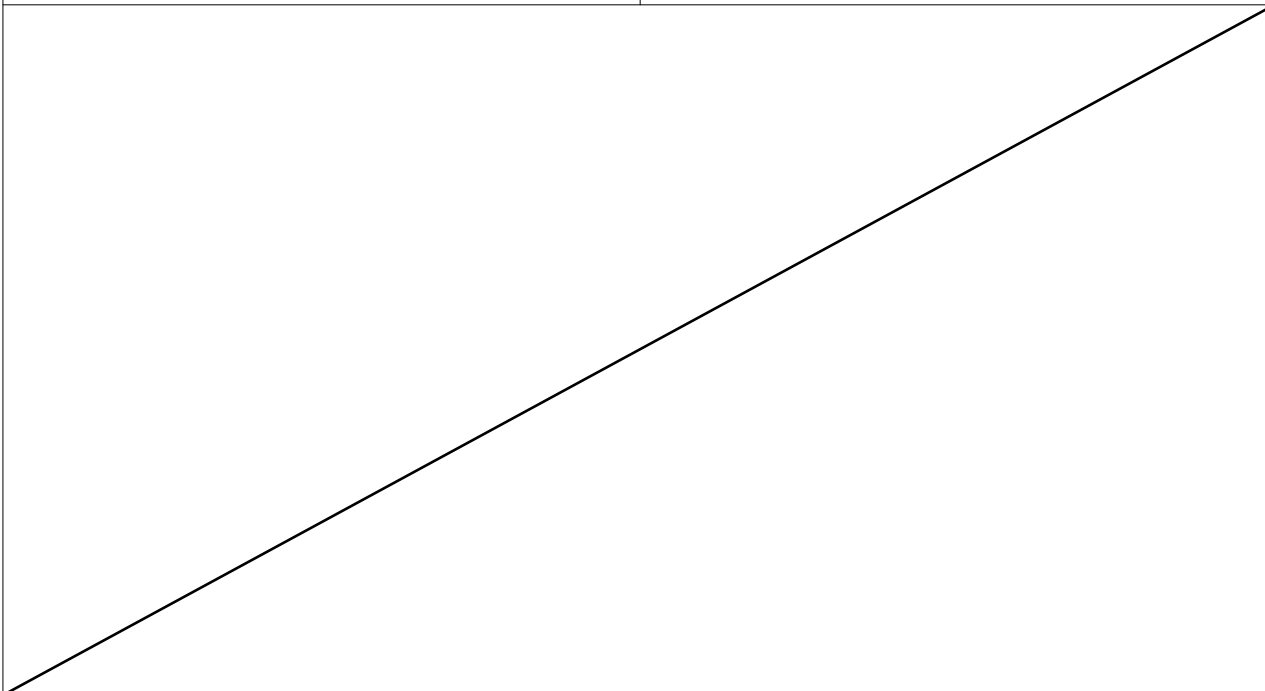


TAG:	O.B.C./ULC NUMBER:	N/A
-	R-VALUE:	N/A
DESCRIPTION:	F.R.R:	N/A
-	STC RATING:	N/A

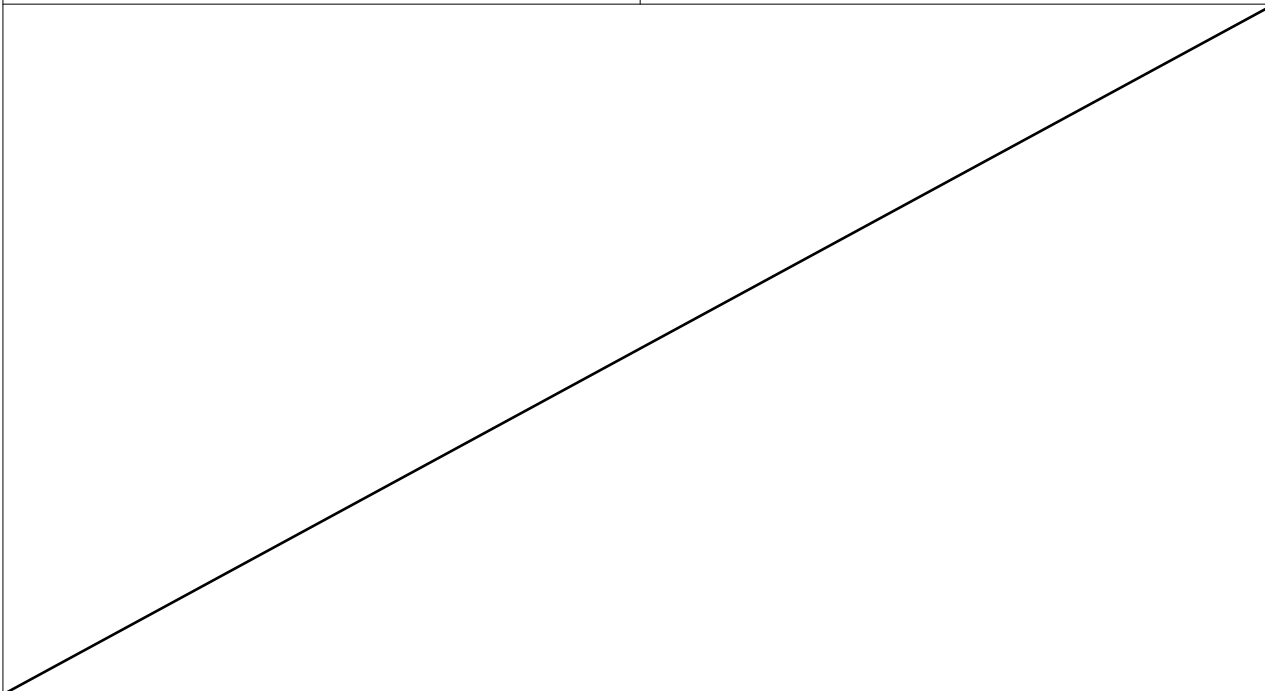


TAG:	O.B.C./ULC NUMBER:	N/A
-	R-VALUE:	N/A
DESCRIPTION:	F.R.R:	N/A
-	STC RATING:	N/A

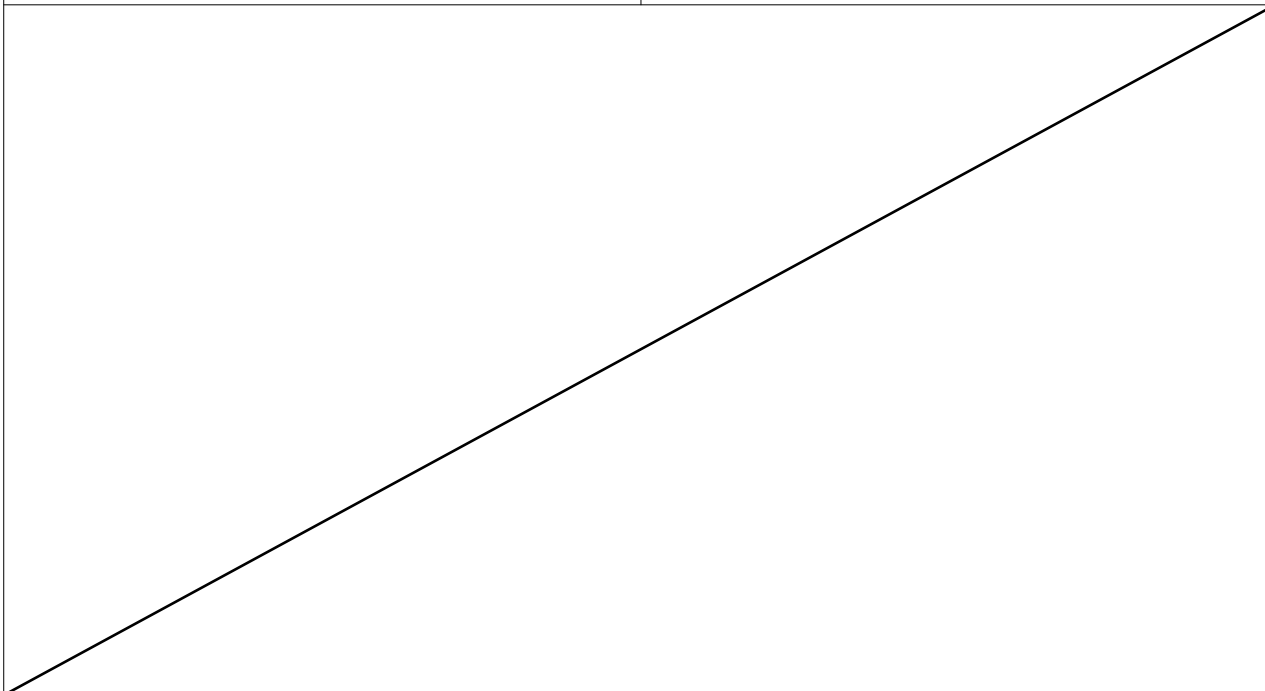

TAG:	O.B.C./ULC NUMBER:	N/A
-	R-VALUE:	N/A
DESCRIPTION:	F.R.R:	N/A
-	STC RATING:	N/A

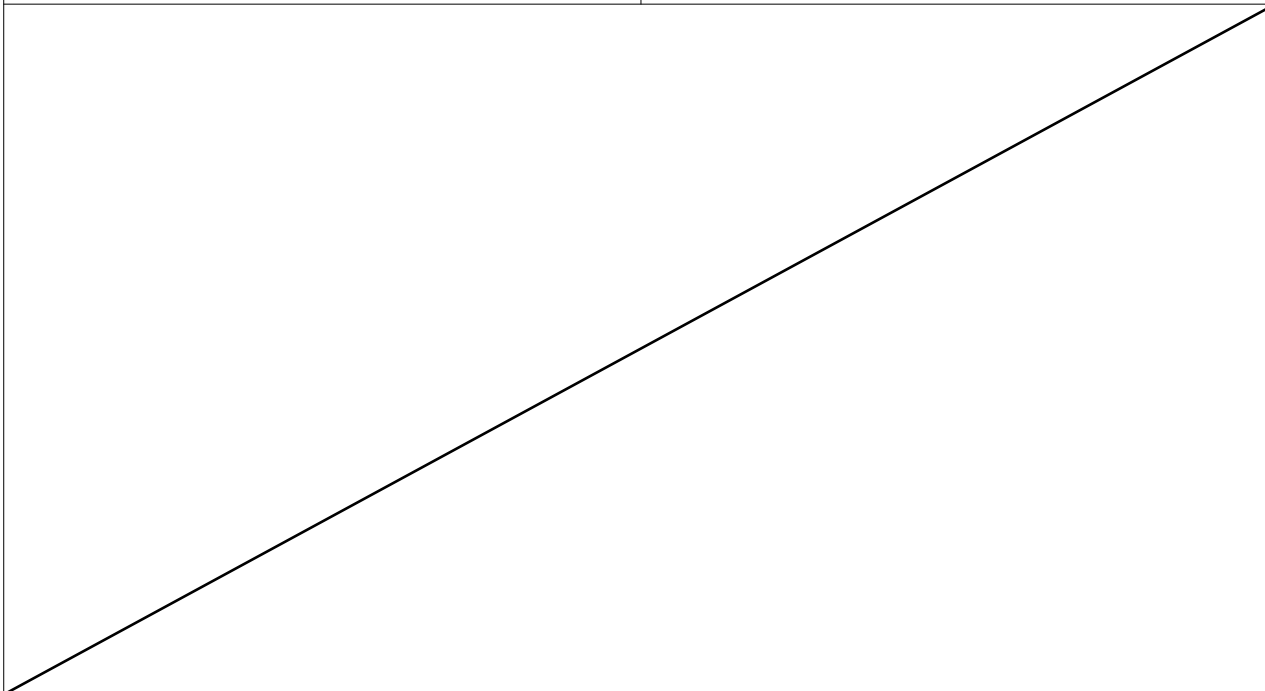

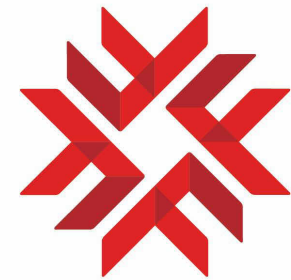

FANSHAW

DONALD J. SMITH
SCHOOL OF BUILDING
TECHNOLOGY

NORTH ARROW



GENERAL NOTES

1. DO NOT SCALE DRAWINGS. WRITTEN DIMENSIONS SHALL HAVE PRECEDENCE OVER SCALED DIMENSIONS.
2. ALL WORK SHALL COMPLY WITH THE 2012 ONTARIO BUILDING CODE AND AMENDMENTS.
3. CONTRACTORS MUST CHECK AND VERIFY ALL DIMENSIONS AND SPECIFICATIONS AND REPORT ANY DISCREPANCIES TO THE ARCHITECT BEFORE PROCEEDING WITH THE WORK.
4. ALL CONTRACTORS AND SUB-CONTRACTORS SHALL HAVE A SET OF APPROVED CONSTRUCTION DOCUMENTS ON SITE AT ALL TIMES.
5. ALL DOCUMENTS REMAIN THE PROPERTY OF THE ARCHITECT. UNAUTHORIZED USE, MODIFICATION, AND/OR REPRODUCTION OF THESE DOCUMENTS IS PROHIBITED WITHOUT WRITTEN PERMISSION. THE CONTRACT DOCUMENTS WERE PREPARED BY THE CONSULTANT FOR THE ACCOUNT OF THE OWNER.
6. THE MATERIAL CONTAINED HEREIN REFLECTS THE CONSULTANT'S BEST JUDGMENT IN LIGHT OF THE INFORMATION AVAILABLE TO HIM/HER AT THE TIME OF PREPARATION. ANY USE WHICH A THIRD PARTY MAKES OF THE CONTRACT DOCUMENTS, OR ANY RELIANCE ON/OR DECISIONS TO BE MADE BASED ON THEM ARE THE RESPONSIBILITY OF SUCH THIRD PARTIES.
7. THE CONSULTANT ACCEPTS NO RESPONSIBILITY FOR DAMAGES, IF ANY, SUFFERED BY ANY THIRD PARTY AS A RESULT OF DECISIONS MADE OR ACTIONS BASED ON THE CONTRACT DOCUMENTS.

PRELIMINARY
NOT FOR CONSTRUCTION


PROJECT TITLE
THE EDEN PROJECT

CLIENT:
Eden Project
PROJECT ADDRESS
555 McCormick Street



DRAWING TITLE
FOUNDATION PLAN

CHECKED GG
DRAWN AFNM
DATE 15/08/25

0001
PROJECT No.
A2.0
DRAWING

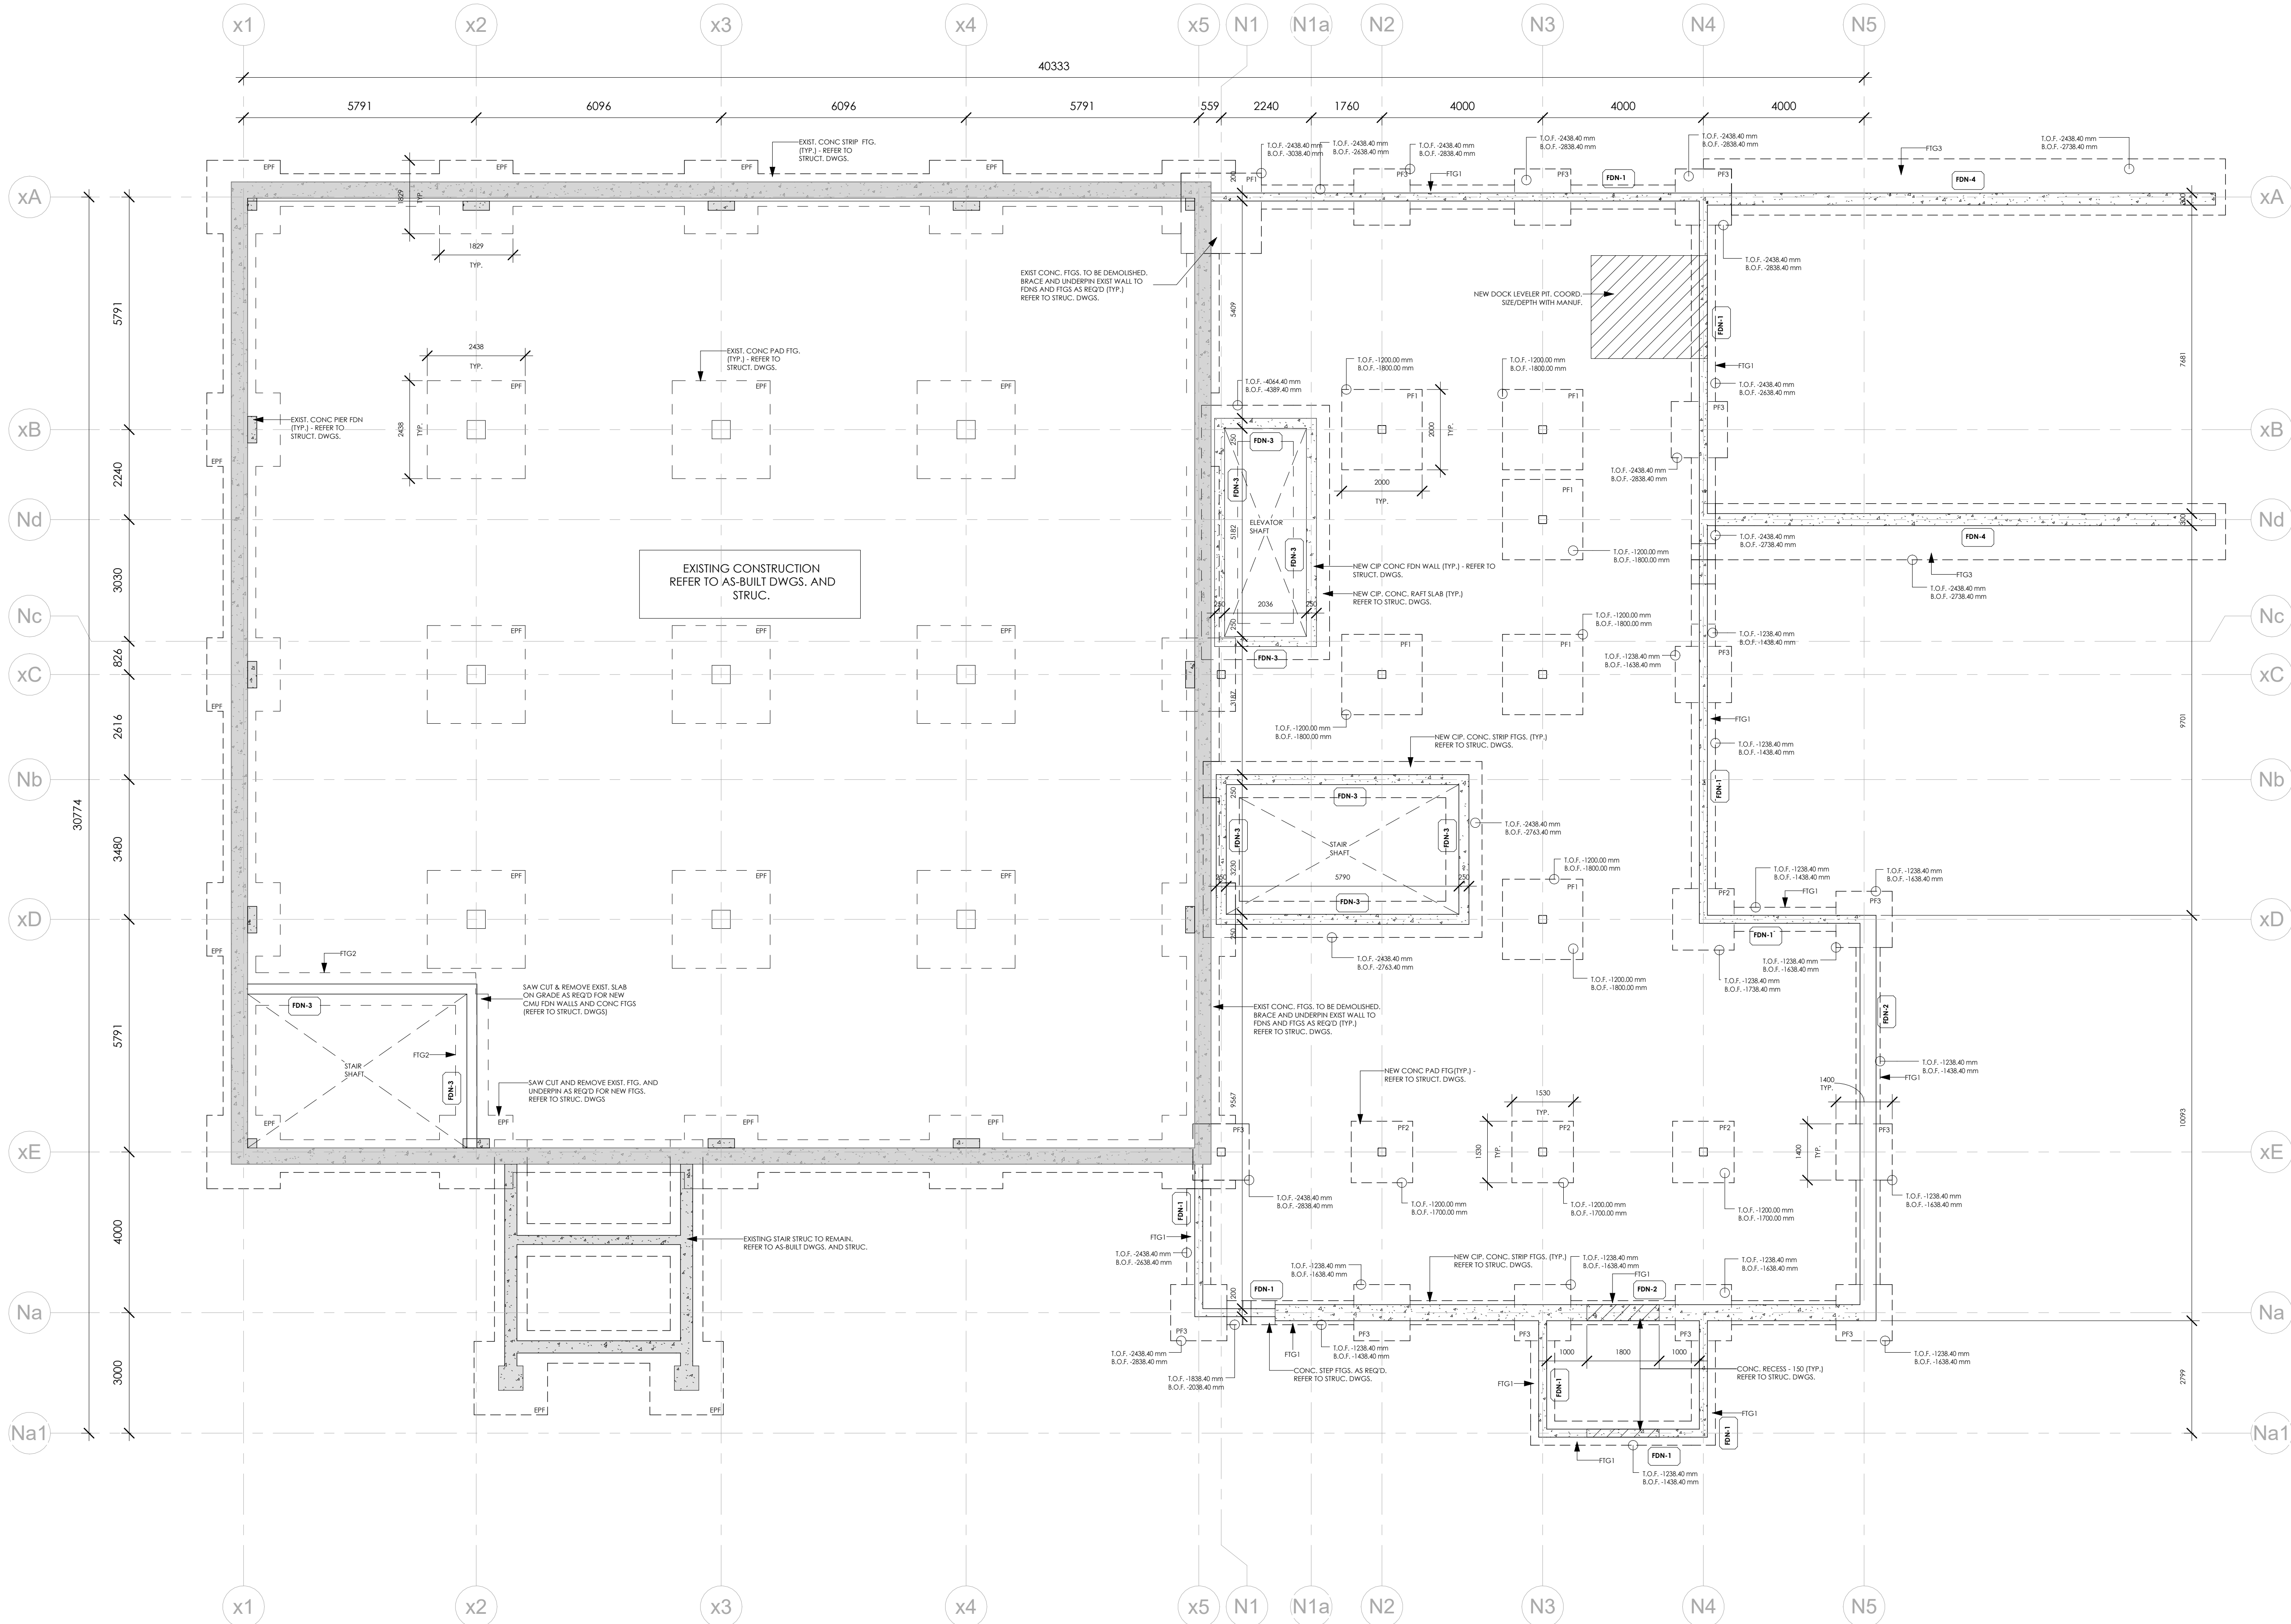


1 Foundation Plan
1 : 80

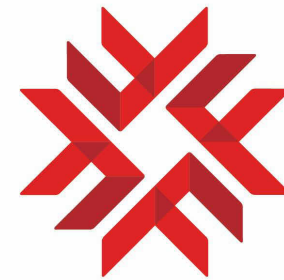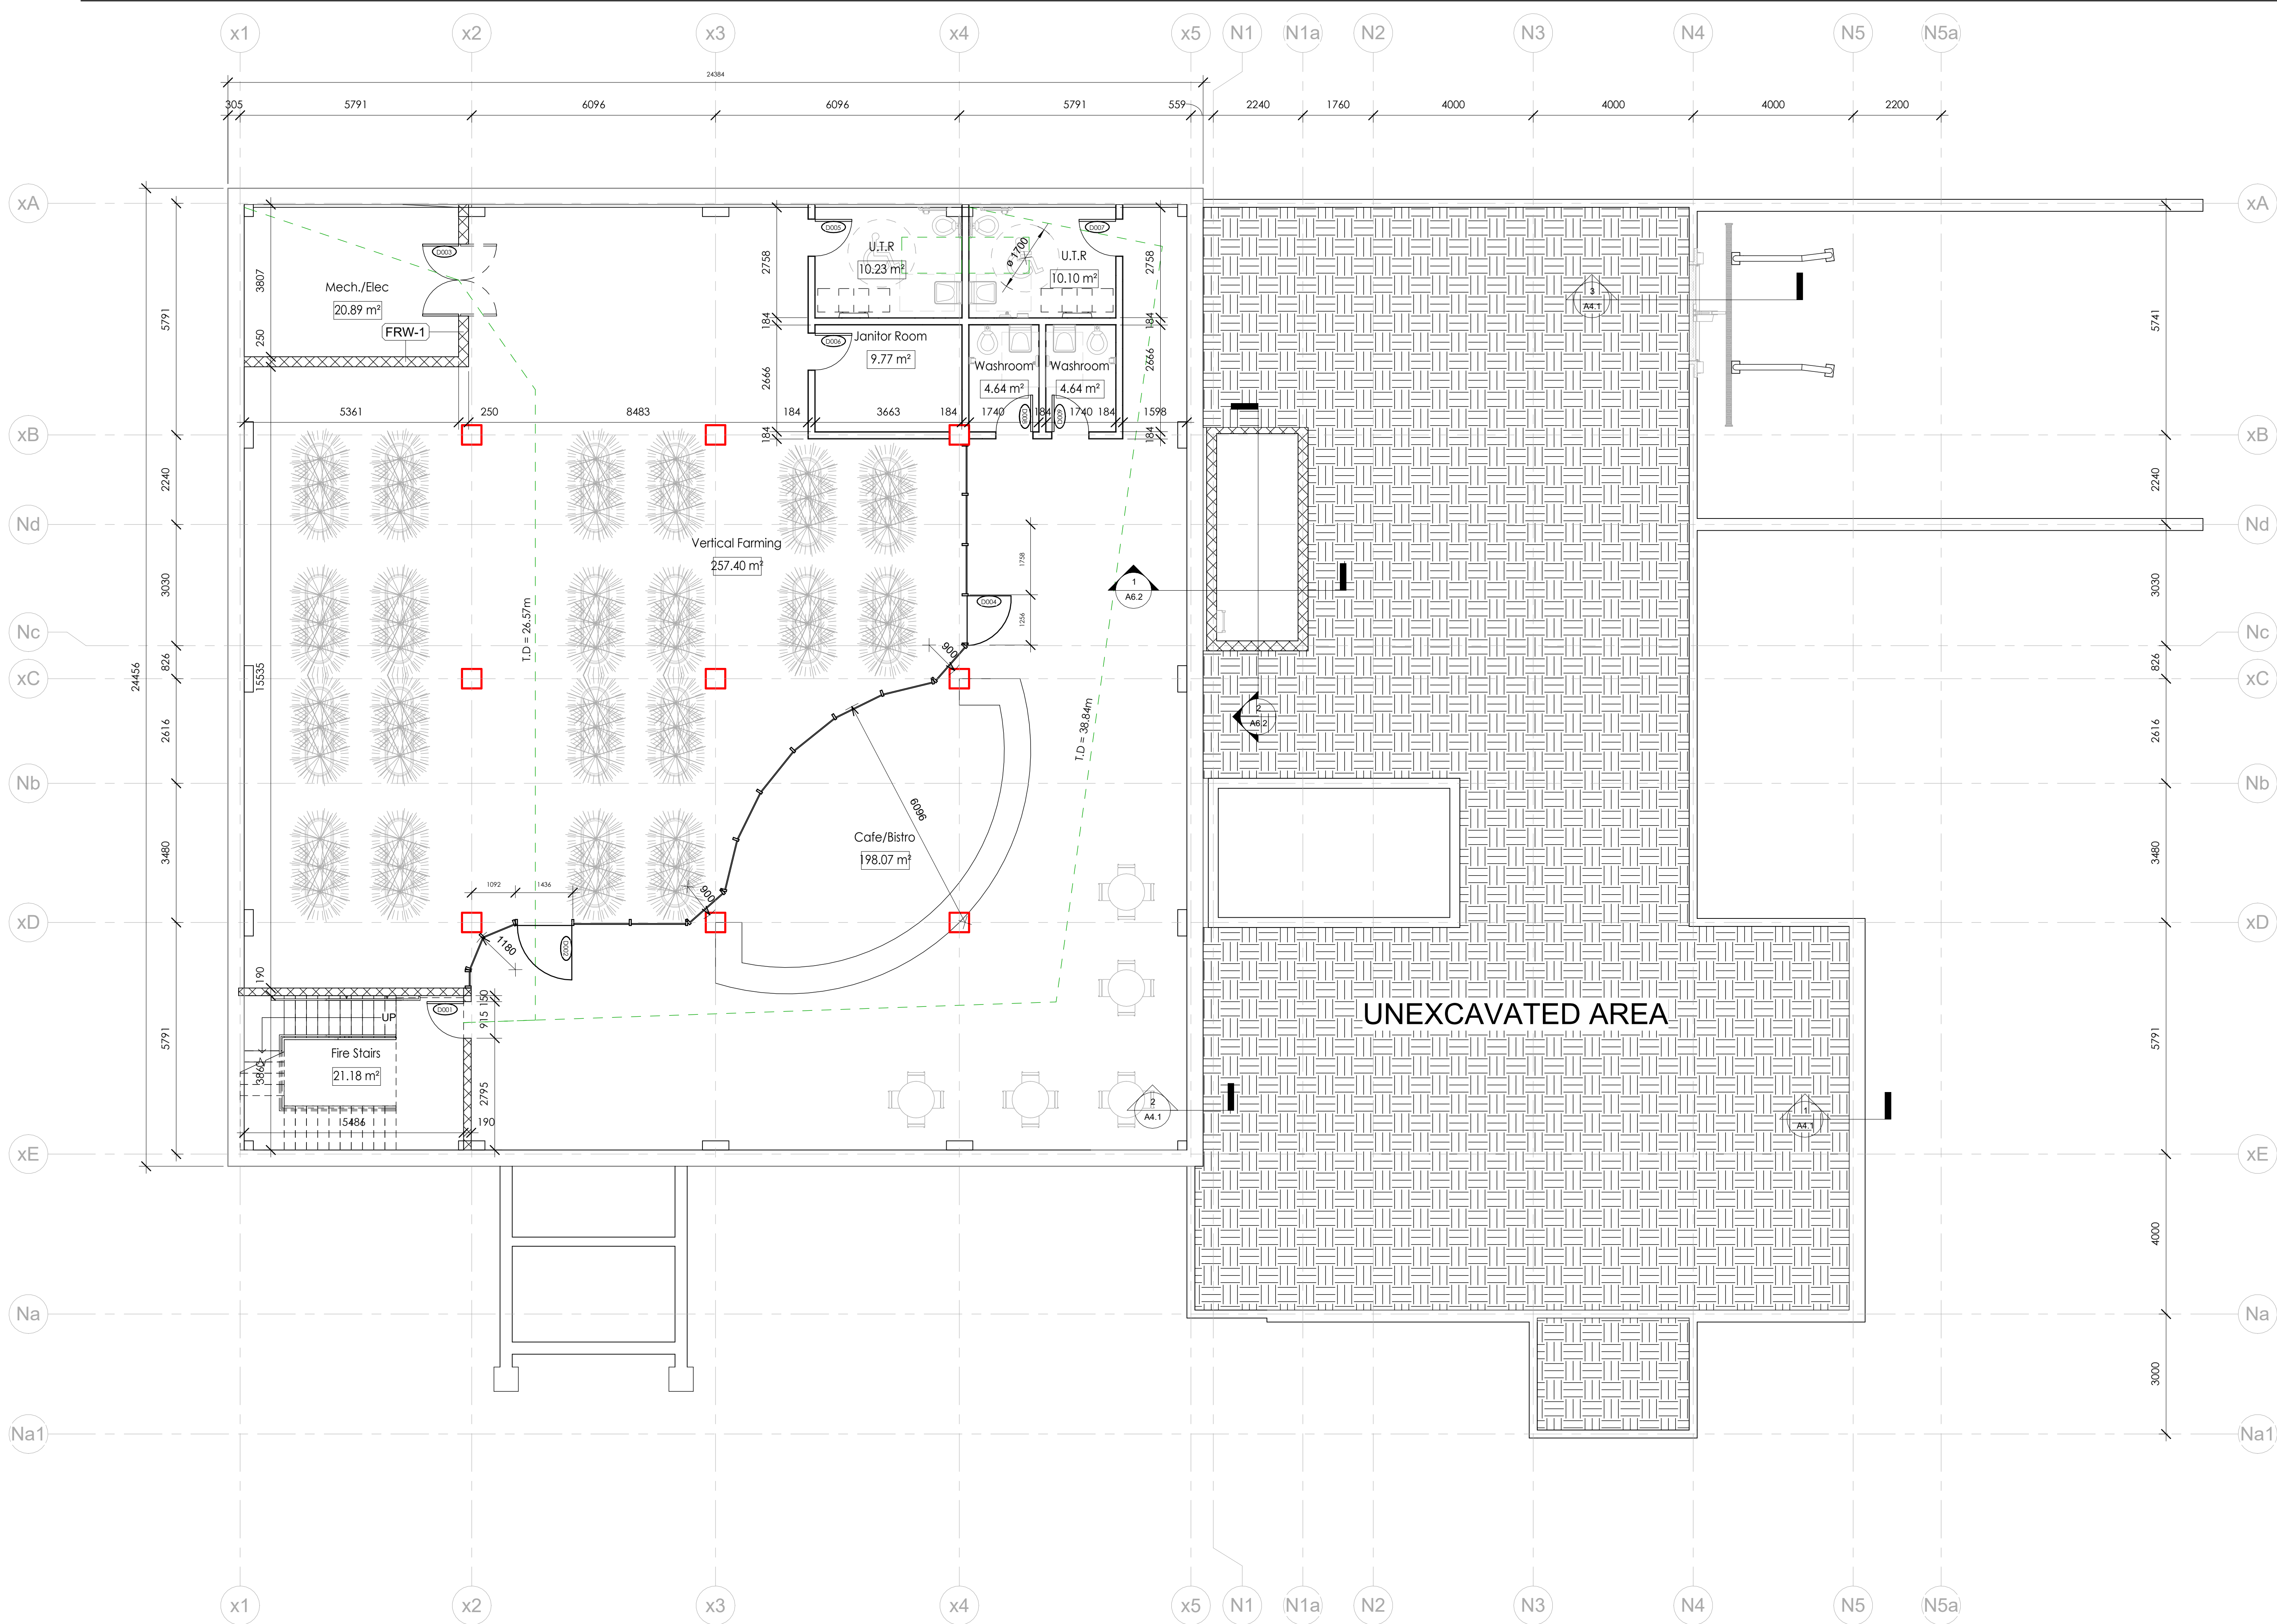

FANSHAWE
DONALD J. SMITH
SCHOOL OF BUILDING
TECHNOLOGY

NORTH ARROW

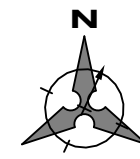

GENERAL NOTES

1. DO NOT SCALE DRAWINGS. WRITTEN DIMENSIONS SHALL HAVE PRECEDENCE OVER SCALED DIMENSIONS.
2. ALL WORK SHALL COMPLY WITH THE 2012 ONTARIO BUILDING CODE AND AMENDMENTS.
3. CONTRACTORS MUST CHECK AND VERIFY ALL DIMENSIONS AND SPECIFICATIONS AND REPORT ANY DISCREPANCIES TO THE ARCHITECT BEFORE PROCEEDING WITH THE WORK.
4. ALL CONTRACTORS AND SUB-CONTRACTORS SHALL HAVE A SET OF APPROVED CONSTRUCTION DOCUMENTS ON SITE AT ALL TIMES.
5. ALL DOCUMENTS REMAIN THE PROPERTY OF THE ARCHITECT. UNAUTHORIZED USE, MODIFICATION, AND/OR REPRODUCTION OF THESE DOCUMENTS IS PROHIBITED WITHOUT WRITTEN PERMISSION. THE CONTRACT DOCUMENTS WERE PREPARED BY THE CONSULTANT FOR THE ACCOUNT OF THE OWNER.
6. THE MATERIAL CONTAINED HEREIN REFLECTS THE CONSULTANT'S BEST JUDGMENT IN LIGHT OF THE INFORMATION AVAILABLE TO HIM/HER AT THE TIME OF PREPARATION. ANY USE WHICH A THIRD PARTY MAKES OF THE CONTRACT DOCUMENTS, OR ANY RELIANCE ON/OR DECISIONS TO BE MADE BASED ON THEM ARE THE RESPONSIBILITY OF SUCH THIRD PARTIES.
7. THE CONSULTANT ACCEPTS NO RESPONSIBILITY FOR DAMAGES, IF ANY, SUFFERED BY ANY THIRD PARTY AS A RESULT OF DECISIONS MADE OR ACTIONS BASED ON THE CONTRACT DOCUMENTS.

PRELIMINARY
NOT FOR CONSTRUCTION

PROJECT TITLE

THE EDEN PROJECT

CLIENT:

Eden Project

PROJECT ADDRESS

555 McCormick Street

DRAWING TITLE

LEVEL 0 - EXISTING BLD. PLAN

CHECKED
GG

DRAWN
AFNM

DATE
15/08/25


0001

PROJECT No.


A2.1

DRAWING

1 L000
1 : 75

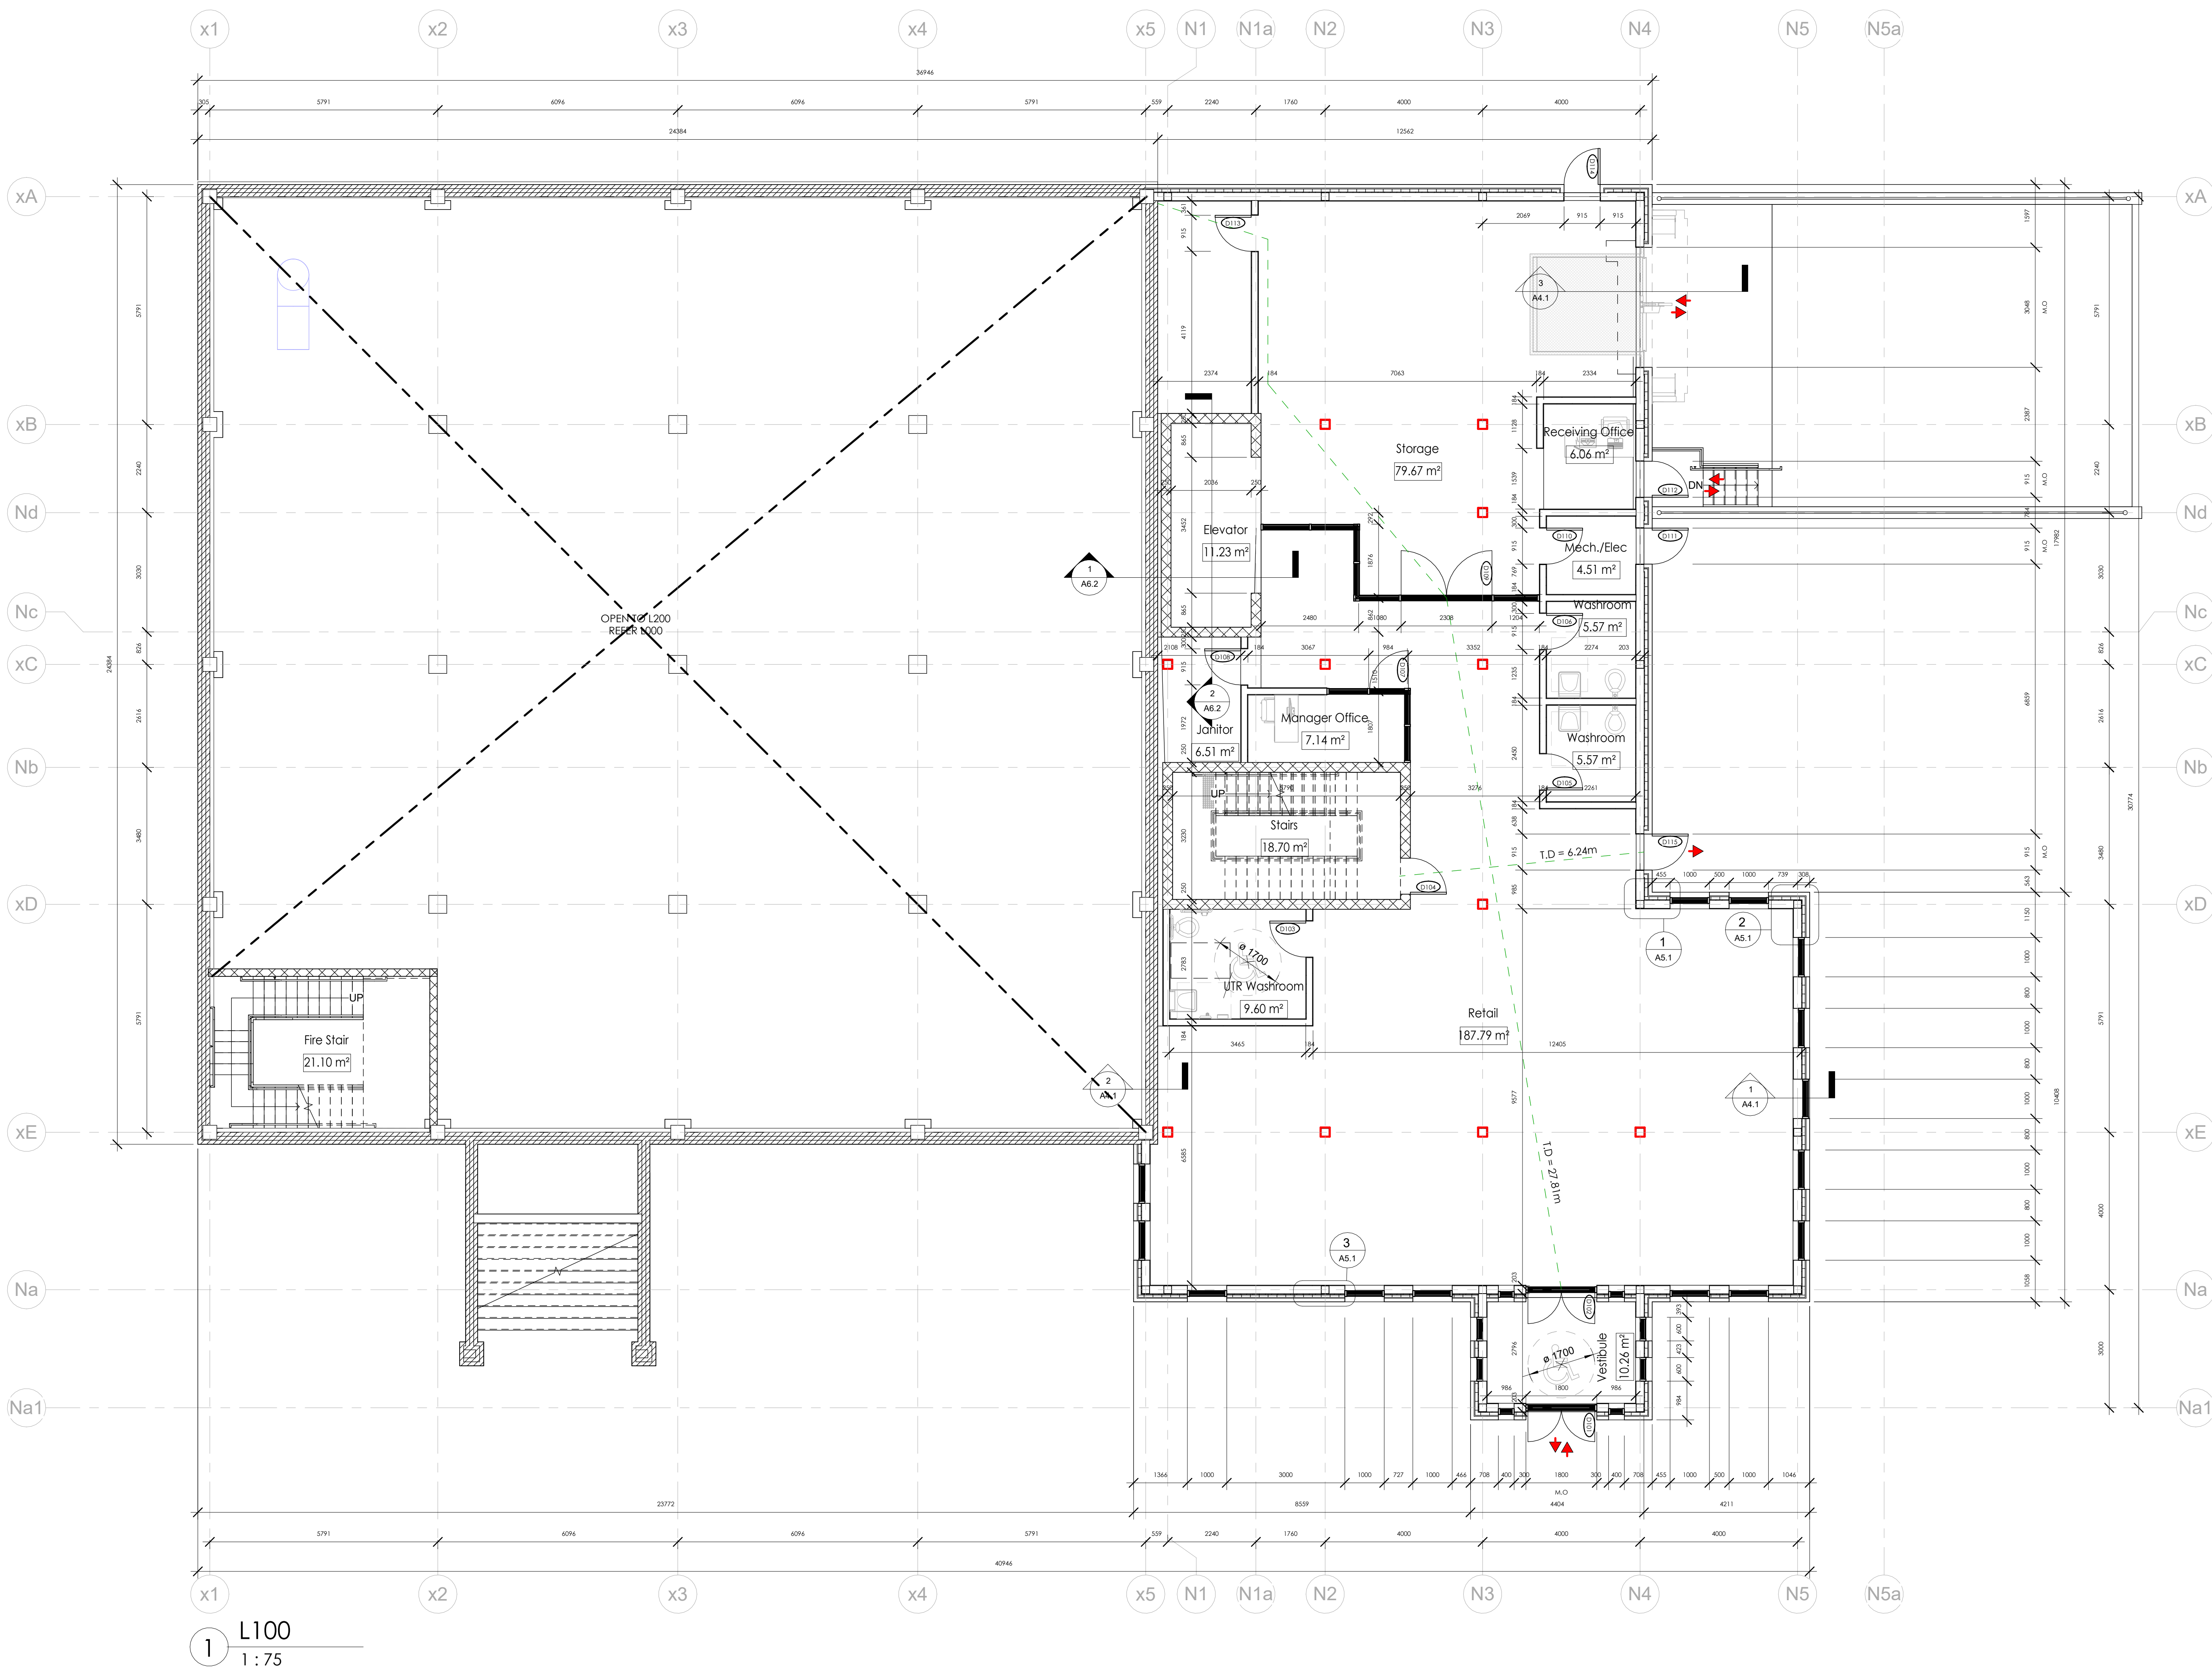

NORTH ARROW

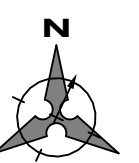

GENERAL NOTES

1. DO NOT SCALE DRAWINGS. WRITTEN DIMENSIONS SHALL HAVE PRECEDENCE OVER SCALED DIMENSIONS.
2. ALL WORK SHALL COMPLY WITH THE 2012 ONTARIO BUILDING CODE AND AMENDMENTS.
3. CONTRACTORS MUST CHECK AND VERIFY ALL DIMENSIONS AND SPECIFICATIONS AND REPORT ANY DISCREPANCIES TO THE ARCHITECT BEFORE PROCEEDING WITH THE WORK.
4. ALL CONTRACTORS AND SUB-CONTRACTORS SHALL HAVE A SET OF APPROVED CONSTRUCTION DOCUMENTS ON SITE AT ALL TIMES.
5. ALL DOCUMENTS REMAIN THE PROPERTY OF THE ARCHITECT. UNAUTHORIZED USE, MODIFICATION, AND/OR REPRODUCTION OF THESE DOCUMENTS IS PROHIBITED WITHOUT WRITTEN PERMISSION. THE CONTRACT DOCUMENTS WERE PREPARED BY THE CONSULTANT FOR THE ACCOUNT OF THE OWNER.
6. THE MATERIAL CONTAINED HEREIN REFLECTS THE CONSULTANT'S BEST JUDGMENT IN LIGHT OF THE INFORMATION AVAILABLE TO HIM/HER AT THE TIME OF PREPARATION. ANY USE WHICH A THIRD PARTY MAKES OF THE CONTRACT DOCUMENTS, OR ANY RELIANCE ON/OR DECISIONS TO BE MADE BASED ON THEM ARE THE RESPONSIBILITY OF SUCH THIRD PARTIES.
7. THE CONSULTANT ACCEPTS NO RESPONSIBILITY FOR DAMAGES, IF ANY, SUFFERED BY ANY THIRD PARTY AS A RESULT OF DECISIONS MADE OR ACTIONS BASED ON THE CONTRACT DOCUMENTS.

PRELIMINARY
NOT FOR CONSTRUCTION

PROJECT TITLE

THE EDEN PROJECT

CLIENT:

Eden Project

PROJECT ADDRESS

555 McCormick Street

DRAWING TITLE

LEVEL 1 - NEW BLD. PLAN

CHECKED
GG

DRAWN
AFNM

DATE
15/08/25

0001

PROJECT No.

A2.2

DRAWING

1 L100
1:75



NORTH ARROW



1. DO NOT SCALE DRAWINGS. WRITTEN DIMENSIONS SHALL HAVE PRECEDENCE OVER SCALED DIMENSIONS.
2. CONTRACTOR SHALL COMPLY WITH THE 2012 ONTARIO BUILDING CODE AND ALL AMENDMENTS.
3. CONTRACTORS MUST CHECK AND VERIFY ALL DIMENSIONS AND CONDITIONS OF WORK AND REPORT ANY DISCREPANCIES TO THE ARCHITECT BEFORE PROCEEDING WITH THE WORK.
4. CONTRACTOR SHALL SUB-CONTRACTORS SHALL HAVE A SET OF APPROVED CONSTRUCTION DOCUMENTS ON SITE AT ALL TIMES. ANY CHANGES TO DOCUMENTS REMAIN THE PROPERTY OF THE ARCHITECT. UNAUTHORIZED USE, MODIFICATION, AND/OR REPRODUCTION OF THESE DOCUMENTS IS PROHIBITED WITHOUT WRITTEN PERMISSION. THE CONTRACT DOCUMENTS WERE PROVIDED TO THE CONTRACTOR FOR THE ACCOUNT OF THE OWNER.
6. THE MATERIAL CONTAINED HEREIN REFLECTS THE INFORMATION THAT THE CONTRACTOR HAS AVAILABLE AT THE TIME OF PREPARATION. ANY DISCREPANCIES OR OMISSIONS, OR ANY RELIANCE ON OR DECISIONS TO BE MADE BASED ON THEM ARE THE SOLE RESPONSIBILITY OF SUCH THIRD PARTIES.
7. THE CONSULTANT ACCEPTS NO RESPONSIBILITY FOR ANY SUCH DISCREPANCIES OR OMISSIONS BY ANY THIRD PARTY AS A RESULT OF DECISIONS MADE OR ACTIONS BASED ON THE CONTRACT DOCUMENTS.

**PRELIMINARY
NOT FOR CONSTRUCTION**

PROJECT TITLE

THE EDEN PROJECT

CLIENT:

Eden Project

PROJECT ADDRESS

555 McCormick Street

DRAWING TITLE

LEVEL 2 - EXISTING BLD. PLAN

CHECKED	DRAWN
GG	AFNM


DATE
15/08/25

0001


A2.3

PROJECT No.


DRAWING

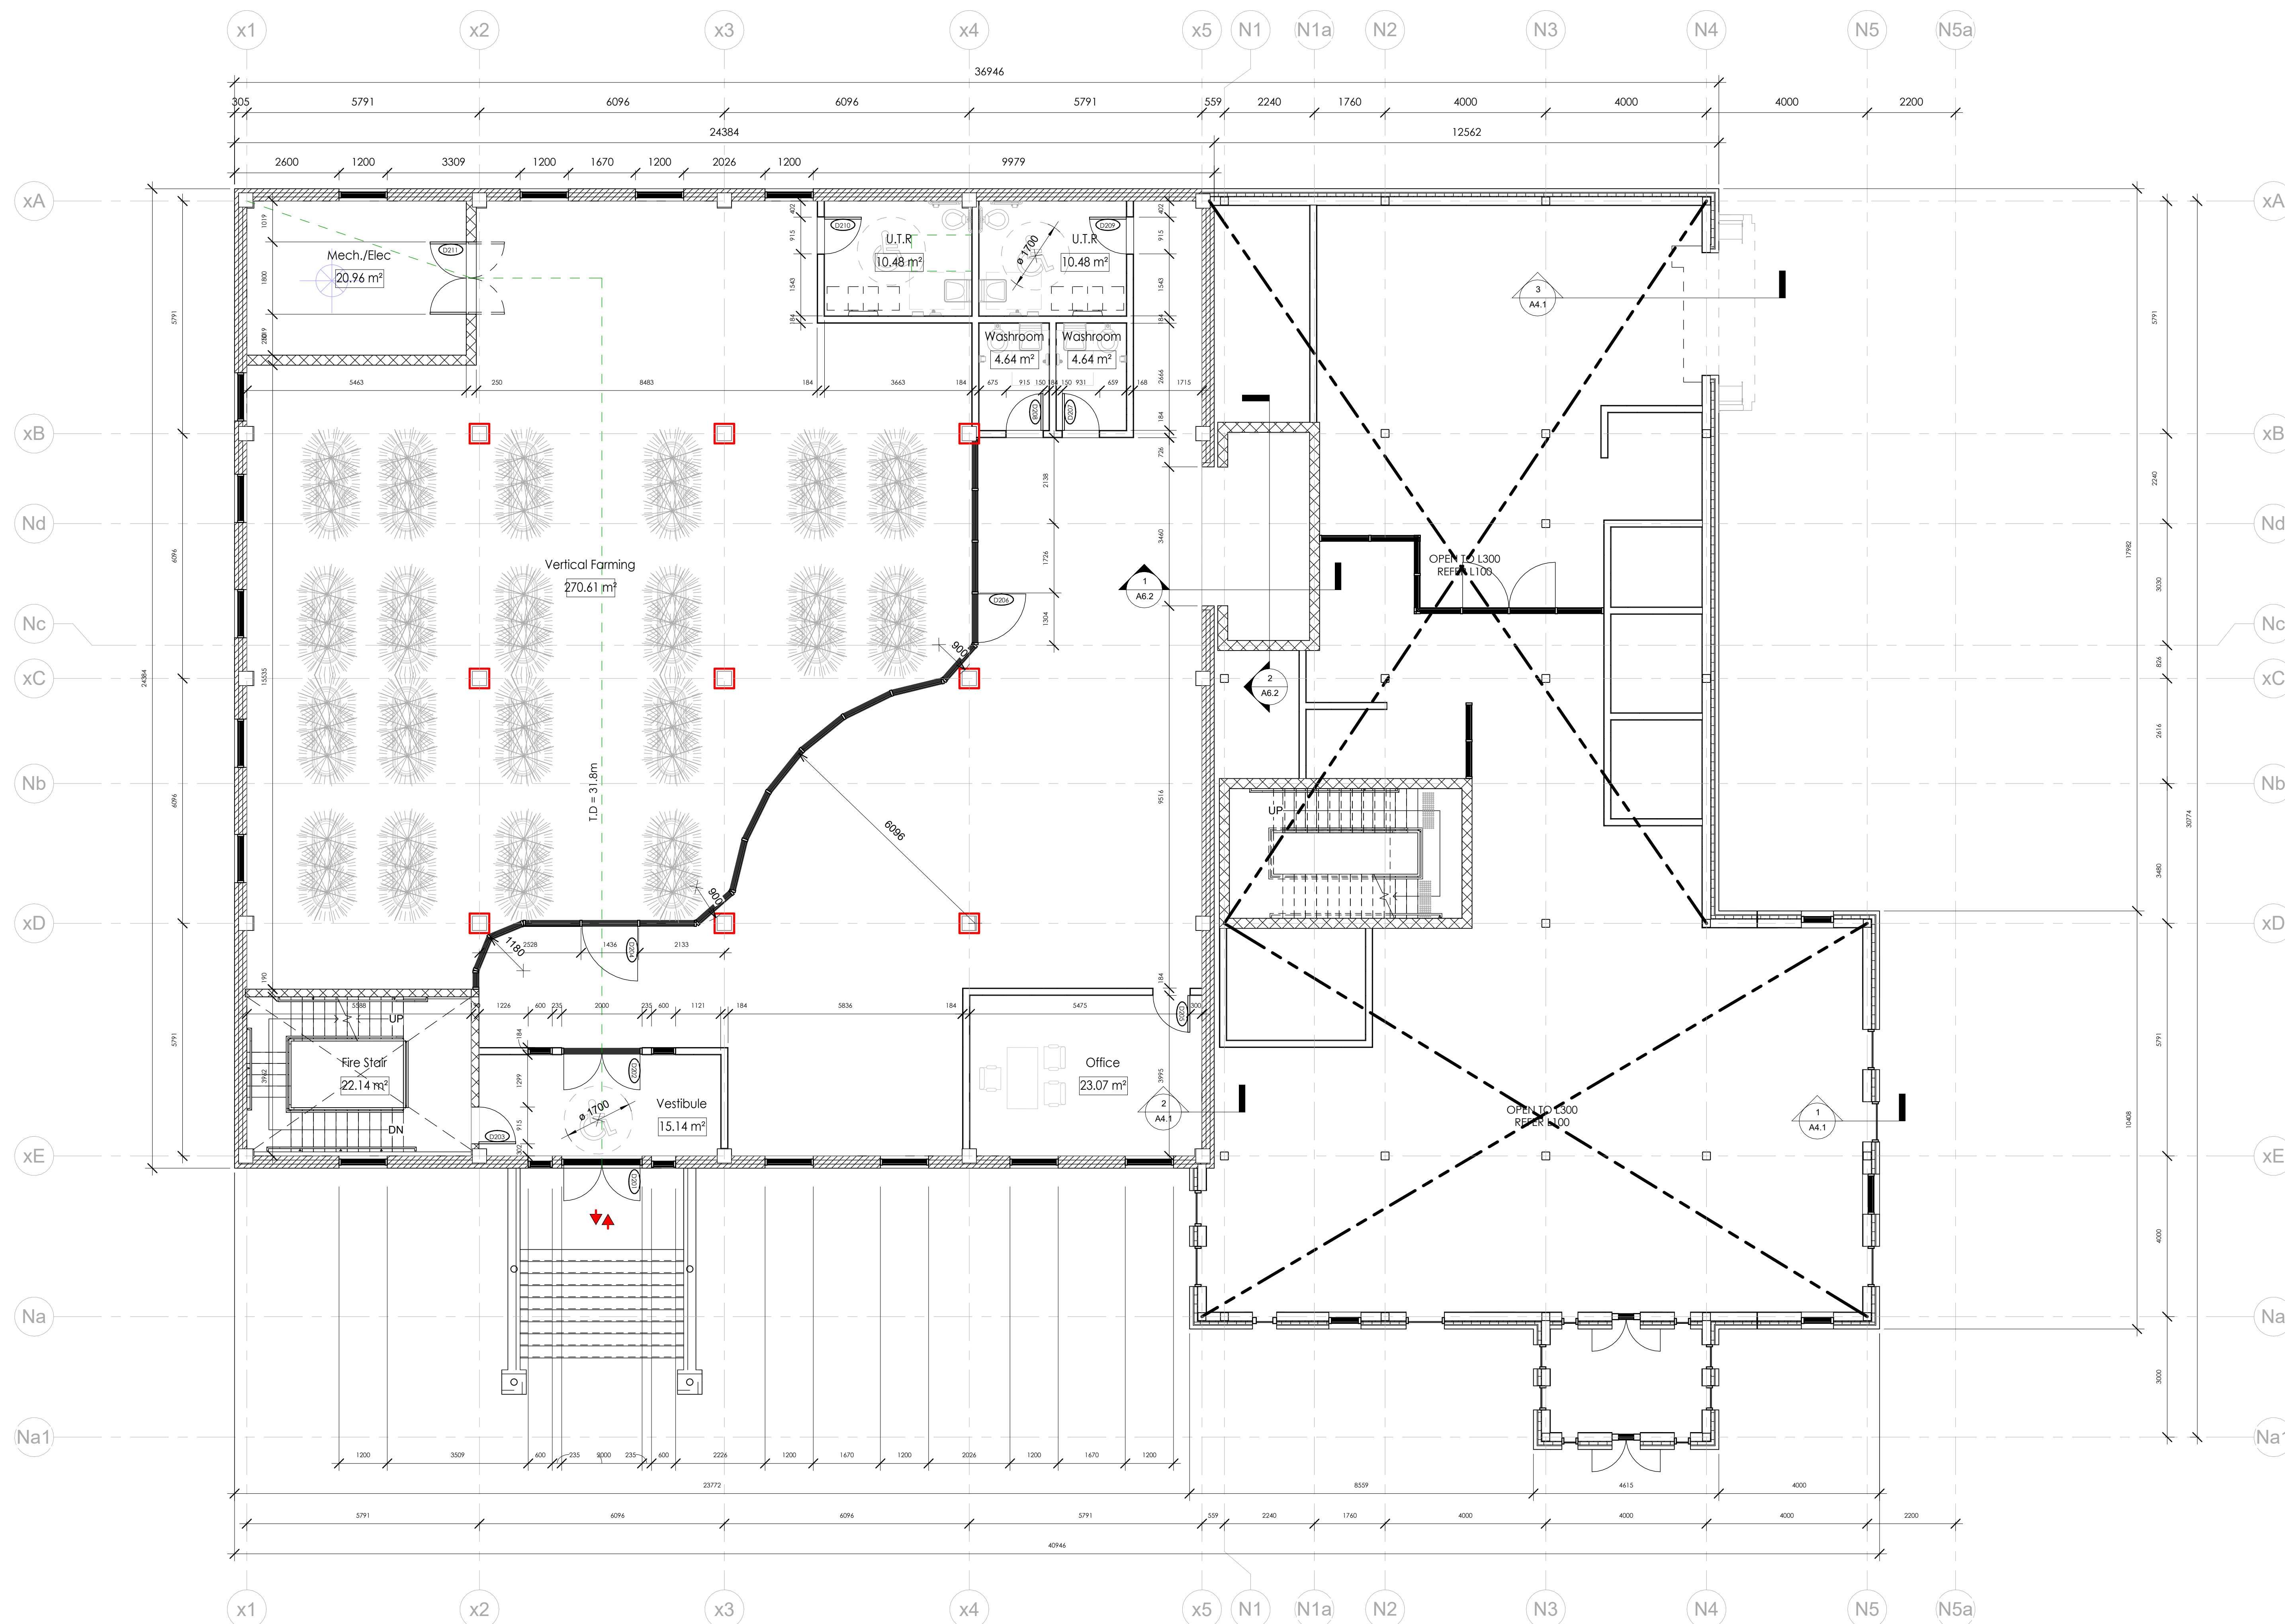

① L200
1 : 75

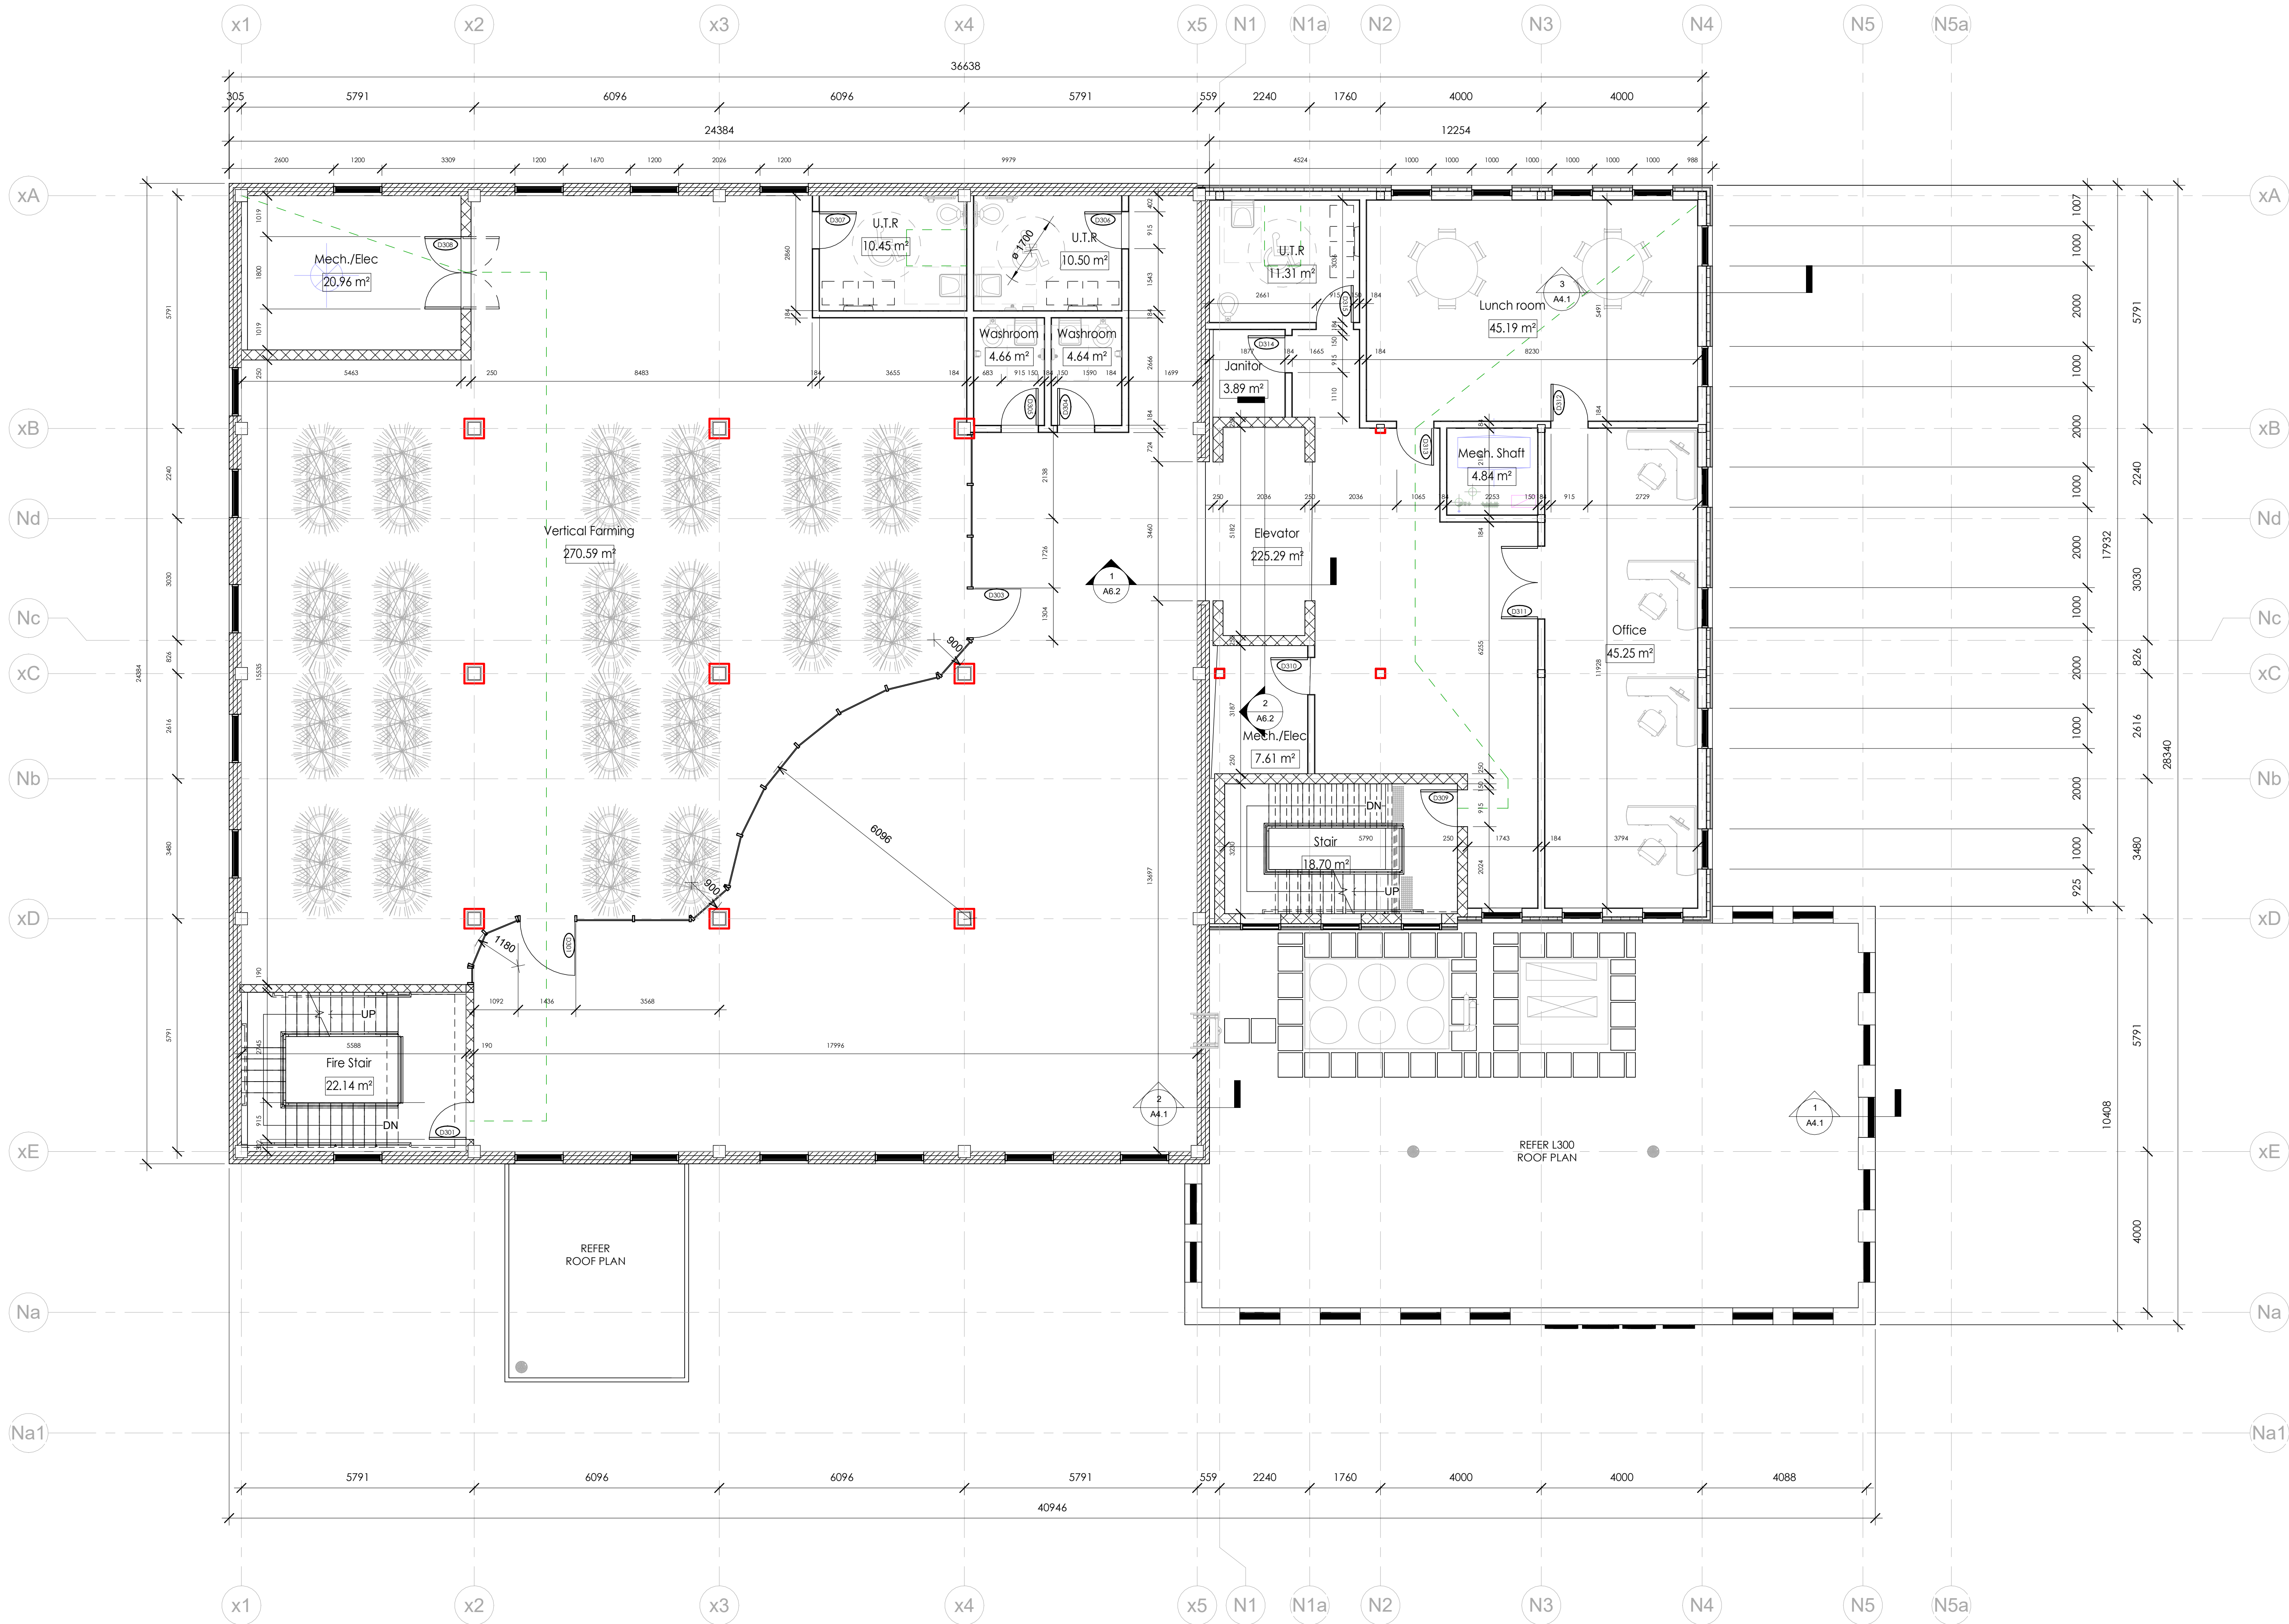

NORTH ARROW

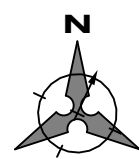

GENERAL NOTES

1. DO NOT SCALE DRAWINGS. WRITTEN DIMENSIONS SHALL HAVE PRECEDENCE OVER SCALED DIMENSIONS.
2. ALL WORK SHALL COMPLY WITH THE 2012 ONTARIO BUILDING CODE AND AMENDMENTS.
3. CONTRACTORS MUST CHECK AND VERIFY ALL DIMENSIONS AND SPECIFICATIONS AND REPORT ANY DISCREPANCIES TO THE ARCHITECT BEFORE PROCEEDING WITH THE WORK.
4. ALL CONTRACTORS AND SUB-CONTRACTORS SHALL HAVE A SET OF APPROVED CONSTRUCTION DOCUMENTS ON SITE AT ALL TIMES.
5. ALL DOCUMENTS REMAIN THE PROPERTY OF THE ARCHITECT. UNAUTHORIZED USE, MODIFICATION, AND/OR REPRODUCTION OF THESE DOCUMENTS IS PROHIBITED WITHOUT WRITTEN PERMISSION. THE CONTRACT DOCUMENTS WERE PREPARED BY THE CONSULTANT FOR THE ACCOUNT OF THE OWNER.
6. THE MATERIAL CONTAINED HEREIN REFLECTS THE CONSULTANT'S BEST JUDGMENT IN LIGHT OF THE INFORMATION AVAILABLE TO HIM/HER AT THE TIME OF PREPARATION. ANY USE WHICH A THIRD PARTY MAKES OF THE CONTRACT DOCUMENTS, OR ANY RELIANCE ON/OR DECISIONS TO BE MADE BASED ON THEM ARE THE RESPONSIBILITY OF SUCH THIRD PARTIES.
7. THE CONSULTANT ACCEPTS NO RESPONSIBILITY FOR DAMAGES, IF ANY, SUFFERED BY ANY THIRD PARTY AS A RESULT OF DECISIONS MADE OR ACTIONS BASED ON THE CONTRACT DOCUMENTS.

PRELIMINARY
NOT FOR CONSTRUCTION

PROJECT TITLE
THE EDEN PROJECT


CLIENT:
Eden Project
PROJECT ADDRESS:
555 McCormick Street

DRAWING TITLE
LEVEL 3 - NEW & EXISTING BLD. PLAN


CHECKED: GG
DRAWN: AFNM
DATE: 15/08/25

0001
PROJECT No.
A2.4
DRAWING

1 L300
1:75

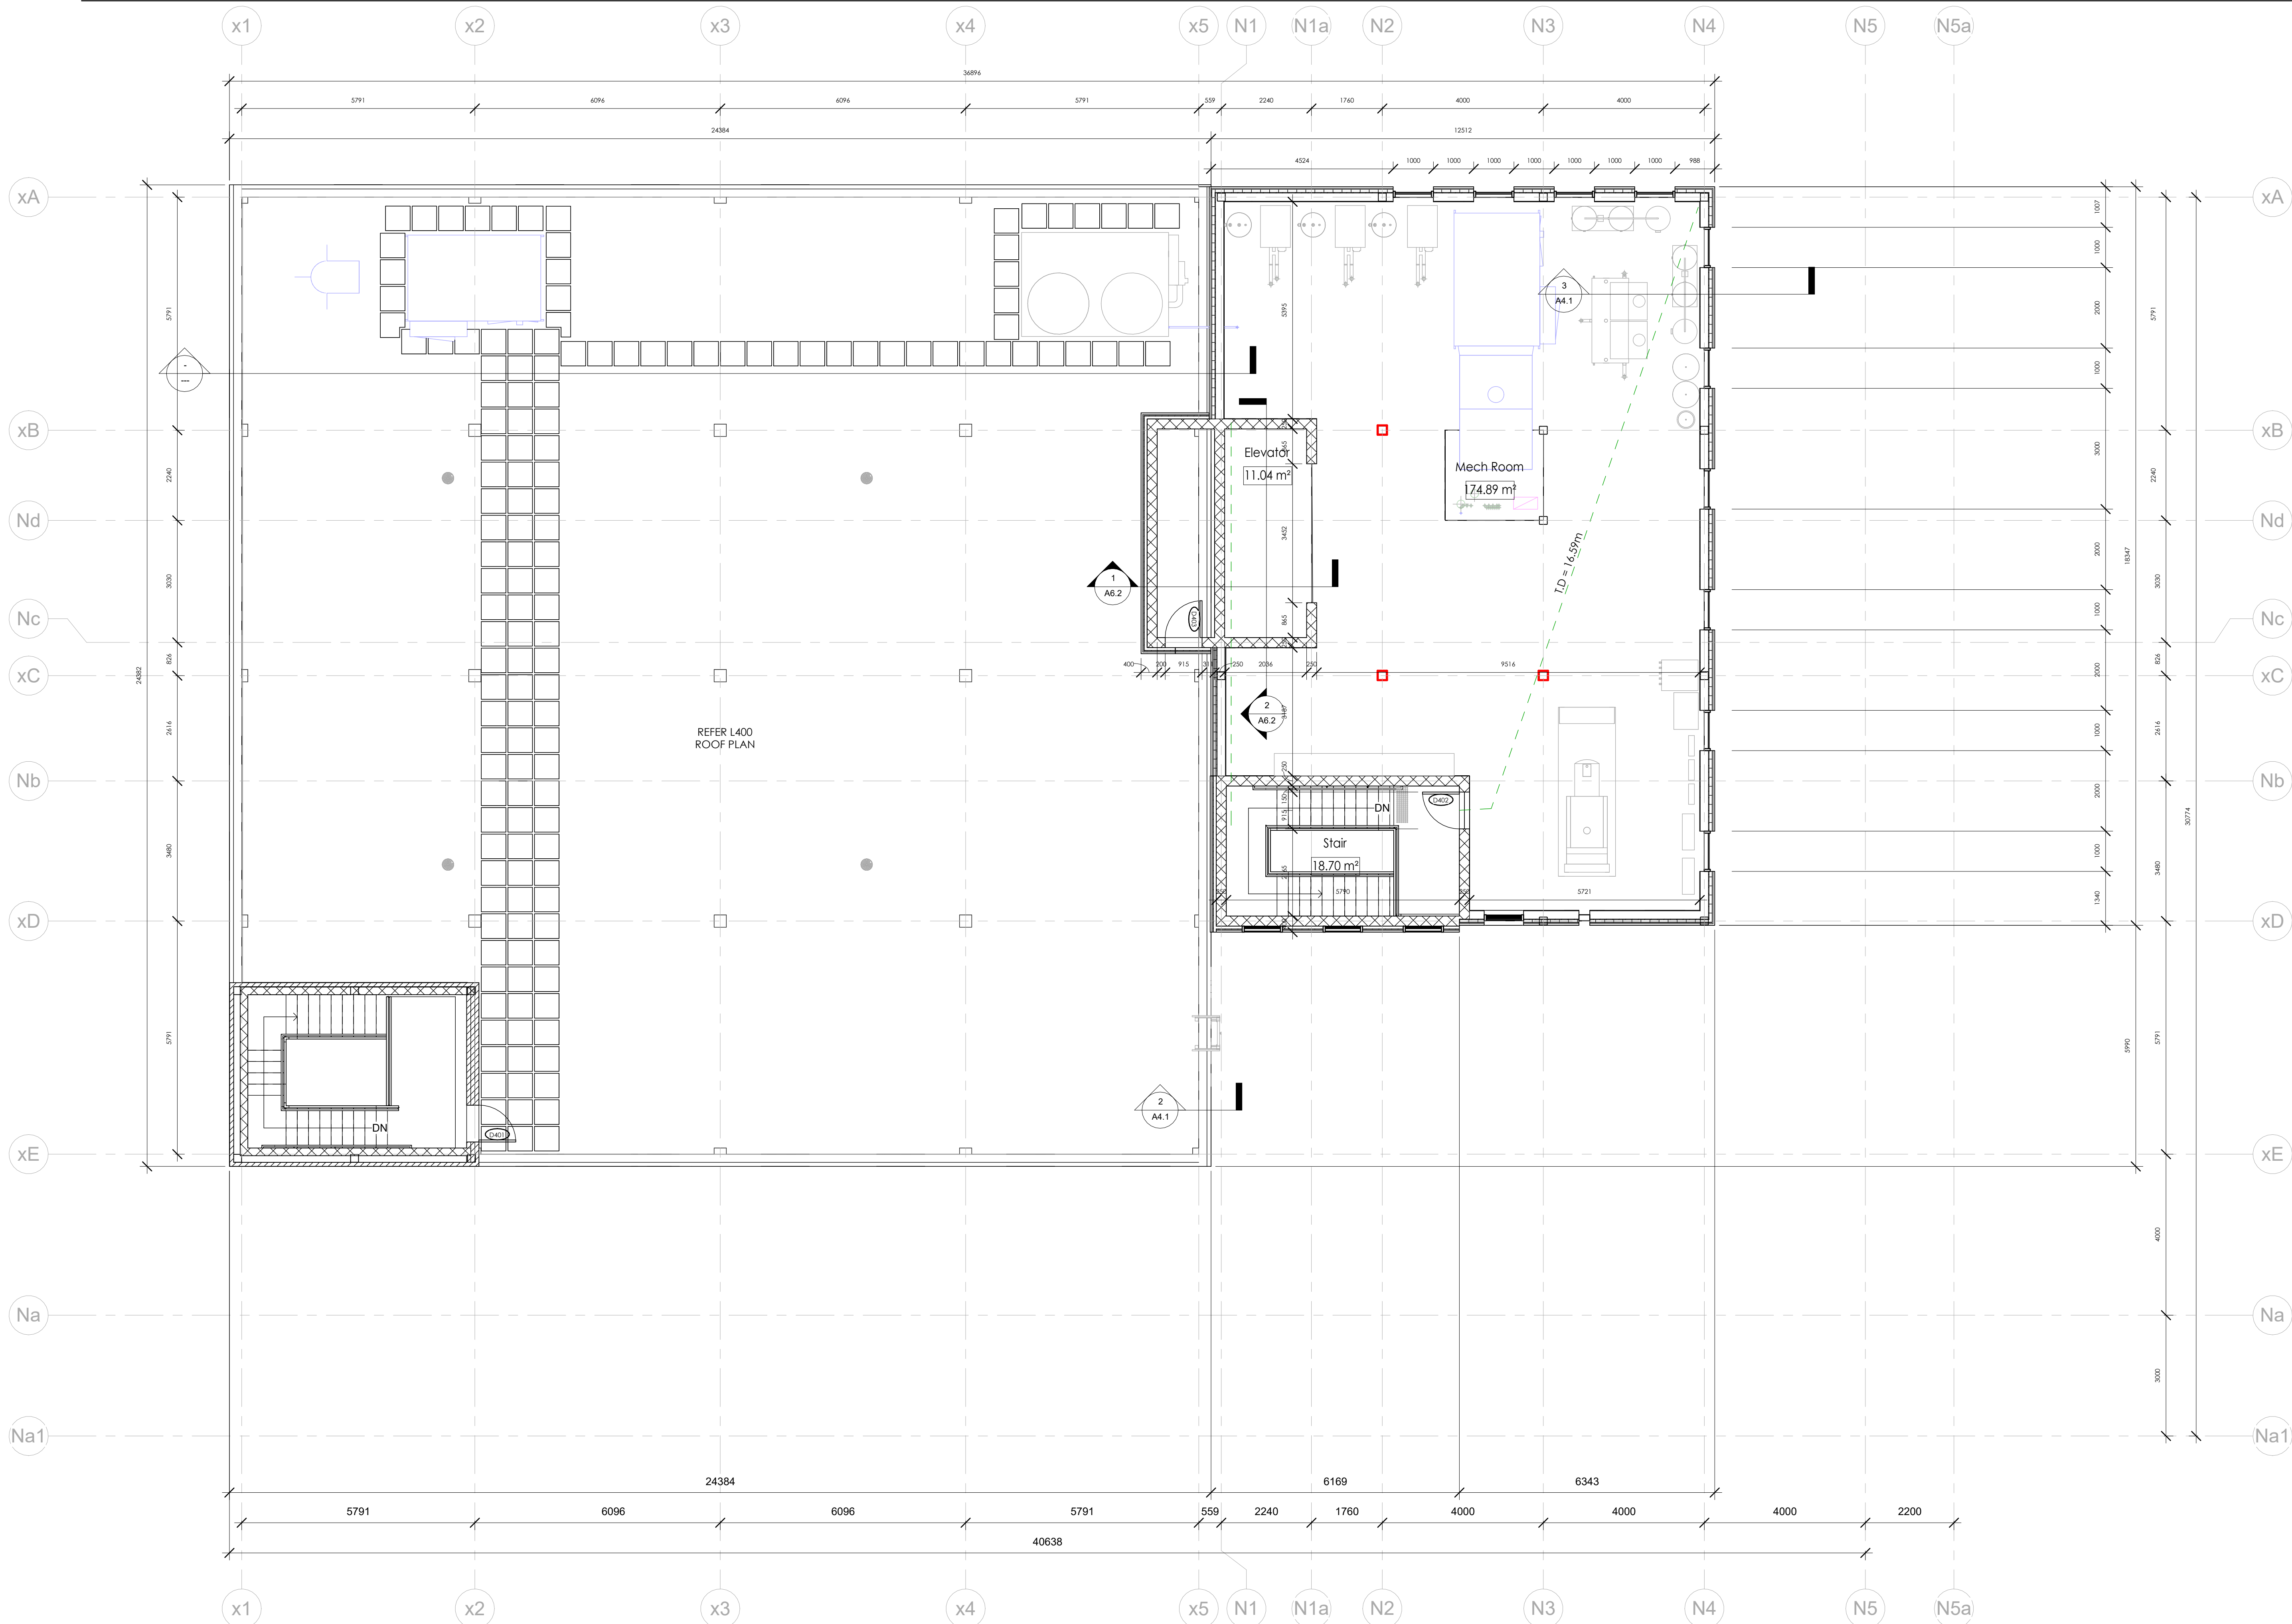


1 L400
1 : 75

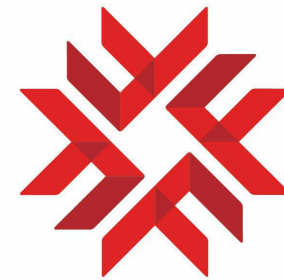

FANSHAW
DONALD J. SMITH
SCHOOL OF BUILDING
TECHNOLOGY

NORTH ARROW

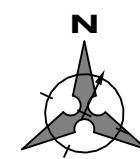

GENERAL NOTES

1. DO NOT SCALE DRAWINGS. WRITTEN DIMENSIONS SHALL HAVE PRECEDENCE OVER SCALED DIMENSIONS.
2. ALL WORK SHALL COMPLY WITH THE 2012 ONTARIO BUILDING CODE AND AMENDMENTS.
3. CONTRACTORS MUST CHECK AND VERIFY ALL DIMENSIONS AND SPECIFICATIONS AND REPORT ANY DISCREPANCIES TO THE ARCHITECT BEFORE PROCEEDING WITH THE WORK.
4. ALL CONTRACTORS AND SUB-CONTRACTORS SHALL HAVE A SET OF APPROVED CONSTRUCTION DOCUMENTS ON SITE AT ALL TIMES.
5. ALL DOCUMENTS REMAIN THE PROPERTY OF THE ARCHITECT. UNAUTHORIZED USE, MODIFICATION, AND/OR REPRODUCTION OF THESE DOCUMENTS IS PROHIBITED WITHOUT WRITTEN PERMISSION. THE CONTRACT DOCUMENTS WERE PREPARED BY THE CONSULTANT FOR THE ACCOUNT OF THE OWNER.
6. THE MATERIAL CONTAINED HEREIN REFLECTS THE CONSULTANT'S BEST JUDGMENT IN LIGHT OF THE INFORMATION AVAILABLE TO HIM/HER AT THE TIME OF PREPARATION. ANY USE WHICH A THIRD PARTY MAKES OF THE CONTRACT DOCUMENTS, OR ANY RELIANCE ON/OR DECISIONS TO BE MADE BASED ON THEM ARE THE RESPONSIBILITY OF SUCH THIRD PARTIES.
7. THE CONSULTANT ACCEPTS NO RESPONSIBILITY FOR DAMAGES, IF ANY, SUFFERED BY ANY THIRD PARTY AS A RESULT OF DECISIONS MADE OR ACTIONS BASED ON THE CONTRACT DOCUMENTS.

PRELIMINARY
NOT FOR CONSTRUCTION


PROJECT TITLE
THE EDEN PROJECT

CLIENT:
Eden Project
PROJECT ADDRESS
555 McCormick Street

DRAWING TITLE
LEVEL 4 - NEW & EXISTING BLD. PLAN


CHECKED
GG
DRAWN
AFNM
DATE
15/08/25

0001
PROJECT No.
A2.5
DRAWING

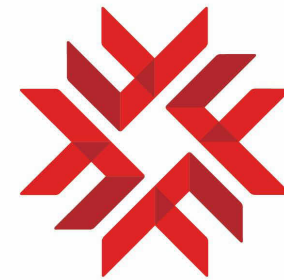

FANSHAWE
DONALD J. SMITH
SCHOOL OF BUILDING
TECHNOLOGY

NORTH ARROW

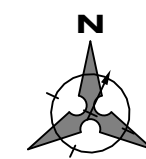

GENERAL NOTES

1. DO NOT SCALE DRAWINGS. WRITTEN DIMENSIONS SHALL HAVE PRECEDENCE OVER SCALED DIMENSIONS.
2. ALL WORK SHALL COMPLY WITH THE 2012 ONTARIO BUILDING CODE AND AMENDMENTS.
3. CONTRACTORS MUST CHECK AND VERIFY ALL DIMENSIONS AND SPECIFICATIONS AND REPORT ANY DISCREPANCIES TO THE ARCHITECT BEFORE PROCEEDING WITH THE WORK.
4. ALL CONTRACTORS AND SUB-CONTRACTORS SHALL HAVE A SET OF APPROVED CONSTRUCTION DOCUMENTS ON SITE AT ALL TIMES.
5. ALL DOCUMENTS REMAIN THE PROPERTY OF THE ARCHITECT. UNAUTHORIZED USE, MODIFICATION, AND/OR REPRODUCTION OF THESE DOCUMENTS IS PROHIBITED WITHOUT WRITTEN PERMISSION. THE CONTRACT DOCUMENTS WERE PREPARED BY THE CONSULTANT FOR THE ACCOUNT OF THE OWNER.
6. THE MATERIAL CONTAINED HEREIN REFLECTS THE CONSULTANT'S BEST JUDGMENT IN LIGHT OF THE INFORMATION AVAILABLE TO HIM/HER AT THE TIME OF PREPARATION. ANY USE WHICH A THIRD PARTY MAKES OF THE CONTRACT DOCUMENTS, OR ANY RELIANCE ON/OR DECISIONS TO BE MADE BASED ON THEM ARE THE RESPONSIBILITY OF SUCH THIRD PARTIES.
7. THE CONSULTANT ACCEPTS NO RESPONSIBILITY FOR DAMAGES, IF ANY, SUFFERED BY ANY THIRD PARTY AS A RESULT OF DECISIONS MADE OR ACTIONS BASED ON THE CONTRACT DOCUMENTS.

PRELIMINARY
NOT FOR CONSTRUCTION

PROJECT TITLE
THE EDEN PROJECT

CLIENT:
Eden Project
PROJECT ADDRESS
555 McCormick Street

DRAWING TITLE
NORTH AND SOUTH ELEVATION

CHECKED
GG

DRAWN
AFNM

DATE
15/08/25

0001
PROJECT No.

A3.1
DRAWING



NORTH ARROW



GENERAL NOTES

1. DO NOT SCALE DRAWINGS. WRITTEN DIMENSIONS SHALL HAVE PRECEDENCE OVER SCALED DIMENSIONS.
2. ALL WORK SHALL COMPLY WITH THE 2012 ONTARIO BUILDING CODE AND AMENDMENTS.
3. CONTRACTORS MUST CHECK AND VERIFY ALL DIMENSIONS AND SPECIFICATIONS AND REPORT ANY DISCREPANCIES TO THE ARCHITECT BEFORE PROCEEDING WITH THE WORK.
4. ALL CONTRACTORS AND SUB-CONTRACTORS SHALL HAVE A SET OF APPROVED CONSTRUCTION DOCUMENTS ON SITE AT ALL TIMES.
5. ALL DOCUMENTS REMAIN THE PROPERTY OF THE ARCHITECT. UNAUTHORIZED USE, MODIFICATION, AND/OR REPRODUCTION OF THESE DOCUMENTS IS PROHIBITED WITHOUT WRITTEN PERMISSION. THE CONTRACT DOCUMENTS WERE PREPARED BY THE CONSULTANT FOR THE ACCOUNT OF THE OWNER.
6. THE MATERIAL CONTAINED HEREIN REFLECTS THE CONSULTANTS BEST JUDGMENT IN LIGHT OF THE INFORMATION AVAILABLE TO HIM/HER AT THE TIME OF PREPARATION. ANY USE WHICH A THIRD PARTY MAKES OF THE CONTRACT DOCUMENTS, OR ANY RELIANCE ON/OR DECISIONS TO BE MADE BASED ON THEM ARE THE RESPONSIBILITY OF SUCH THIRD PARTIES.
7. THE CONSULTANT ACCEPTS NO RESPONSIBILITY FOR DAMAGES, IF ANY, SUFFERED BY ANY THIRD PARTY AS A RESULT OF DECISIONS MADE OR ACTIONS BASED ON THE CONTRACT DOCUMENTS.

GENERAL ELEVATION NOTES

1. THE APPROVED BUILDING ELEVATIONS SHALL FORM THE BASIS FOR THE BUILDING PERMIT APPLICATION.
2. ALL SITE LIGHTING SHALL NOT RESULT IN ANY GLARE OR SPILL OVER TO SURROUNDING PROPERTIES OR PUBLIC VIEW.
3. ALL ROOFTOP MECHANICAL EQUIPMENT SHALL BE FULLY SCREENED FROM PUBLIC VIEW AND SURROUNDING RESIDENTIAL PROPERTIES.
4. BUILDING COLOURS MAY BE SUBJECT TO MINOR ADJUSTMENTS IN TONE AND/OR SHADE.
5. ANY PROPOSED SIGNAGE IS FOR ILLUSTRATION PURPOSE(S), AND SUBJECT TO THE GOVERNING AUTHORITY SIGN BY-LAW.

MATERIAL TAG LEGEND & NOTES

01	EXISTING RED COMMON BRICK WALL (TYP.) TO REMAIN.
02	SIDING PANELS WOOD VERTICAL WHITE (TYP.) BY GOODFELLOW INC.
03	HOJROD BRICK STRETCHER (TYP.) BY BRAMPTON BRICK
04	EXISTING CONCRETE STAIR (TYP.)
05	DOOR CURTAIN WALL DOUBLE - SEE DOOR SCHEDULE (TYP.)
06	WINDOW WALL C/W TINTED GLASS - SEE WINDOW SCHEDULE (TYP.) BY KAWNEER
07	WINDOW WALL C/W SPANDREL PANELS - SEE WINDOW SCHEDULE (TYP.) BY KAWNEER
08	ILLUMINATED BACKLIT STOREFRONT SIGNAGE REFER TO SIGN SHOP DWGS.
09	SINGLE FLUSH DOOR - SEE DOOR SCHEDULE (TYP.) BY JD DOORS INC.
10	SCREEN BRICK MODULAR (TYP.) BY BRAMPTON BRICK
11	LOADING DOCK OVERHEAD DOOR - SEE DOOR SCHEDULE (TYP.) BY JD DOORS INC.
12	CAST-IN-PLACE CONCRETE FOUNDATION / RETAINING WALL - REFER TO STRUCT.
13	EXIST. CONCRETE FOUNDATION / RETAINING WALL
14	CIP CONC STRIP / PAD FOOTINGS - REFER TO STRUCT.
15	EXIST. CIP CONC STRIP / PAD FOOTINGS
16	EXIST. CIP PIER FOUNDATIONS
17	HOLLOW METAL DOORSEE DOOR SCHEDULE (TYP.) BY JD DOORS INC.
18	LOADING DOCK RAILING REFER TO SHOP DWGS. BY SERCO DOCK PRODUCTS
19	LOADING DOCK SHELTER REFER TO SHOP DWGS. BY SERCO DOCK PRODUCTS
20	ROOF ACCESS LADDER AS PER MOL GUIDELINES - SUPPLIED BY OWNER
21	GALVANIZED STEEL PIPE RAILING REFER TO SHOP DWGS.
22	LOADING DOCK LEVELER REFER TO SHOP DWGS. BY SERCO DOCK PRODUCTS

PROJECT TITLE

THE EDEN PROJECT

CLIENT:

Eden Project

PROJECT ADDRESS

555 McCormick Street

DRAWING TITLE

EAST AND WEST ELEVATION

CHECKED
GG

DRAWN
AFNM

DATE
15/08/25


0001

PROJECT No.


A3.2

DRAWING


PRELIMINARY
NOT FOR CONSTRUCTION

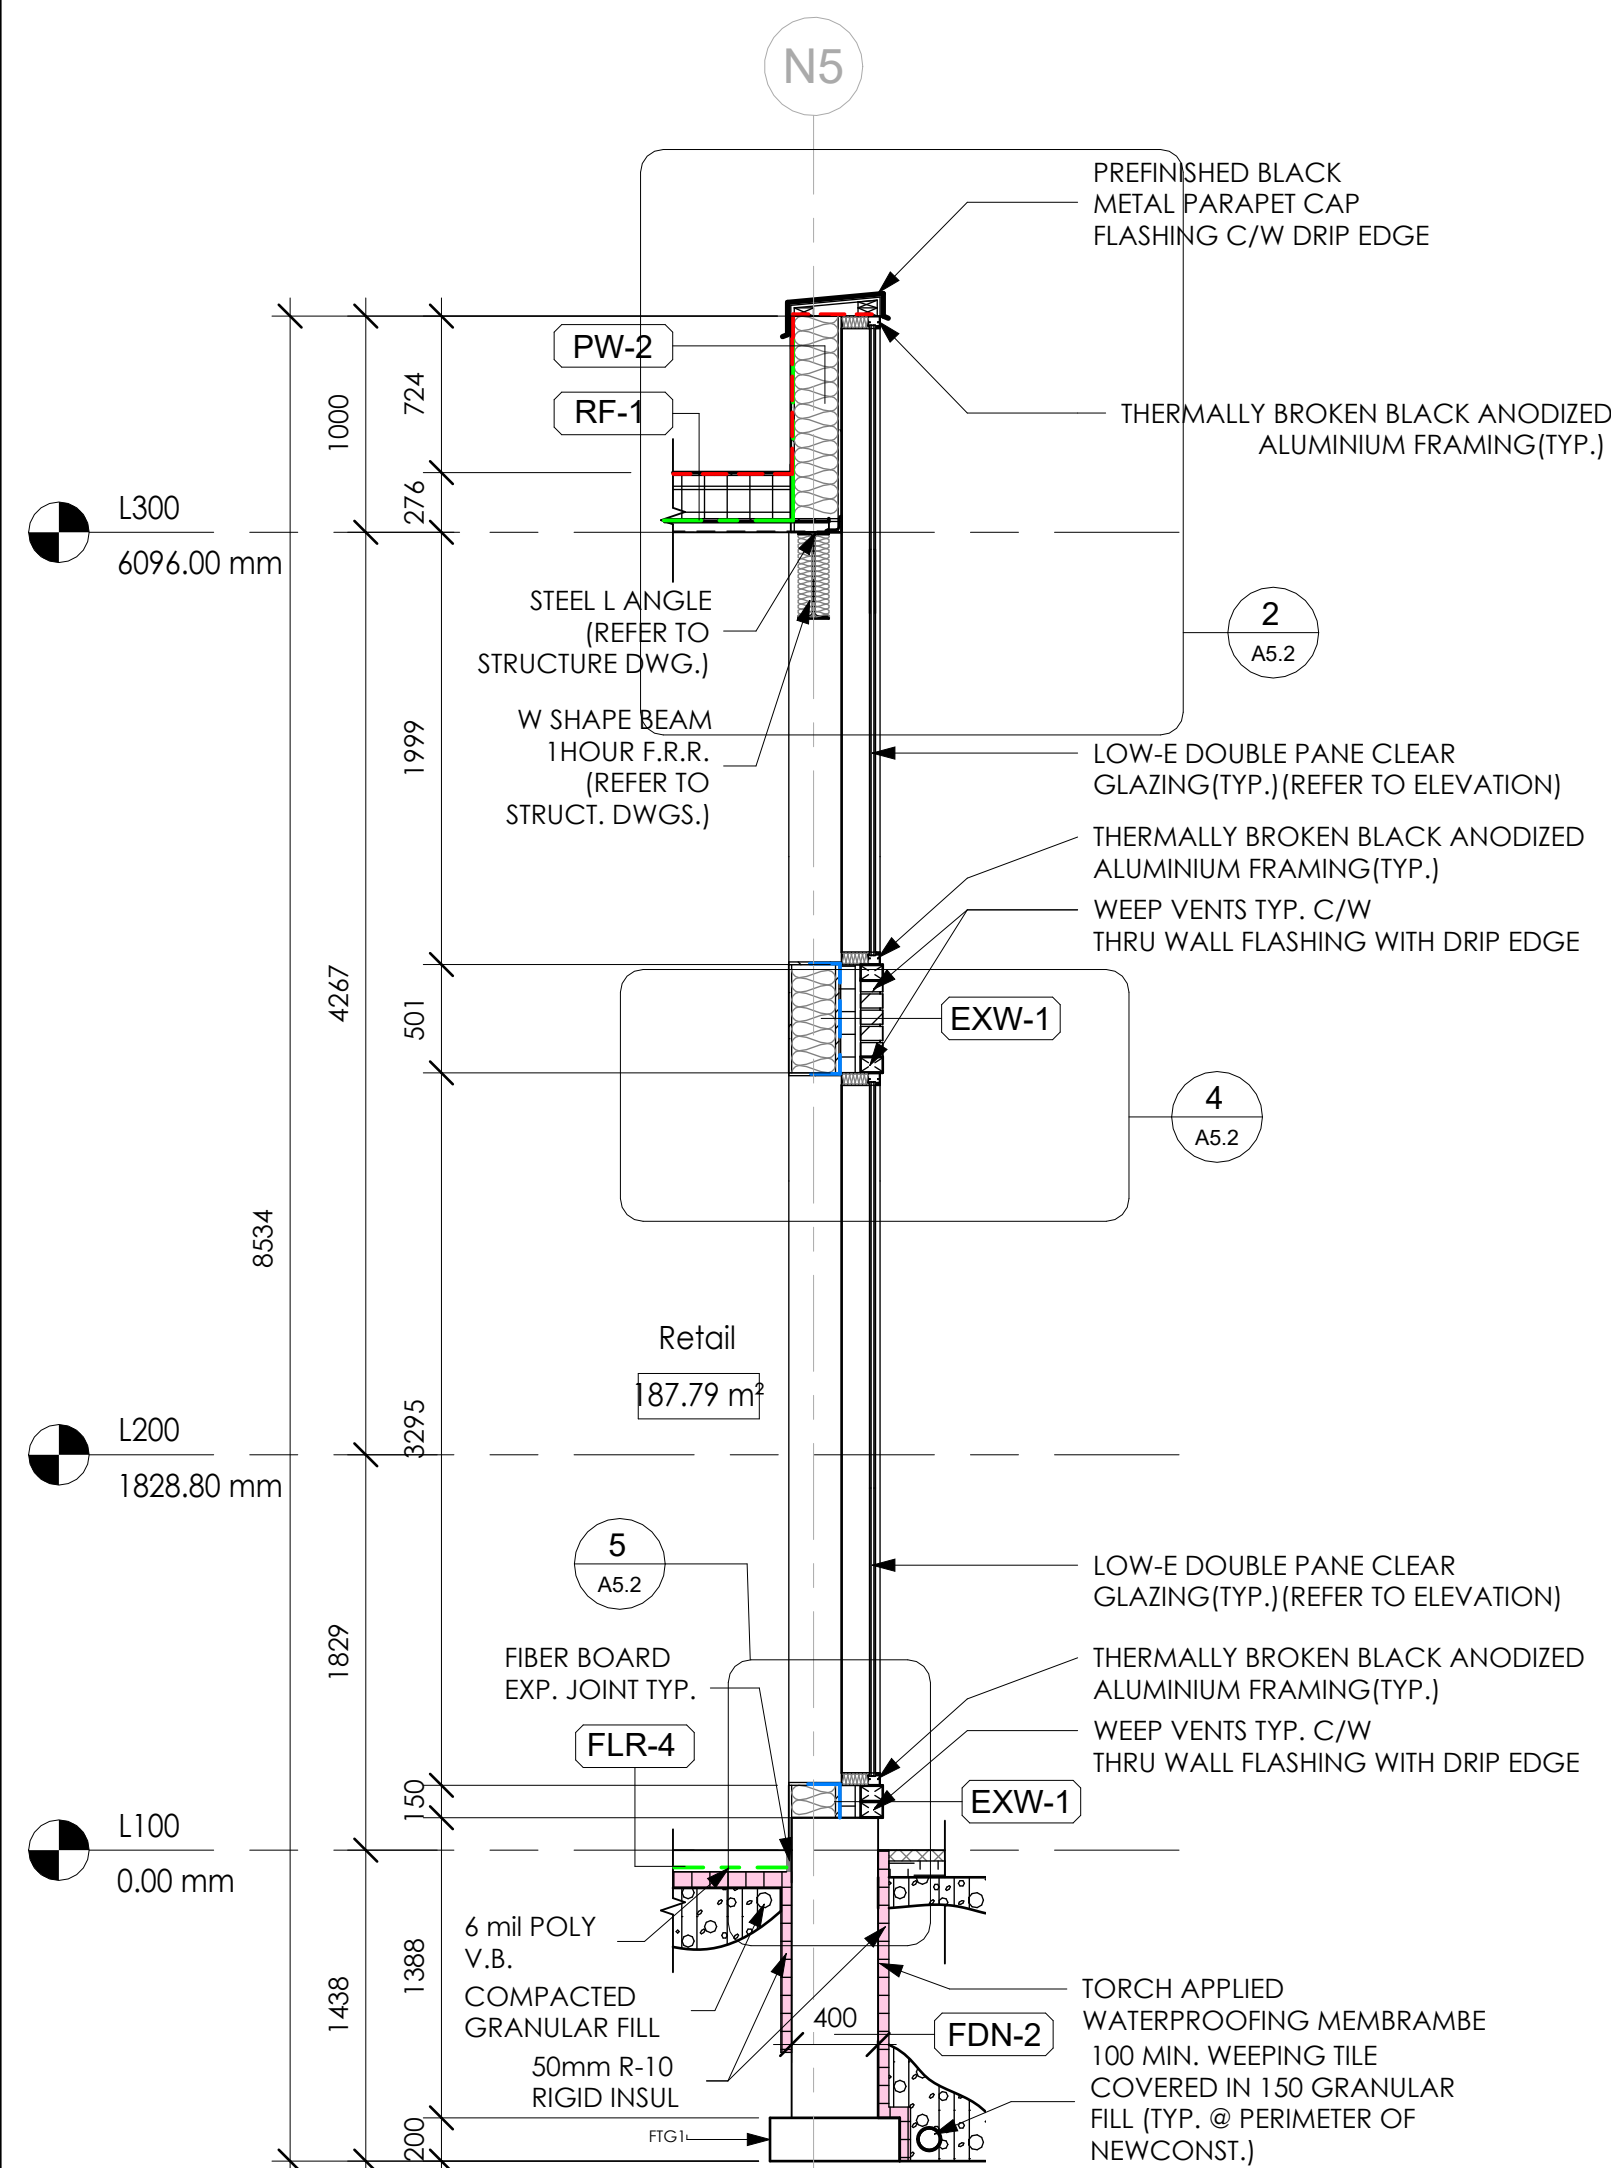


1 TYPICAL WALL ASSEMBLY @ GLAZED OPENING
1 : 35

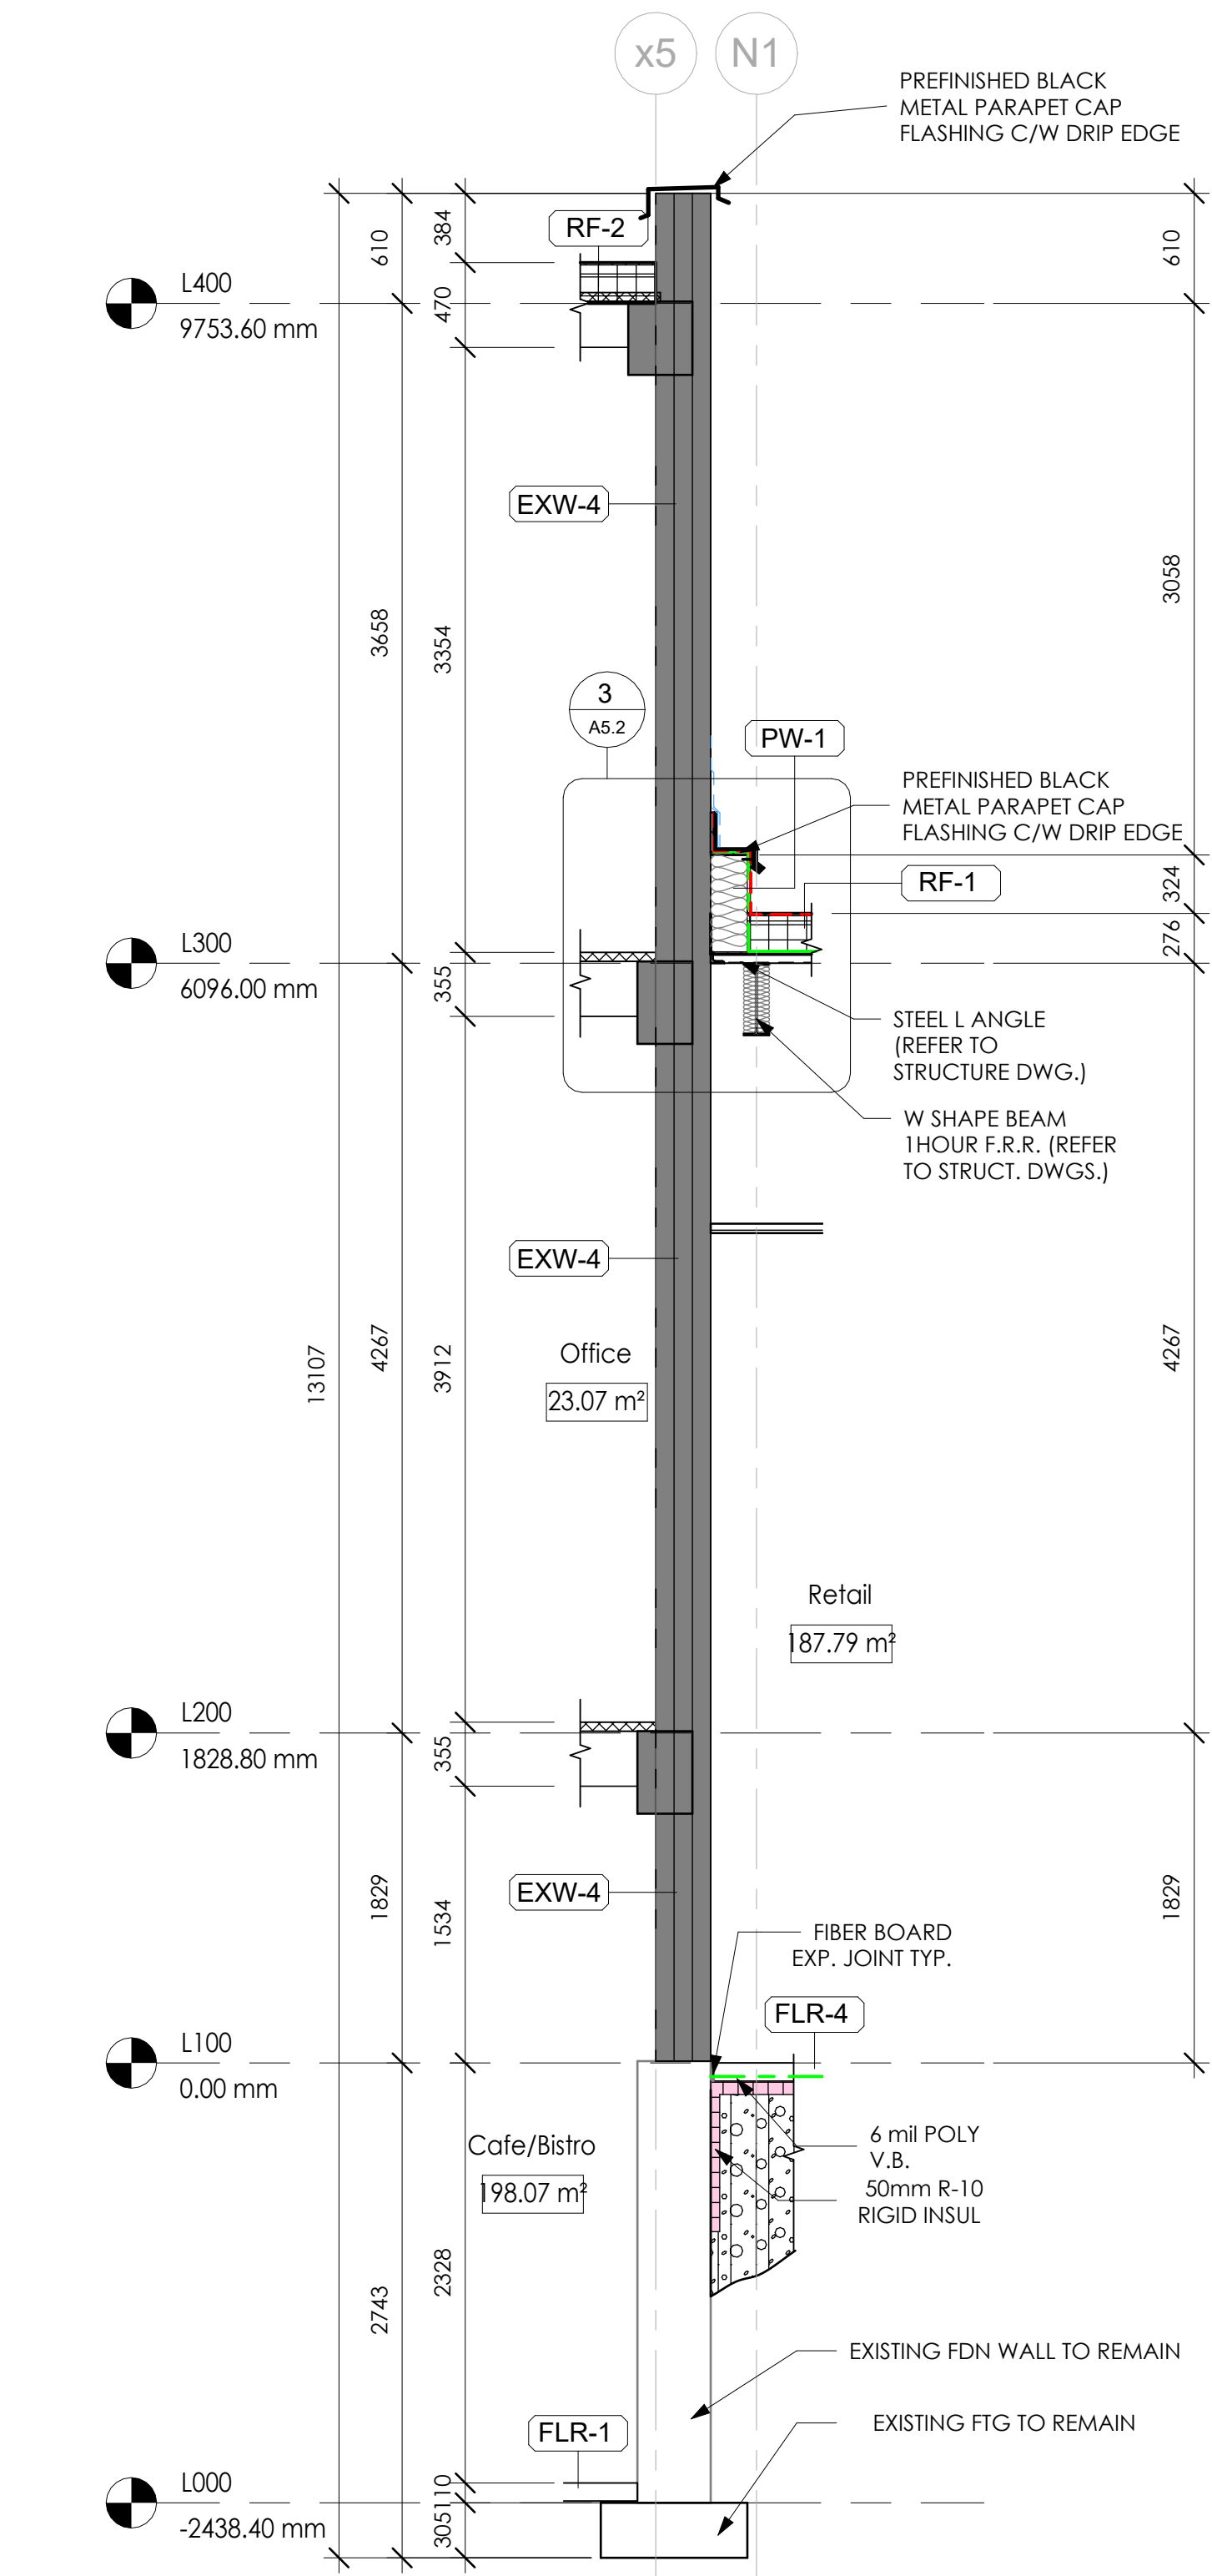

2 NEW TO EXISTING @ LOW ROOF
1 : 35

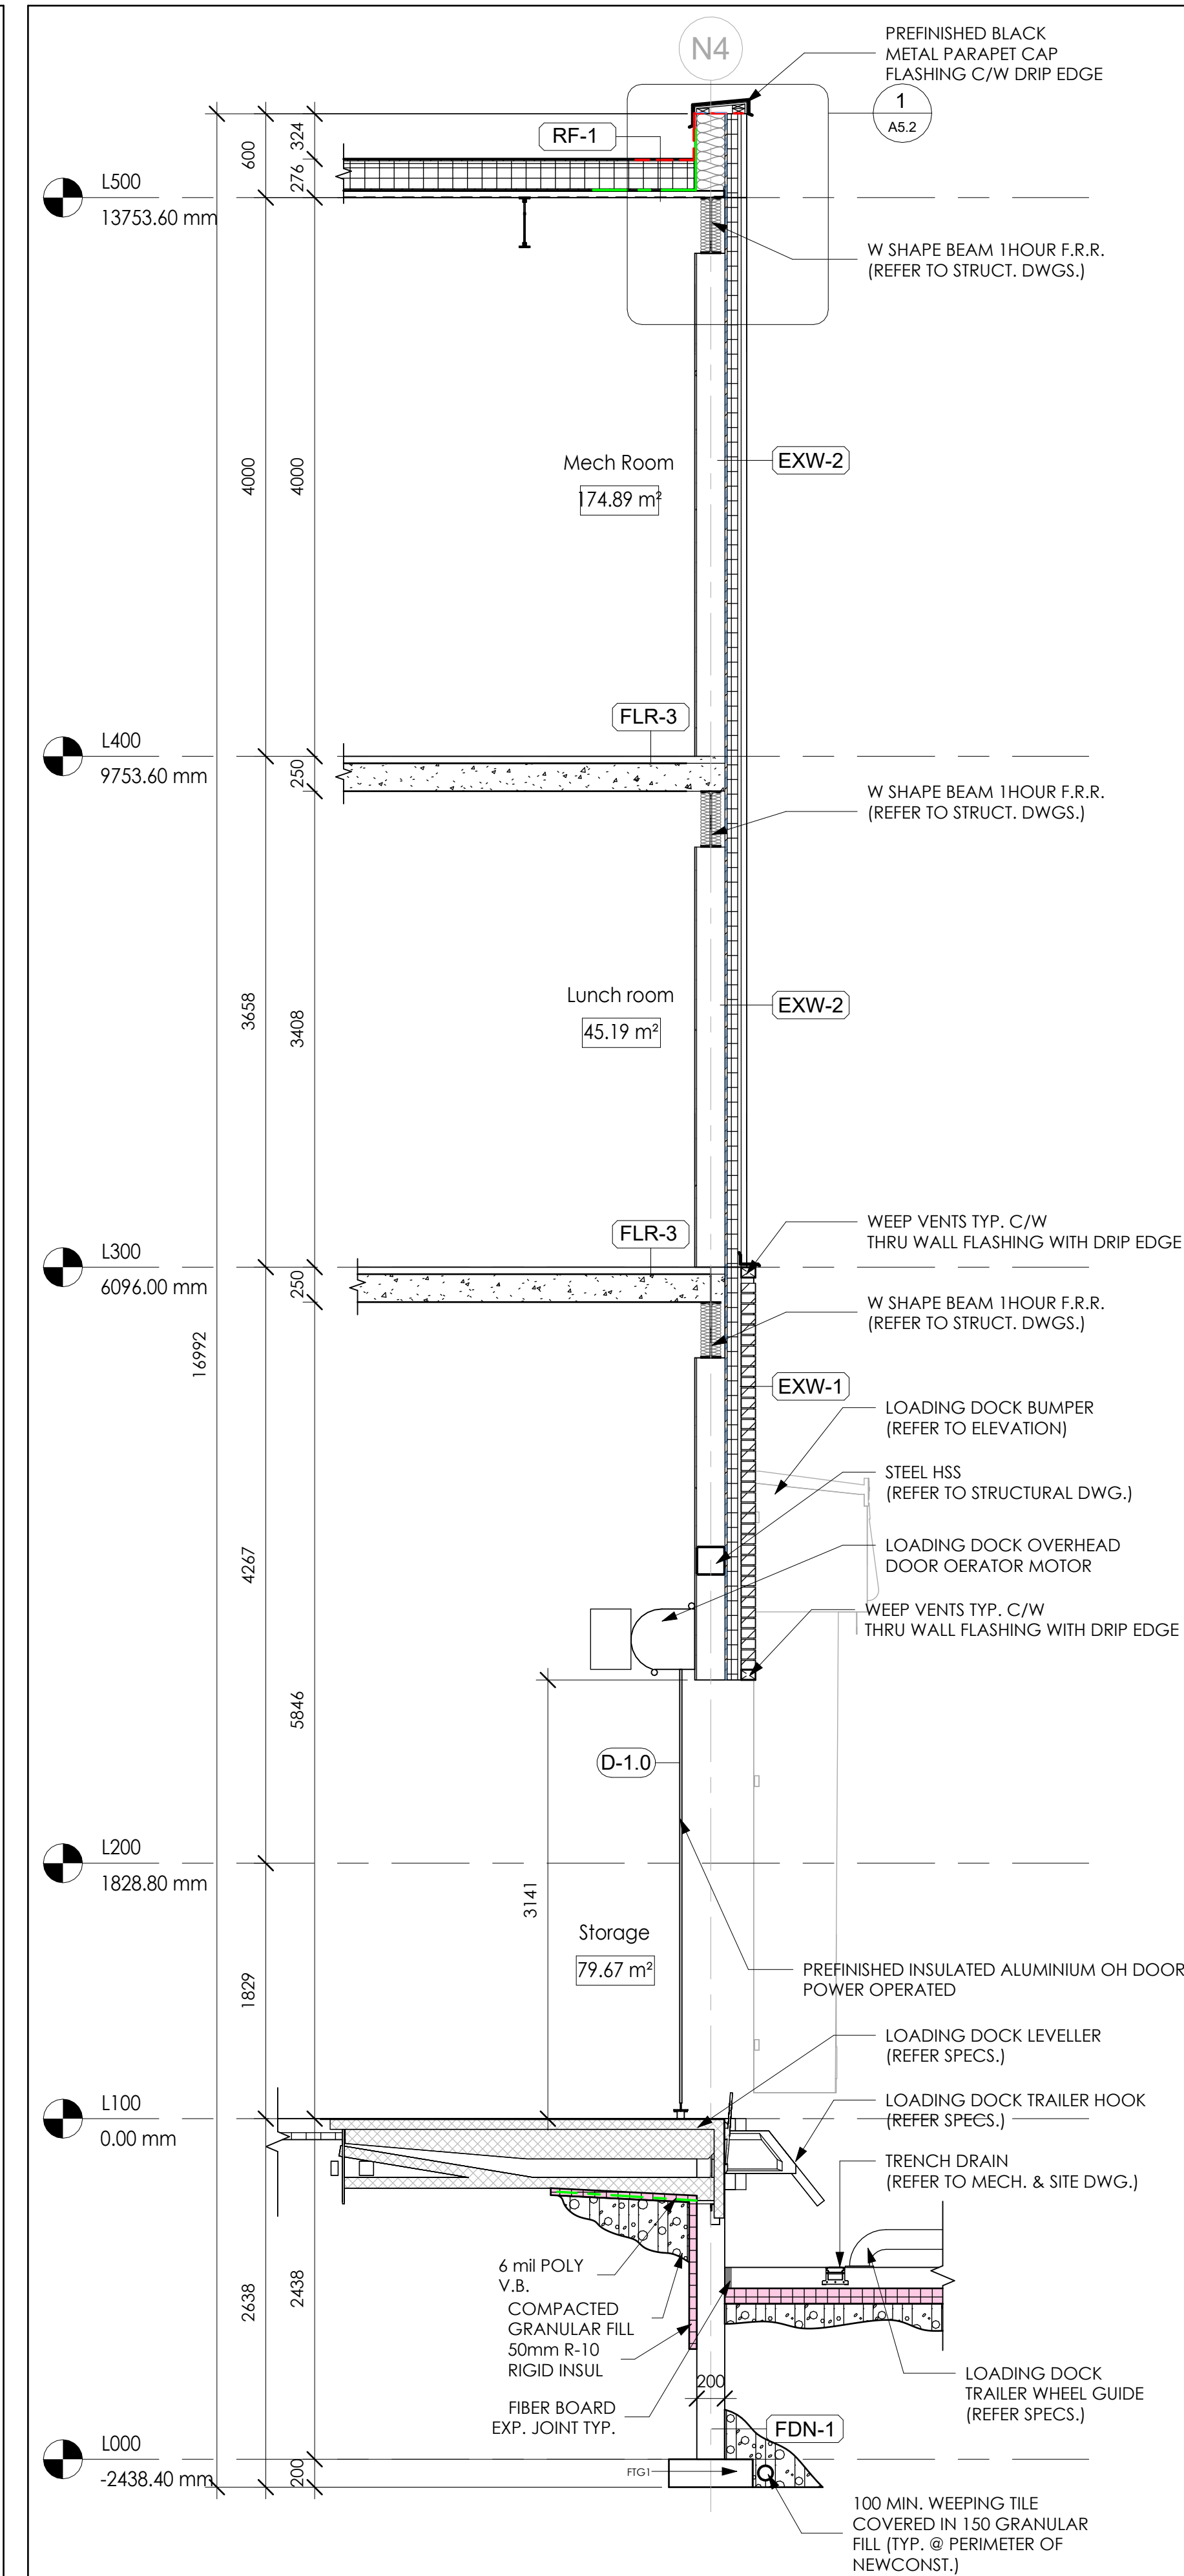


3 LOADING DOCK SECTION
1 : 35

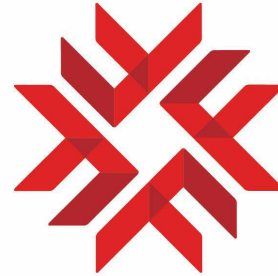

FANSHAW
DONALD J. SMITH
SCHOOL OF BUILDING
TECHNOLOGY

NORTH ARROW

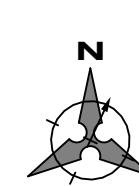

GENERAL NOTES

- DO NOT SCALE DRAWINGS. WRITTEN DIMENSIONS SHALL HAVE PRECEDENCE OVER SCALED DIMENSIONS.
- ALL WORK SHALL COMPLY WITH THE 2012 ONTARIO BUILDING CODE AND AMENDMENTS.
- CONTRACTORS MUST CHECK AND VERIFY ALL DIMENSIONS AND SPECIFICATIONS AND REPORT ANY DISCREPANCIES TO THE ARCHITECT BEFORE PROCEEDING WITH THE WORK.
- ALL CONTRACTORS AND SUB-CONTRACTORS SHALL HAVE A SET OF APPROVED CONSTRUCTION DOCUMENTS ON SITE AT ALL TIMES.
- ALL DOCUMENTS REMAIN THE PROPERTY OF THE ARCHITECT. UNAUTHORIZED USE, MODIFICATION, AND/OR REPRODUCTION OF THESE DOCUMENTS IS PROHIBITED WITHOUT WRITTEN PERMISSION. THE CONTRACT DOCUMENTS WERE PREPARED BY THE CONSULTANT FOR THE ACCOUNT OF THE OWNER.
- THE MATERIAL CONTAINED HEREIN REFLECTS THE CONSULTANT'S BEST JUDGMENT IN LIGHT OF THE INFORMATION AVAILABLE TO HIM/HER AT THE TIME OF PREPARATION. ANY USE WHICH A THIRD PARTY MAKES OF THE CONTRACT DOCUMENTS, OR ANY RELIANCE ON/OR DECISIONS TO BE MADE BASED ON THEM ARE THE RESPONSIBILITY OF SUCH THIRD PARTIES.
- THE CONSULTANT ACCEPTS NO RESPONSIBILITY FOR DAMAGES, IF ANY, SUFFERED BY ANY THIRD PARTY AS A RESULT OF DECISIONS MADE OR ACTIONS BASED ON THE CONTRACT DOCUMENTS.

PROJECT TITLE

THE EDEN PROJECT

CLIENT:

Eden Project

PROJECT ADDRESS

555 McCormick Street

DRAWING TITLE

WALL SECTIONS

CHECKED	DRAWN	DATE
GG	AFNM	15/08/25




0001

PROJECT No.


A4.1

DRAWING

PRELIMINARY
NOT FOR CONSTRUCTION

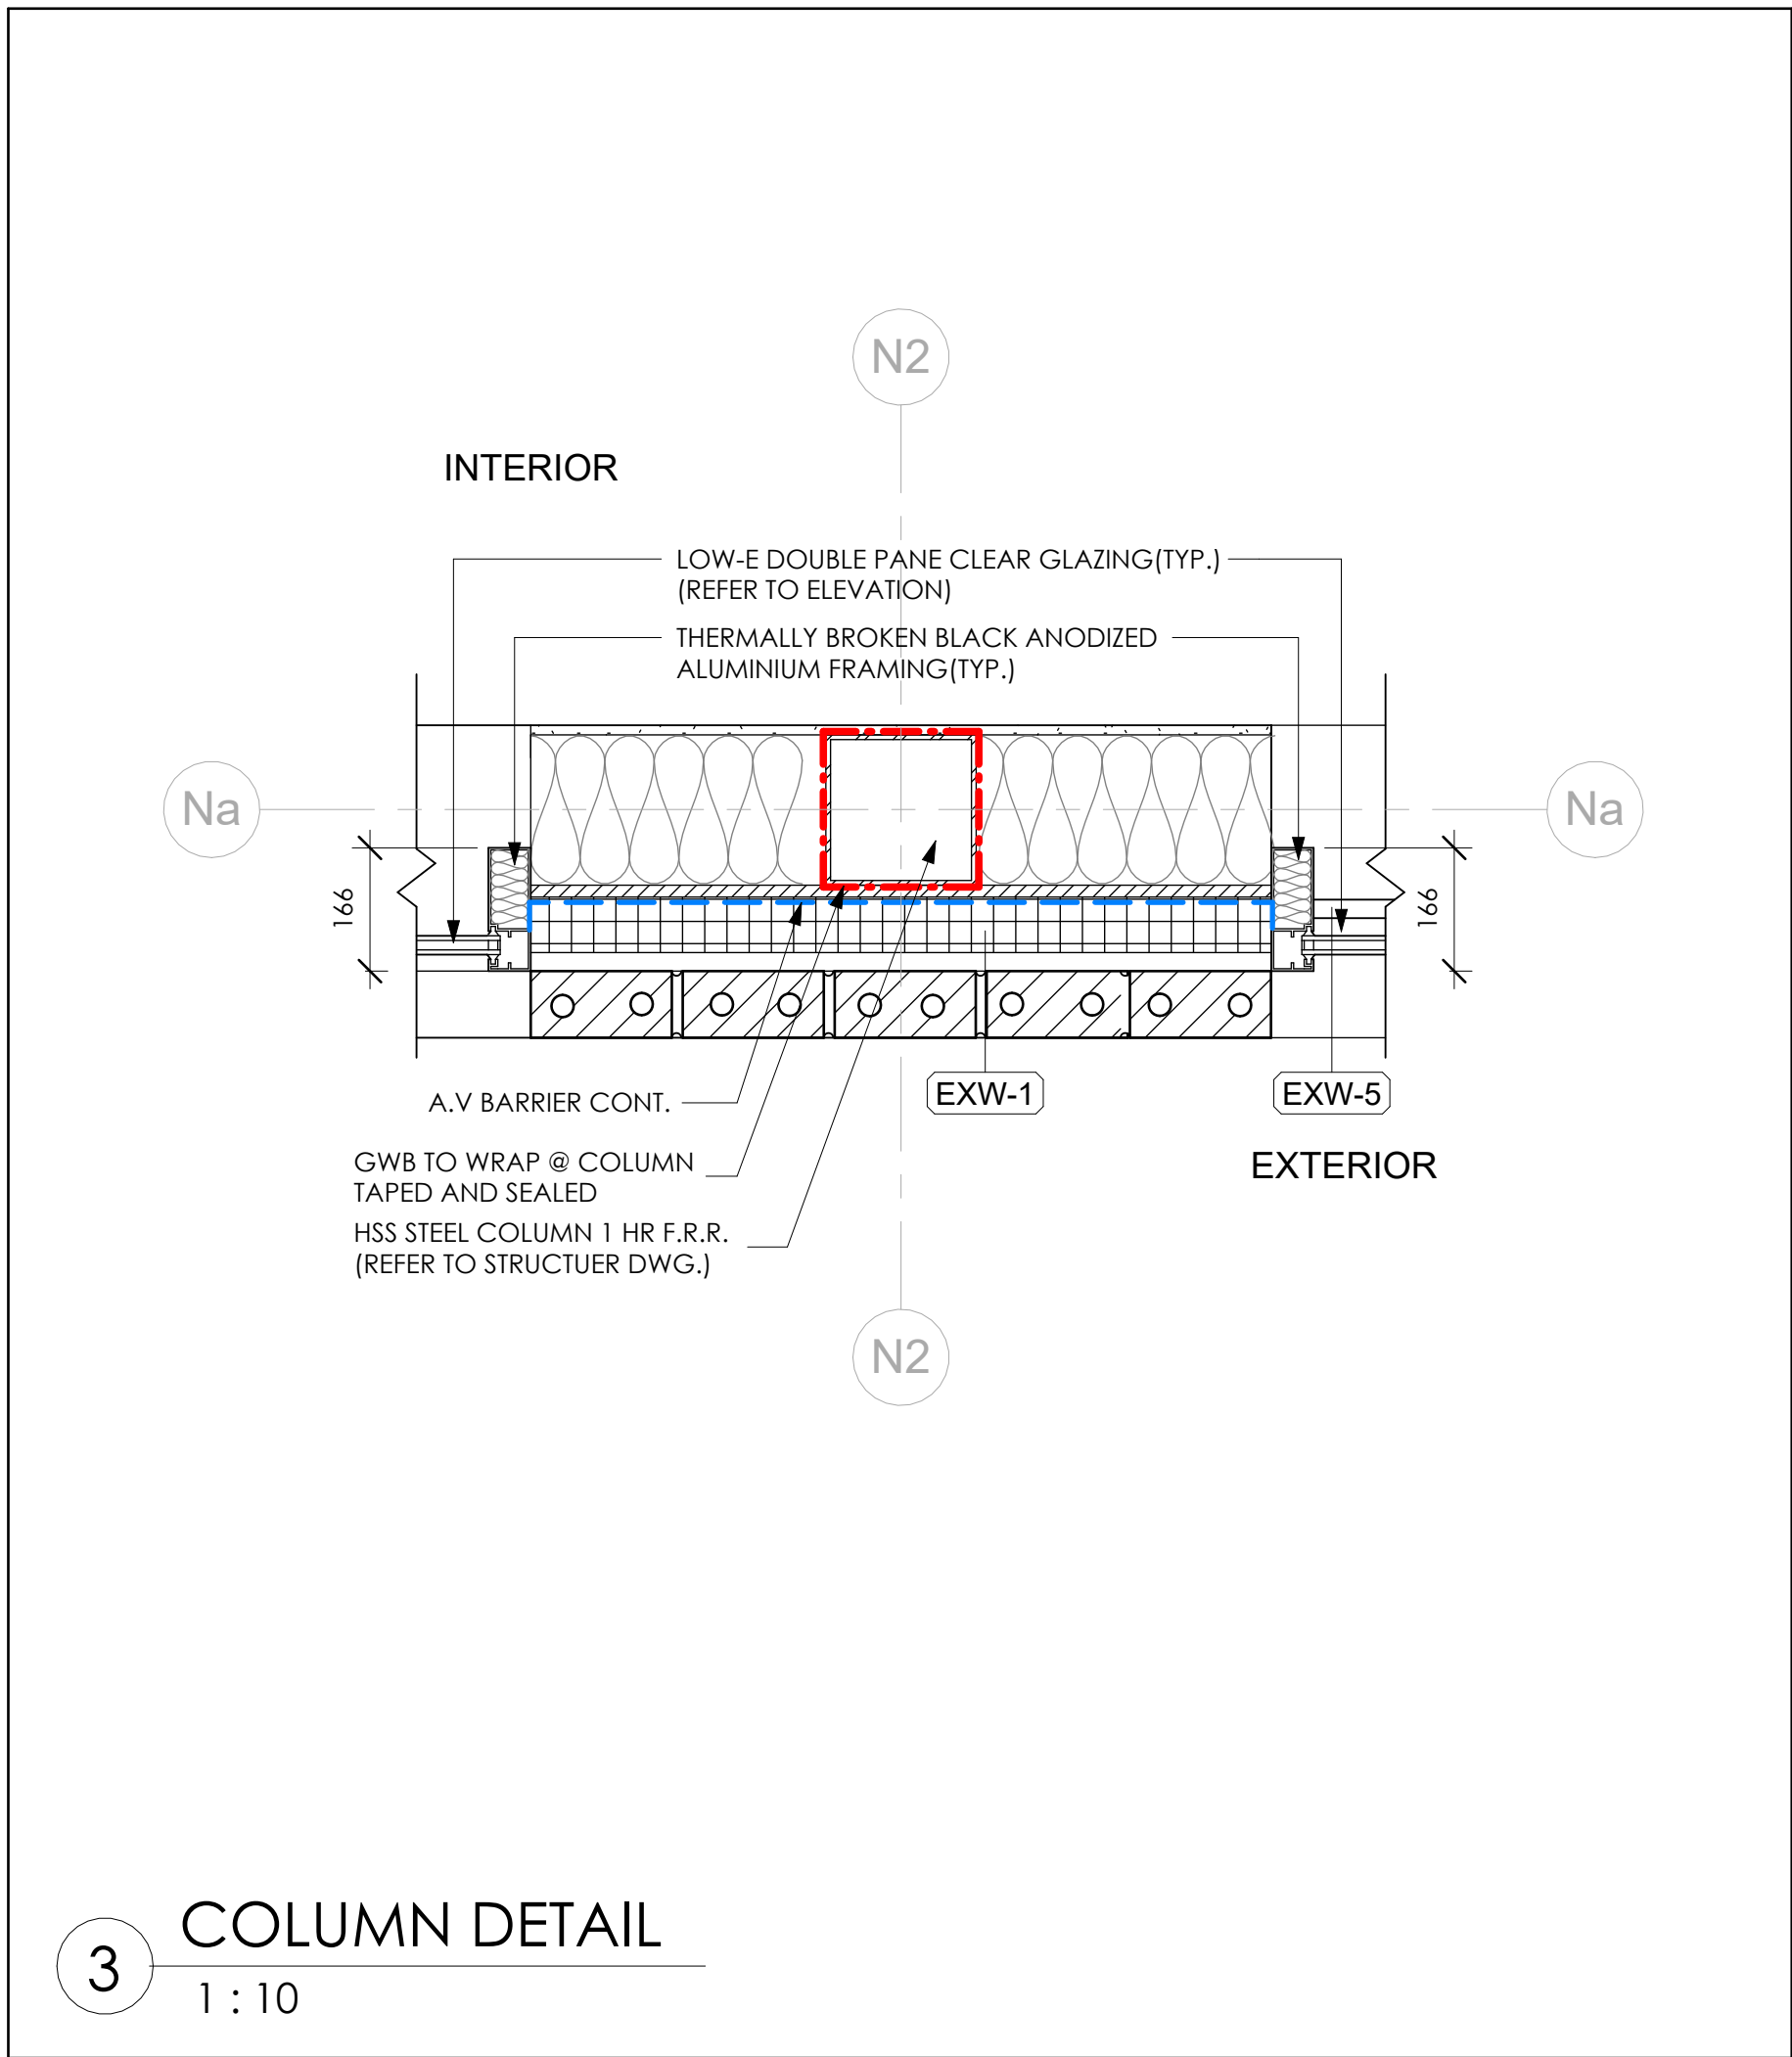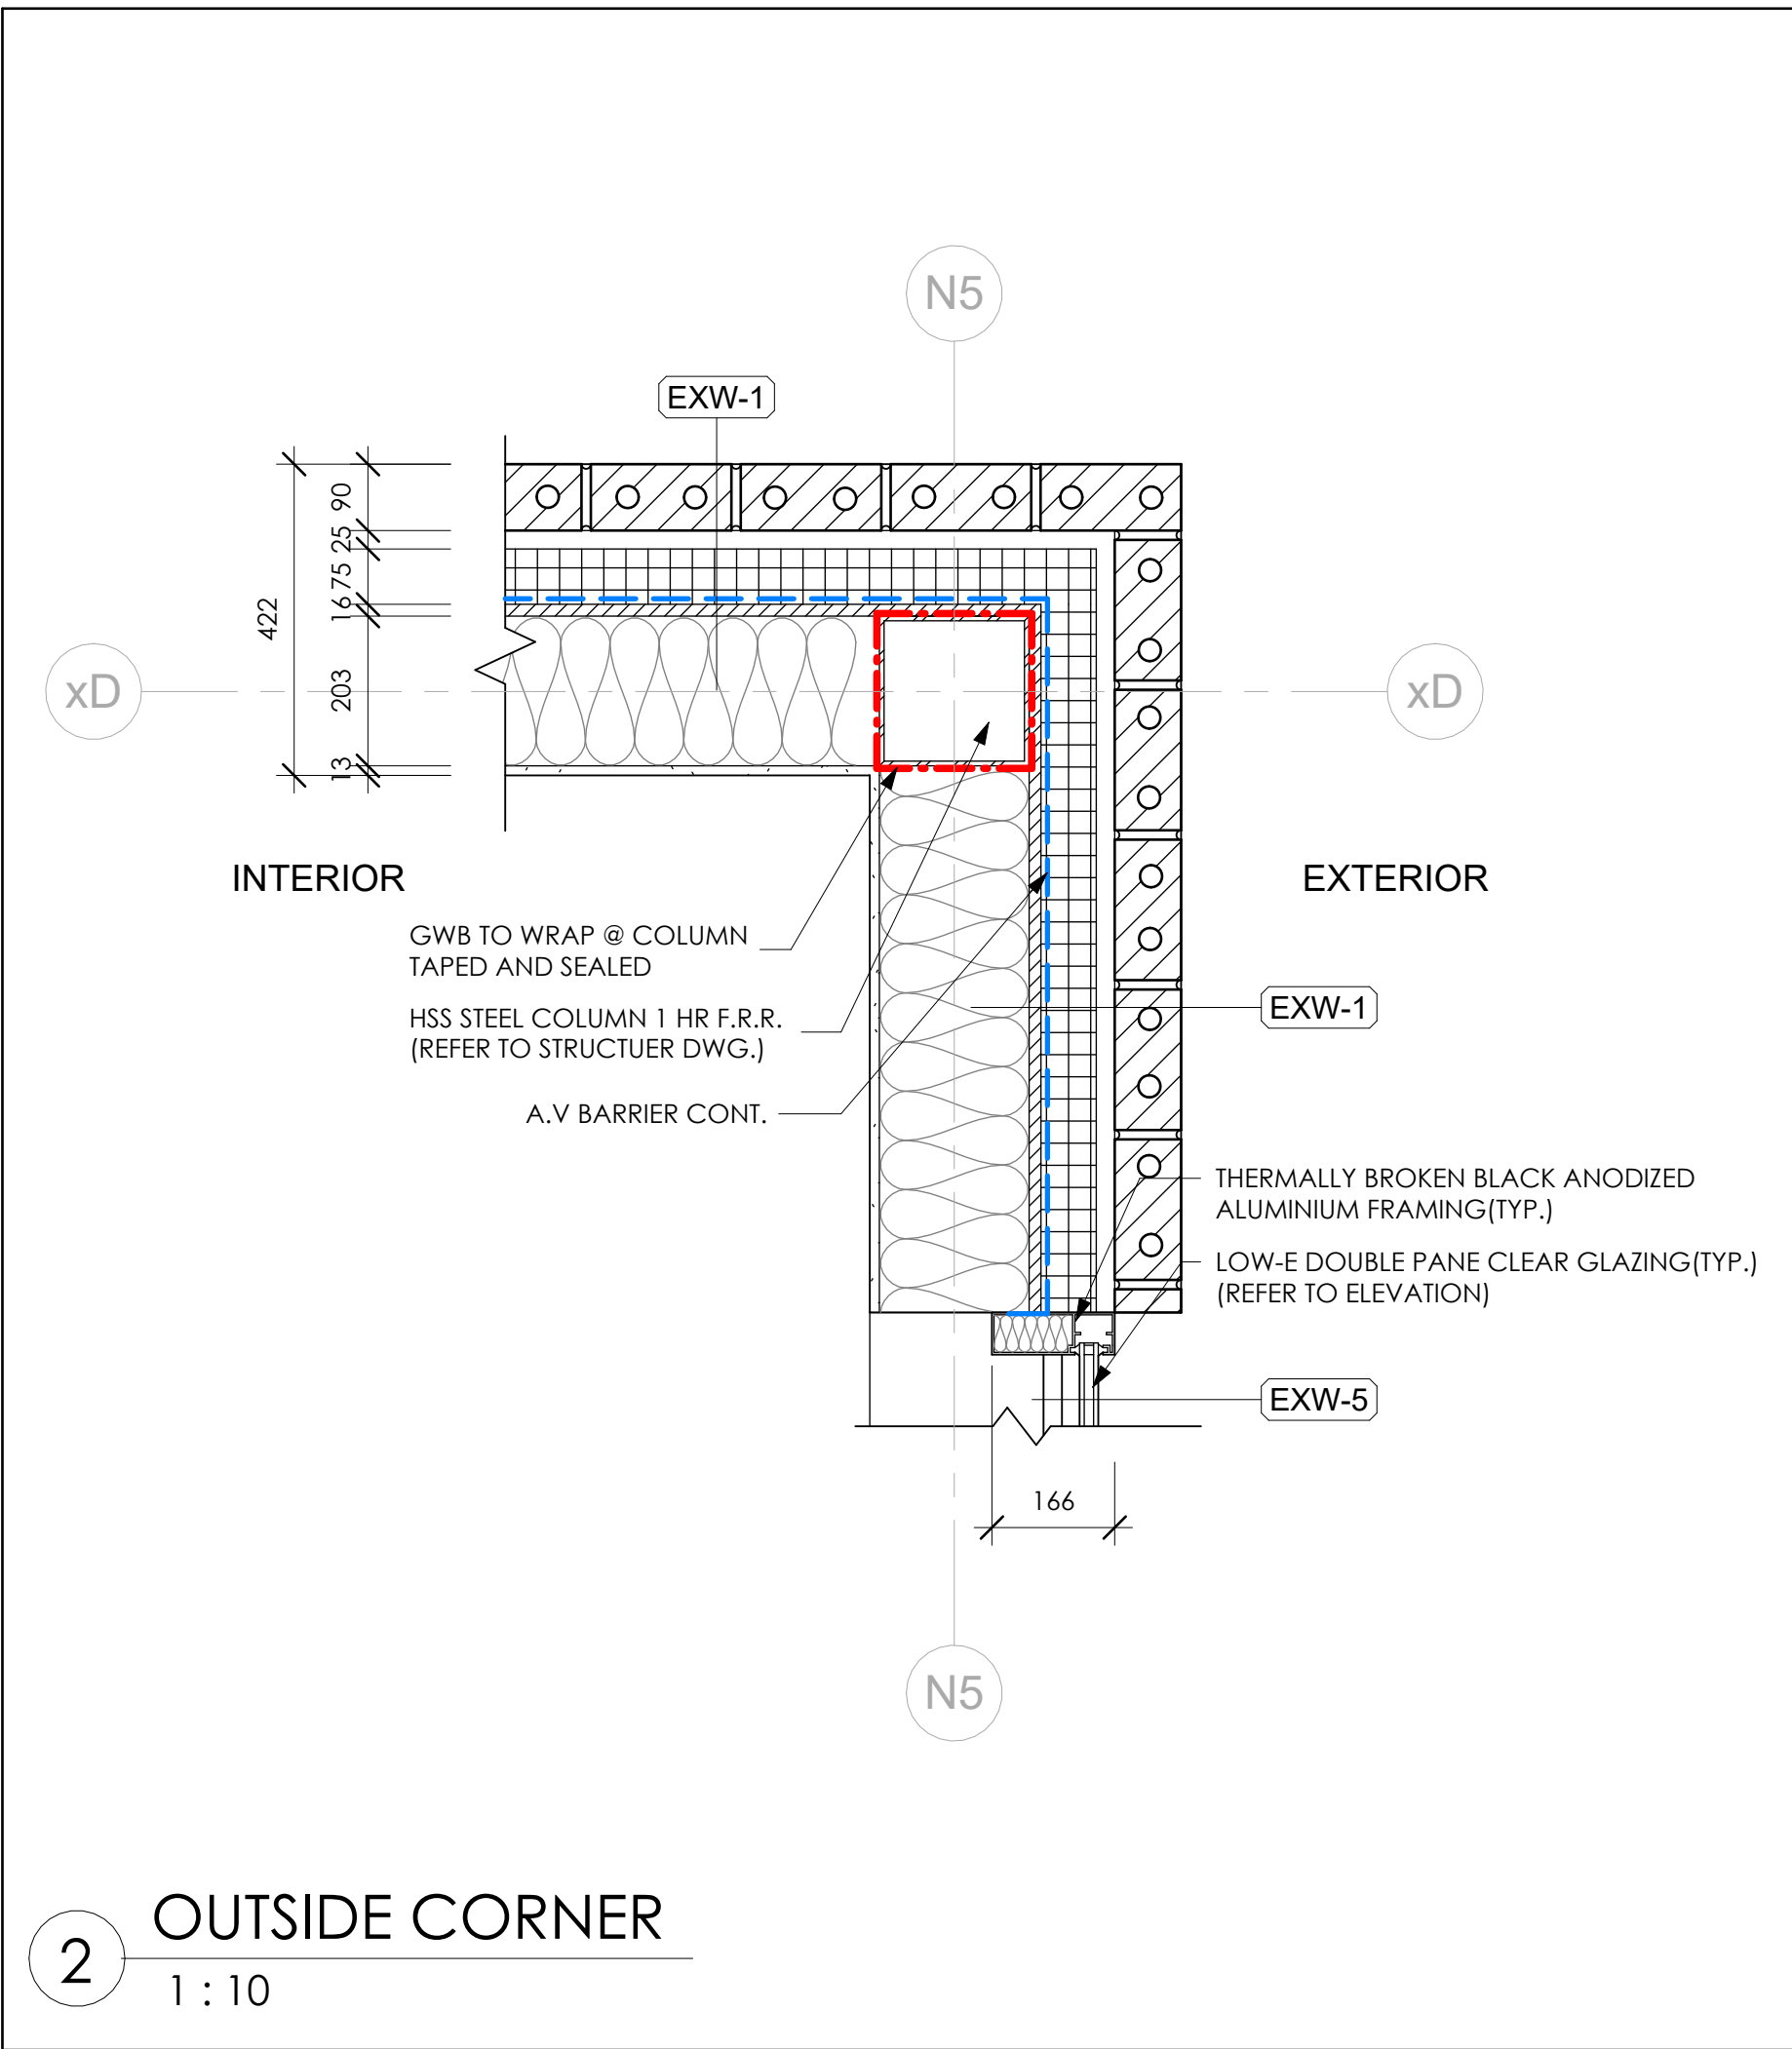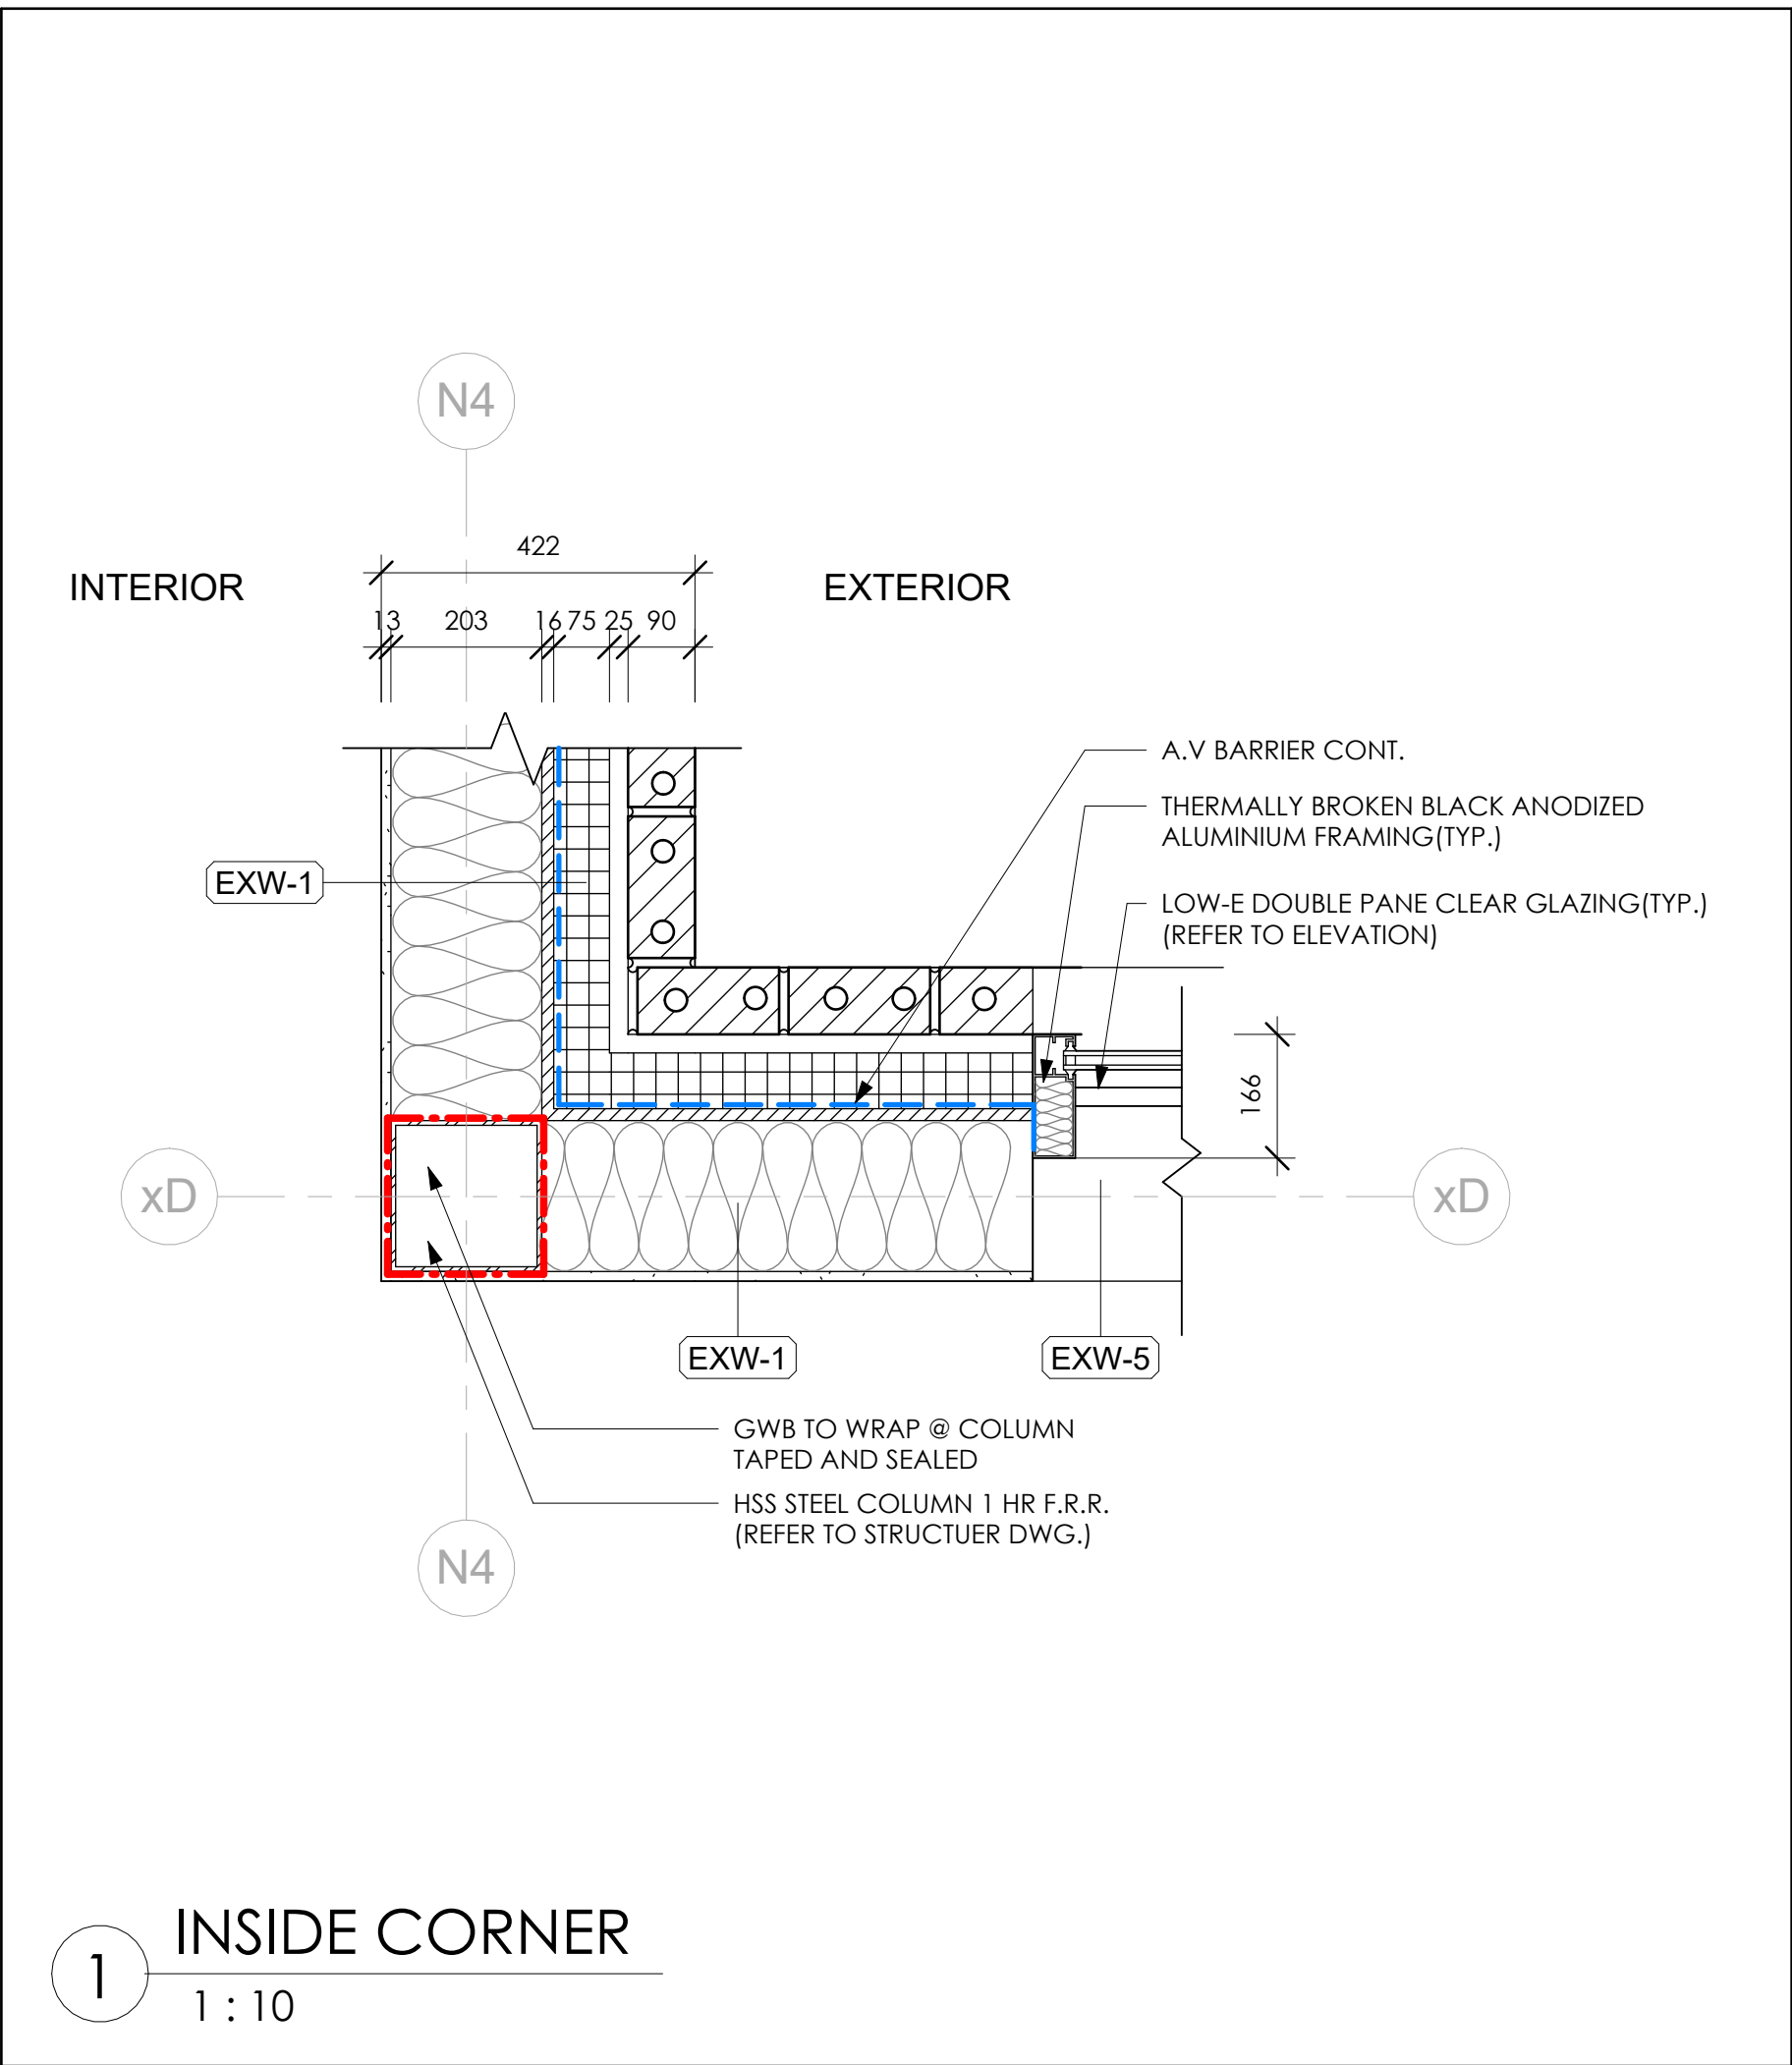

NORTH ARROW

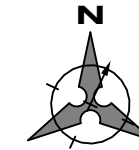

- GENERAL NOTES
1. DO NOT SCALE DRAWINGS. WRITTEN DIMENSIONS SHALL HAVE PRECEDENCE OVER SCALED DIMENSIONS.
 2. ALL WORK SHALL COMPLY WITH THE 2012 ONTARIO BUILDING CODE AND AMENDMENTS.
 3. CONTRACTORS MUST CHECK AND VERIFY ALL DIMENSIONS AND SPECIFICATIONS AND REPORT ANY DISCREPANCIES TO THE ARCHITECT BEFORE PROCEEDING WITH THE WORK.
 4. ALL CONTRACTORS AND SUB-CONTRACTORS SHALL HAVE A SET OF APPROVED CONSTRUCTION DOCUMENTS ON SITE AT ALL TIMES.
 5. ALL DOCUMENTS REMAIN THE PROPERTY OF THE ARCHITECT. UNAUTHORIZED USE, MODIFICATION, AND/OR REPRODUCTION OF THESE DOCUMENTS IS PROHIBITED WITHOUT WRITTEN PERMISSION. THE CONTRACT DOCUMENTS WERE PREPARED BY THE CONSULTANT FOR THE ACCOUNT OF THE OWNER.
 6. THE MATERIAL CONTAINED HEREIN REFLECTS THE CONSULTANT'S BEST JUDGEMENT IN LIGHT OF THE INFORMATION AVAILABLE TO HIM/HER AT THE TIME OF PREPARATION. ANY USE WHICH A THIRD PARTY MAKES OF THE CONTRACT DOCUMENTS, OR ANY RELIANCE ON/OR DECISIONS TO BE MADE BASED ON THEM ARE THE RESPONSIBILITY OF SUCH THIRD PARTIES.
 7. THE CONSULTANT ACCEPTS NO RESPONSIBILITY FOR DAMAGES, IF ANY, SUFFERED BY ANY THIRD PARTY AS A RESULT OF DECISIONS MADE OR ACTIONS BASED ON THE CONTRACT DOCUMENTS

PRELIMINARY
NOT FOR CONSTRUCTION

PROJECT TITLE
THE EDEN PROJECT







CLIENT:
Eden Project

PROJECT ADDRESS
555 McCormick Street

DRAWING TITLE
PLAN DETAILS

CHECKED GG	DRAWN AFNM	DATE 15/08/25
---------------	---------------	------------------

0001 PROJECT No.	A5.1 DRAWING
---------------------	-----------------

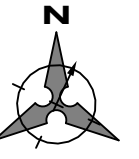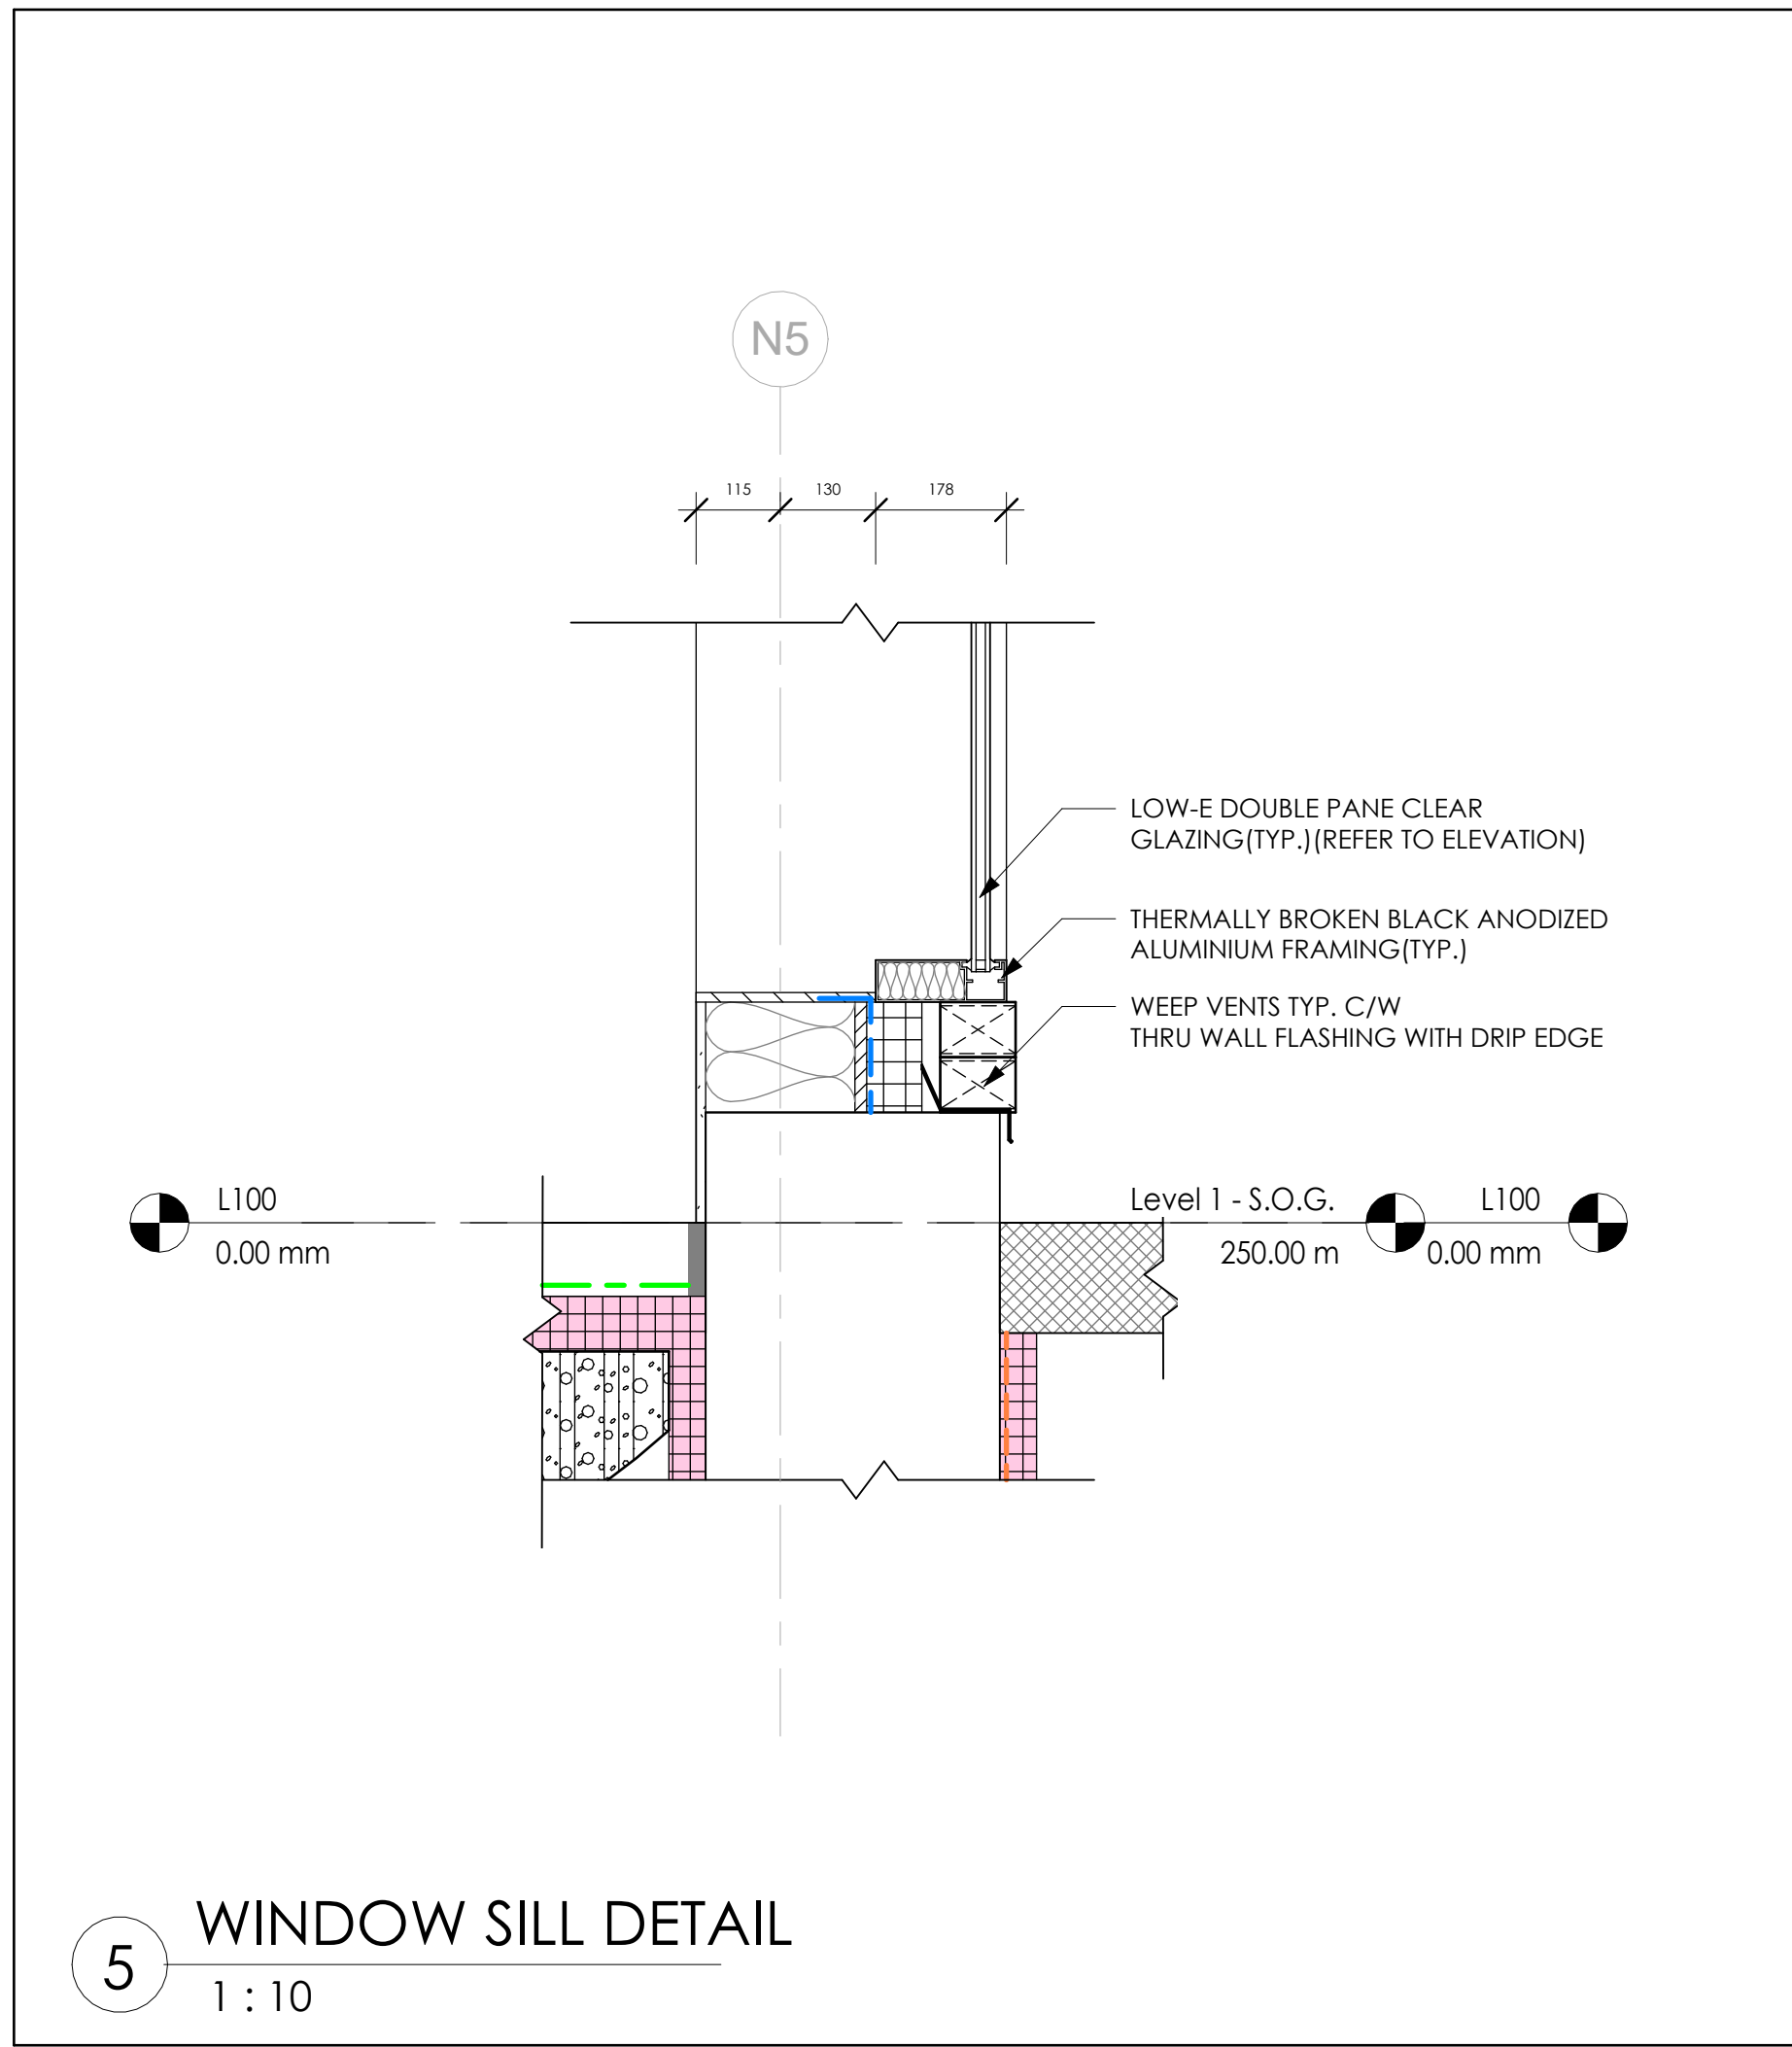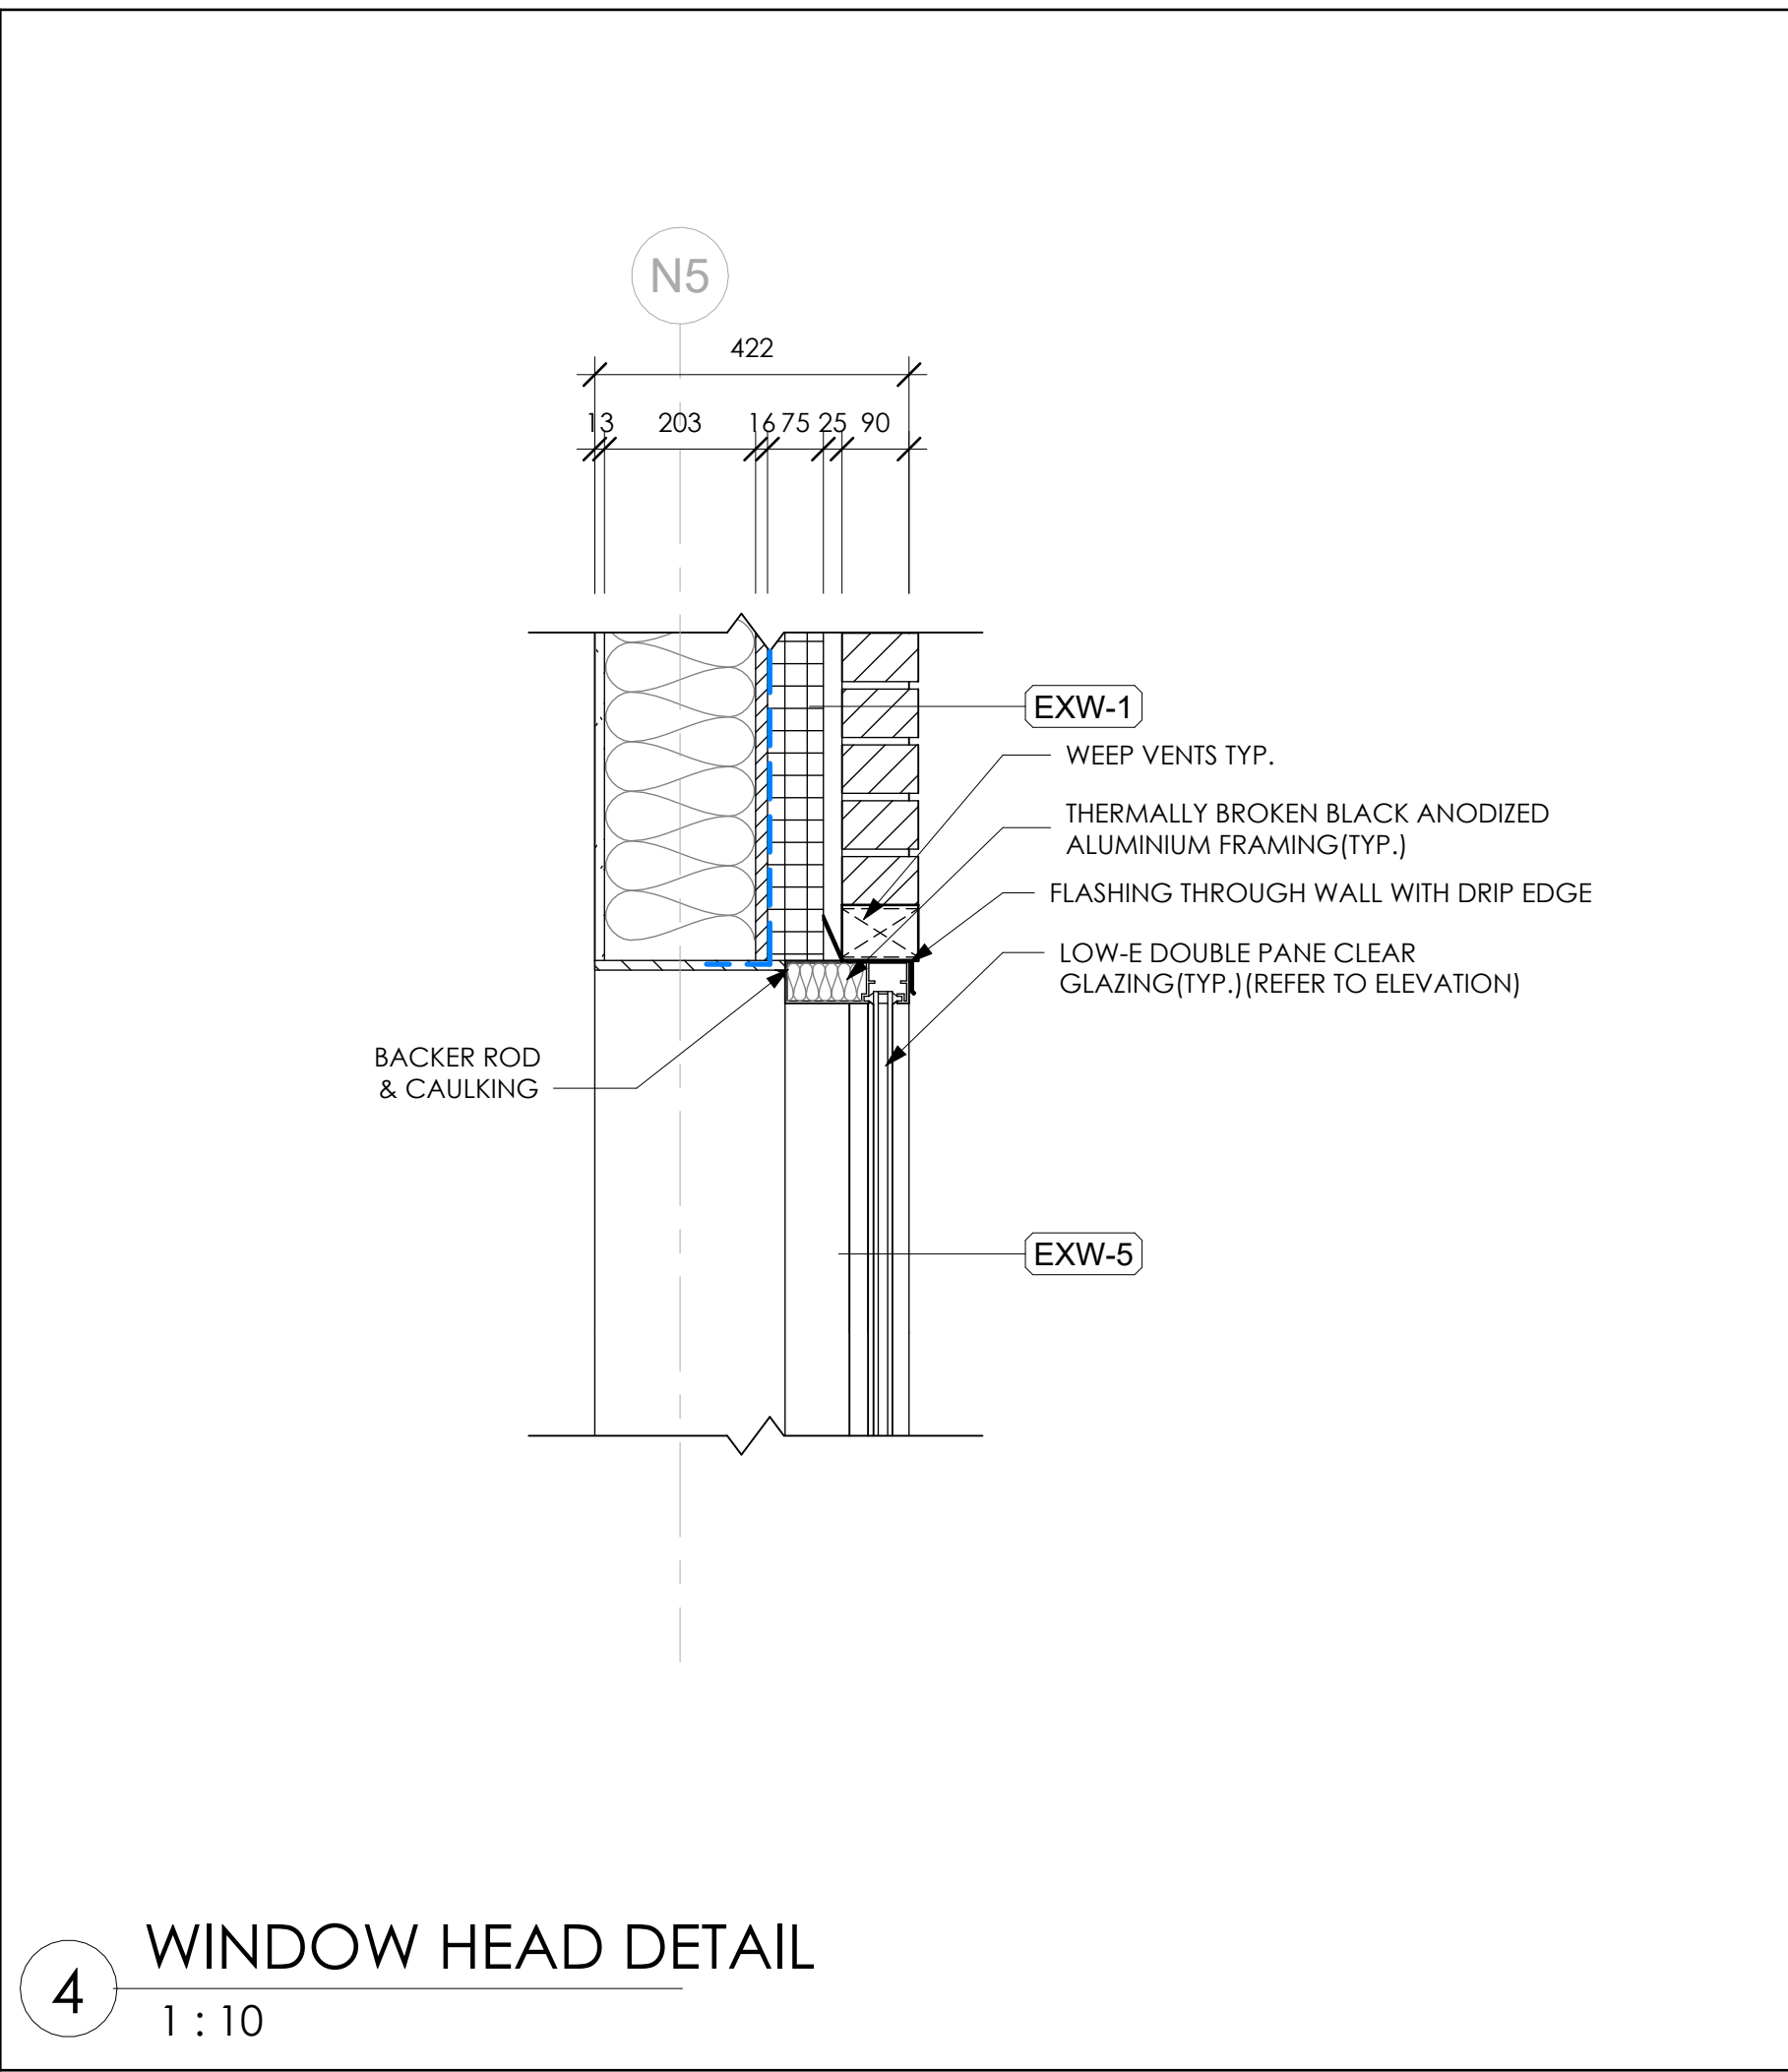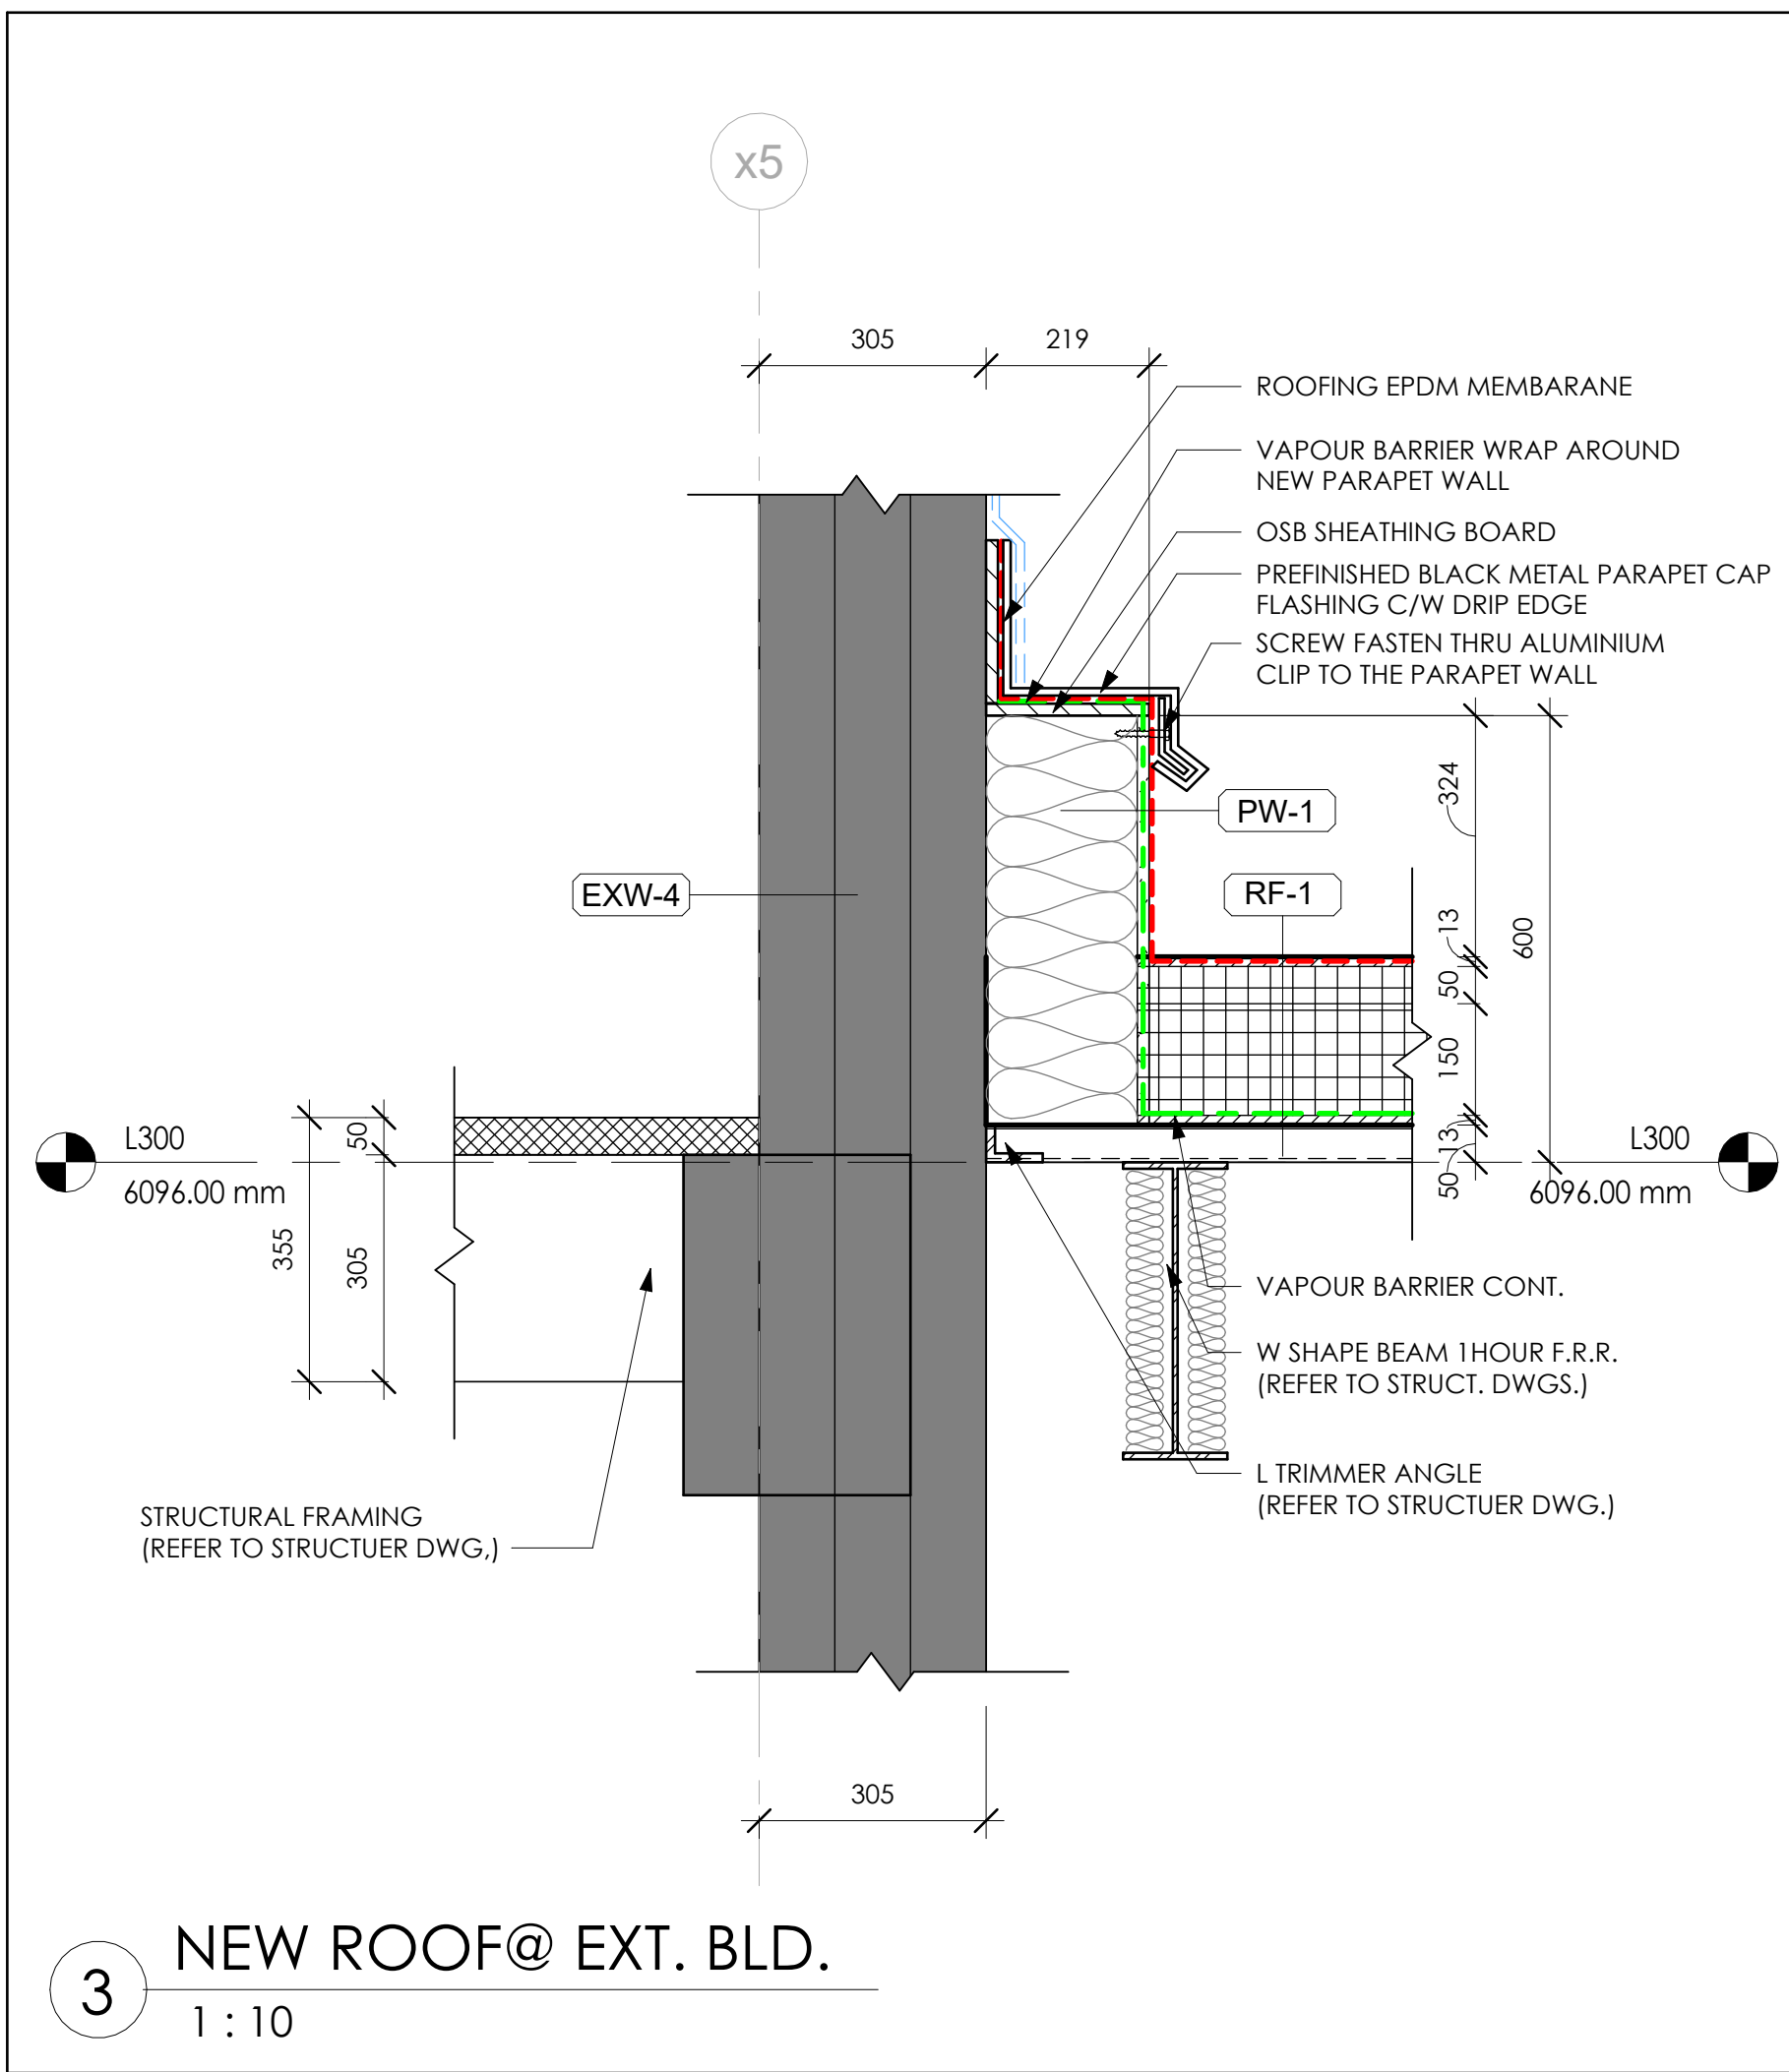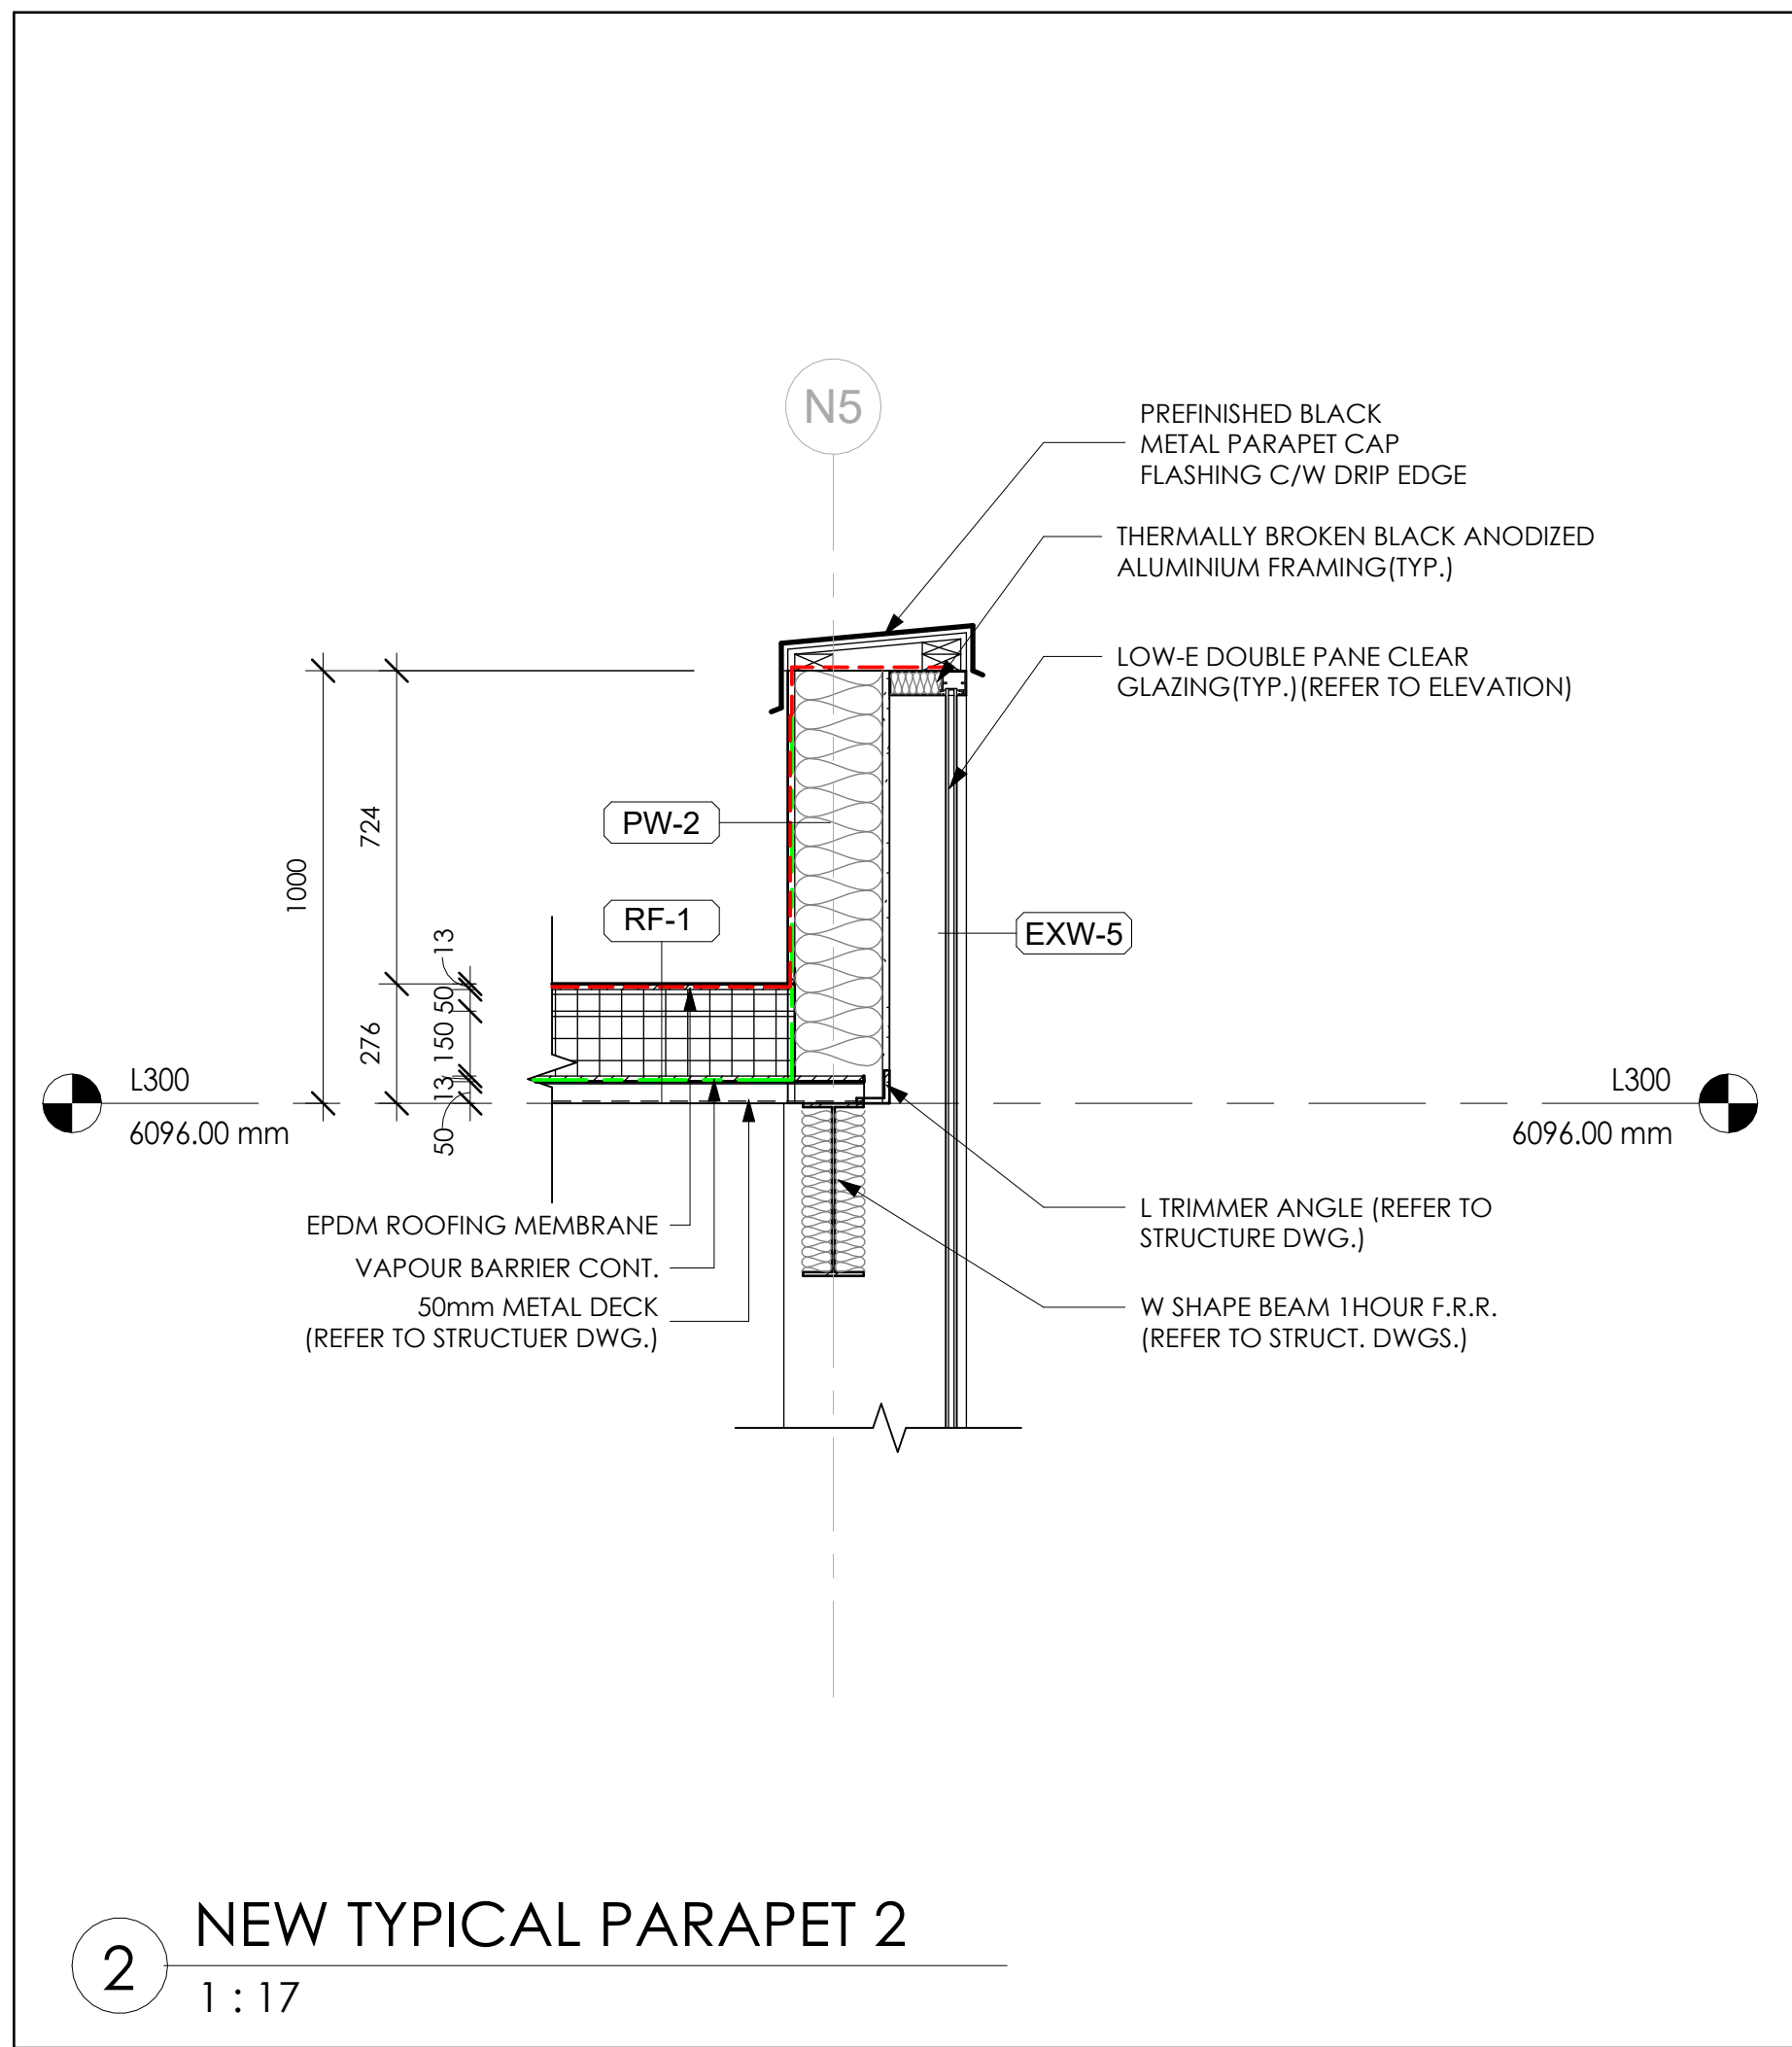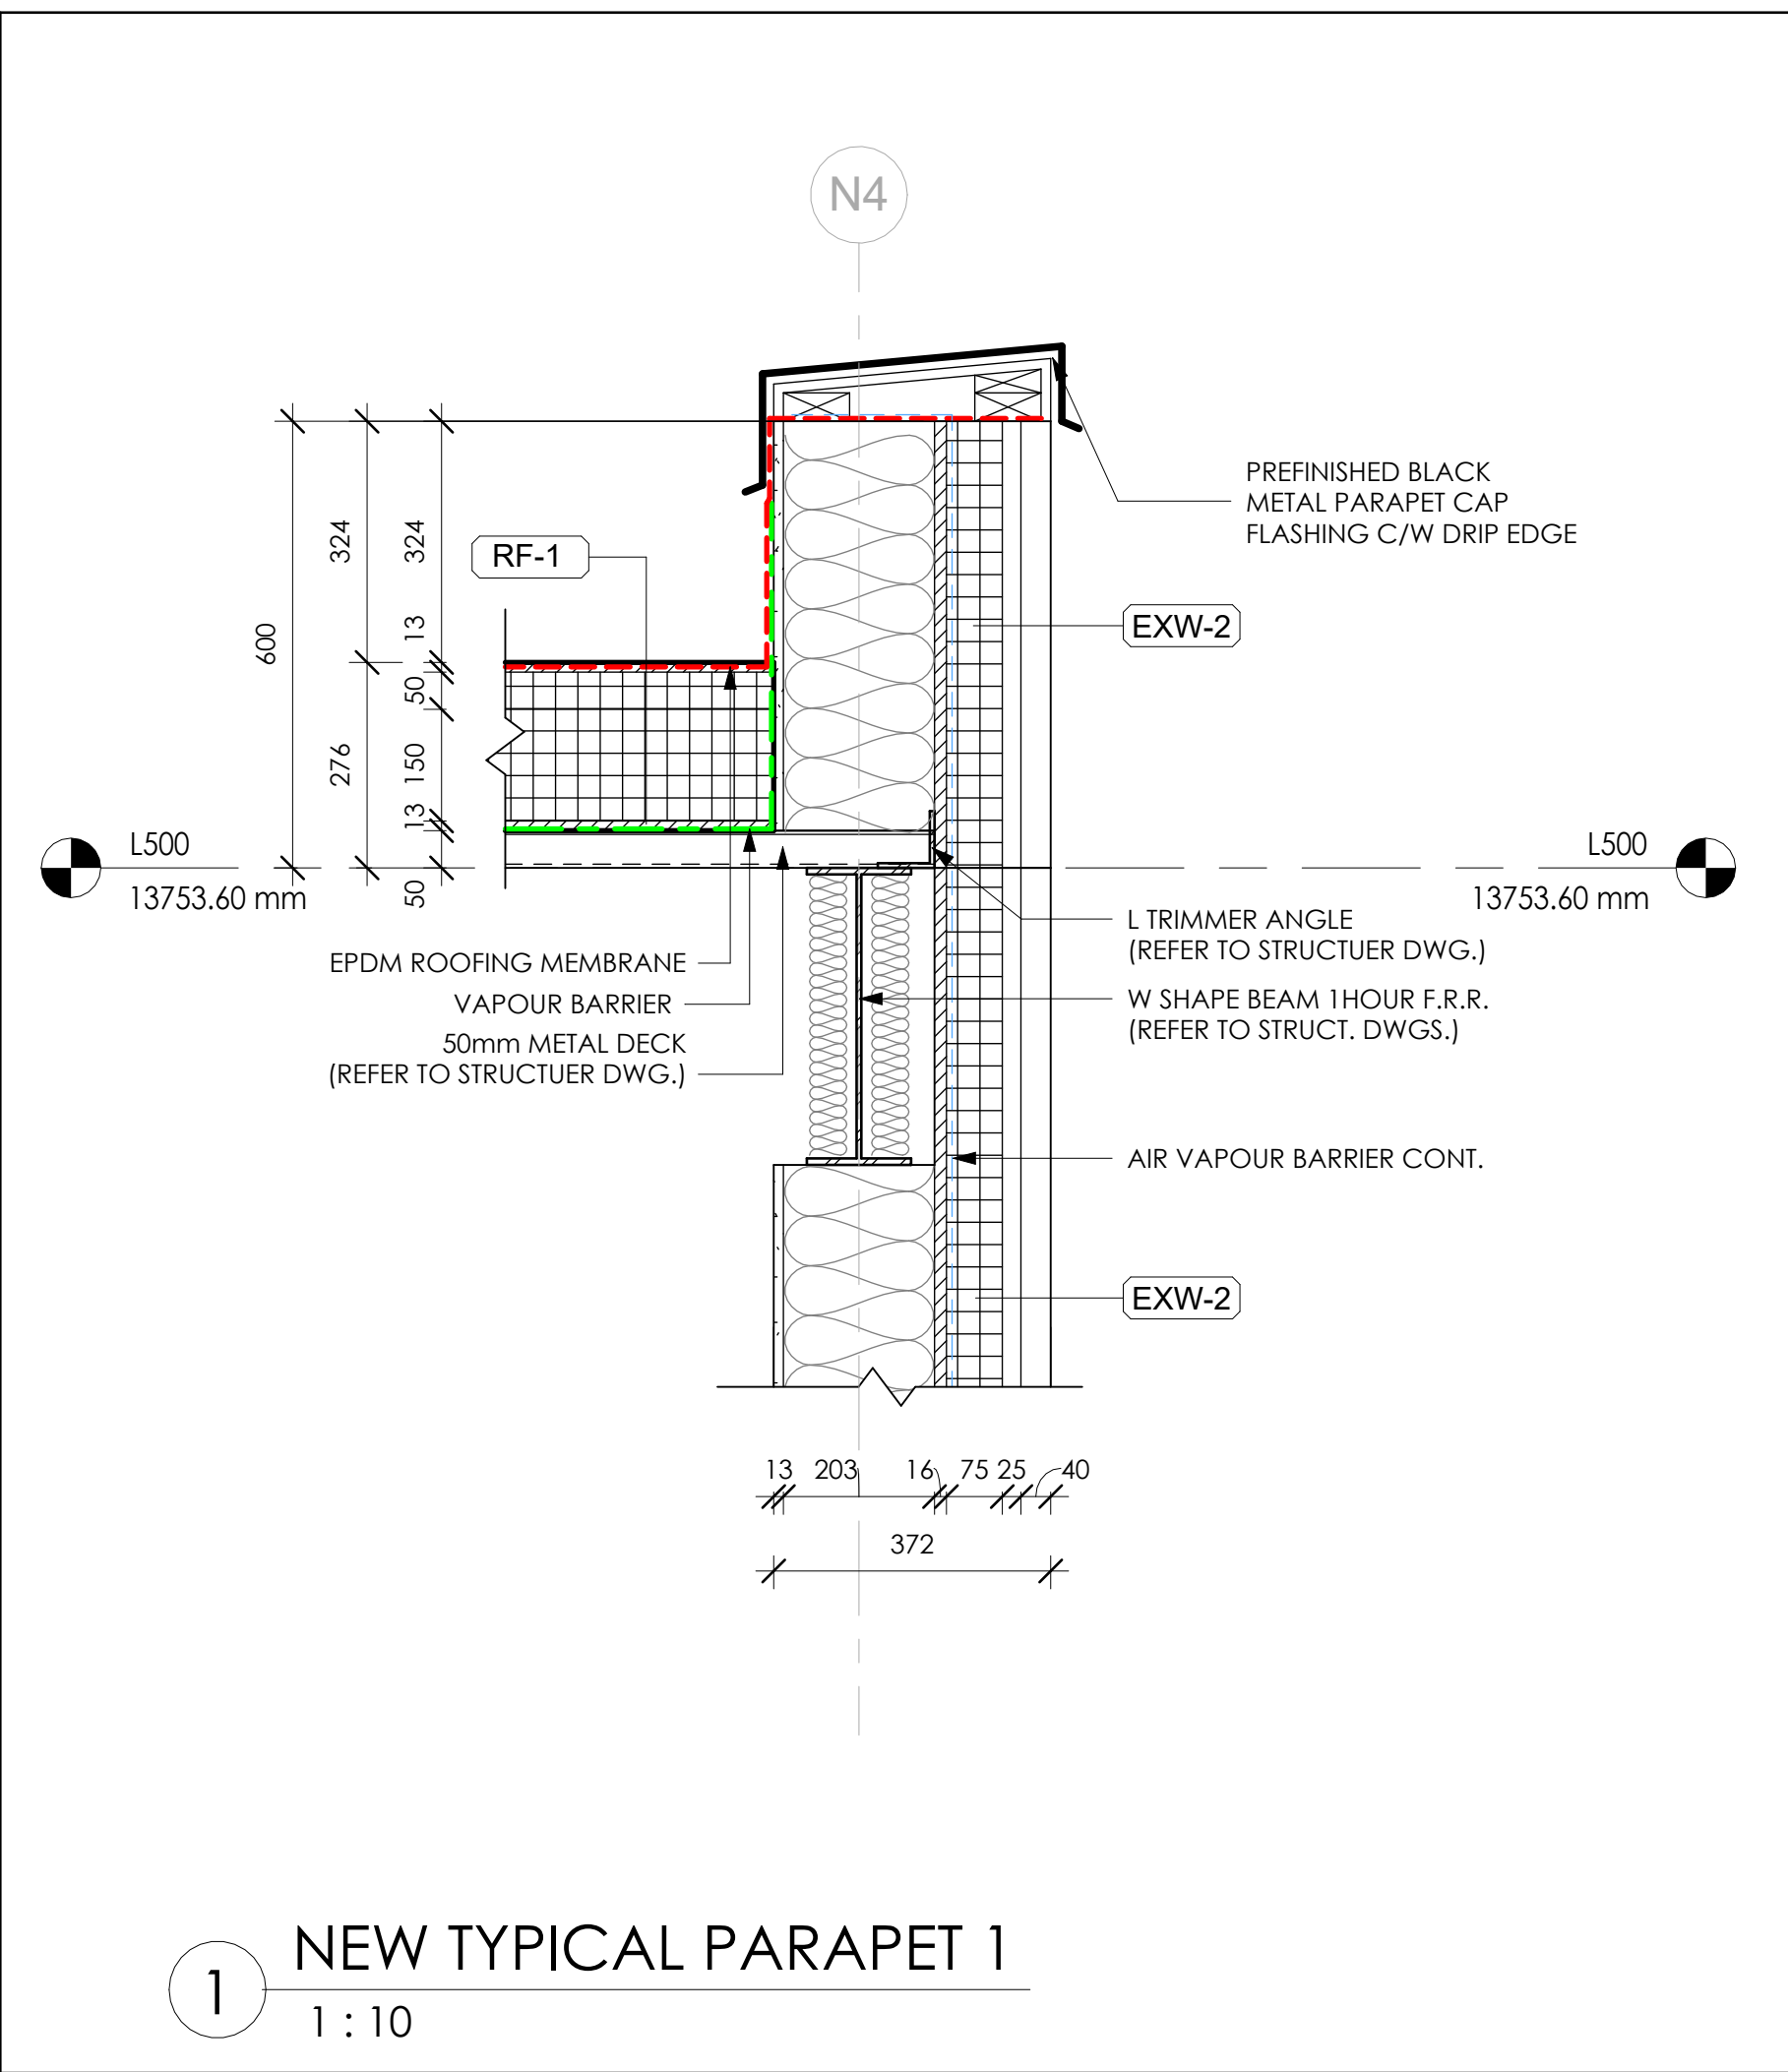

- GENERAL NOTES
1. DO NOT SCALE DRAWINGS. WRITTEN DIMENSIONS SHALL HAVE PRECEDENCE OVER SCALED DIMENSIONS.
 2. ALL WORK SHALL COMPLY WITH THE 2012 ONTARIO BUILDING CODE AND AMENDMENTS.
 3. CONTRACTORS MUST CHECK AND VERIFY ALL DIMENSIONS AND SPECIFICATIONS AND REPORT ANY DISCREPANCIES TO THE ARCHITECT BEFORE PROCEEDING WITH THE WORK.
 4. ALL CONTRACTORS AND SUB-CONTRACTORS SHALL HAVE A SET OF APPROVED CONSTRUCTION DOCUMENTS ON SITE AT ALL TIMES.
 5. ALL DOCUMENTS REMAIN THE PROPERTY OF THE ARCHITECT. UNAUTHORIZED USE, MODIFICATION, AND/OR REPRODUCTION OF THESE DOCUMENTS IS PROHIBITED WITHOUT WRITTEN PERMISSION. THE CONTRACT DOCUMENTS WERE PREPARED BY THE CONSULTANT FOR THE ACCOUNT OF THE OWNER.
 6. THE MATERIAL CONTAINED HEREIN REFLECTS THE CONSULTANT'S BEST JUDGMENT IN LIGHT OF THE INFORMATION AVAILABLE TO HIM/HER AT THE TIME OF PREPARATION. ANY USE WHICH A THIRD PARTY MAKES OF THE CONTRACT DOCUMENTS, OR ANY RELIANCE ON/OR DECISIONS TO BE MADE BASED ON THEM ARE THE RESPONSIBILITY OF SUCH THIRD PARTIES.
 7. THE CONSULTANT ACCEPTS NO RESPONSIBILITY FOR DAMAGES, IF ANY, SUFFERED BY ANY THIRD PARTY AS A RESULT OF DECISIONS MADE OR ACTIONS BASED ON THE CONTRACT DOCUMENTS.

PRELIMINARY
NOT FOR CONSTRUCTION

PROJECT TITLE
THE EDEN PROJECT


CLIENT:
Eden Project

PROJECT ADDRESS
555 McCormick Street


DRAWING TITLE
SECTION DETAILS

CHECKED | DRAWN | DATE
GG | AFNM | 15/08/25


0001 | **A5.2**
PROJECT No. | DRAWING

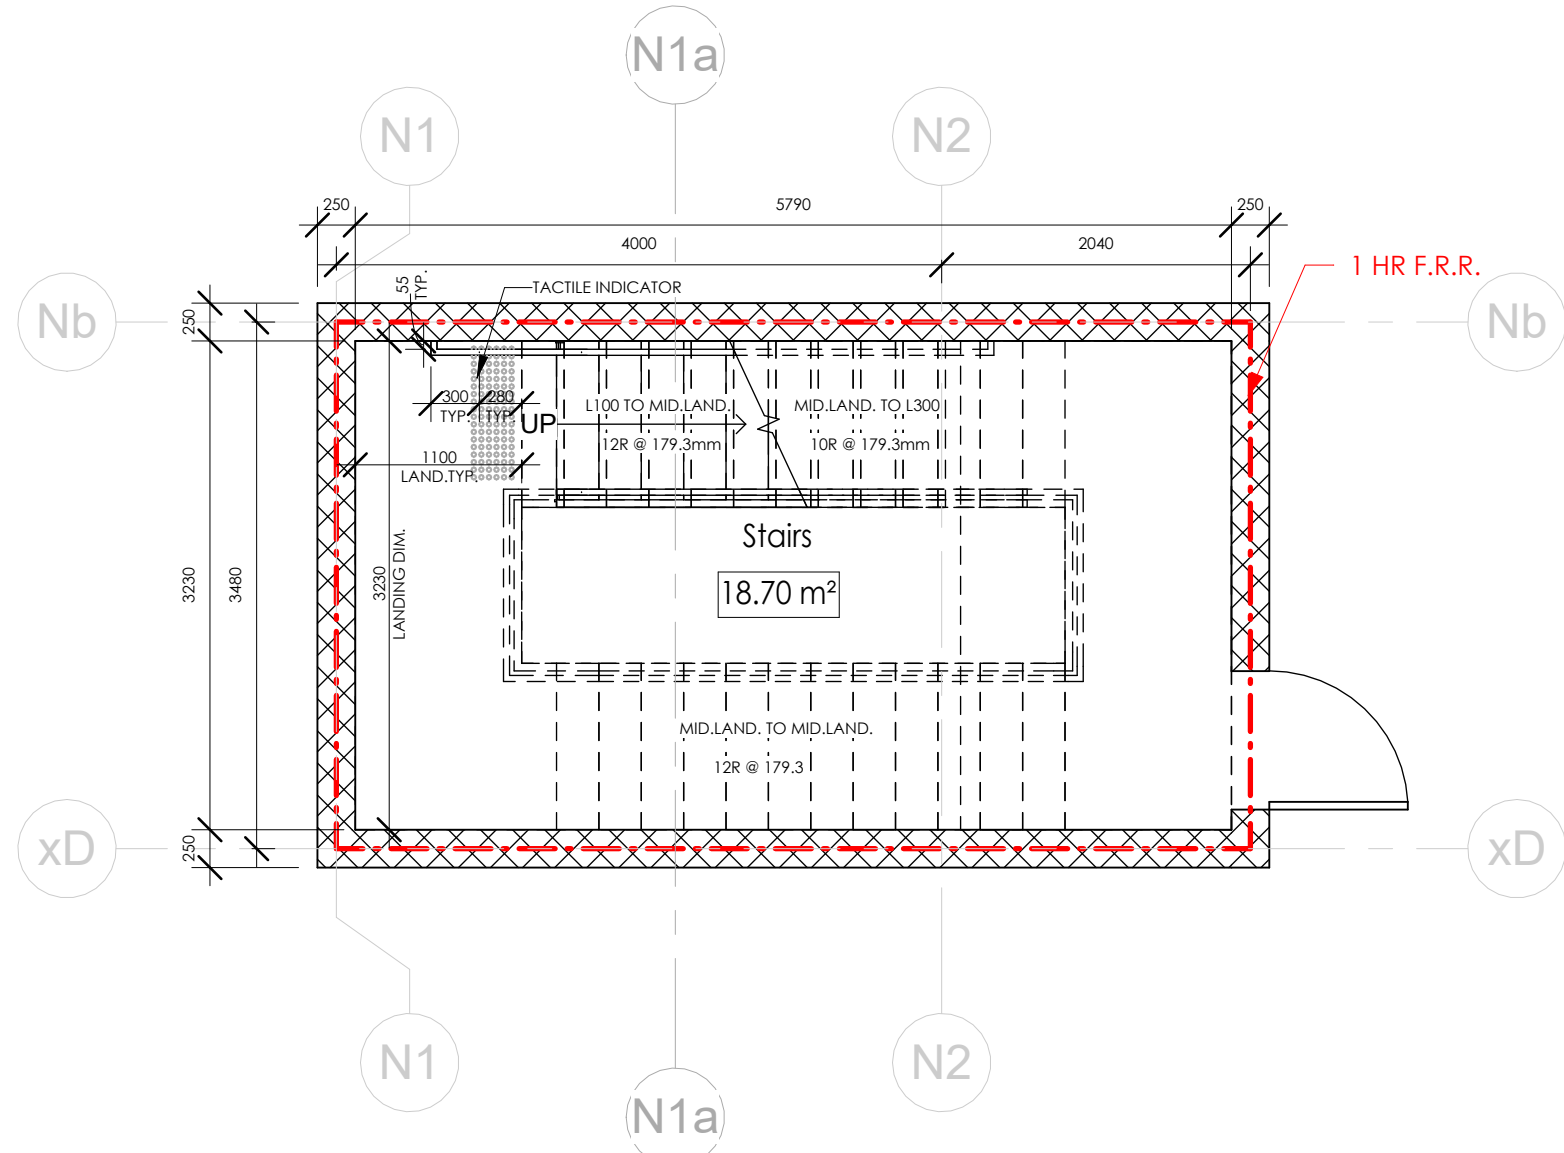


1 L100 Stair Plan
1 : 50

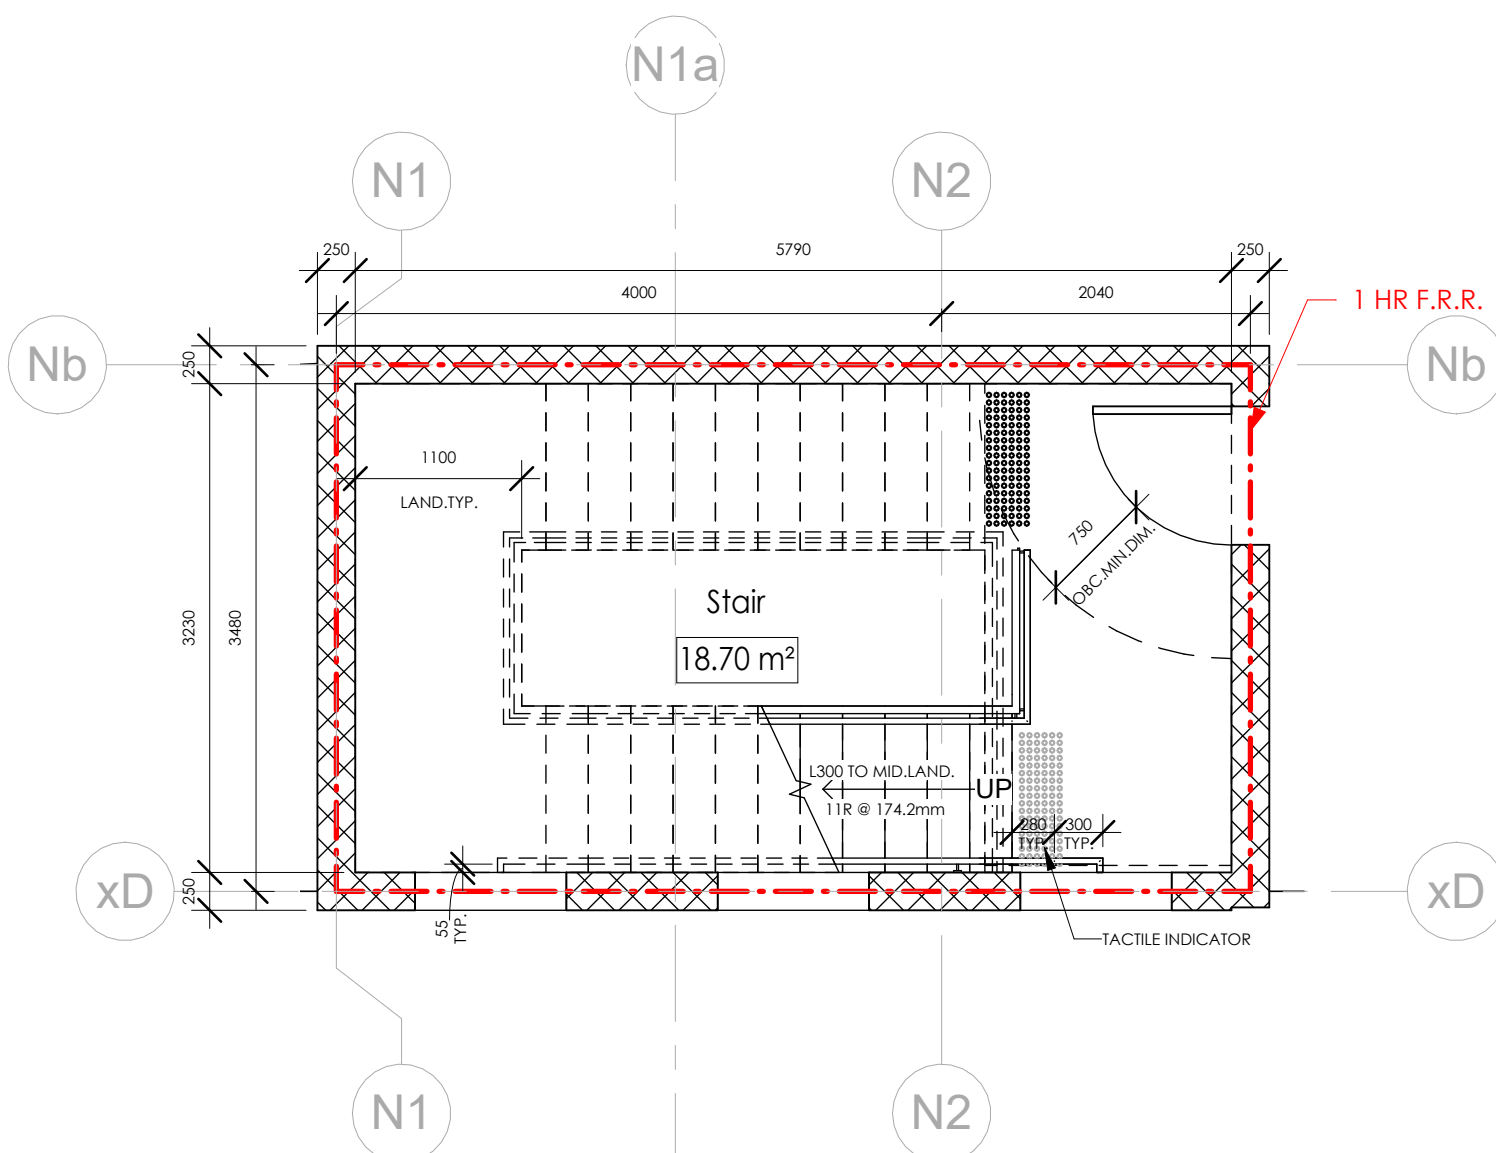


2 L300 Stair Plan
1 : 50

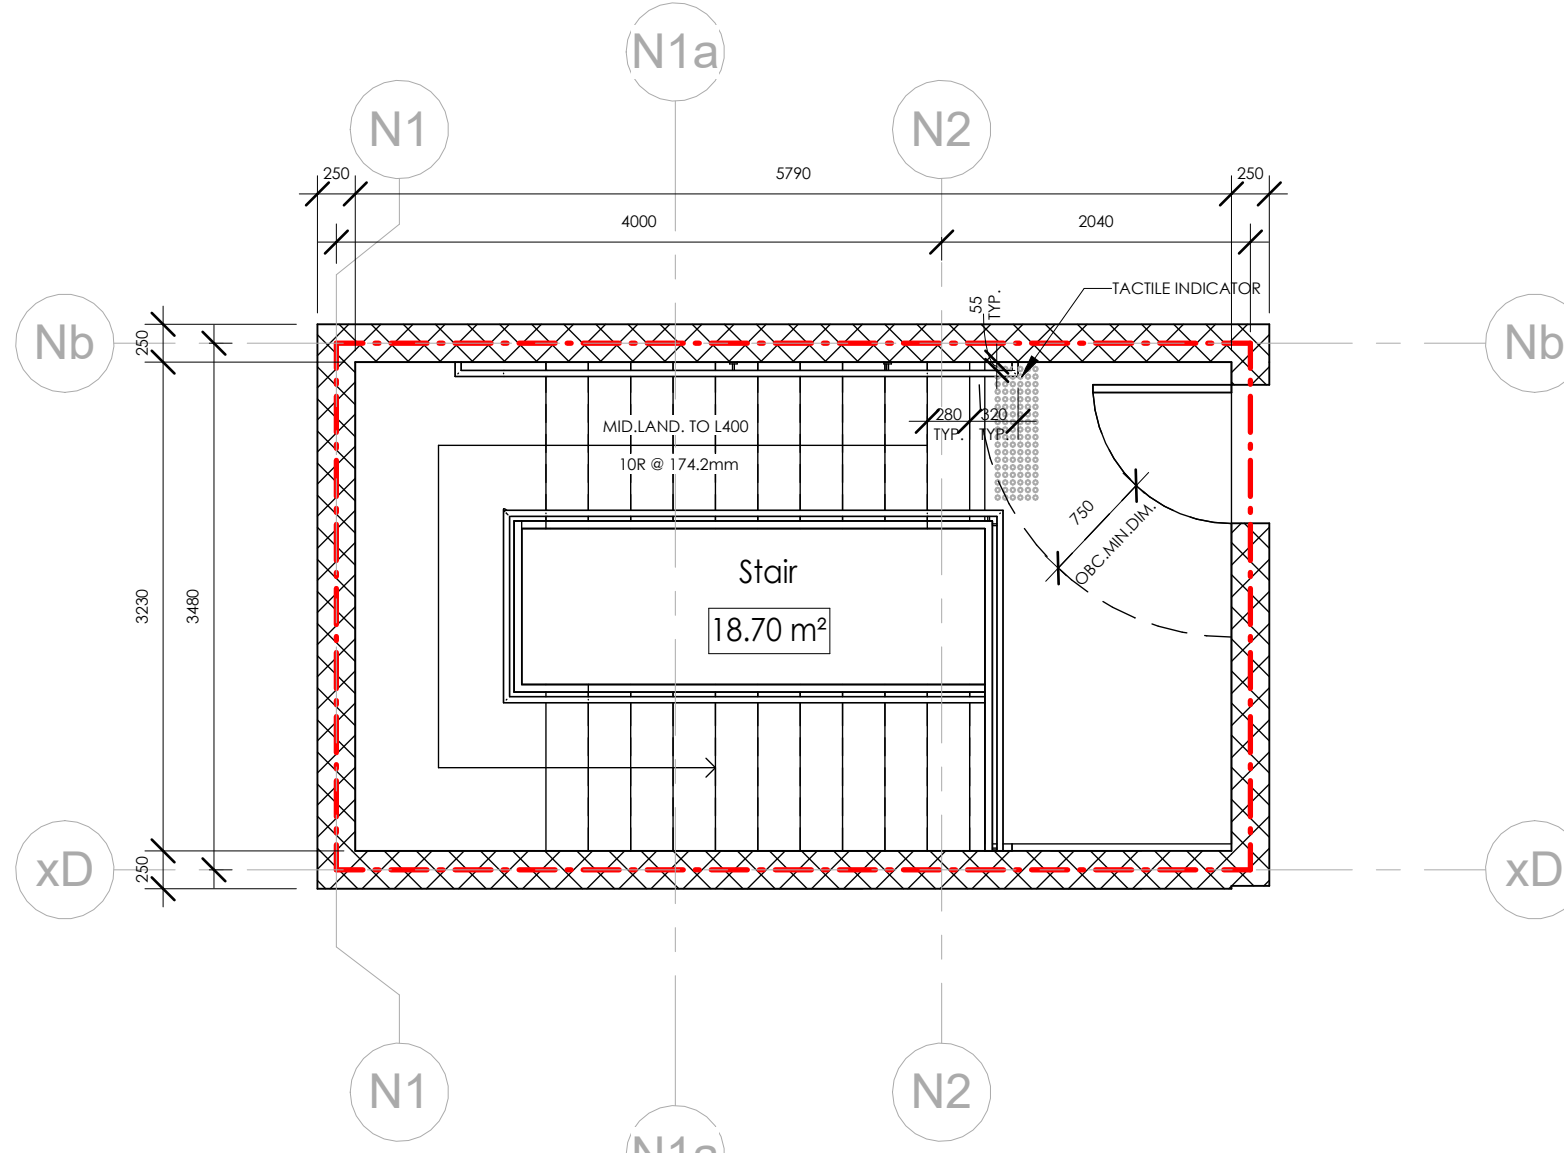

3 L400 Stair Plan
1 : 50

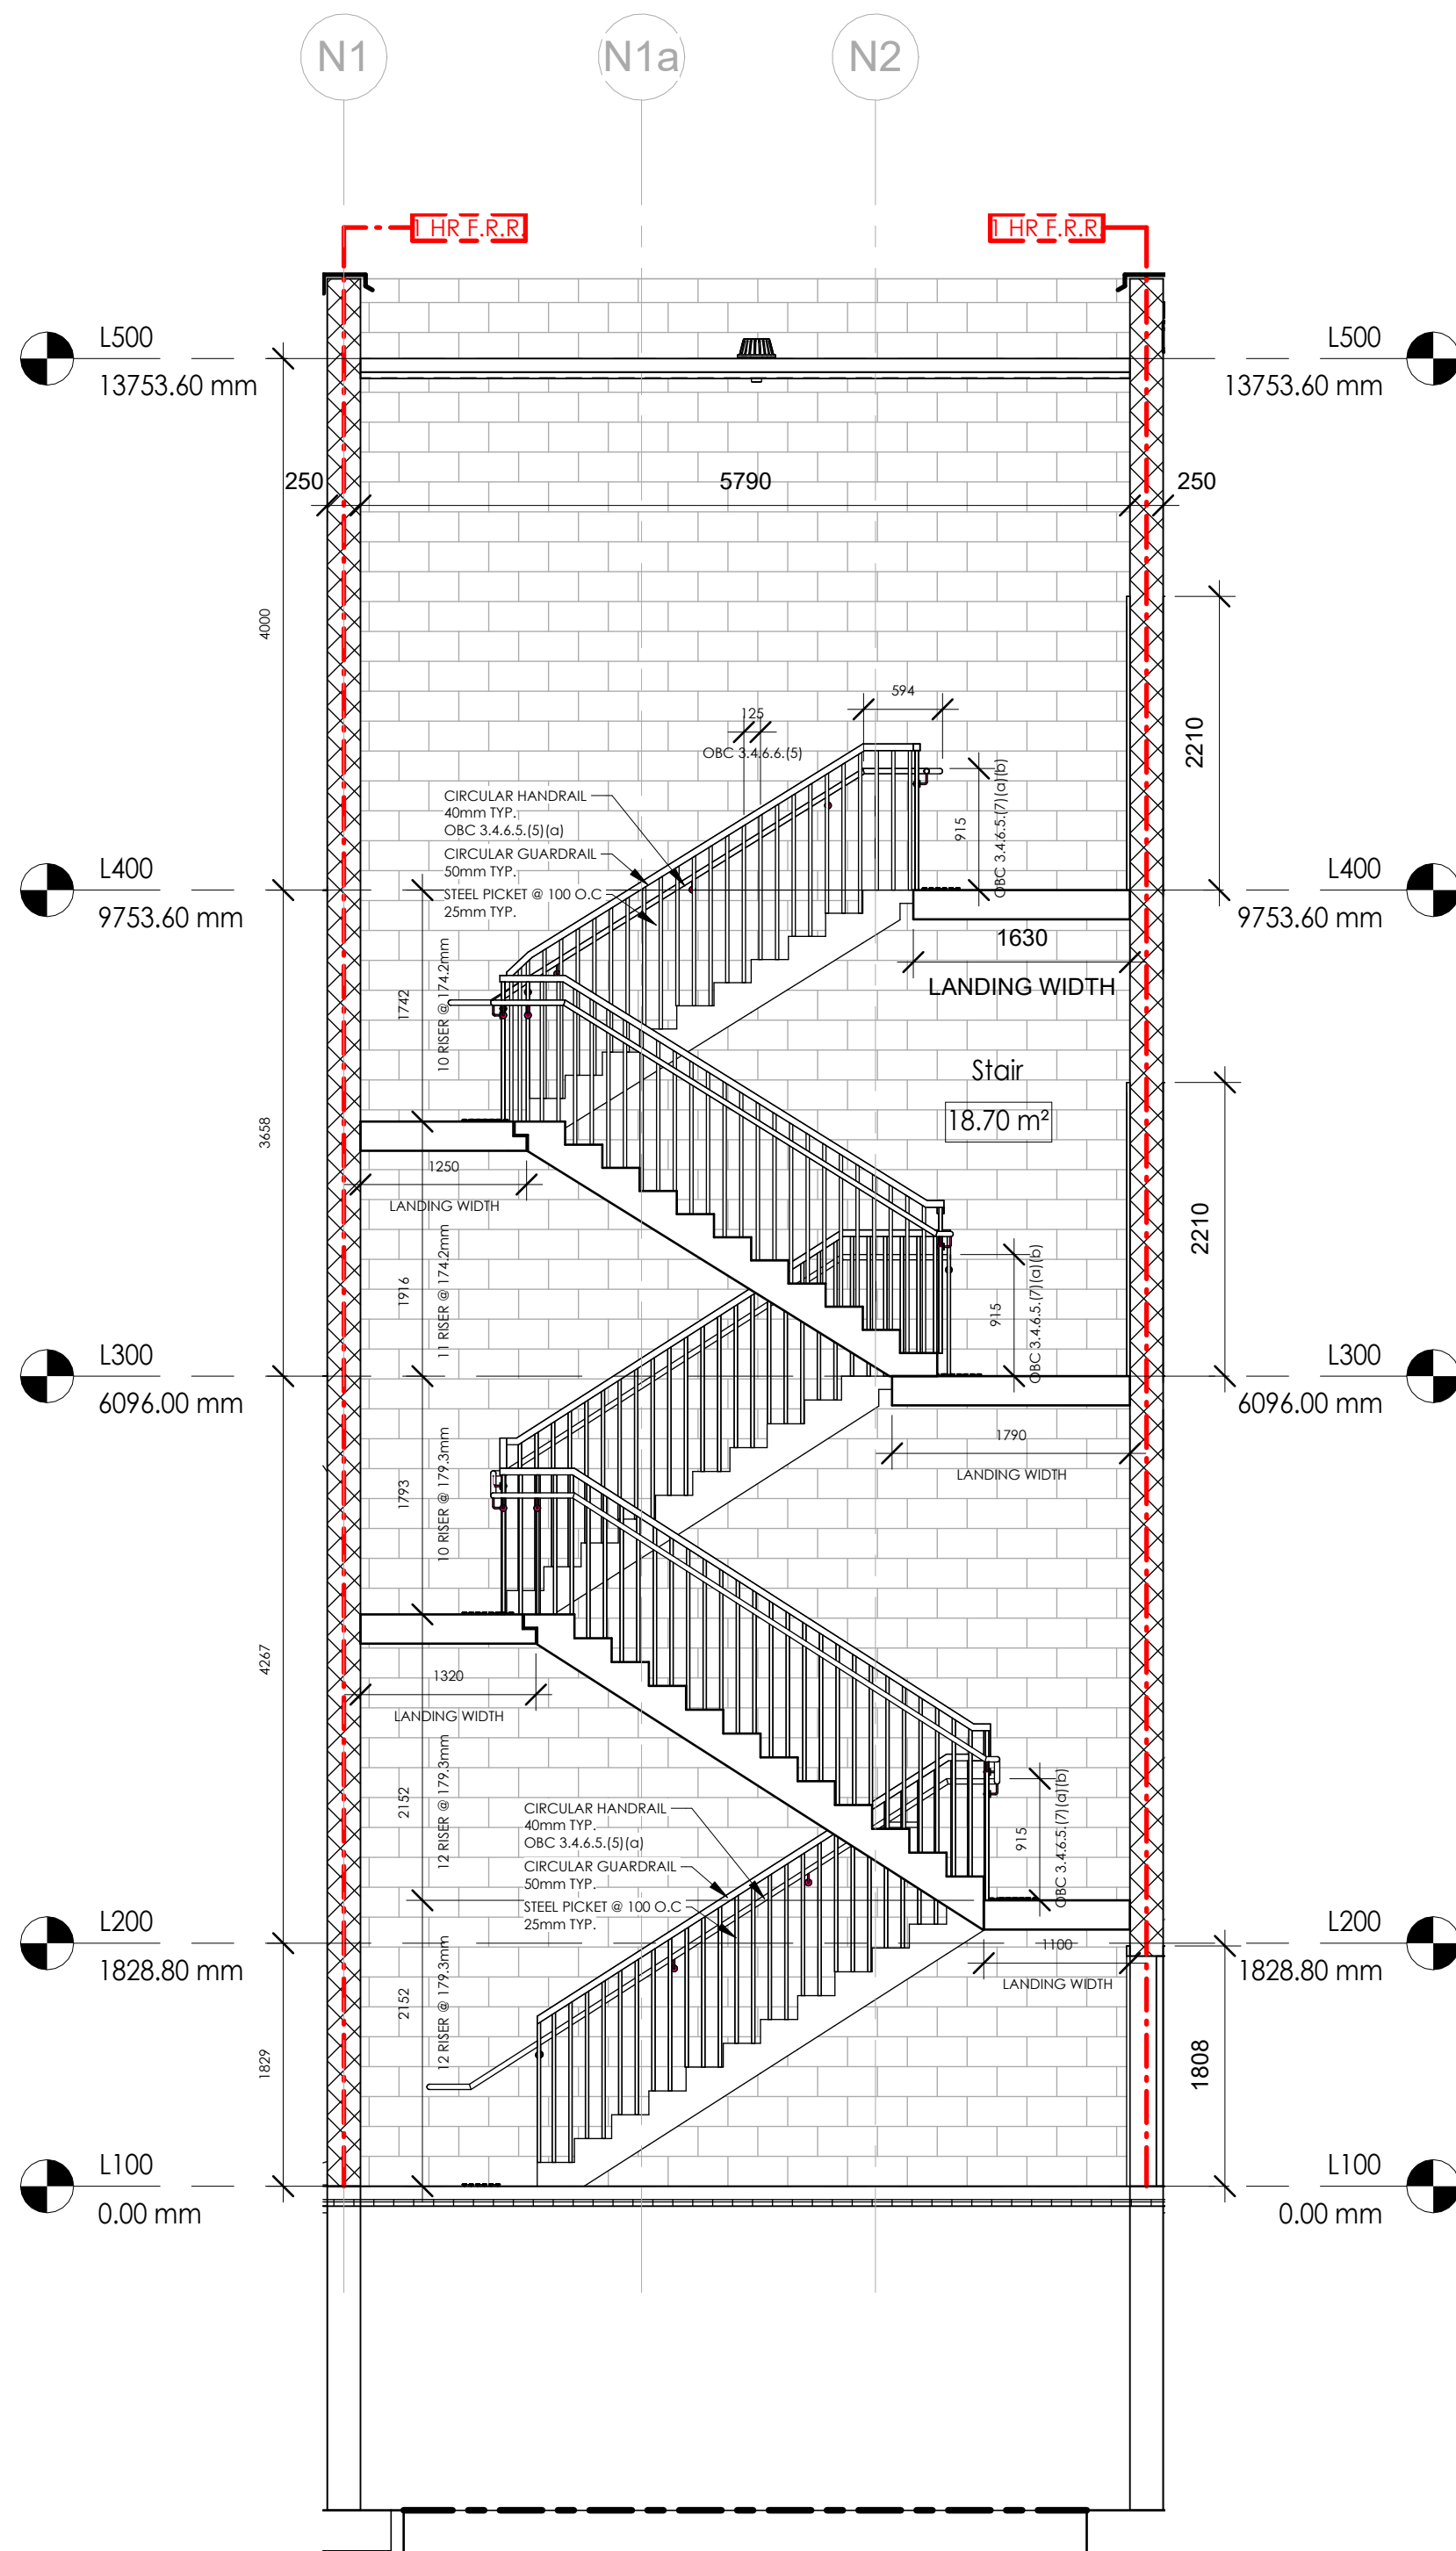


4 STAIR SECTION
1 : 50

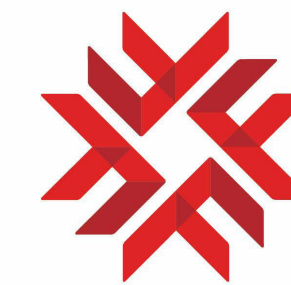

FANSHAW
DONALD J. SMITH
SCHOOL OF BUILDING
TECHNOLOGY

NORTH ARROW

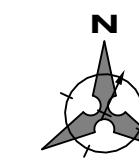

GENERAL NOTES

1. DO NOT SCALE DRAWINGS. WRITTEN DIMENSIONS SHALL HAVE PRECEDENCE OVER SCALED DIMENSIONS.
2. ALL WORK SHALL COMPLY WITH THE 2012 ONTARIO BUILDING CODE AND AMENDMENTS.
3. CONTRACTORS MUST CHECK AND VERIFY ALL DIMENSIONS AND SPECIFICATIONS AND REPORT ANY DISCREPANCIES TO THE ARCHITECT BEFORE PROCEEDINGS WITH THE WORK.
4. ALL CONTRACTORS AND SUB-CONTRACTORS SHALL HAVE A SET OF APPROVED CONSTRUCTION DOCUMENTS ON SITE AT ALL TIMES.
5. ALL DOCUMENTS REMAIN THE PROPERTY OF THE ARCHITECT. UNAUTHORIZED USE, MODIFICATION, AND/OR REPRODUCTION OF THESE DOCUMENTS IS PROHIBITED WITHOUT WRITTEN PERMISSION. THE CONTRACT DOCUMENTS WERE PREPARED BY THE CONSULTANT FOR THE ACCOUNT OF THE OWNER.
6. THE MATERIAL CONTAINED HEREIN REFLECTS THE CONSULTANTS BEST JUDGEMENT IN LIGHT OF THE INFORMATION AVAILABLE TO HIM/HER AT THE TIME OF PREPARATION. ANY USE WHICH A THIRD PARTY MAKES OF THE CONTRACT DOCUMENTS, OR ANY RELIANCE ON/OR DECISIONS TO BE MADE BASED ON THEM ARE THE RESPONSIBILITY OF SUCH THIRD PARTIES.
7. THE CONSULTANT ACCEPTS NO RESPONSIBILITY FOR DAMAGES, IF ANY, SUFFERED BY ANY THIRD PARTY AS A RESULT OF DECISIONS MADE OR ACTIONS BASED ON THE CONTRACT DOCUMENTS.

PRELIMINARY
NOT FOR CONSTRUCTION







PROJECT TITLE
THE EDEN PROJECT

CLIENT:
Eden Project
PROJECT ADDRESS
555 McCormick Street

DRAWING TITLE
STAIR PLANS & SECTION

CHECKED GG | DRAWN AFNM | DATE 15/08/25

PROJECT No. 0001 | DRAWING A6.1

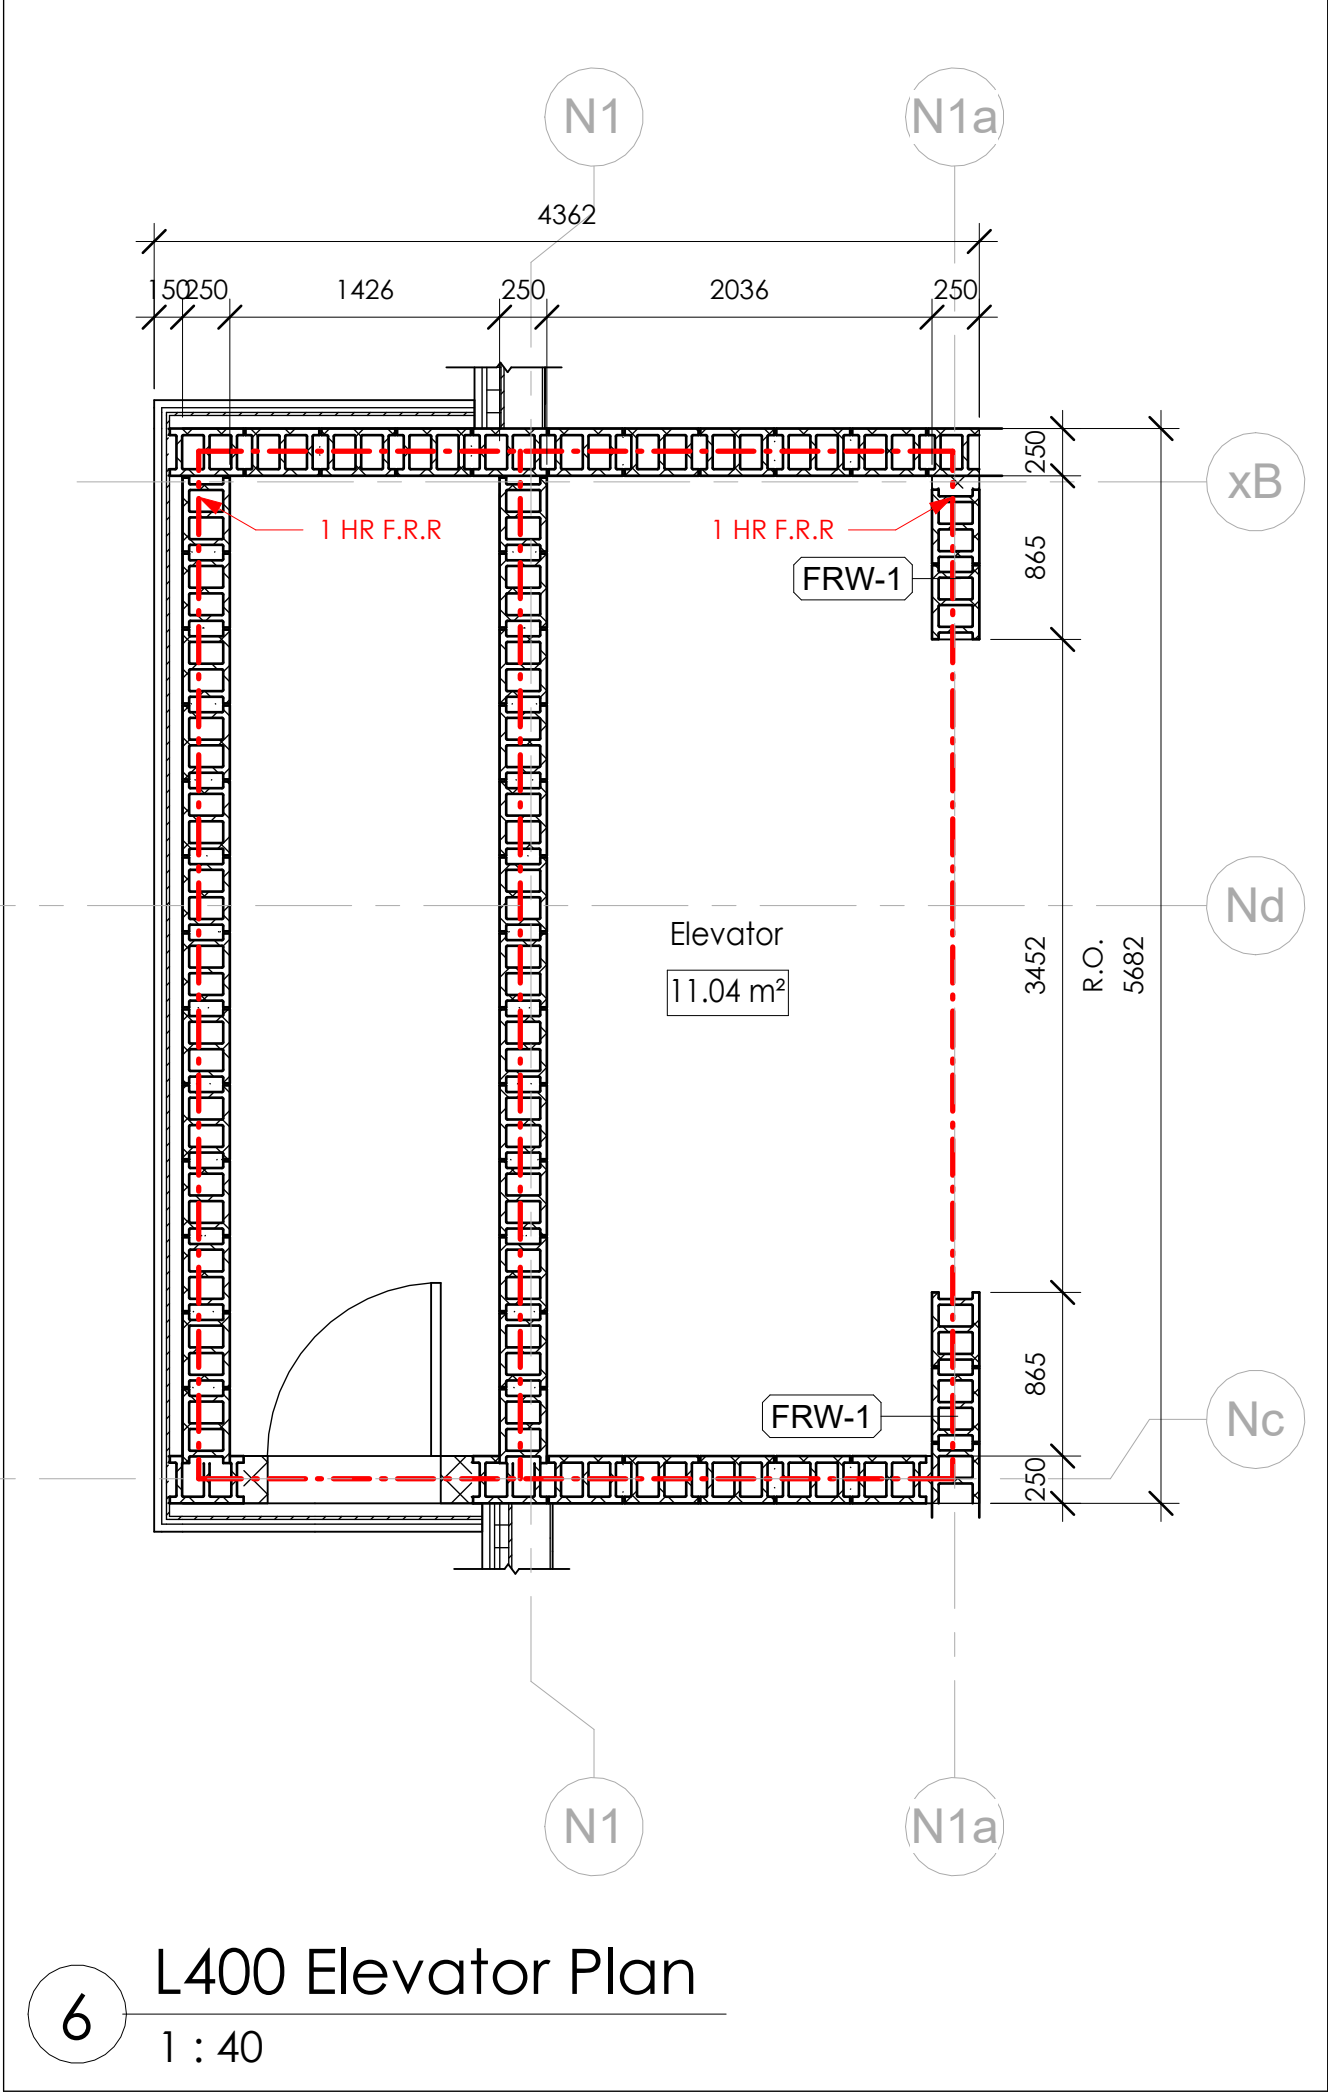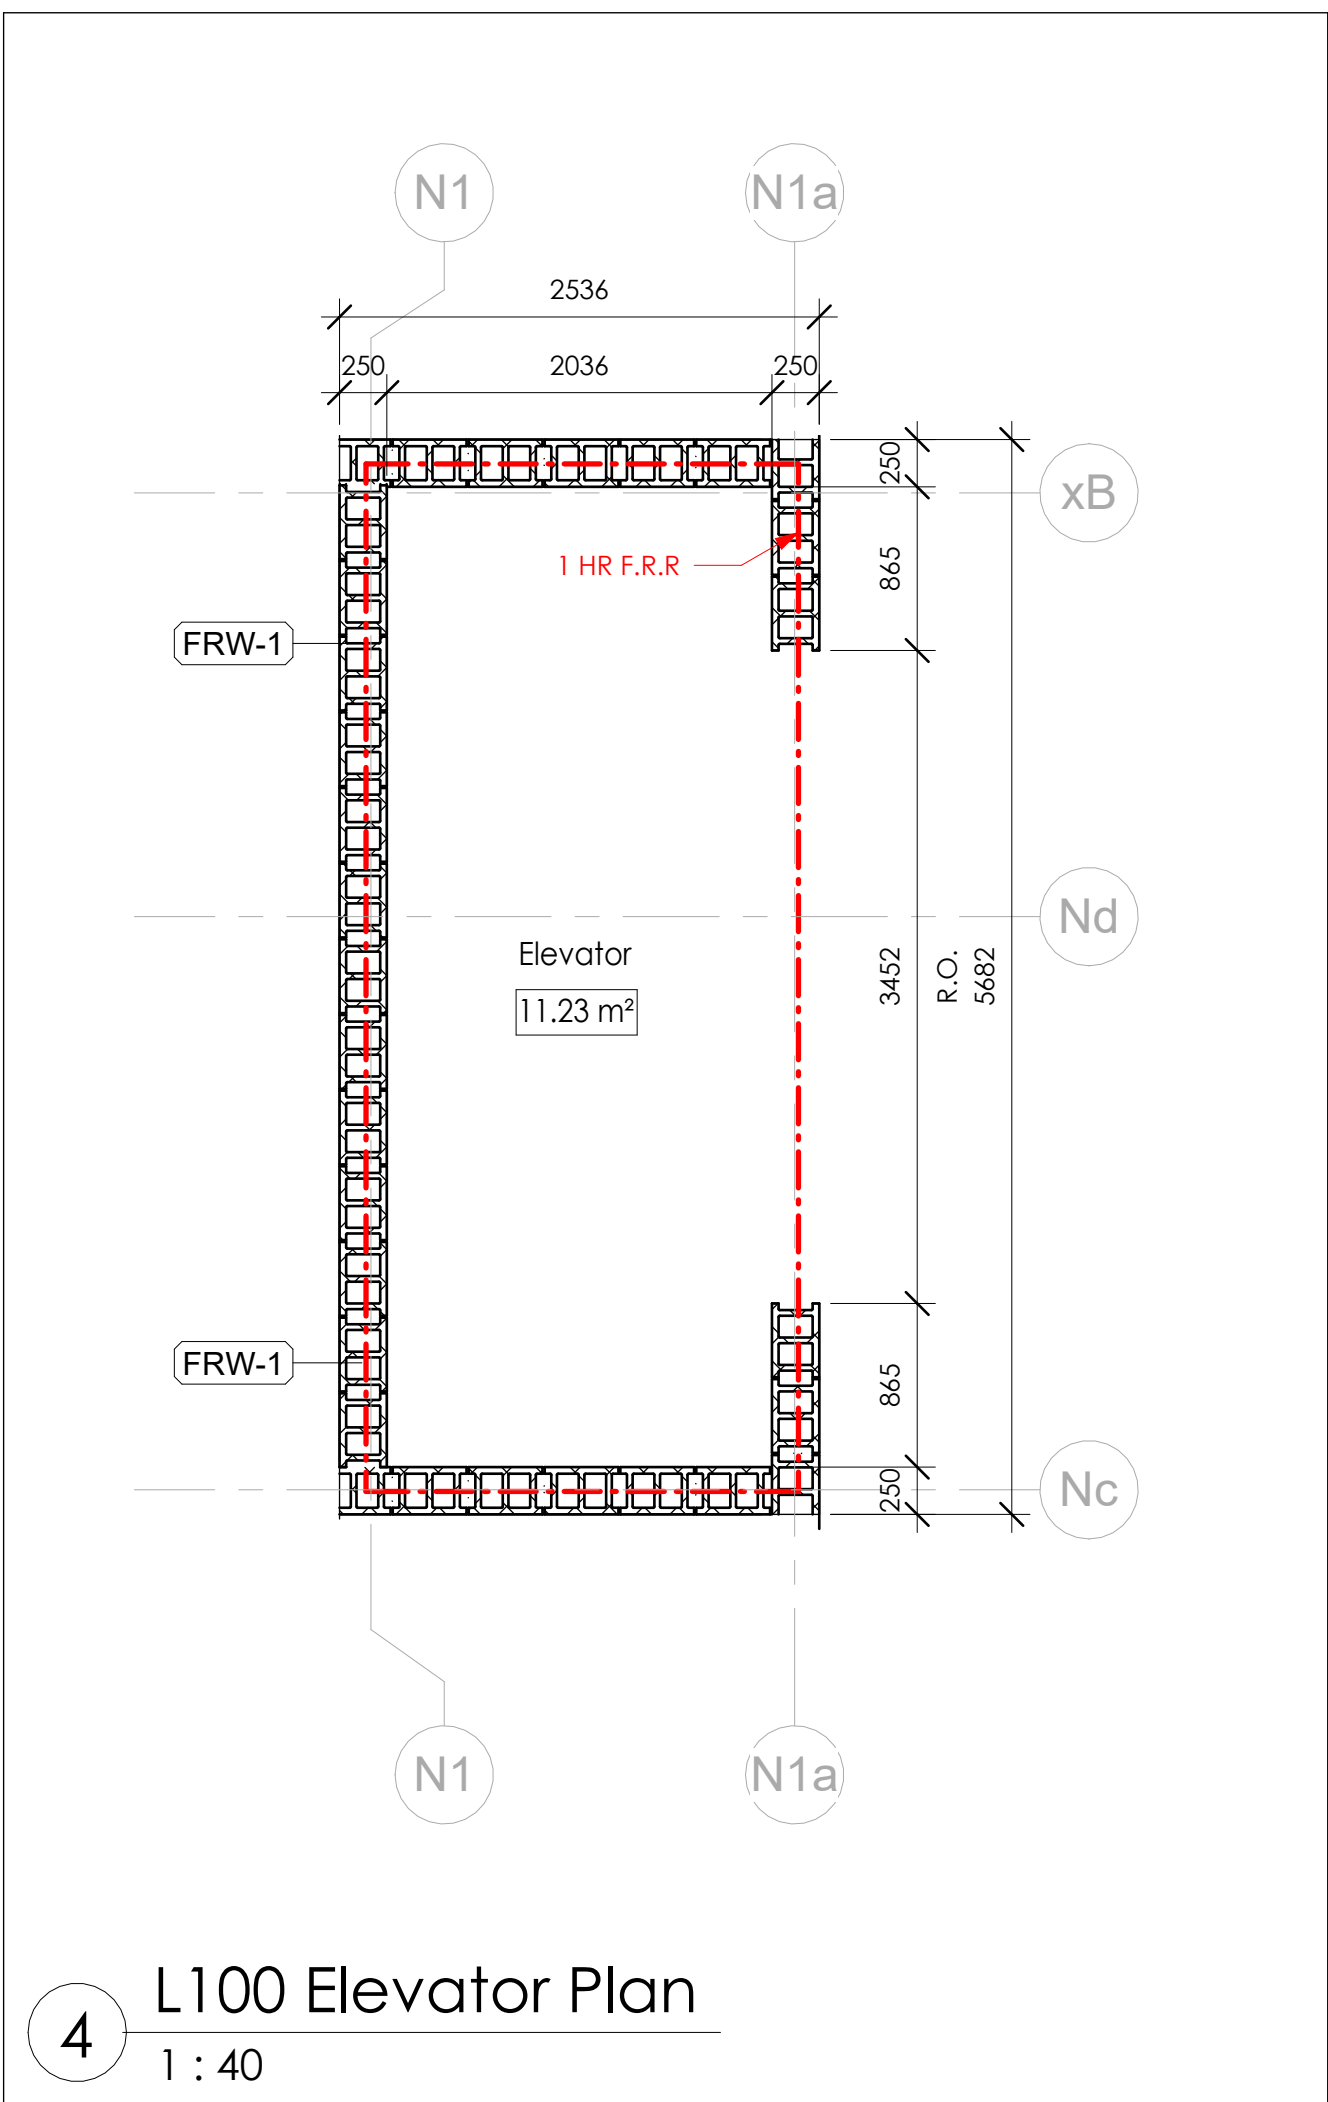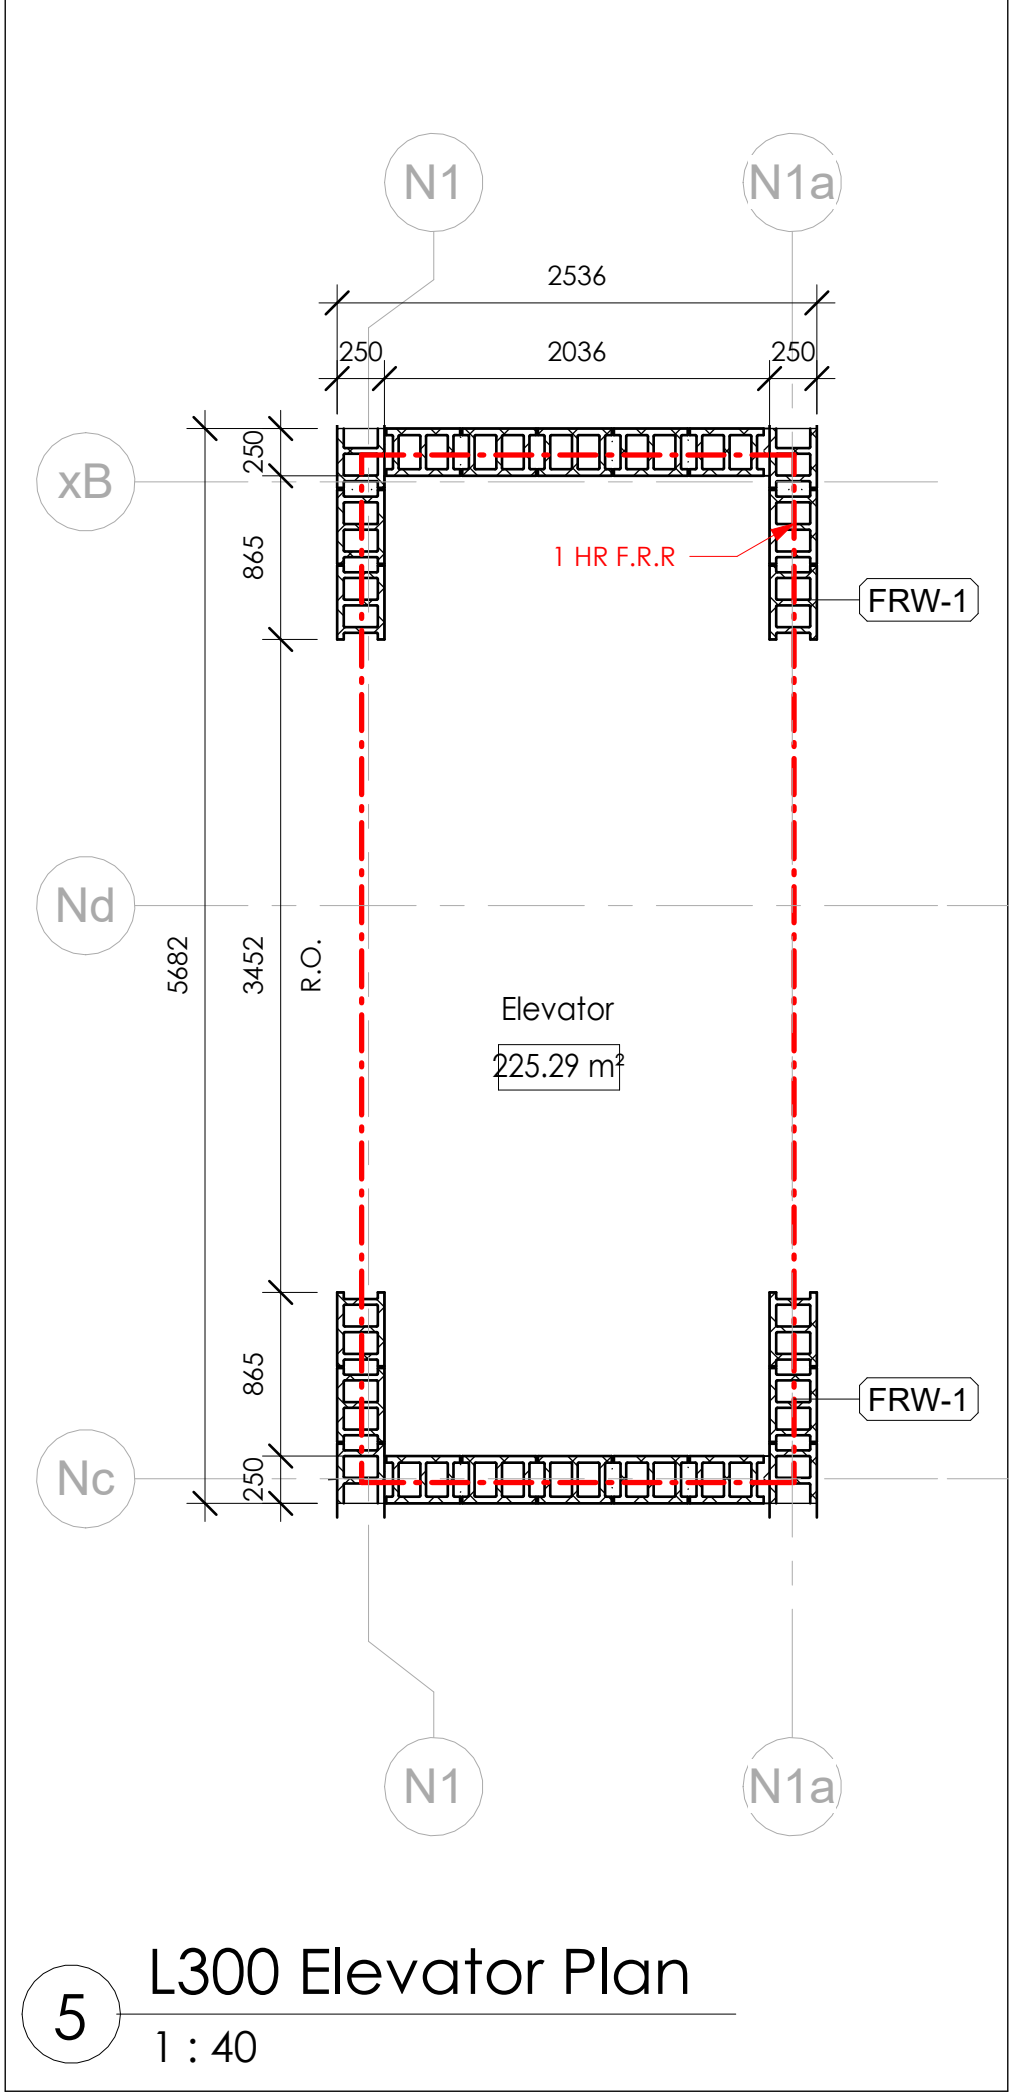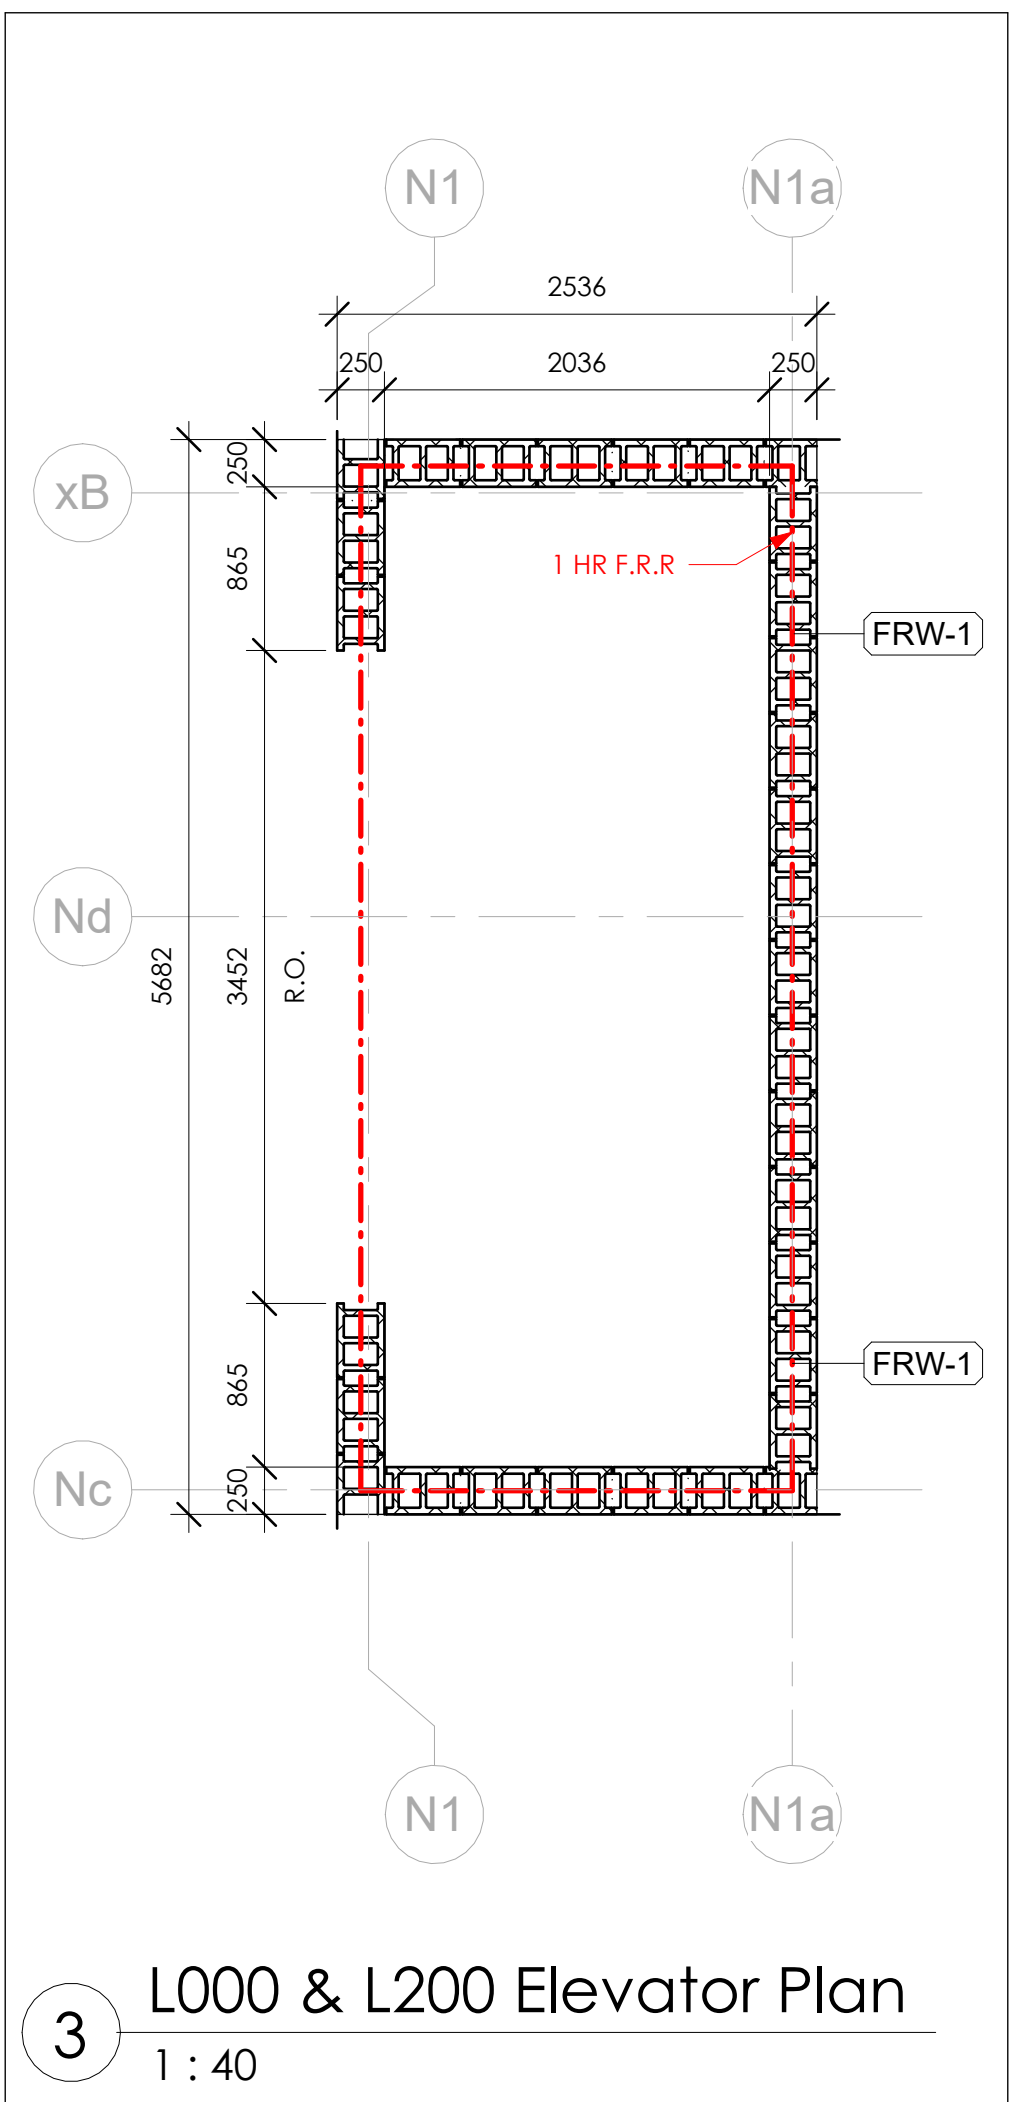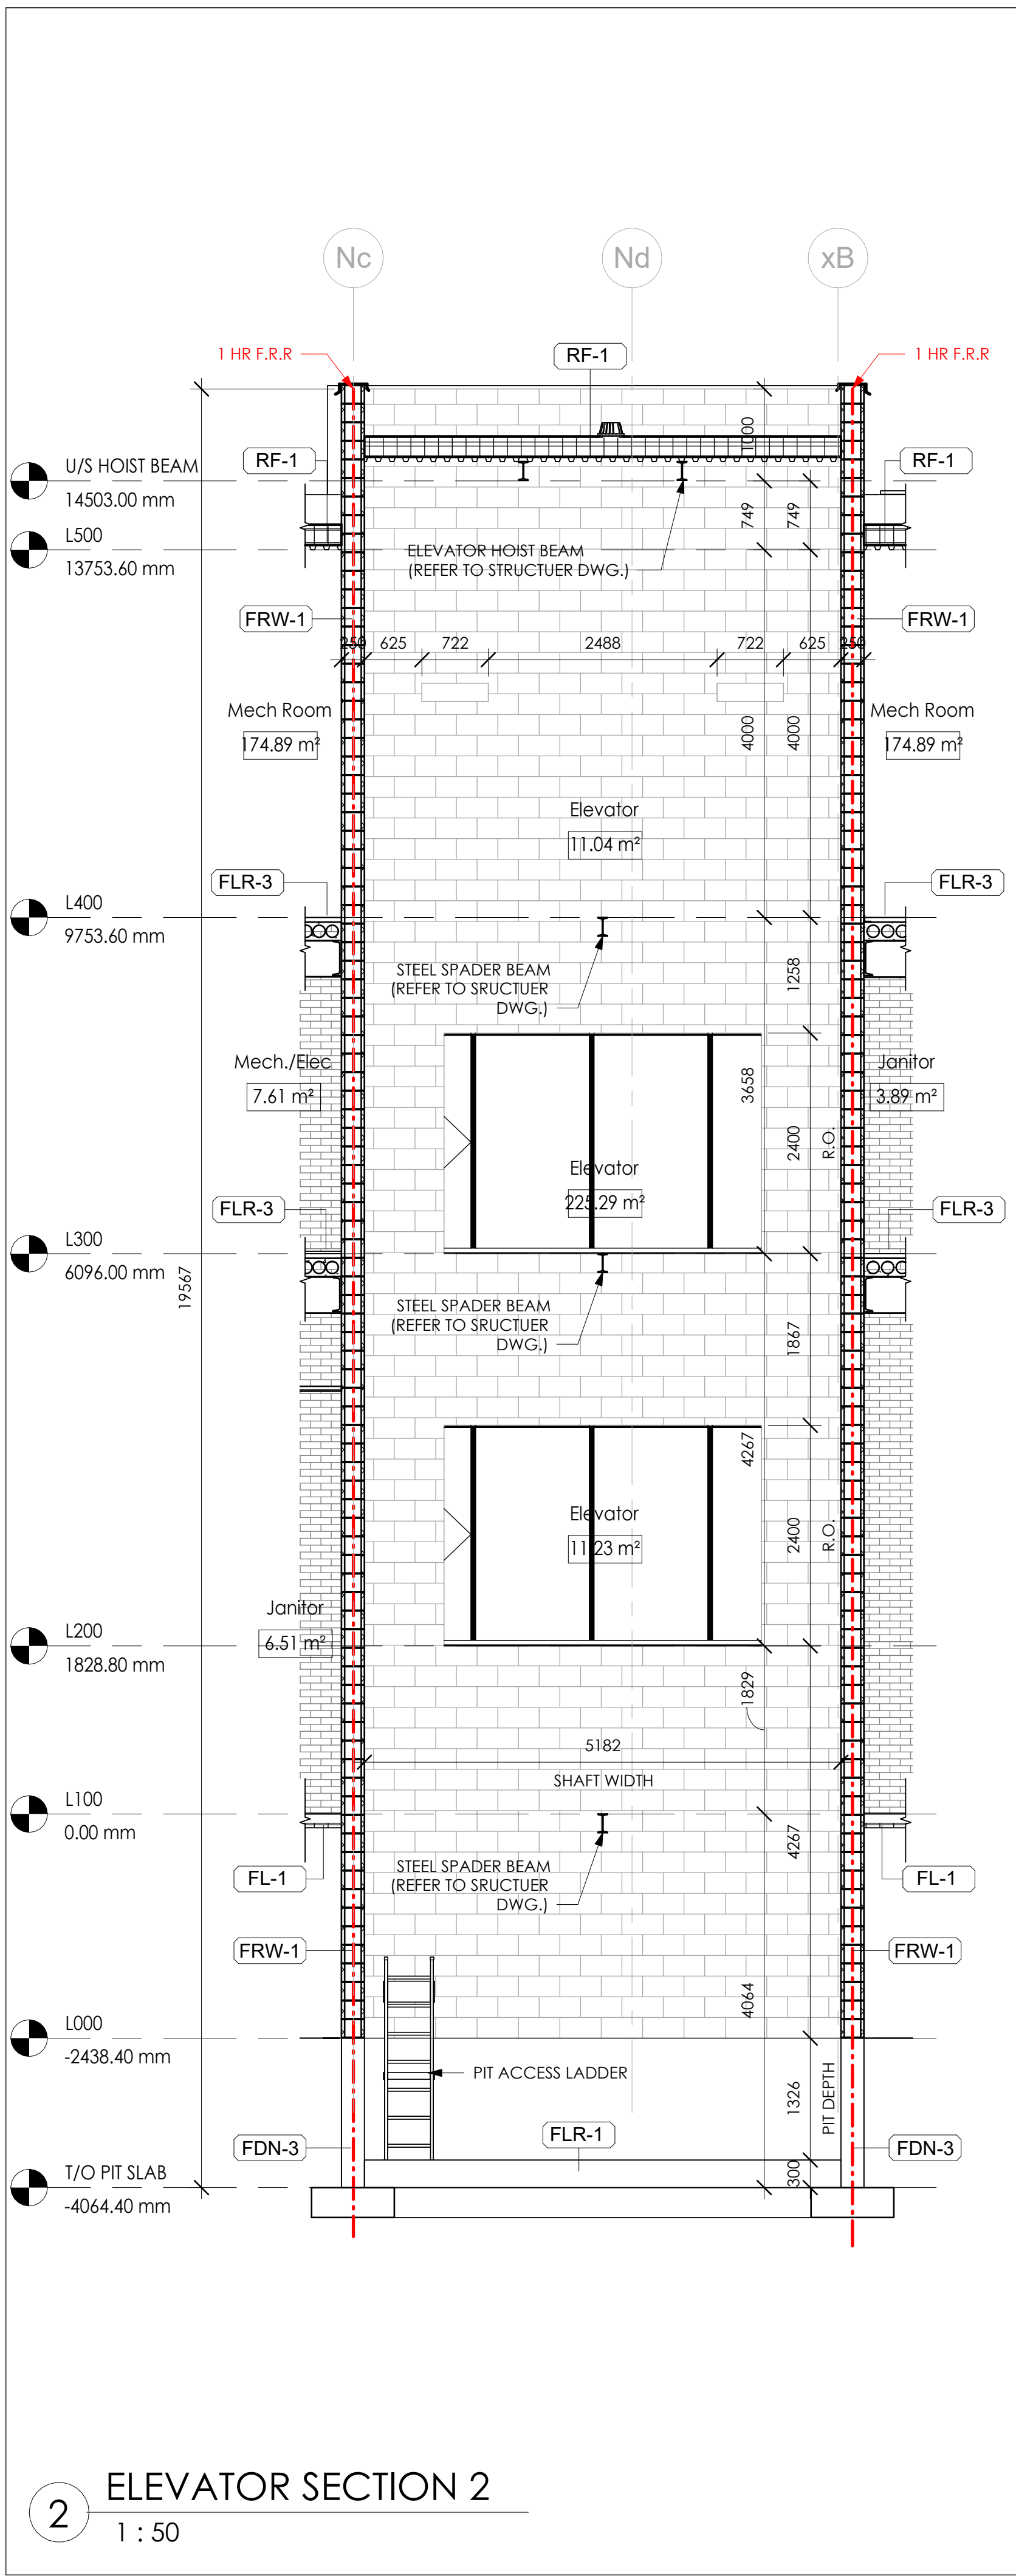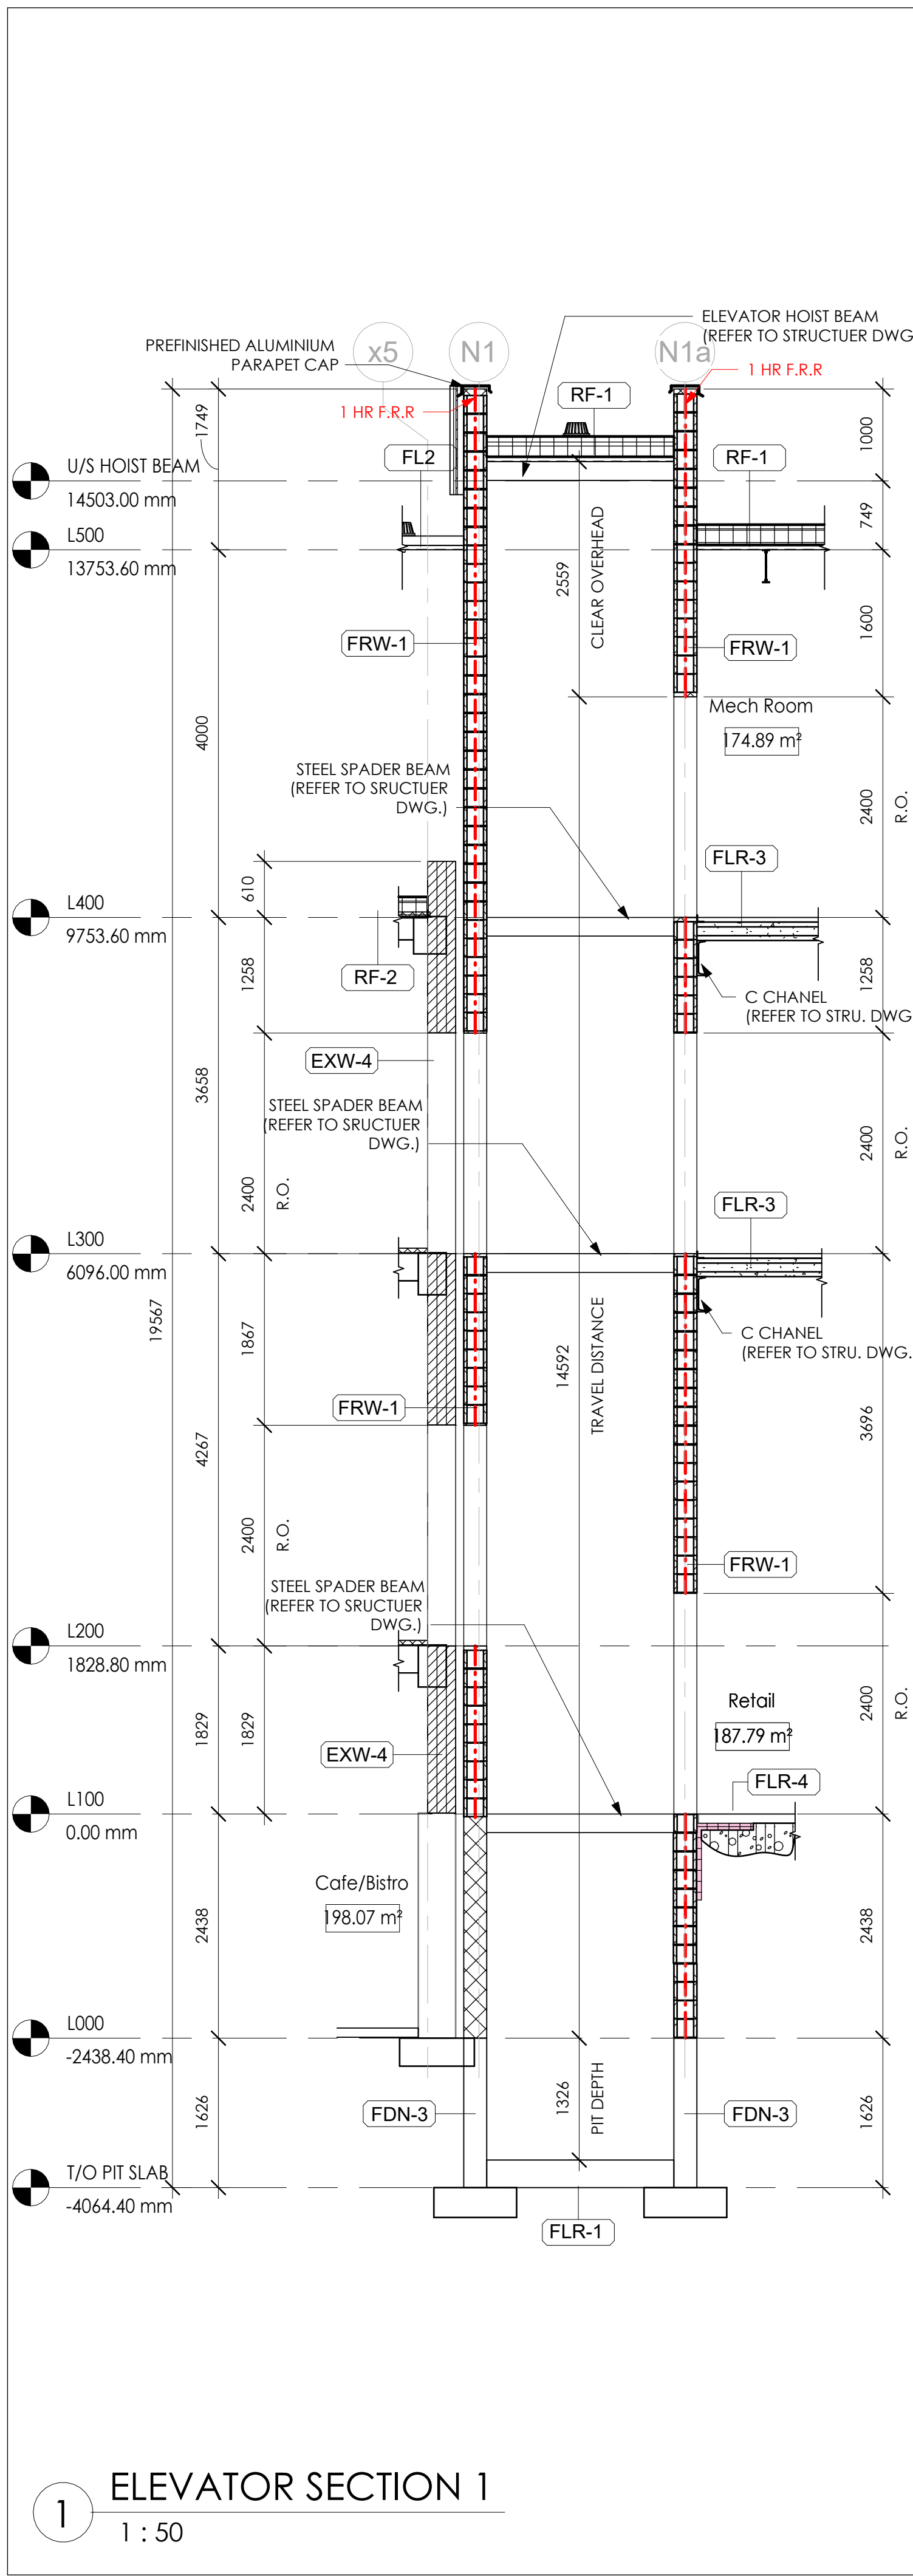

NORTH ARROW

GENERAL NOTES

- DO NOT SCALE DRAWINGS. WRITTEN DIMENSIONS SHALL HAVE PRECEDENCE OVER SCALED DIMENSIONS.
- ALL WORK SHALL COMPLY WITH THE 2012 ONTARIO BUILDING CODE AND AMENDMENTS.
- CONTRACTORS MUST CHECK AND VERIFY ALL DIMENSIONS AND SPECIFICATIONS AND REPORT ANY DISCREPANCIES TO THE ARCHITECT BEFORE PROCEEDING WITH THE WORK.
- ALL CONTRACTORS AND SUB-CONTRACTORS SHALL HAVE A SET OF APPROVED CONSTRUCTION DOCUMENTS ON SITE AT ALL TIMES.
- ALL DOCUMENTS REMAIN THE PROPERTY OF THE ARCHITECT. UNAUTHORIZED USE, MODIFICATION, AND/OR REPRODUCTION OF THESE DOCUMENTS IS PROHIBITED WITHOUT WRITTEN PERMISSION. THE CONTRACT DOCUMENTS WERE PREPARED BY THE CONSULTANT FOR THE ACCOUNT OF THE OWNER.
- THE MATERIAL CONTAINED HEREIN REFLECTS THE CONSULTANT'S BEST JUDGMENT IN LIGHT OF THE INFORMATION AVAILABLE TO HIM/HER AT THE TIME OF PREPARATION. ANY USE WHICH A THIRD PARTY MAKES OF THE CONTRACT DOCUMENTS, OR ANY RELIANCE ON OR DECISIONS TO BE MADE BASED ON THEM ARE THE RESPONSIBILITY OF SUCH THIRD PARTIES.
- THE CONSULTANT ACCEPTS NO RESPONSIBILITY FOR DAMAGES, IF ANY, SUFFERED BY ANY THIRD PARTY AS A RESULT OF DECISIONS MADE OR ACTIONS BASED ON THE CONTRACT DOCUMENTS.

PROJECT TITLE

THE EDEN PROJECT

CLIENT:

Eden Project

PROJECT ADDRESS


555 McCormick Street

DRAWING TITLE


ELEVATOR PLANS & SECTIONS

CHECKED	DRAWN	DATE
GG	AFNM	15/08/25


0001	A6.2
PROJECT No.	DRAWING

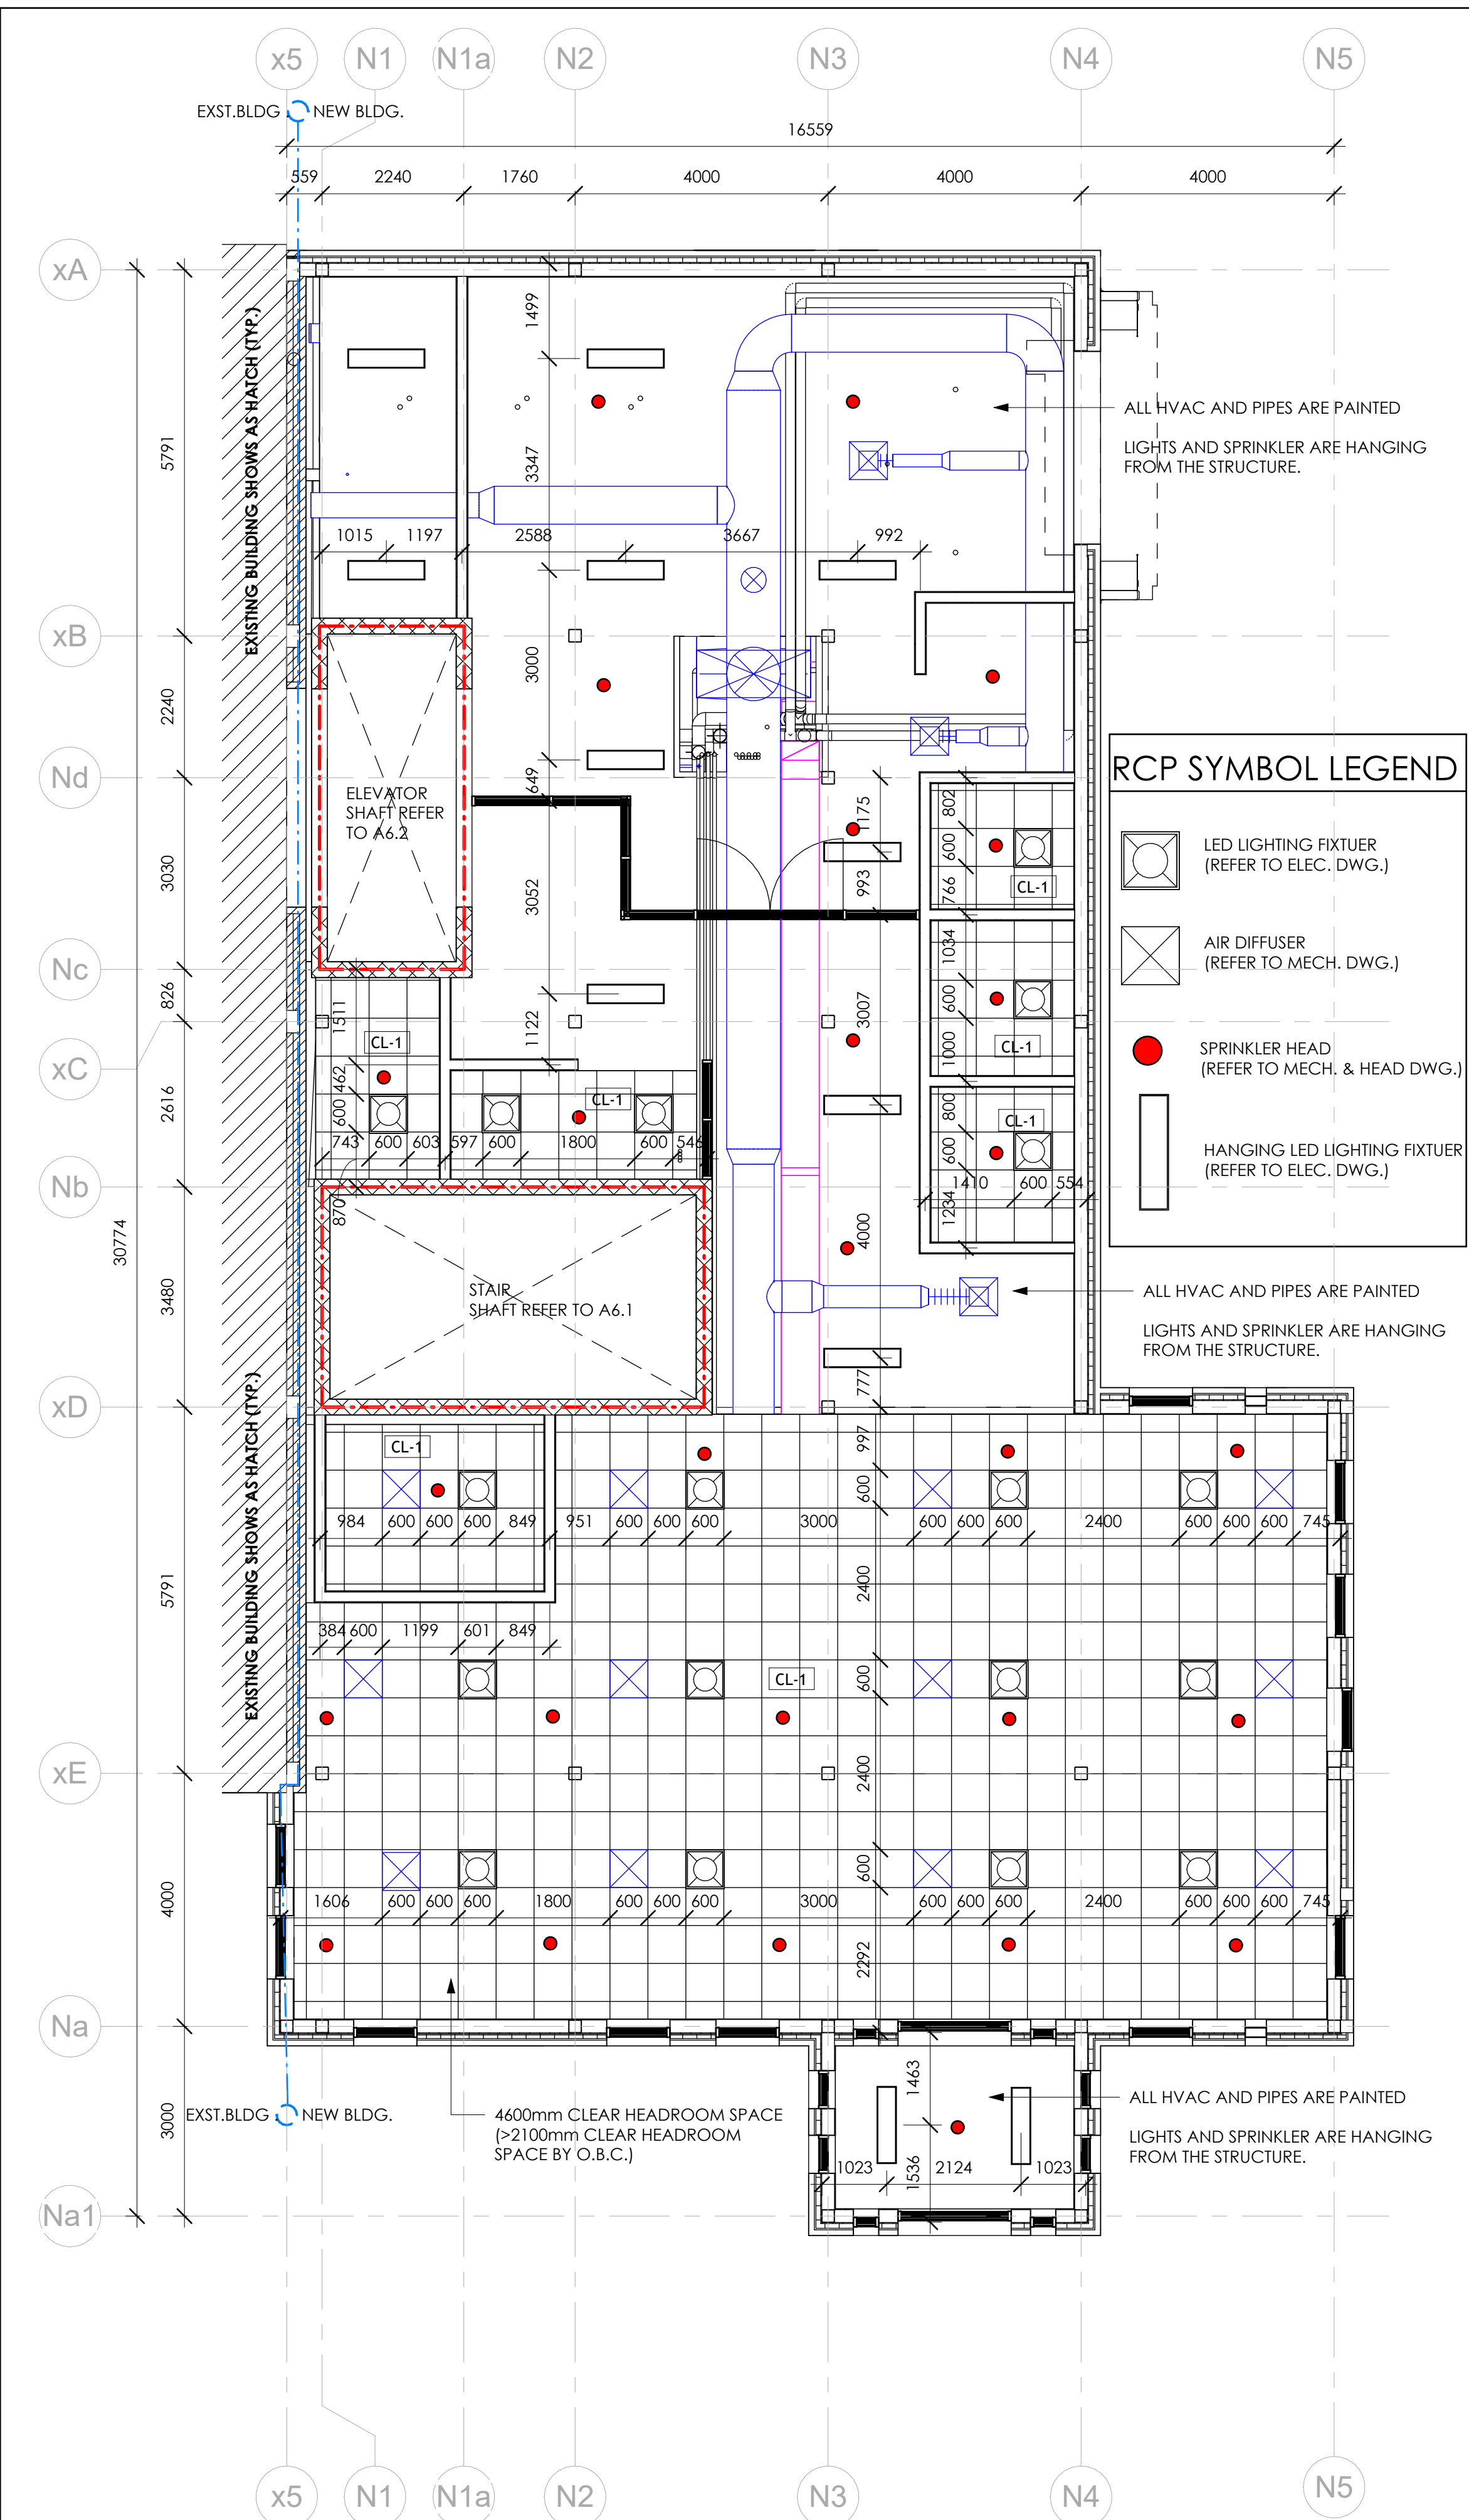

1 L100 ENLARGED R.C.P. MARKET PLAN
1:75

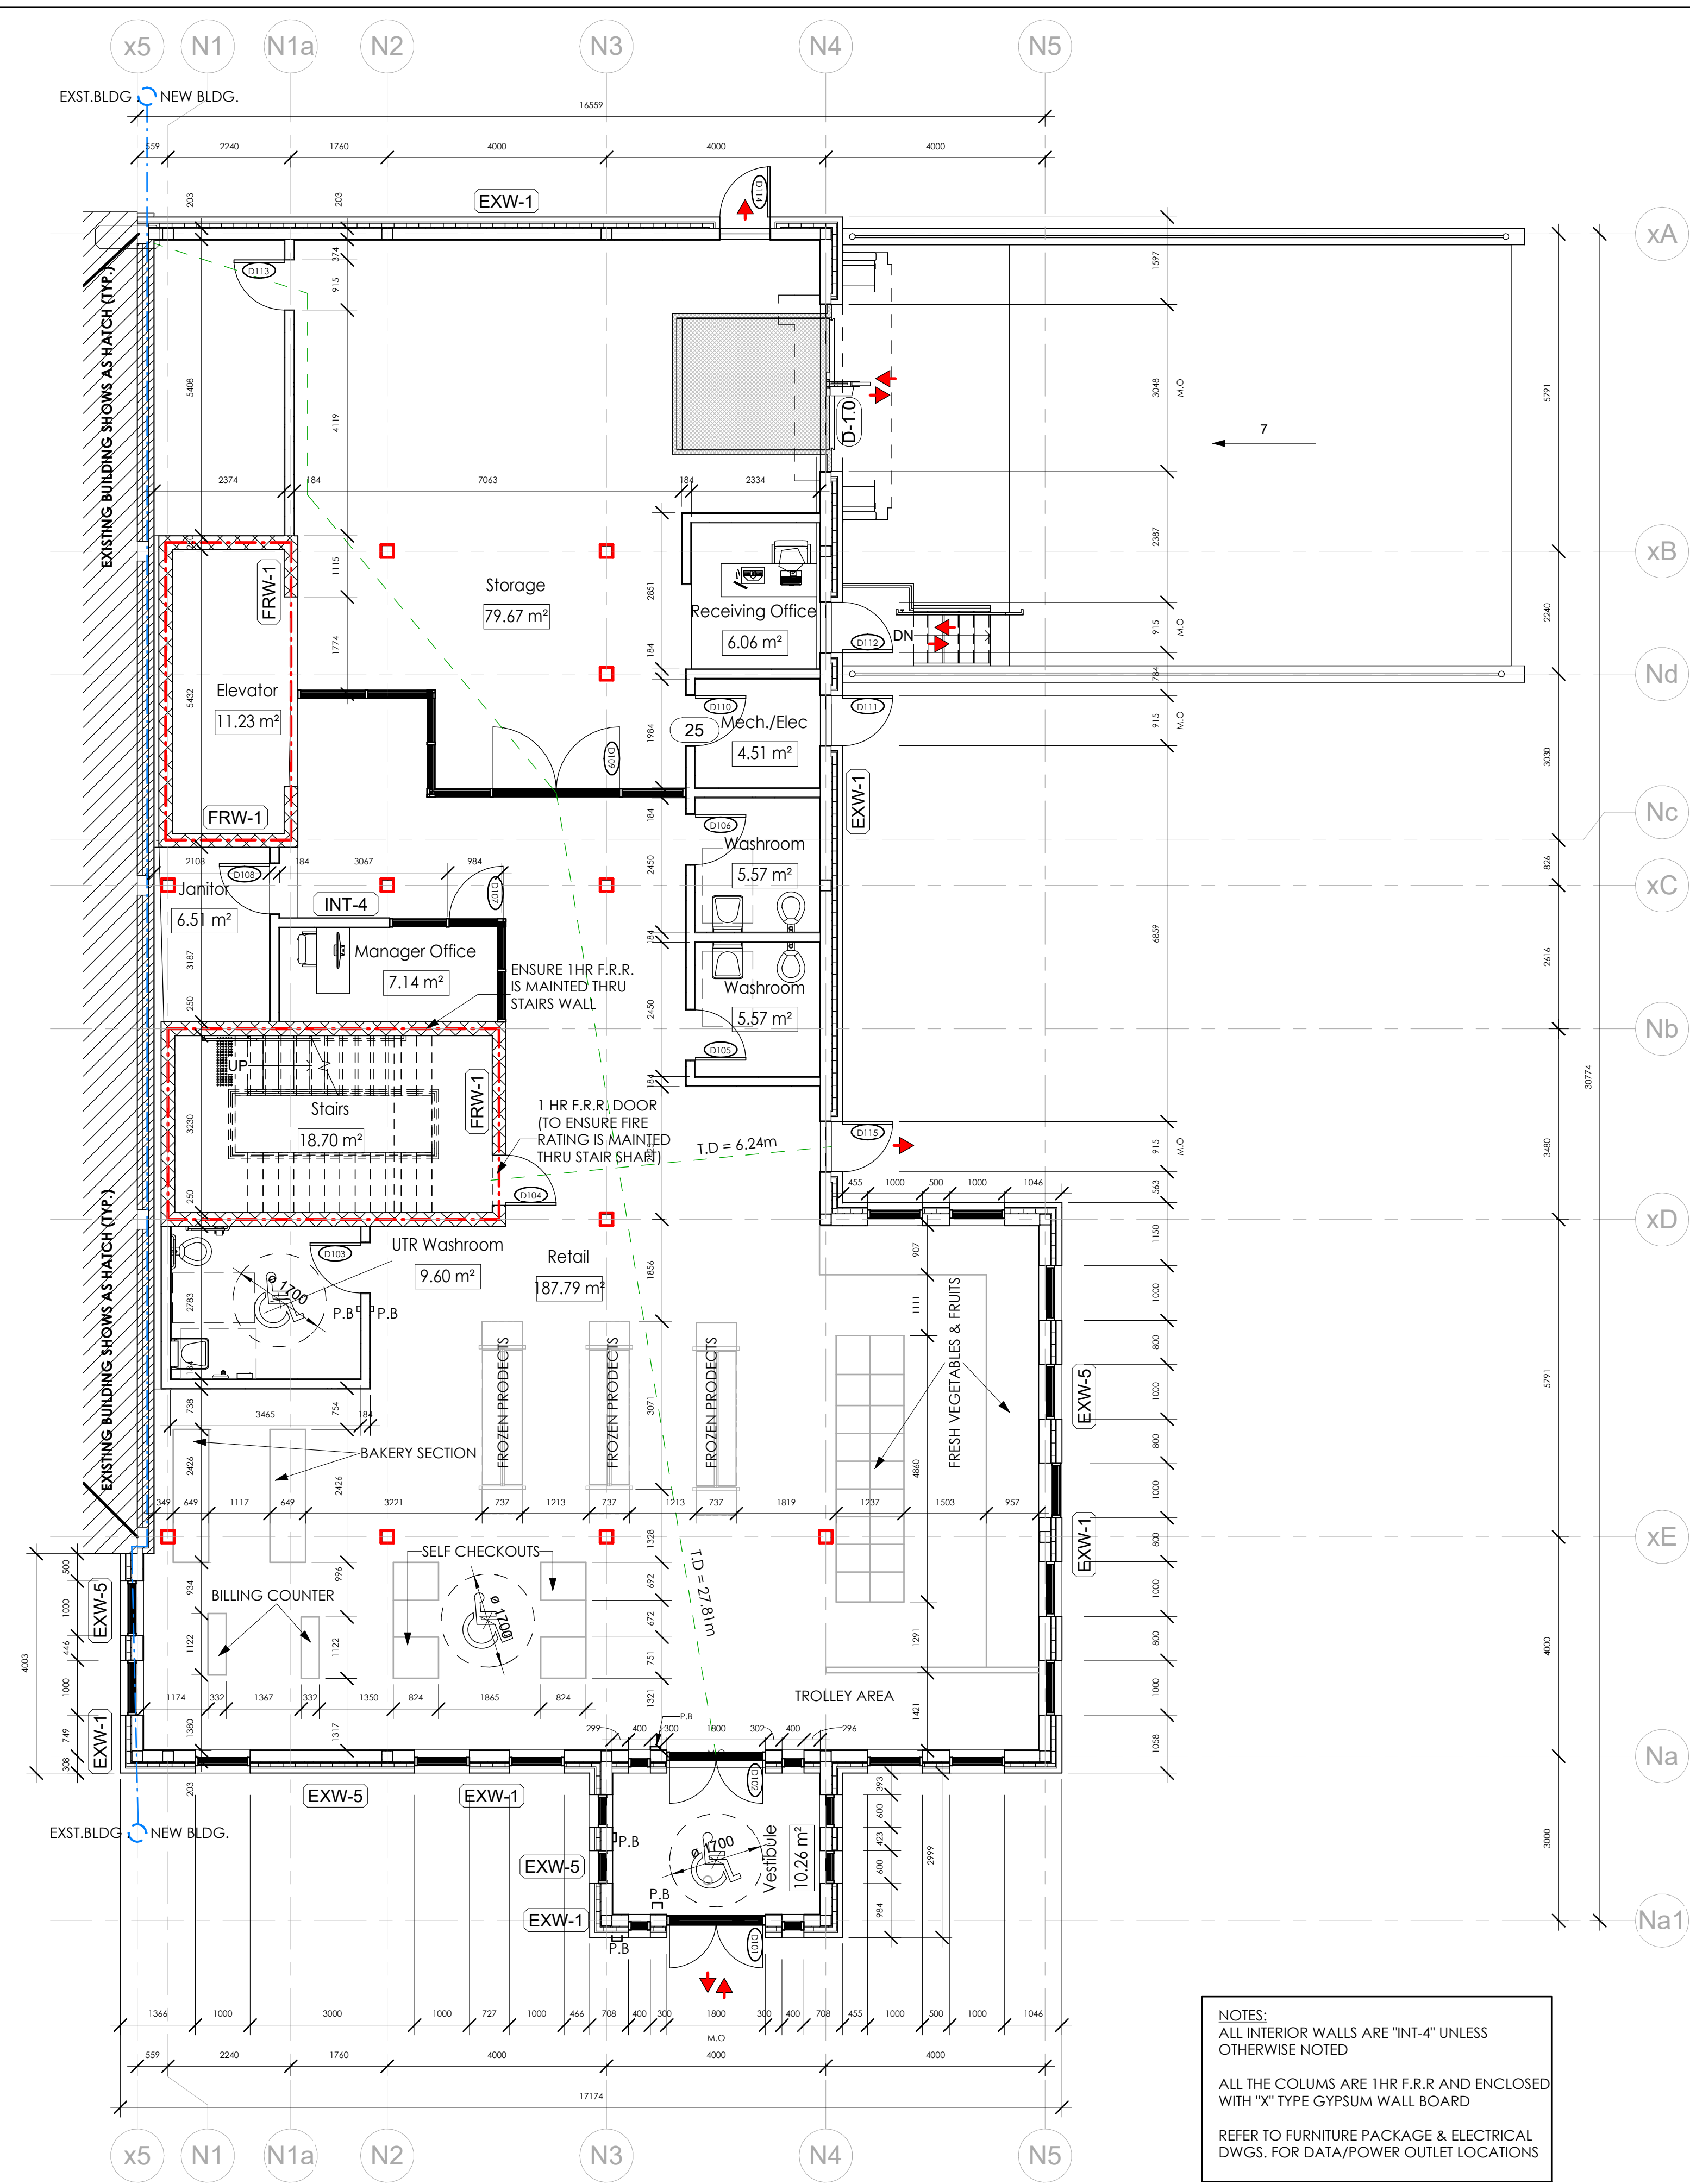

2 L100 ENLARGED MARKET PLAN
1:75

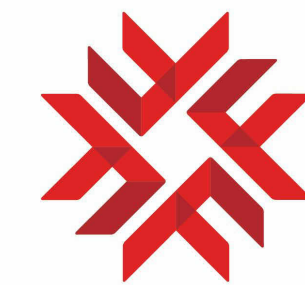

FANSHAW
DONALD J. SMITH
SCHOOL OF BUILDING
TECHNOLOGY

NORTH ARROW



GENERAL NOTES

1. DO NOT SCALE DRAWINGS. WRITTEN DIMENSIONS SHALL HAVE PRECEDENCE OVER SCALED DIMENSIONS.
2. ALL WORK SHALL COMPLY WITH THE 2012 ONTARIO BUILDING CODE AND AMENDMENTS.
3. CONTRACTORS MUST CHECK AND VERIFY ALL DIMENSIONS AND SPECIFICATIONS AND REPORT ANY DISCREPANCIES TO THE ARCHITECT BEFORE PROCEEDING WITH THE WORK.
4. ALL CONTRACTORS AND SUB-CONTRACTORS SHALL HAVE A SET OF APPROVED CONSTRUCTION DOCUMENTS ON SITE AT ALL TIMES.
5. ALL DOCUMENTS REMAIN THE PROPERTY OF THE ARCHITECT. UNAUTHORIZED USE, MODIFICATION, AND/OR REPRODUCTION OF THESE DOCUMENTS IS PROHIBITED WITHOUT WRITTEN PERMISSION. THE CONTRACT DOCUMENTS WERE PREPARED BY THE CONSULTANT FOR THE ACCOUNT OF THE OWNER.
6. THE MATERIAL CONTAINED HEREIN REFLECTS THE CONSULTANT'S BEST JUDGMENT IN LIGHT OF THE INFORMATION AVAILABLE TO HIM/HER AT THE TIME OF PREPARATION. ANY USE WHICH A THIRD PARTY MAKES OF THE CONTRACT DOCUMENTS, OR ANY RELIANCE ON/ONOR DECISIONS TO BE MADE BASED ON THEM ARE THE RESPONSIBILITY OF SUCH THIRD PARTIES.
7. THE CONSULTANT ACCEPTS NO RESPONSIBILITY FOR DAMAGES, IF ANY, SUFFERED BY ANY THIRD PARTY AS A RESULT OF DECISIONS MADE OR ACTIONS BASED ON THE CONTRACT DOCUMENTS.

PRELIMINARY
NOT FOR CONSTRUCTION


PROJECT TITLE
THE EDEN PROJECT

CLIENT:
Eden Project
PROJECT ADDRESS
555 McCormick Street


DRAWING TITLE
ENLARGED LEVEL 1 FLOOR & CEILING PLAN

CHECKED
GG
DRAWN
AFNM
DATE
15/08/25


0001
PROJECT No.
A7.1
DRAWING

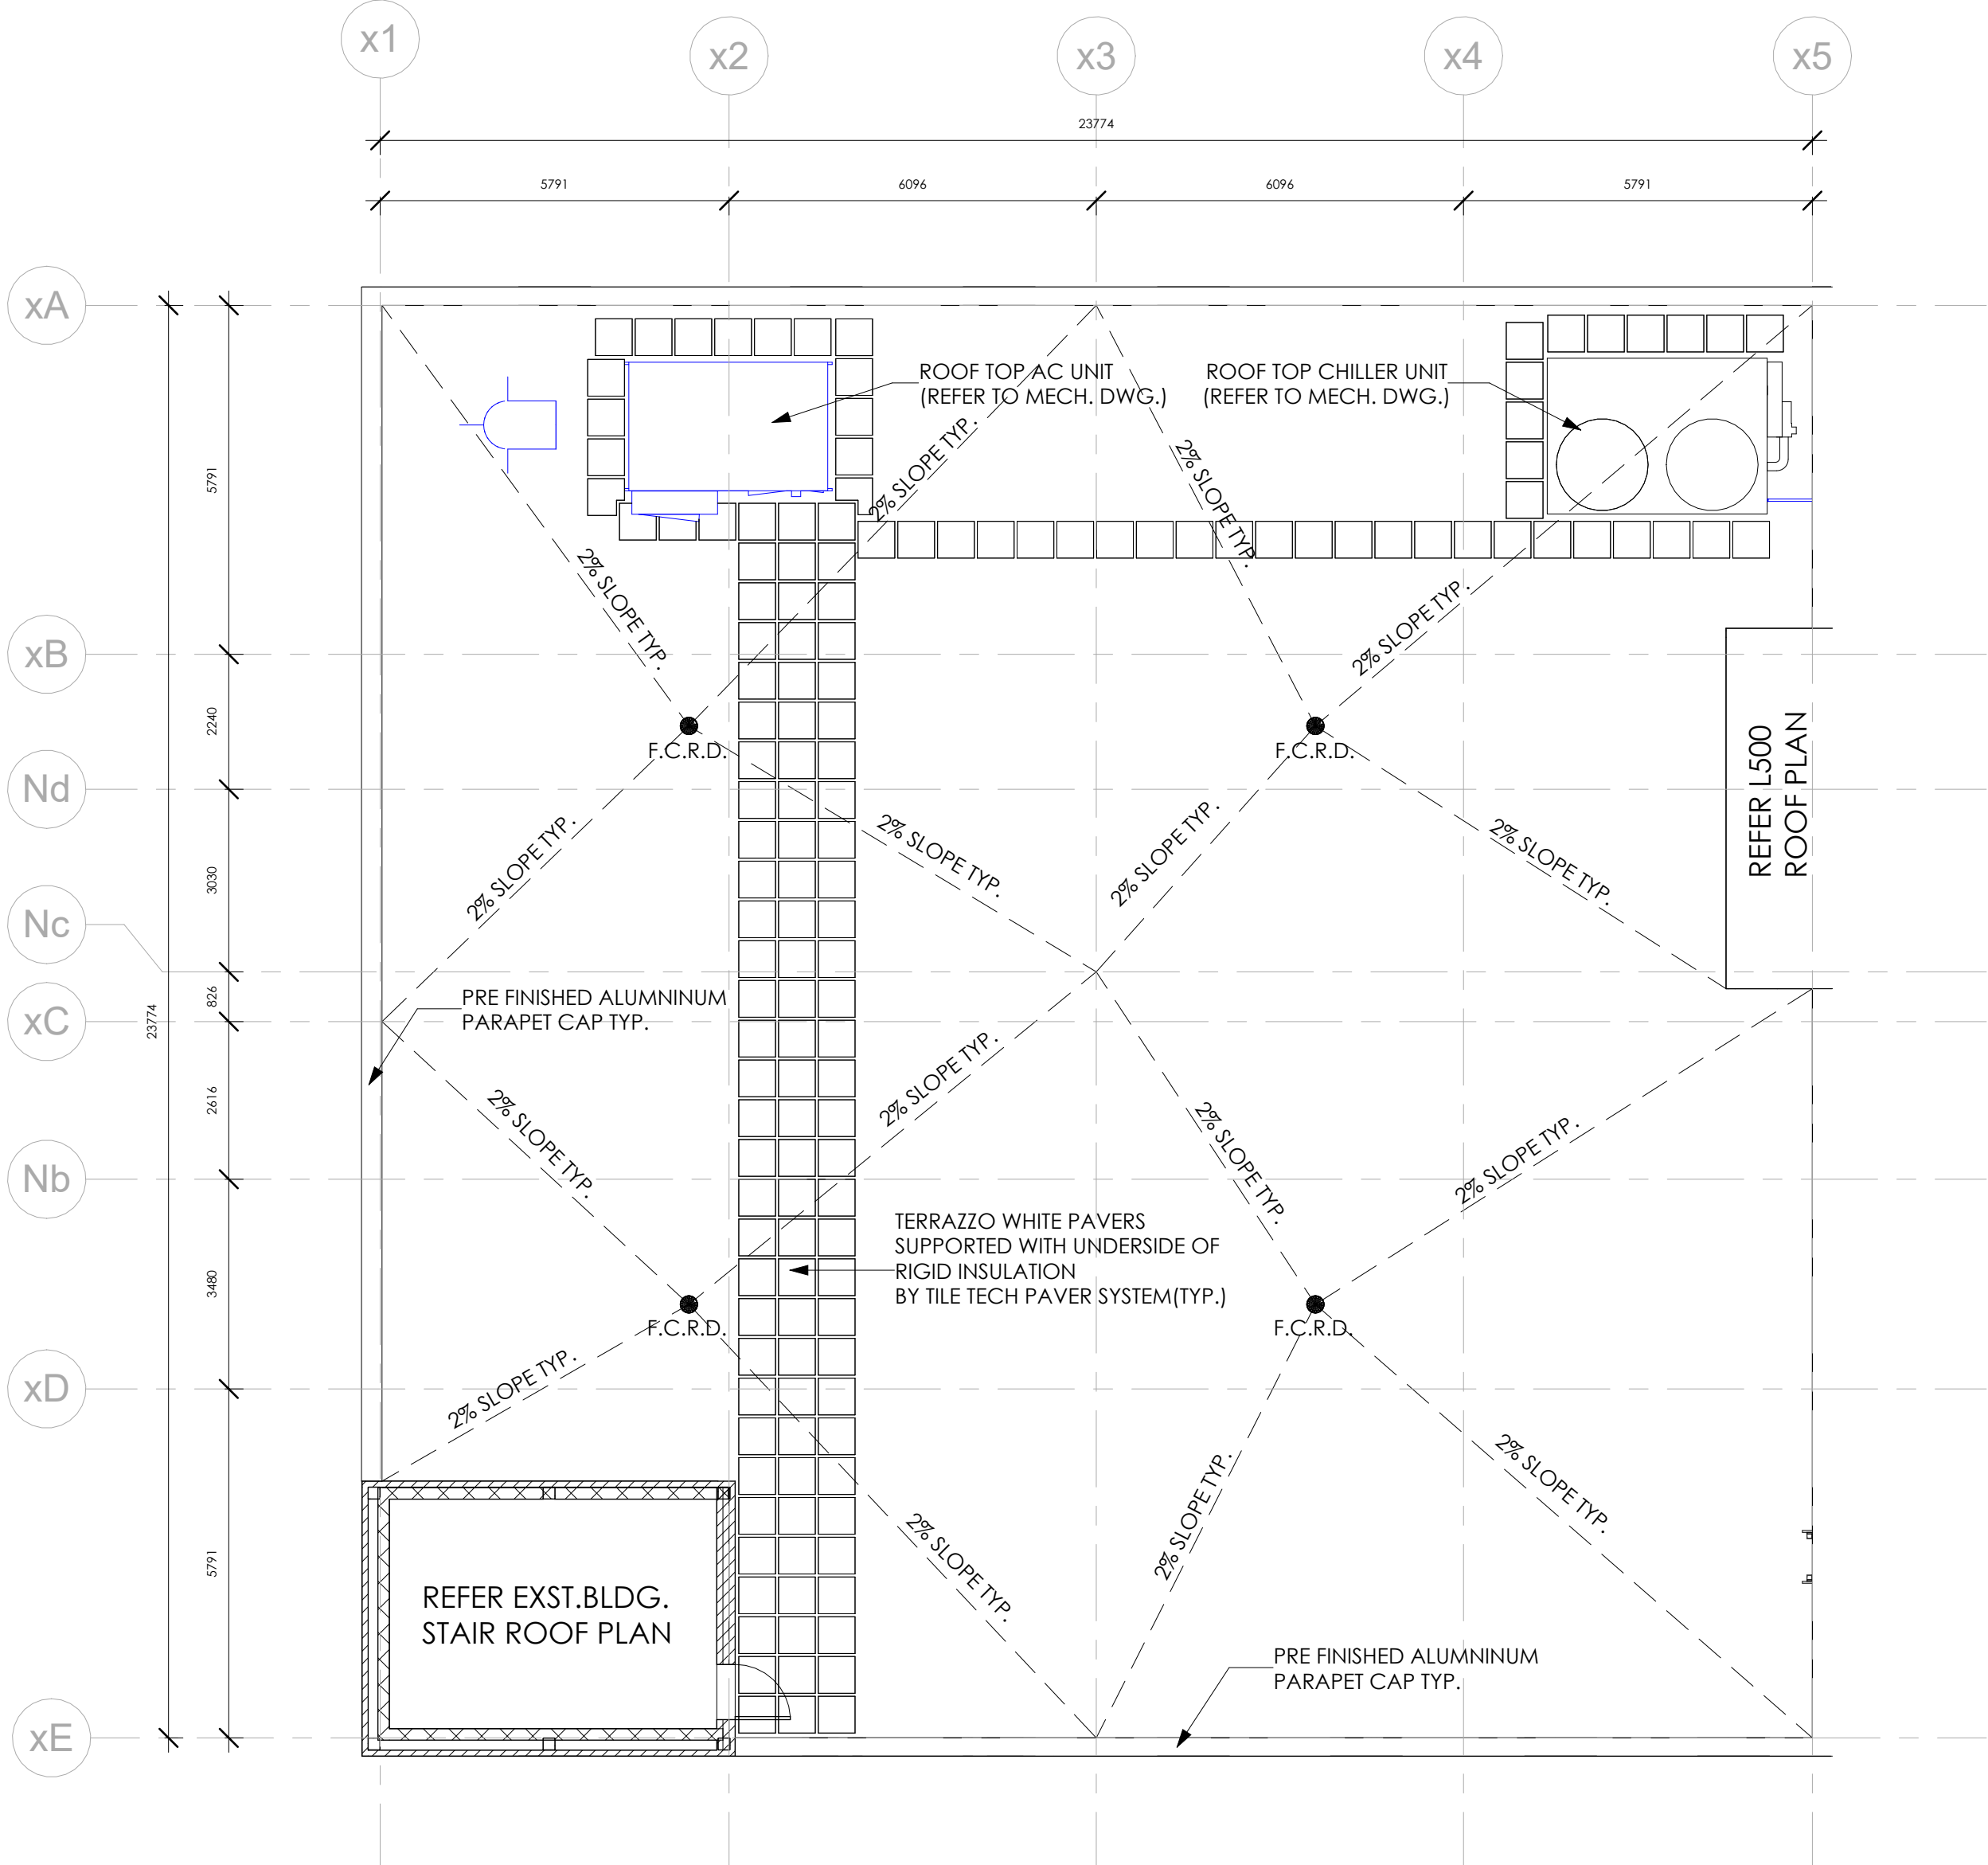


1 L400 ROOF PLAN
1 : 100

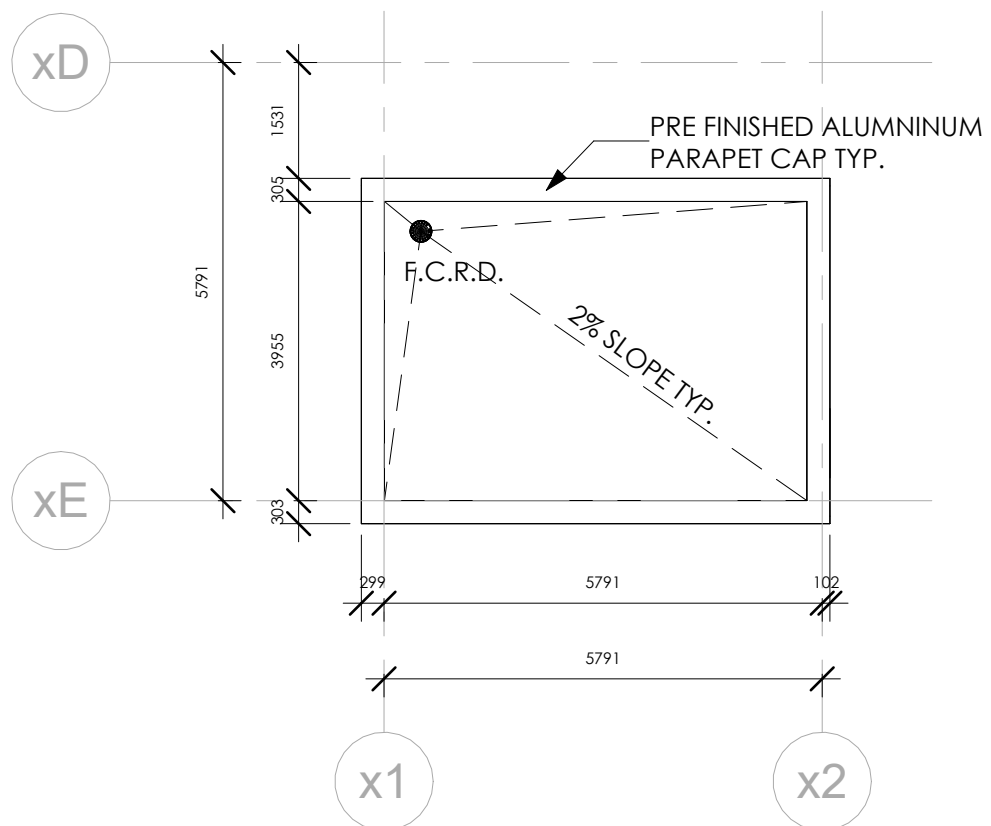


2 EXST.BLDG. STAIR ROOF PLAN
1 : 100

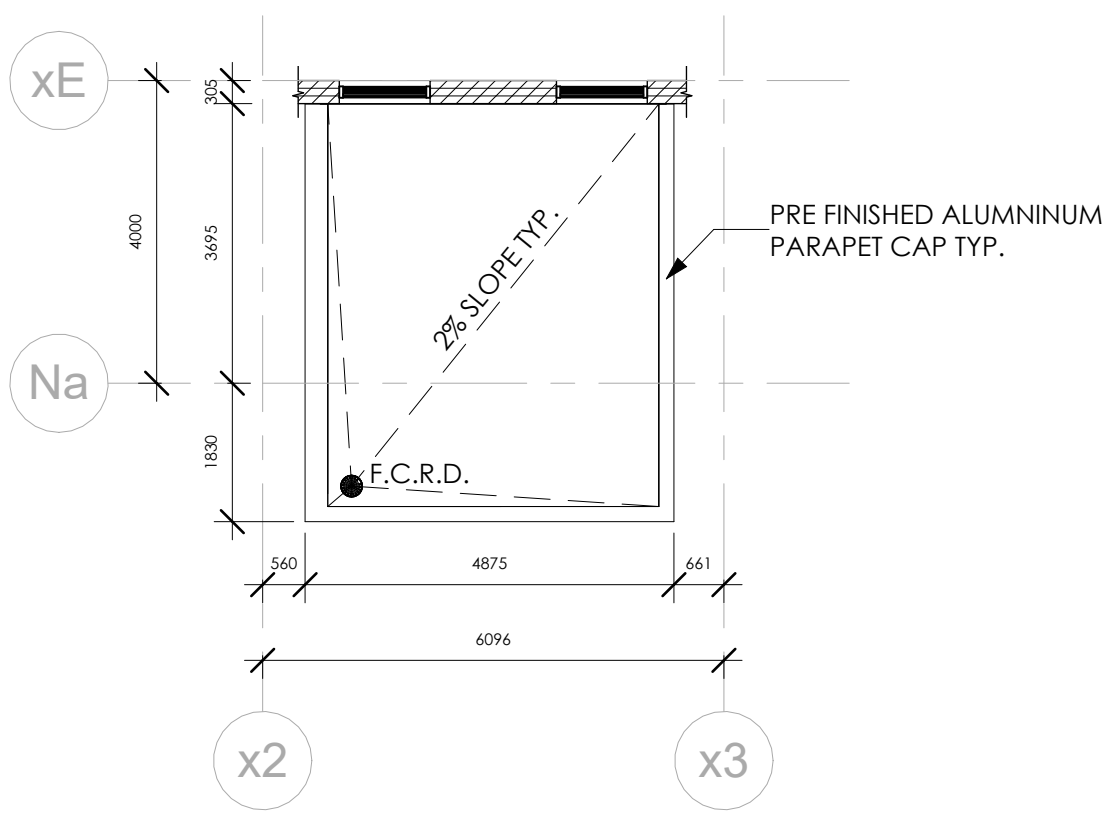


3 EXST.BLDG. CANOPY ROOF PLAN
1 : 100

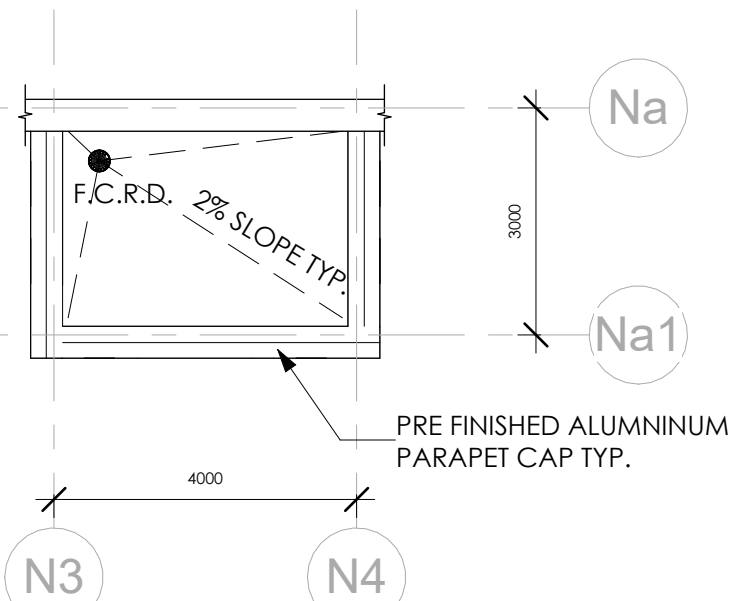


4 MAIN VEST. ROOF PLAN
1 : 100

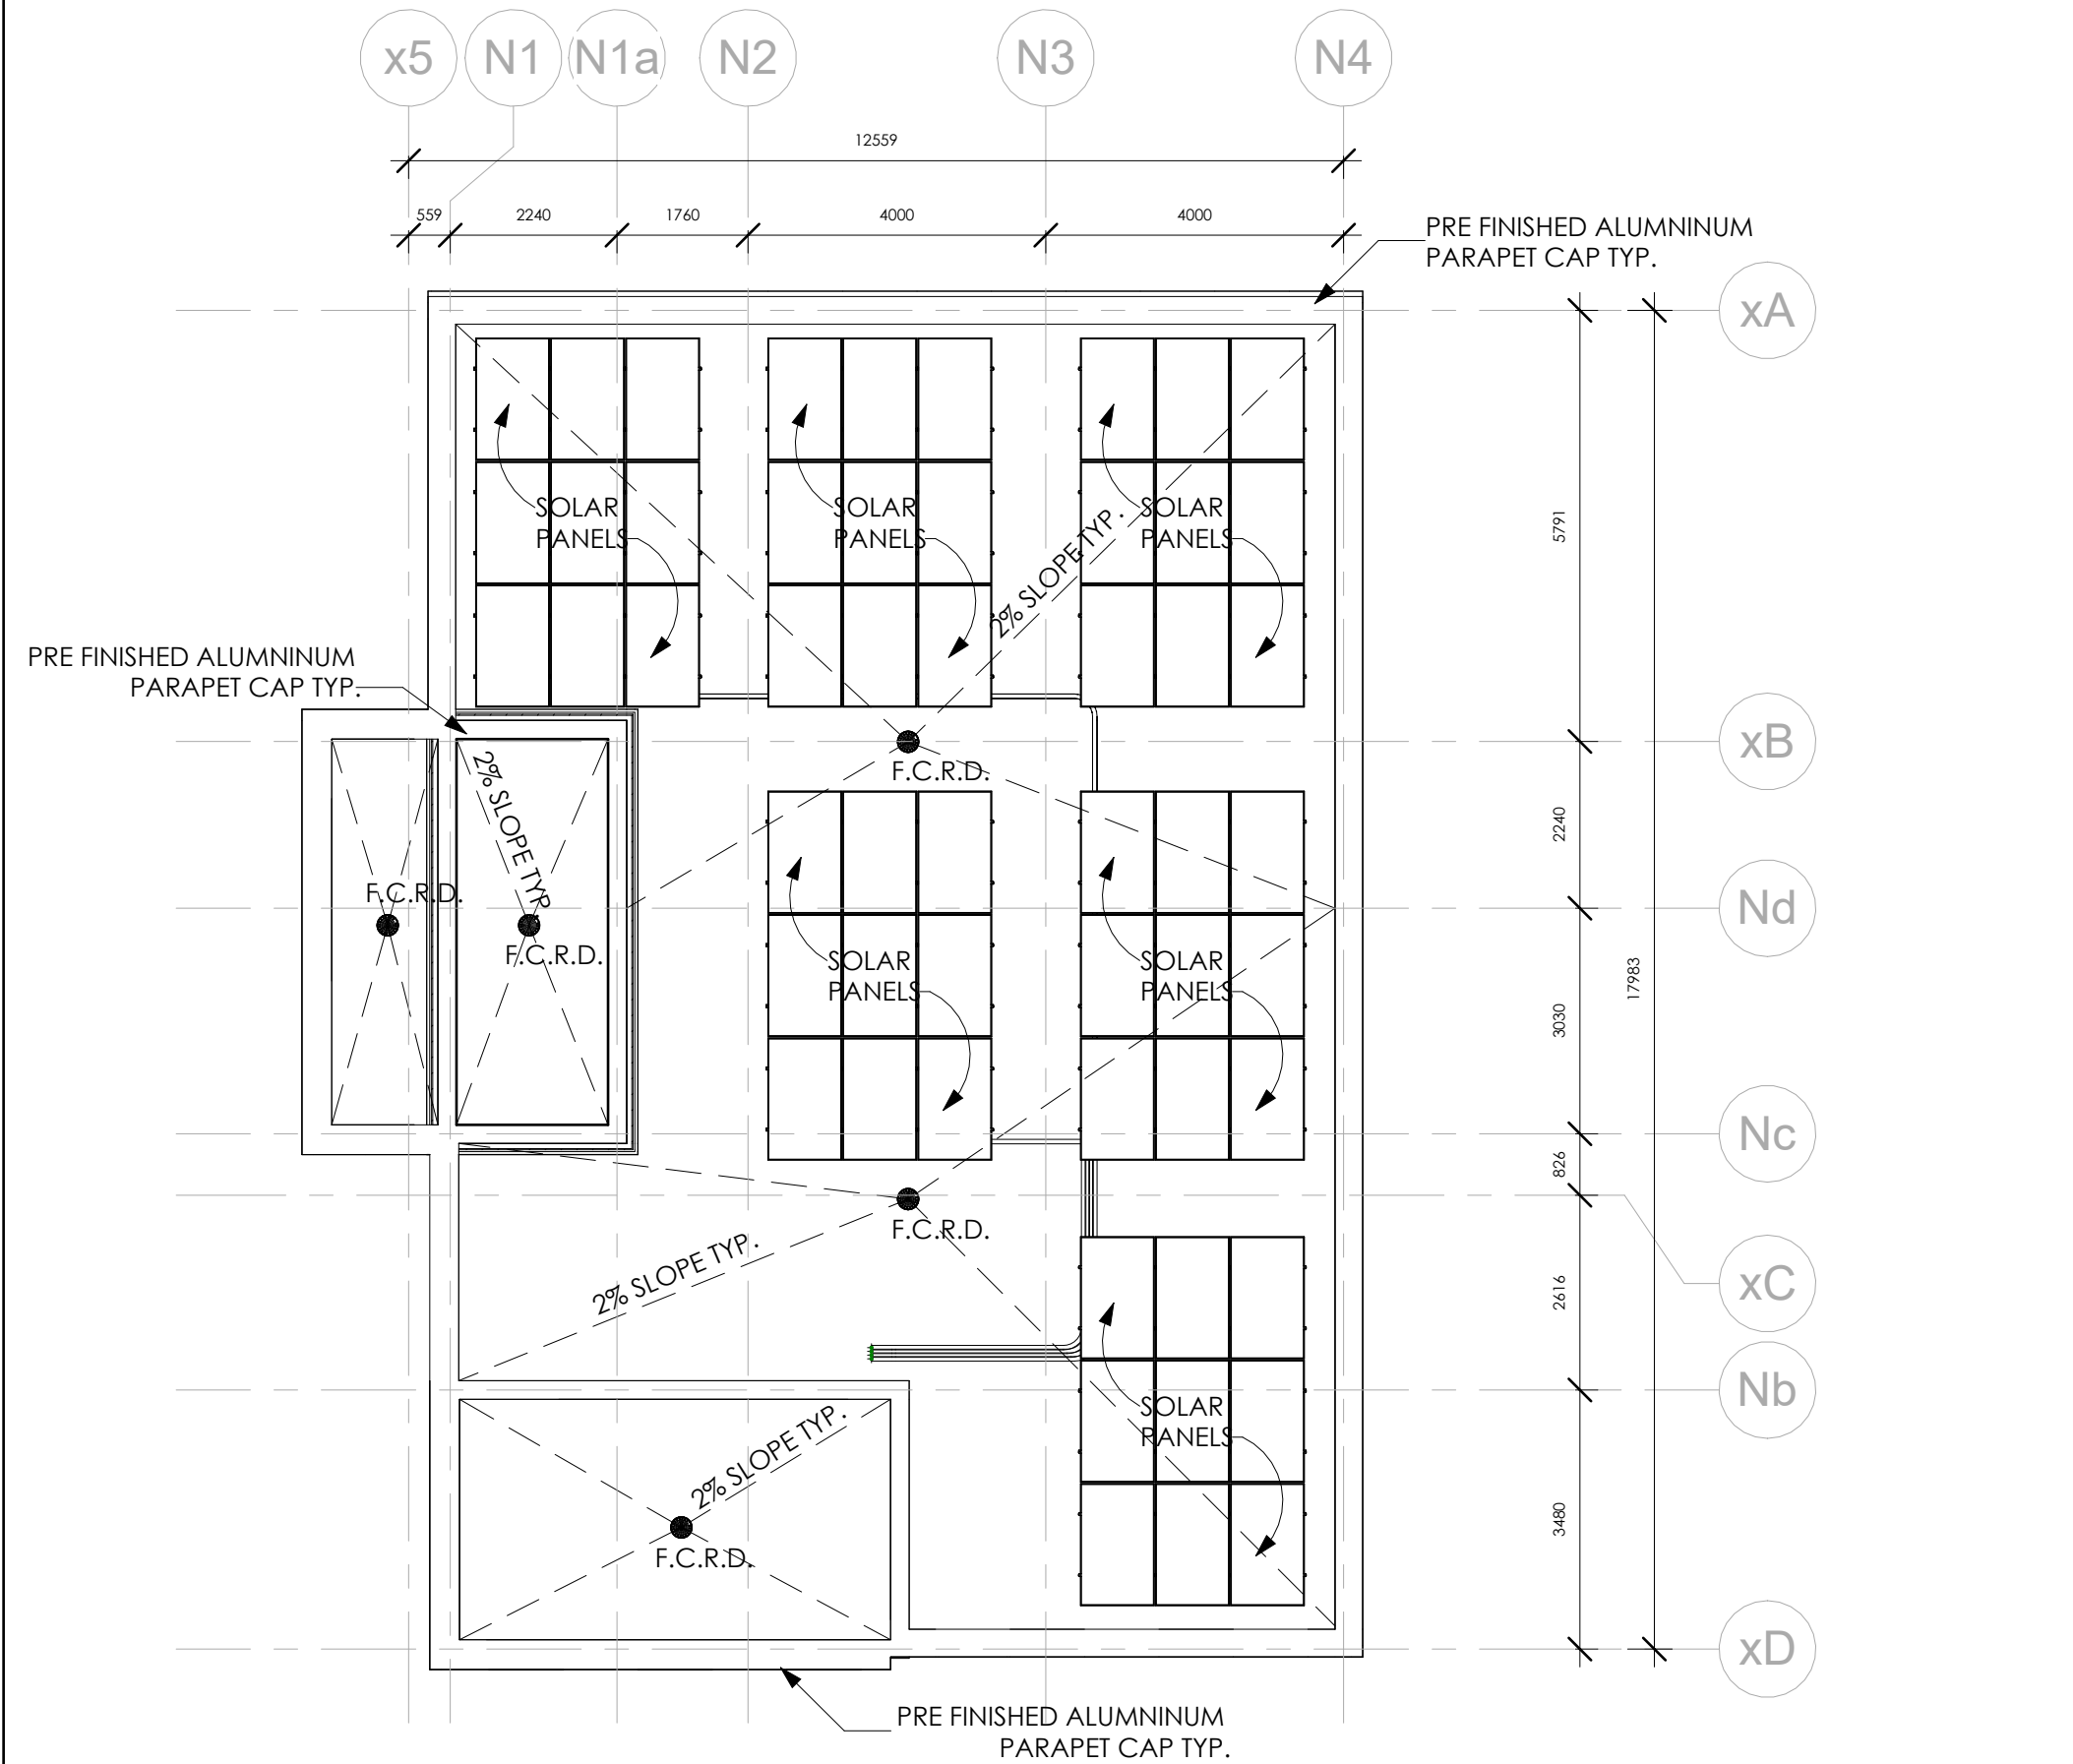

5 L500 ROOF PLAN
1 : 100

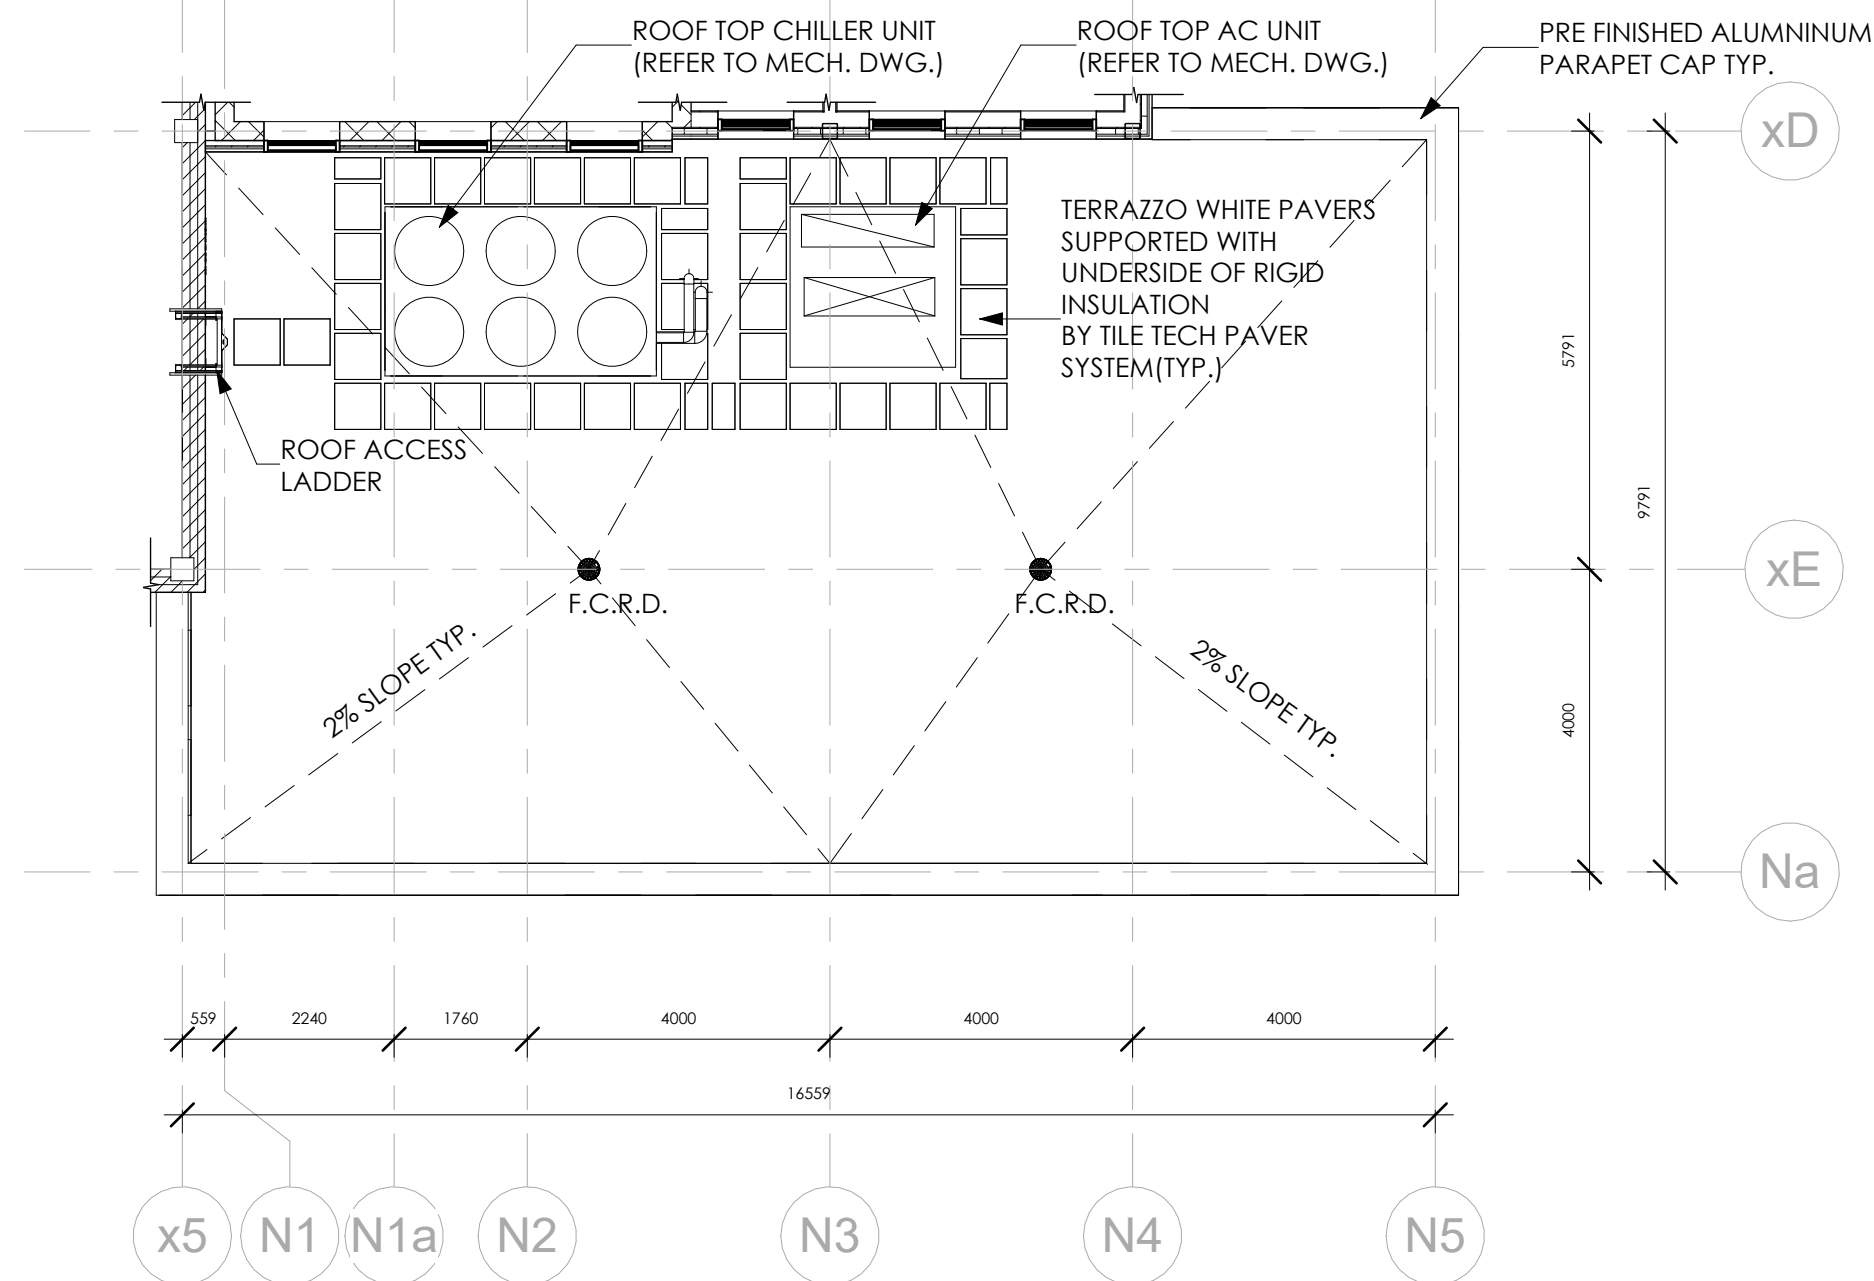


6 L300 ROOF PLAN
1 : 100

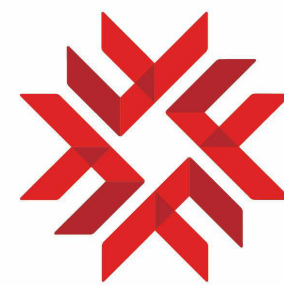

FANSHAWE
DONALD J. SMITH
SCHOOL OF BUILDING
TECHNOLOGY

NORTH ARROW

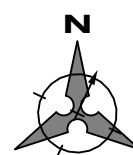

GENERAL NOTES

1. DO NOT SCALE DRAWINGS. WRITTEN DIMENSIONS SHALL HAVE PRECEDENCE OVER SCALED DIMENSIONS.
2. ALL WORK SHALL COMPLY WITH THE 2012 ONTARIO BUILDING CODE AND AMENDMENTS.
3. CONTRACTORS MUST CHECK AND VERIFY ALL DIMENSIONS AND SPECIFICATIONS AND REPORT ANY DISCREPANCIES TO THE ARCHITECT BEFORE PROCEEDING WITH THE WORK.
4. ALL CONTRACTORS AND SUB-CONTRACTORS SHALL HAVE A SET OF APPROVED CONSTRUCTION DOCUMENTS ON SITE AT ALL TIMES.
5. ALL DOCUMENTS REMAIN THE PROPERTY OF THE ARCHITECT. UNAUTHORIZED USE, MODIFICATION, AND/OR REPRODUCTION OF THESE DOCUMENTS IS PROHIBITED WITHOUT WRITTEN PERMISSION. THE CONTRACT DOCUMENTS WERE PREPARED BY THE CONSULTANT FOR THE ACCOUNT OF THE OWNER.
6. THE MATERIAL CONTAINED HEREIN REFLECTS THE CONSULTANT'S BEST JUDGEMENT IN LIGHT OF THE INFORMATION AVAILABLE TO HIM/HER AT THE TIME OF PREPARATION. ANY USE WHICH A THIRD PARTY MAKES OF THE CONTRACT DOCUMENTS, OR ANY RELIANCE ON/OR DECISIONS TO BE MADE BASED ON THEM ARE THE RESPONSIBILITY OF SUCH THIRD PARTIES.
7. THE CONSULTANT ACCEPTS NO RESPONSIBILITY FOR DAMAGES, IF ANY, SUFFERED BY ANY THIRD PARTY AS A RESULT OF DECISIONS MADE OR ACTIONS BASED ON THE CONTRACT DOCUMENTS.

PRELIMINARY
NOT FOR CONSTRUCTION

PROJECT TITLE
THE EDEN PROJECT

CLIENT:
Eden Project
PROJECT ADDRESS
555 McCormick Street

DRAWING TITLE
ROOF PLANS

CHECKED
GG

DRAWN
AFNM

DATE
15/08/25

0001
PROJECT No.

A8.1
DRAWING