


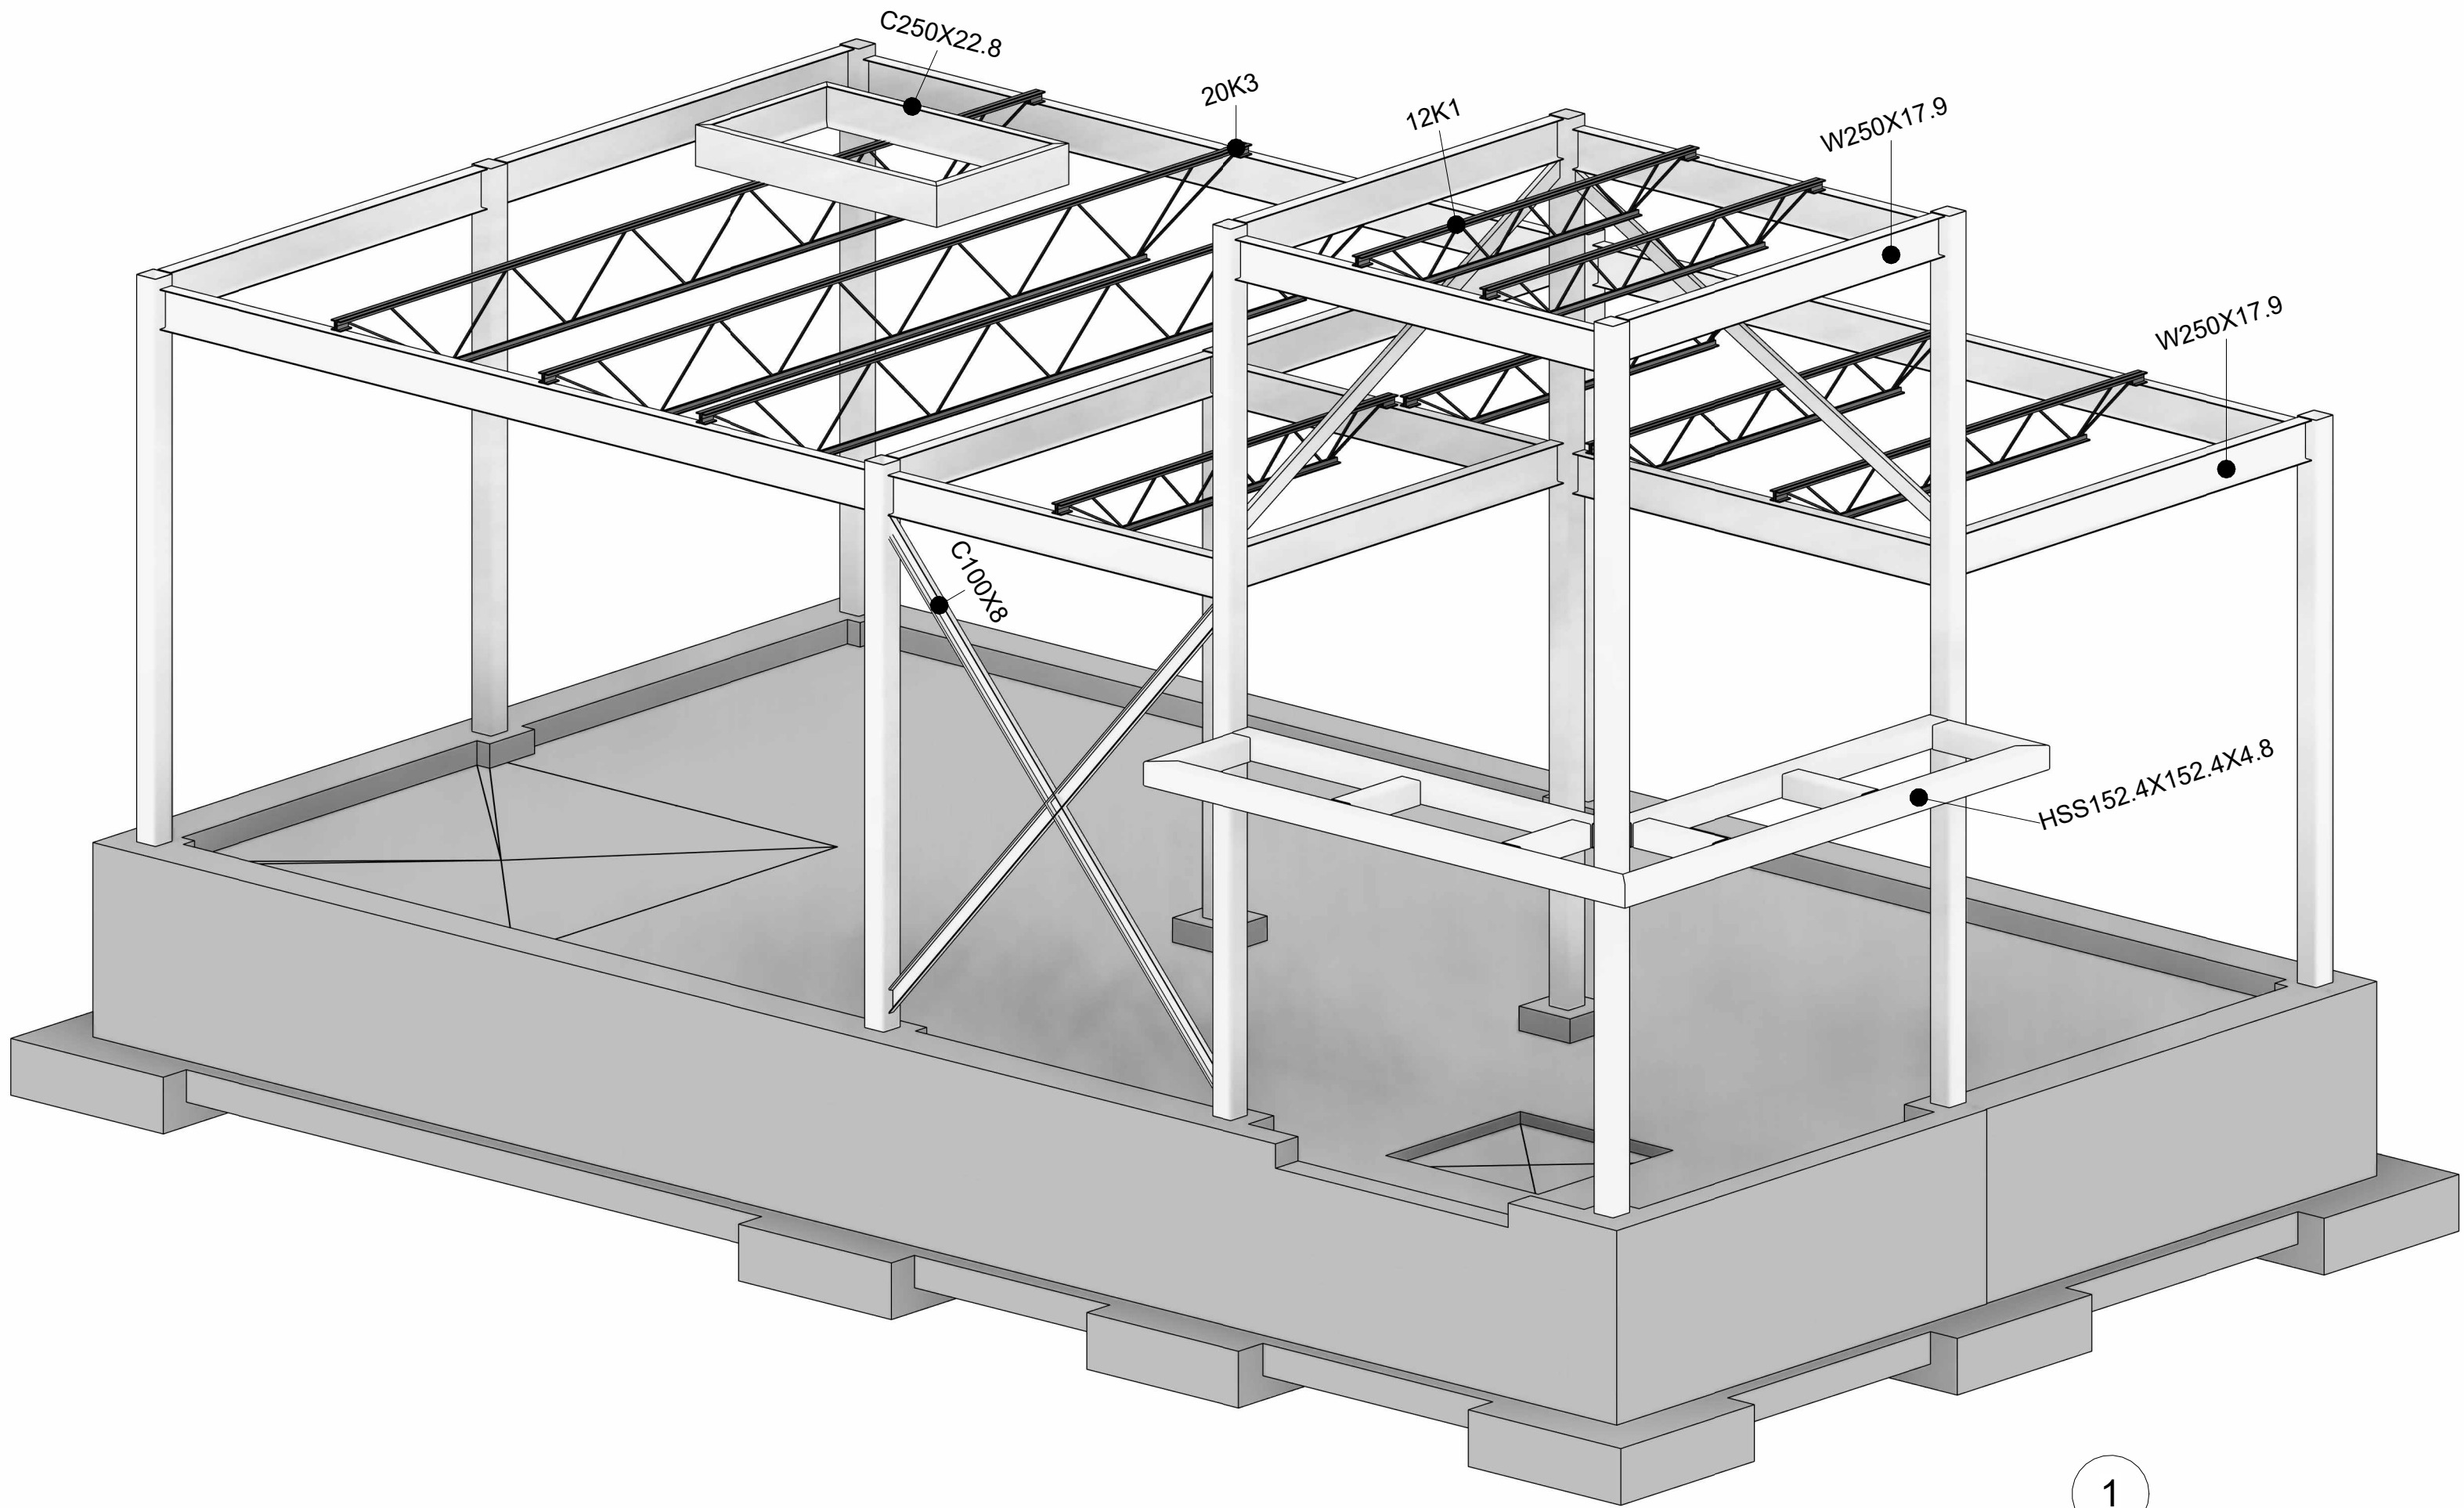

CAST IN PLACE CONCRETE TAKEOFF					
Type Mark	Count	Material: Volume	Material: Cost	Total Concrete Cost (\$)	Notes
FD-1	4	11.72 m³	\$235.00	2754.31	Foundation Wall
FD-2	2	1.48 m³	\$235.00	346.96	Foundation Wall
FD-3	11	0.79 m³	\$235.00	186.03	Column Piers
FL-1	3	10.97 m³	\$235.00	2578.19	Slab on Grade
PF-1	11	5.54 m³	\$235.00	1302.84	Pad Footings
RF-1	2	3.63 m³	\$235.00	853.85	Metal Deck In-fill
STF-1	4	2.54 m³	\$235.00	595.81	Strip Footings
STF-2	2	0.33 m³	\$235.00	76.48	Strip Footings
		37.00 m³		8694.46	

Structural Foundation Schedule						
Type Mark	Count	Length	Width	Foundation Thickness	Elevation at Top	Elevation at Bottom
PF-1	11	1200	1200	350	243.80 m	243.45 m
STF-1	4	REFER TO PLAN	600	200	243.80 m	243.60 m
STF-2	2	REFER TO PLAN	450	200	243.80 m	243.60 m


17

REVISIONS

NO. | DATE | REVISION | BY


Key Plan

North Arrow

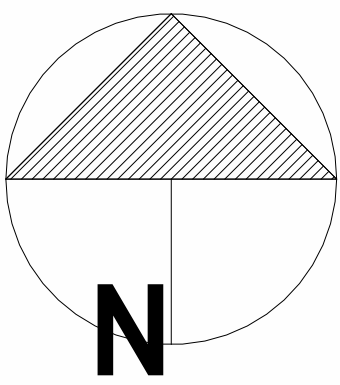

2 BIM ISOMETRIC - STRUCTURAL

Column Schedule				
U/S Entry Metal Deck				U/S Entry Metal Deck
250500				250500
U/S Metal Deck				U/S Metal Deck
248500				248500
T/O Steel Canopy				T/O Steel Canopy
247400				247400
T/O Foundation				T/O Foundation
245000				245000
Column Locations	A-1, A-2, A-3, B-1, B-2, Ay-1, Ay-2	B-2x, B-3, Ay-2x, Ay-3		

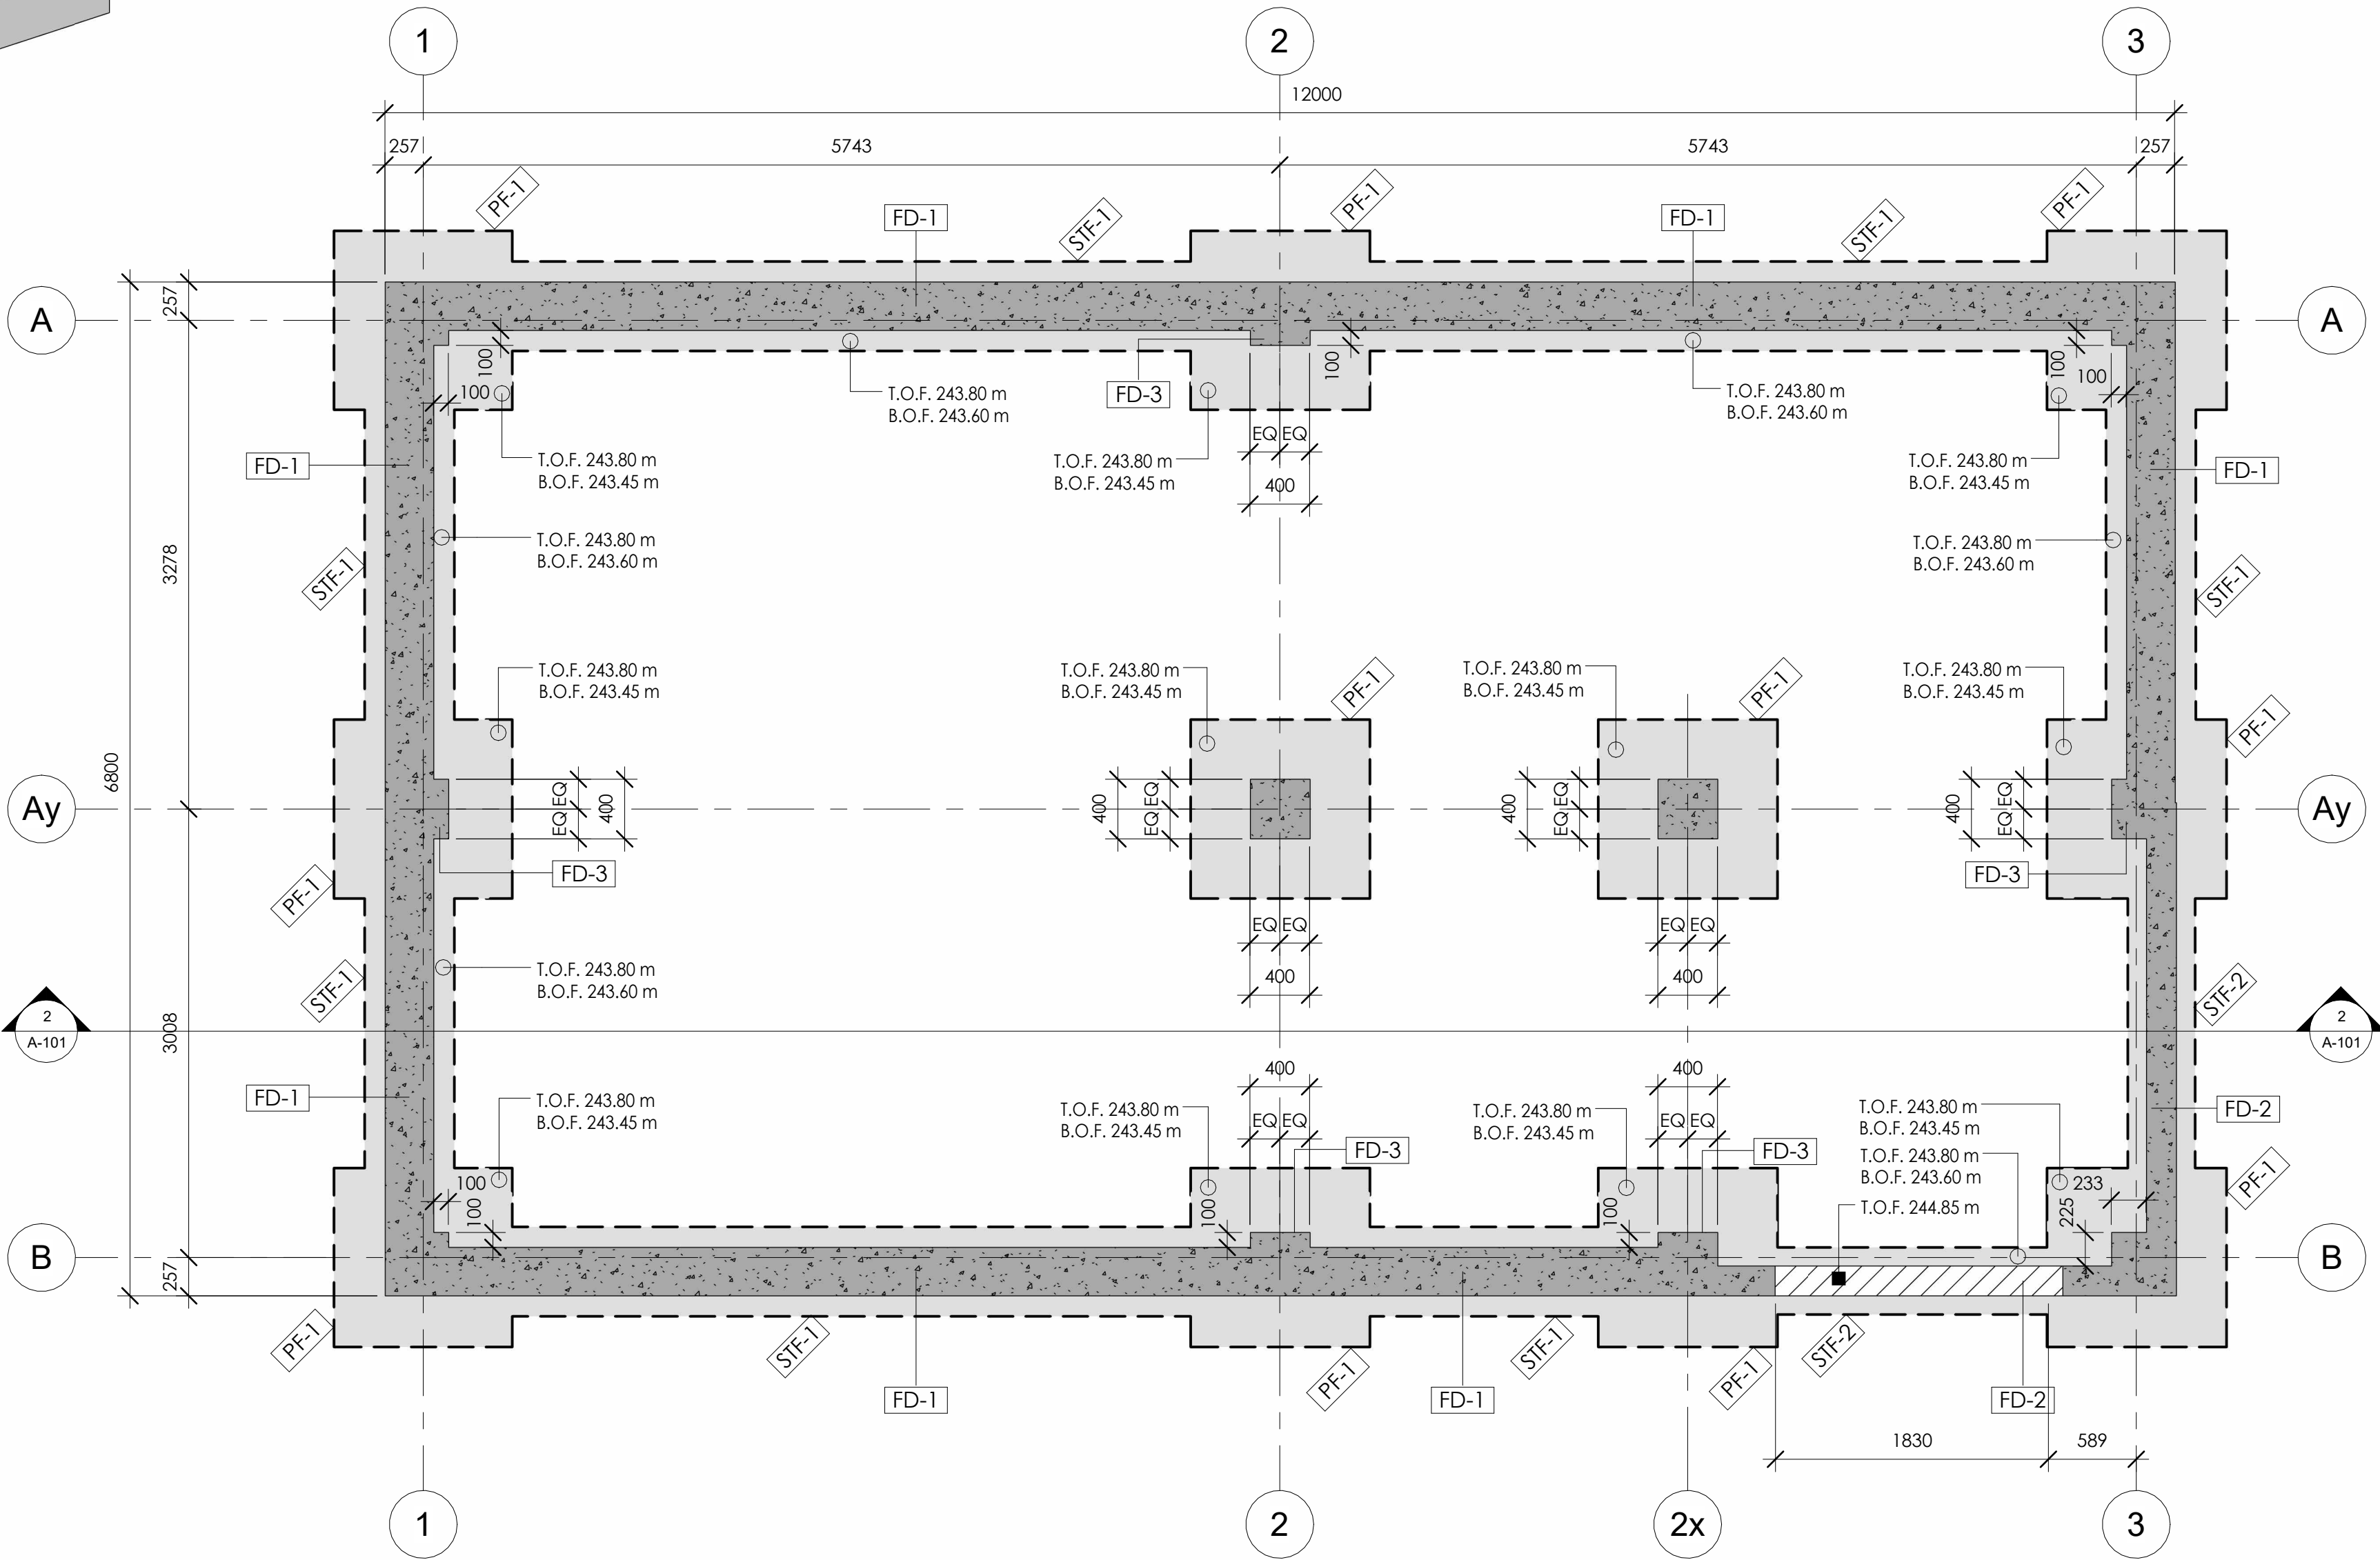


1 FOUNDATION PLAN

1 : 35

GRAPHIC COLUMN SCHEDULE

1 : 35

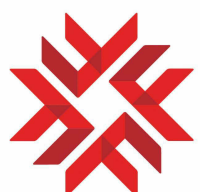

FANSHAWE

School of Building Technology
ARCHITECTURAL
TECHNOLOGY

PROJECT TITLE
Capstone Commerical
Project

PROJECT ADDRESS
1001 Commercial Way,
London, ON

DRAWING TITLE
FOUNDATION & STRUCTURES


DRAWN
AFNM

DATE
01/04/25


W2025-VDC
CLASS NO.

S-101
DRAWING


REVISION

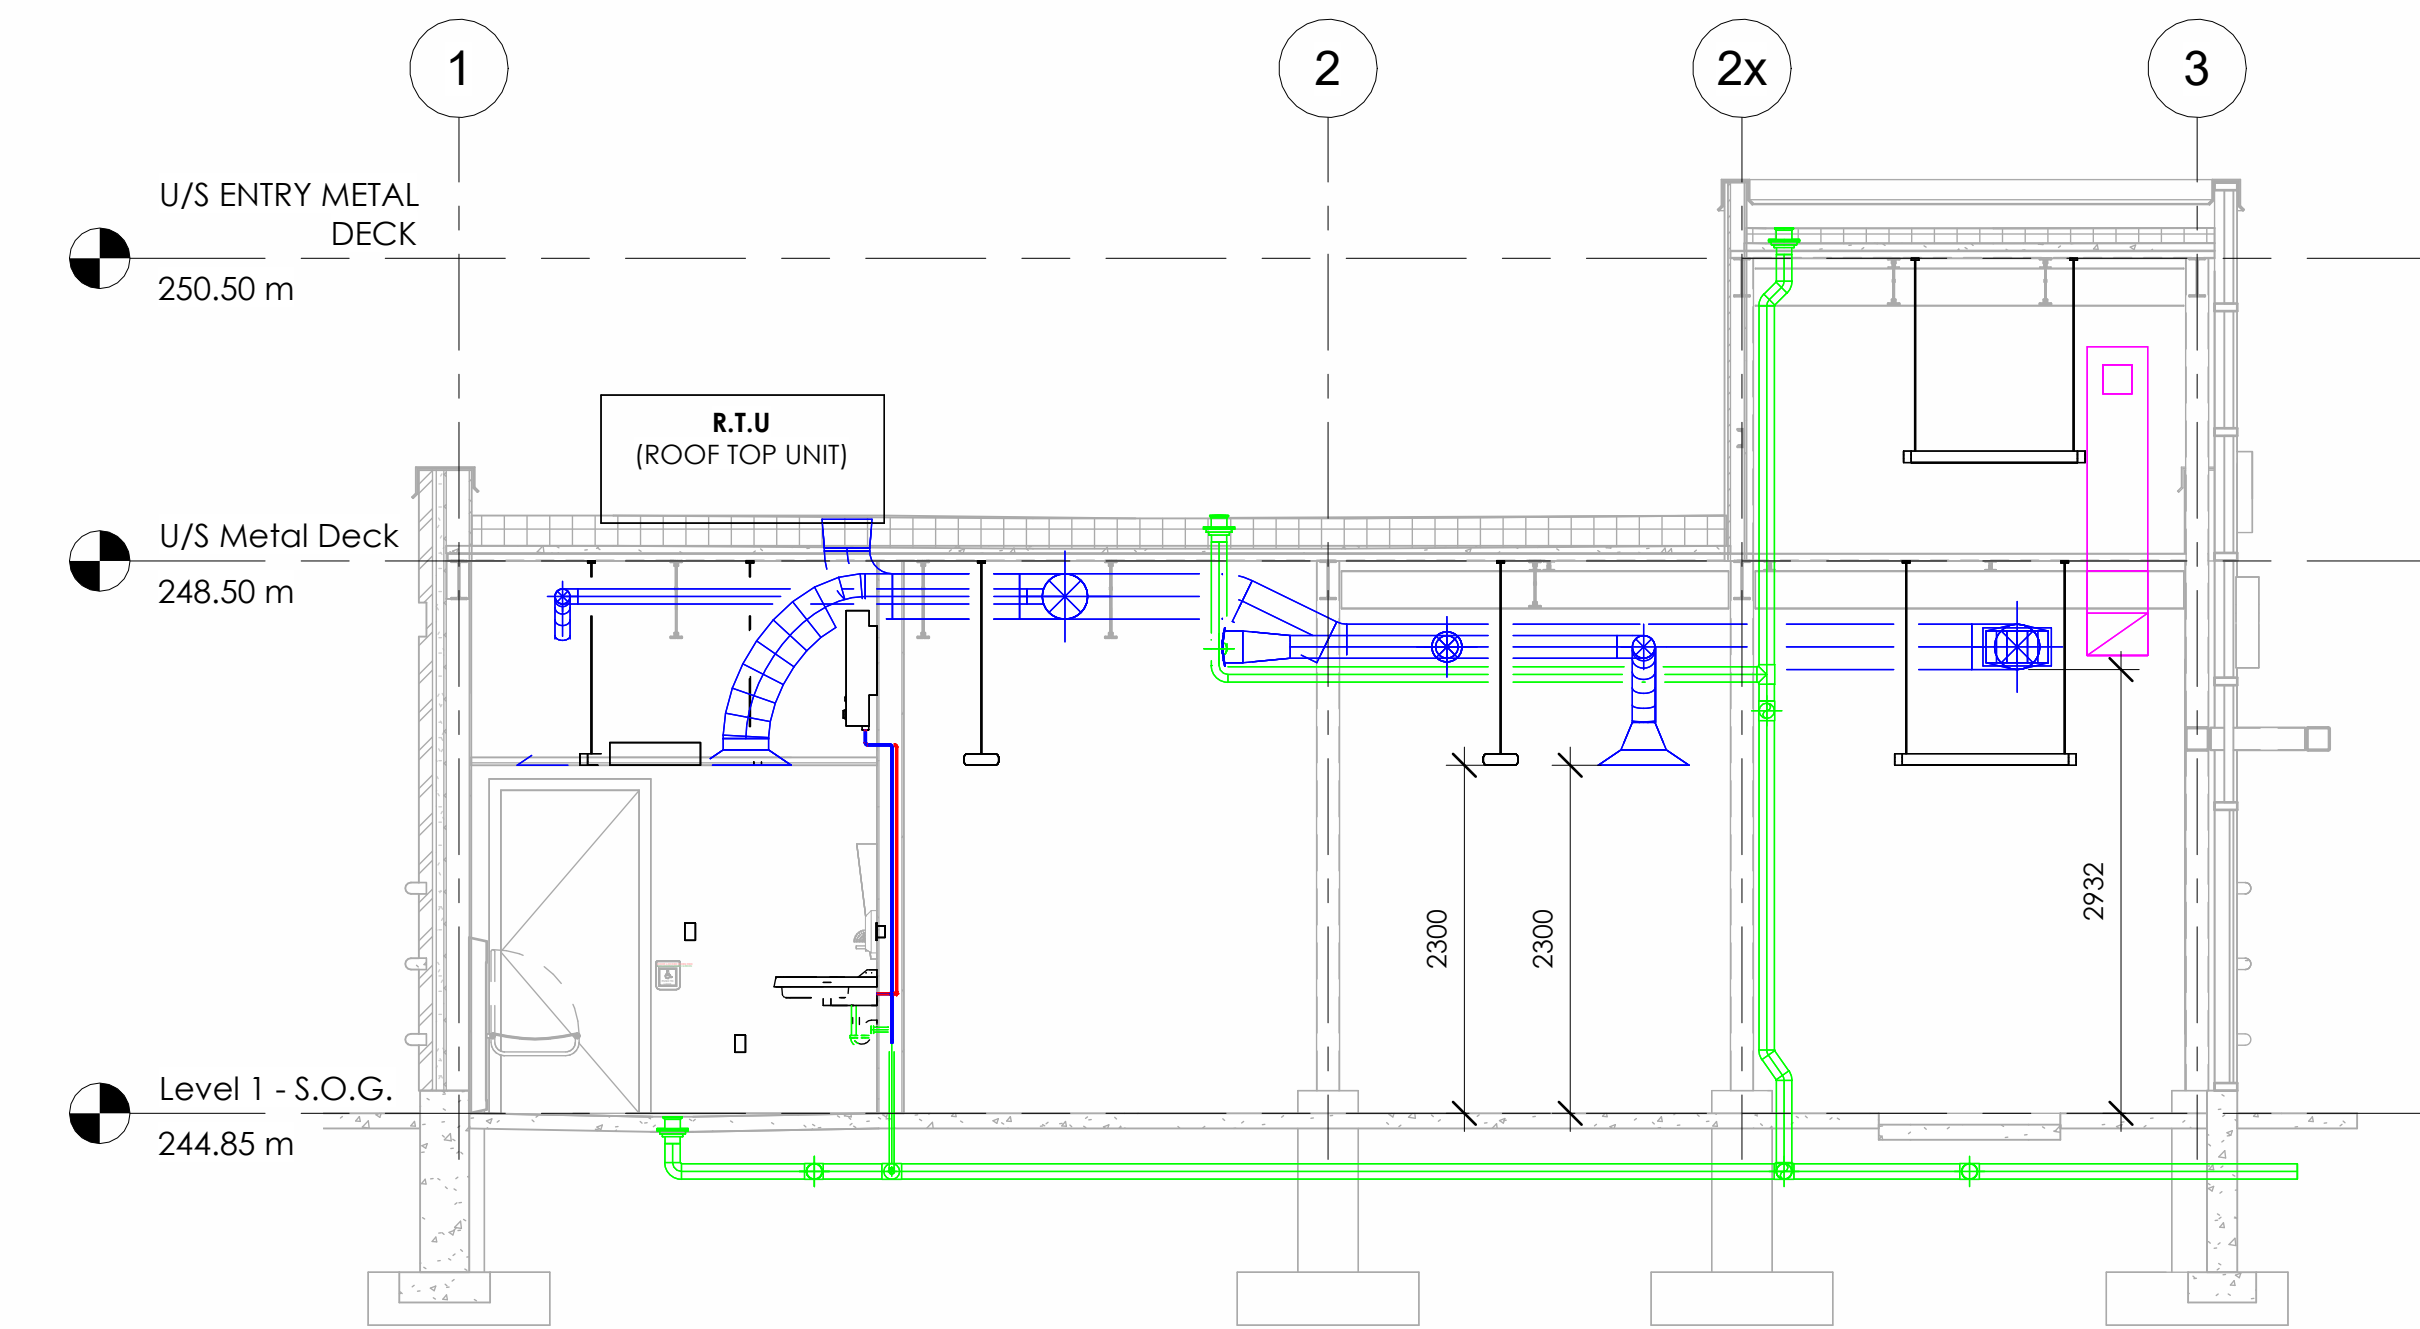

1 BIM ISOMETRIC - SYSTEMS M.E.P.

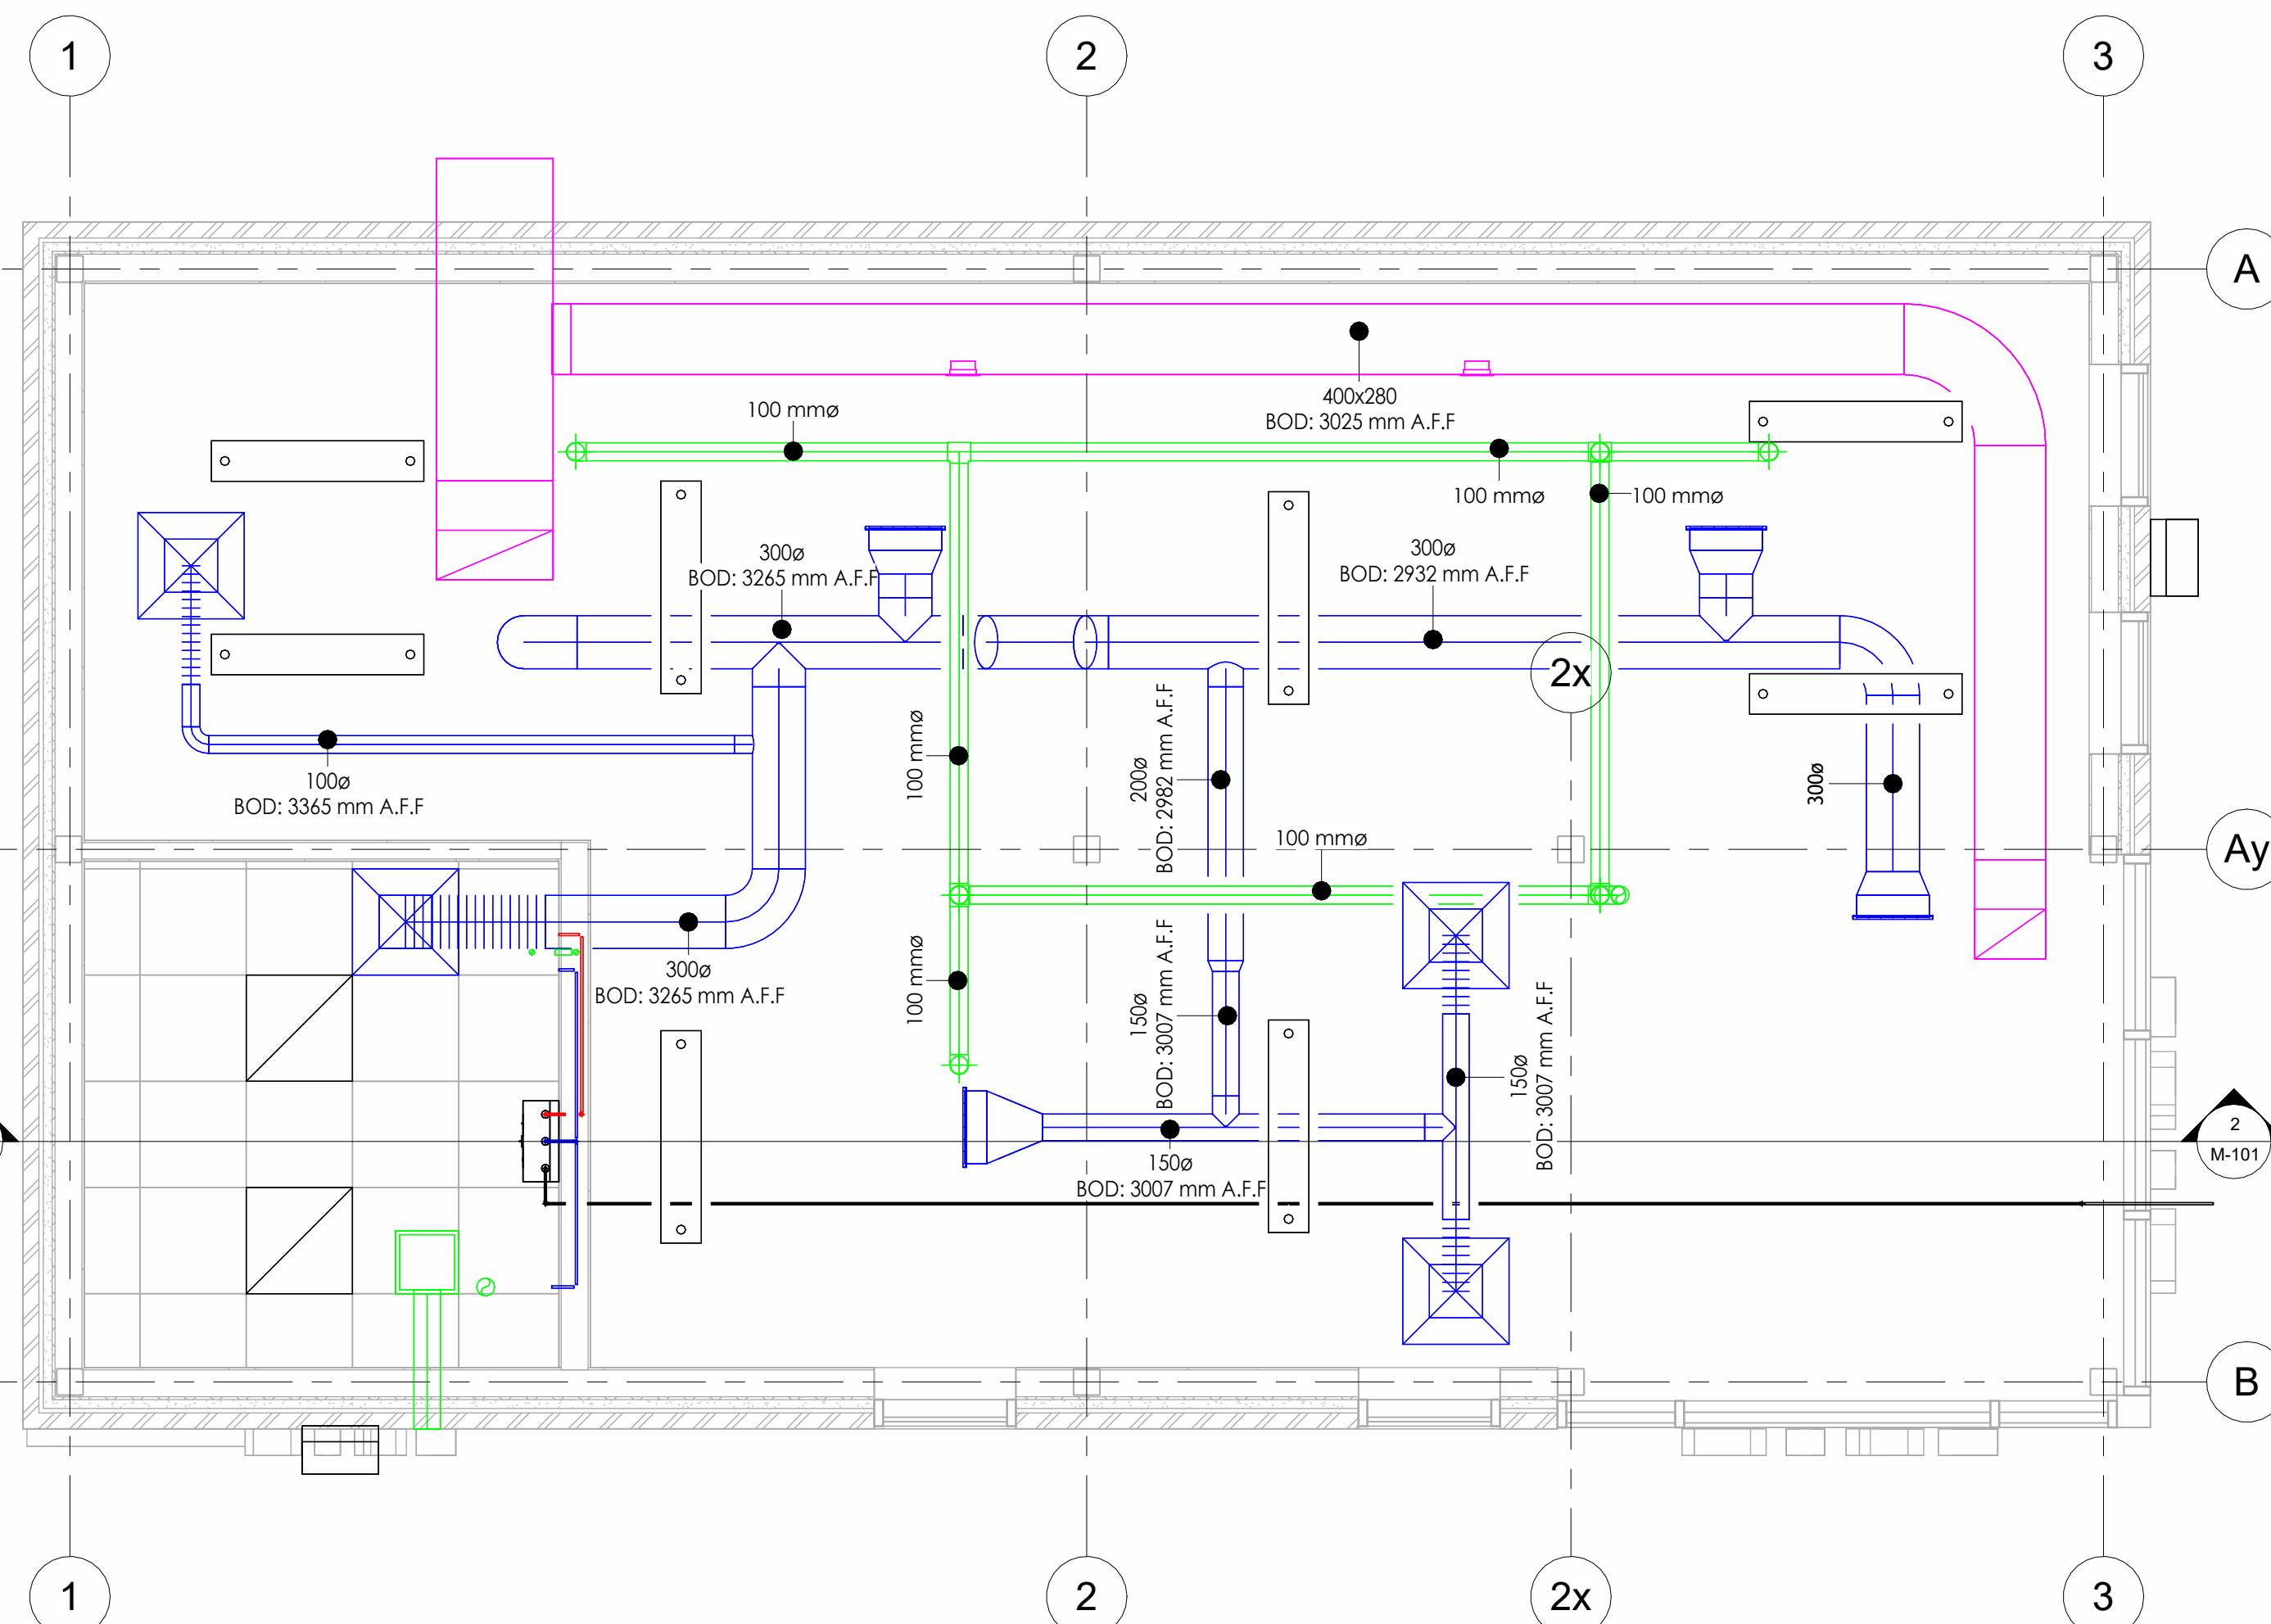

4 SYSTEMS R.C.P.
1 : 35

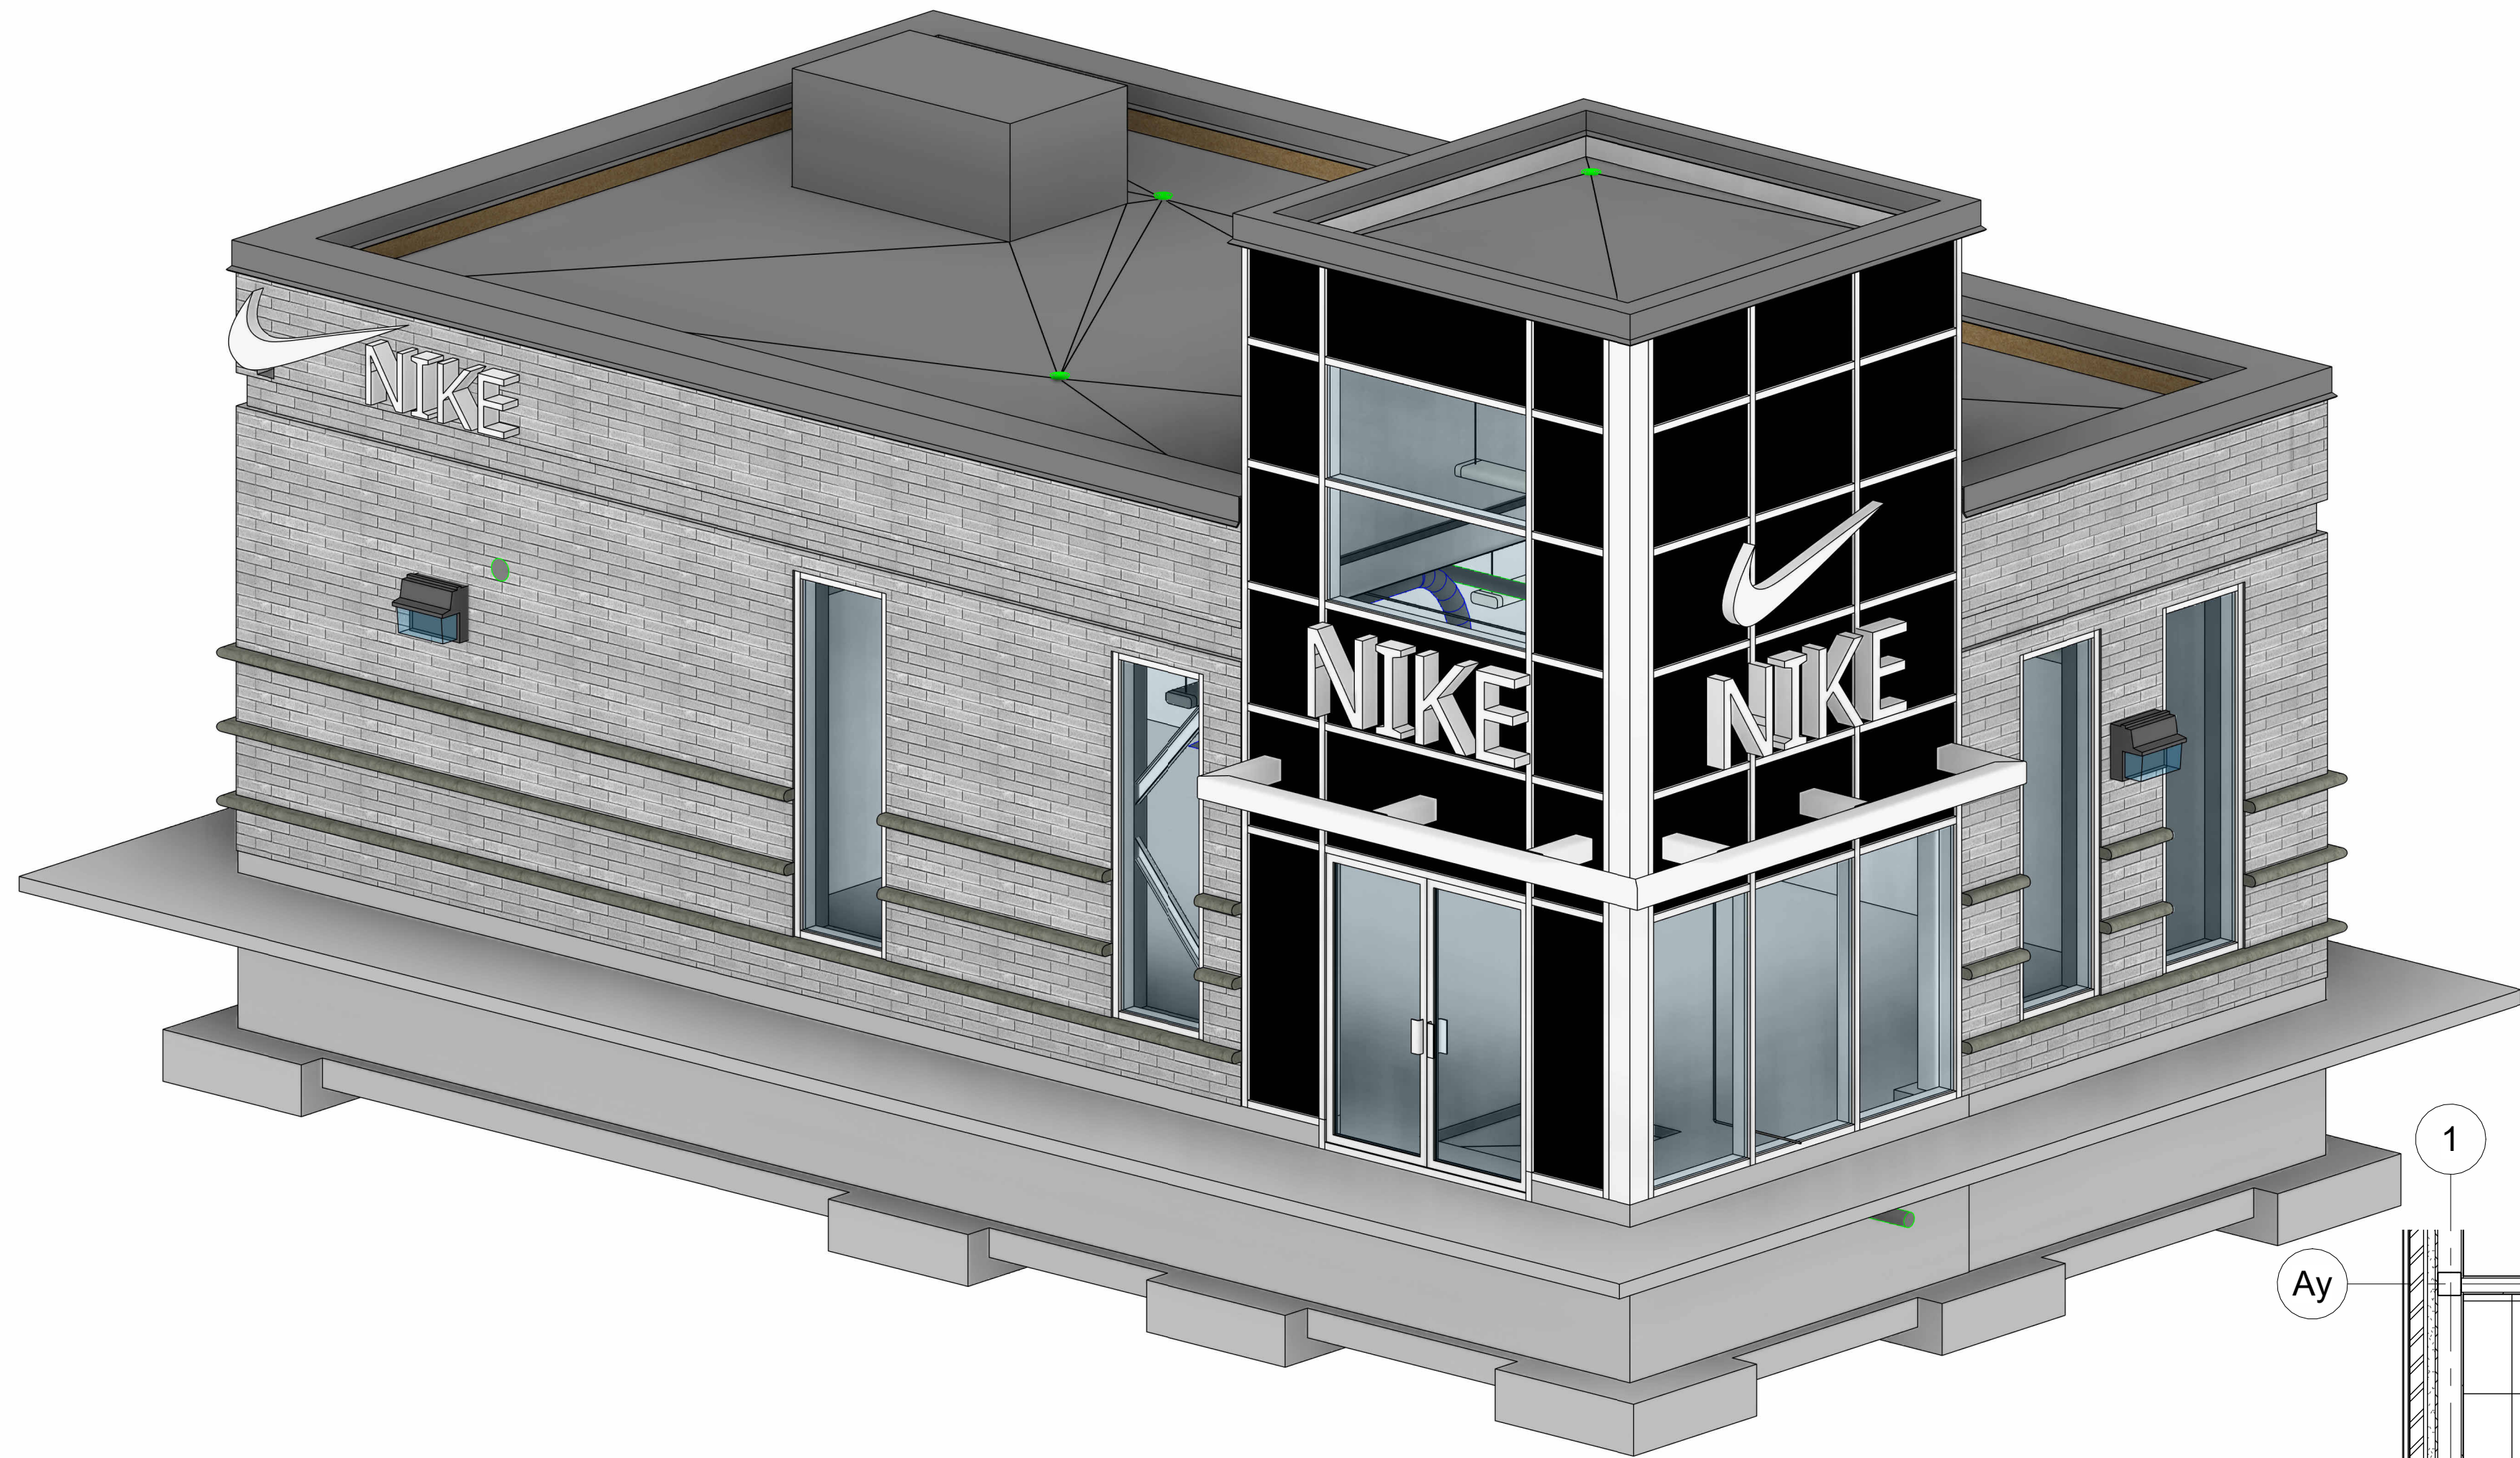

Clay Masonry Material Takeoff	
Material: Name	Material: Area
90 Clay Brick - Grey, Running Bond	110 m ²

Metal Panel Material Takeoff	
Material: Name	Material: Area
Corrugated Metal Siding	16 m ²

Aluminium Panel Material Takeoff	
Material: Name	Material: Area
Aluminium Panel (A.C.P.)	22 m ²

Glazing Material Takeoff	
Material: Name	Material: Area
Glass	20 m ²


Sheet List	
Sheet Name	Sheet Number
FOUNDATION & STRUCTURES	S-101
SYSTEMS (M.E.P.)	M-101
ARCHITECTURE	A-101

BUILDING ASSEMBLIES	
EXTERIOR WALL - ExW1 90 Clay Brick - Grey, Running Bond 25 Air Space 50 Closed Cell Foam Insulation 16 Exterior Grade Sheathing 92 Metal Stud @ 406mm O.C. Max. 13 Gypsum Wall Board - Prime & Paint	EXTERIOR WALL - ExW2 - Corrugated Metal Siding 16 Exterior Grade Sheathing 92 Metal Stud @ 406mm O.C. Max. 13 Gypsum Wall Board - Prime & Paint
FOUNDATION WALL - FD-1 325 CAST IN PLACE CONCRETE	FOUNDATION WALL - FD-3 200 CAST IN PLACE CONCRETE
INTERIOR PARTITION - PT-1 13 Gypsum Wall Board - Prime & Paint 92 Metal Stud @ 406mm O.C. Max. 13 Gypsum Wall Board - Prime & Paint	INTERIOR PARTITION - PT-2 13 Gypsum Wall Board - Prime & Paint 152 Metal Stud @ 406mm O.C. Max. 13 Gypsum Wall Board - Prime & Paint
CURTAIN WALL - CW-1 - Aluminum Curtain Wall - Framing c/w Thermally Broken Glazing & A.C.P.	CEILING (A.C.T.) - CL-1 600x600 Acoustic Ceiling Tile
CONC. SLAB ON GRADE - FL-1 100 CAST IN PLACE CONCRETE	EPDM MEMBRANE ROOF - RF-1 - EPDM Roof Membrane 200 Rigid Board Insulation


REVISIONS		
NO.	DATE	REVISION

Key Plan


North Arrow

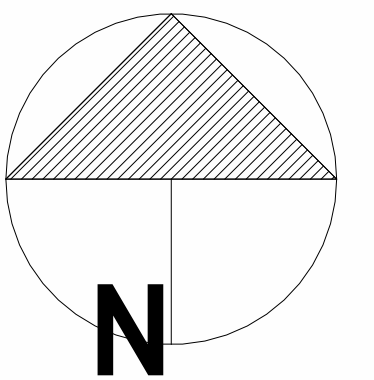


1 BIM ISOMETRIC - ARCHITECTURAL

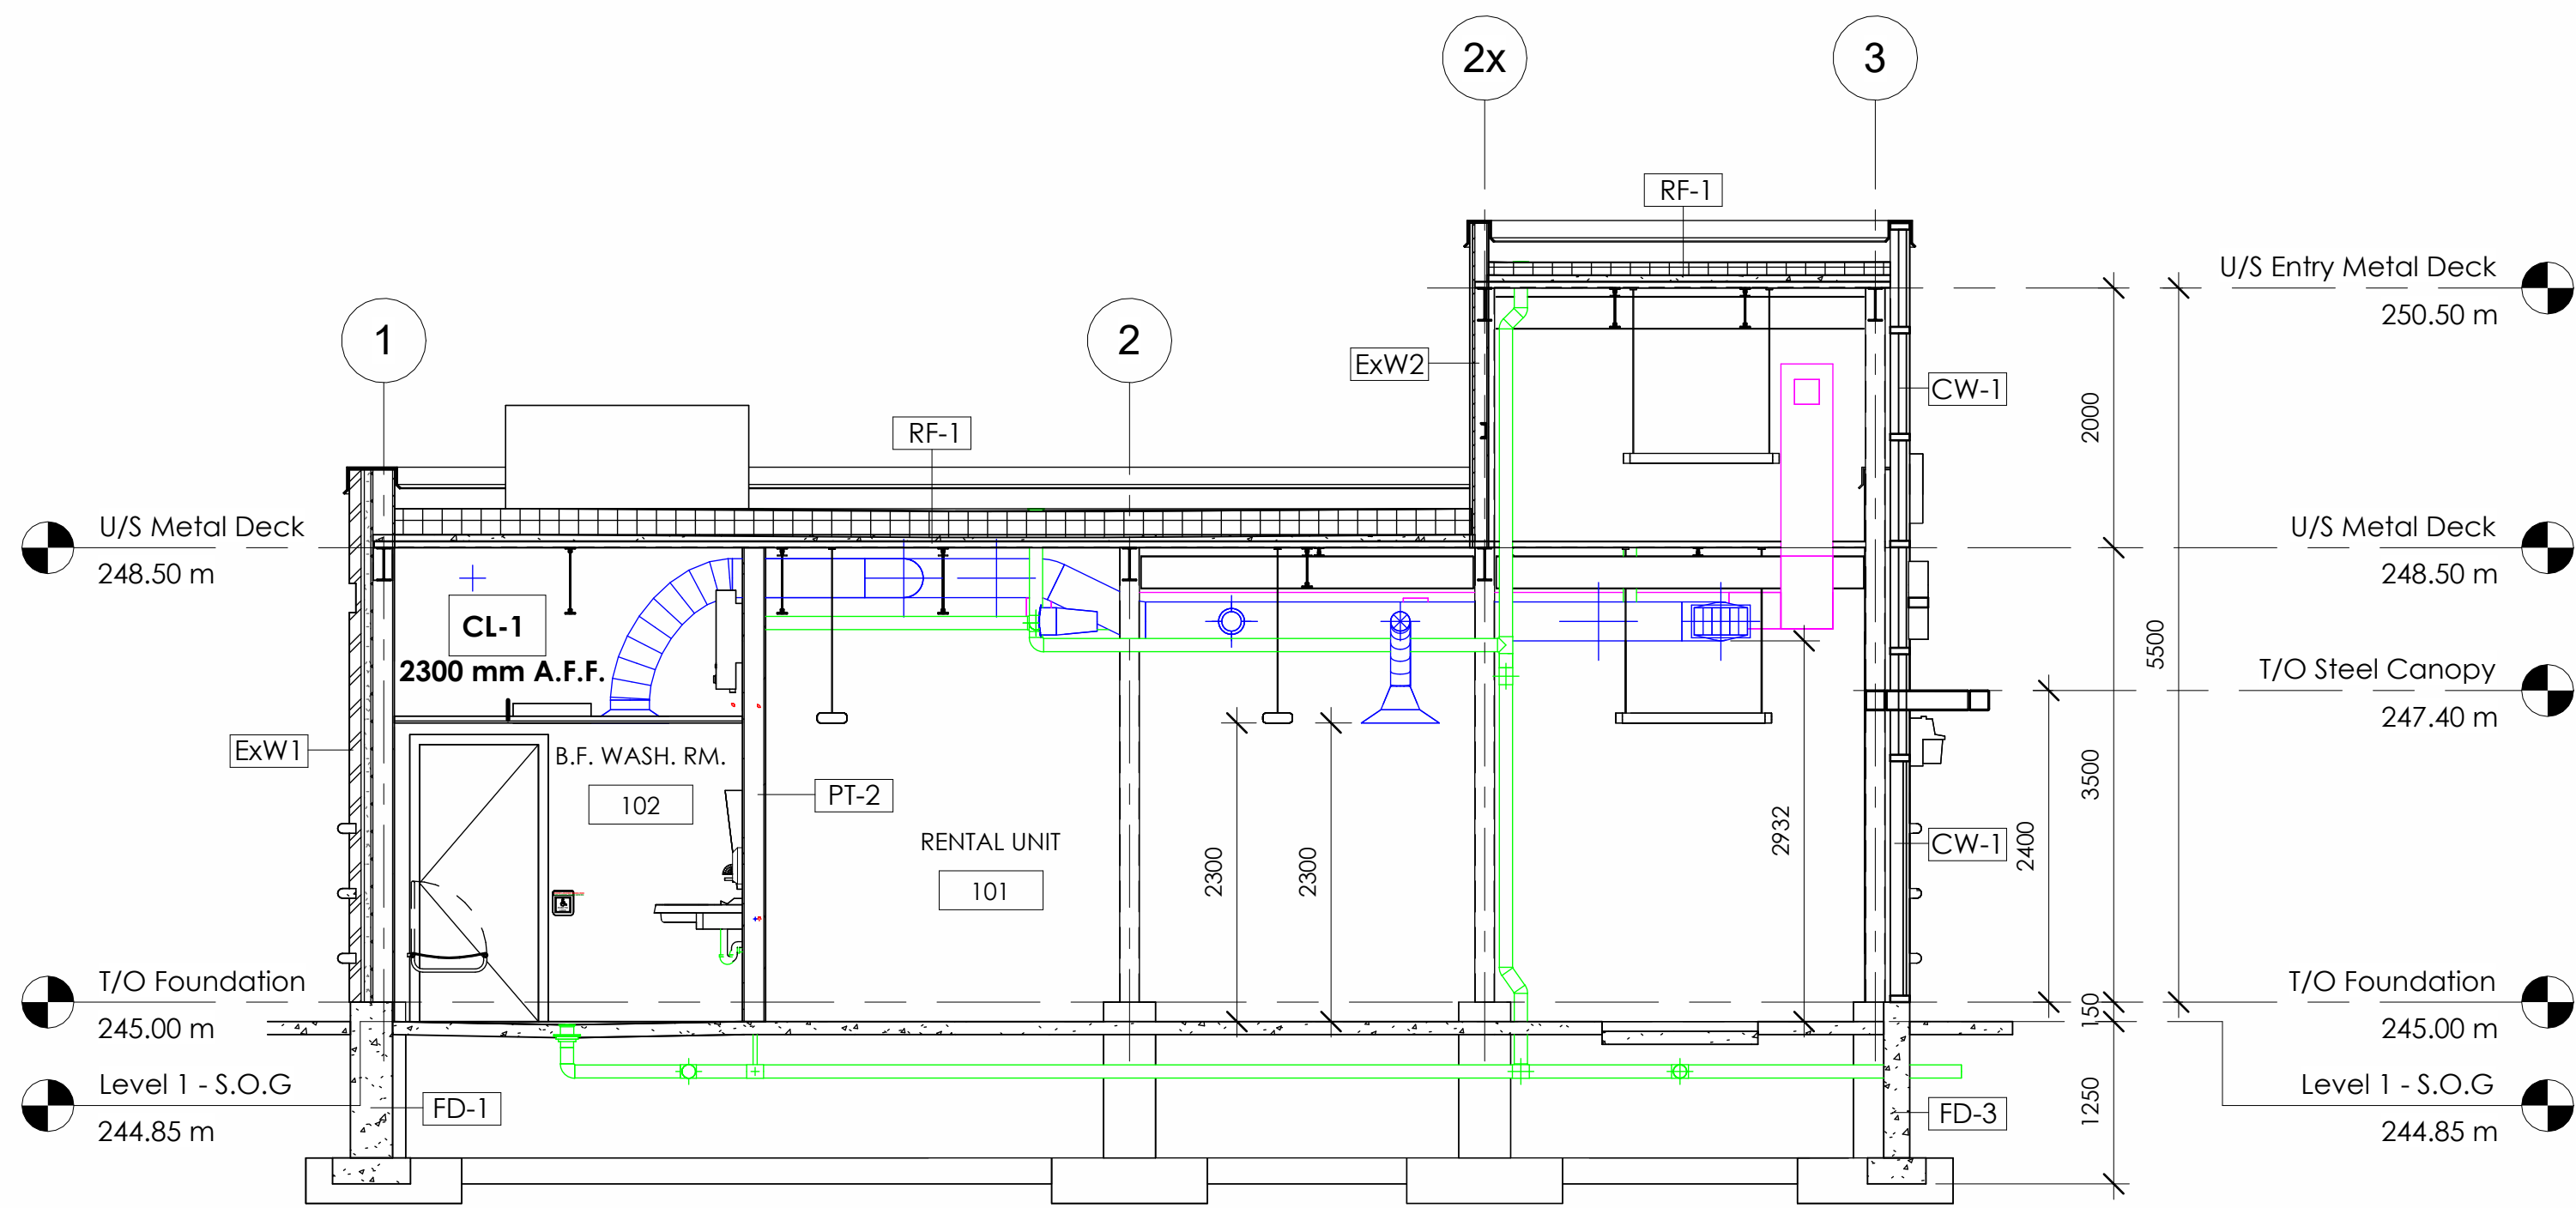


2 EAST-WEST BUILDING SECTION
1:50

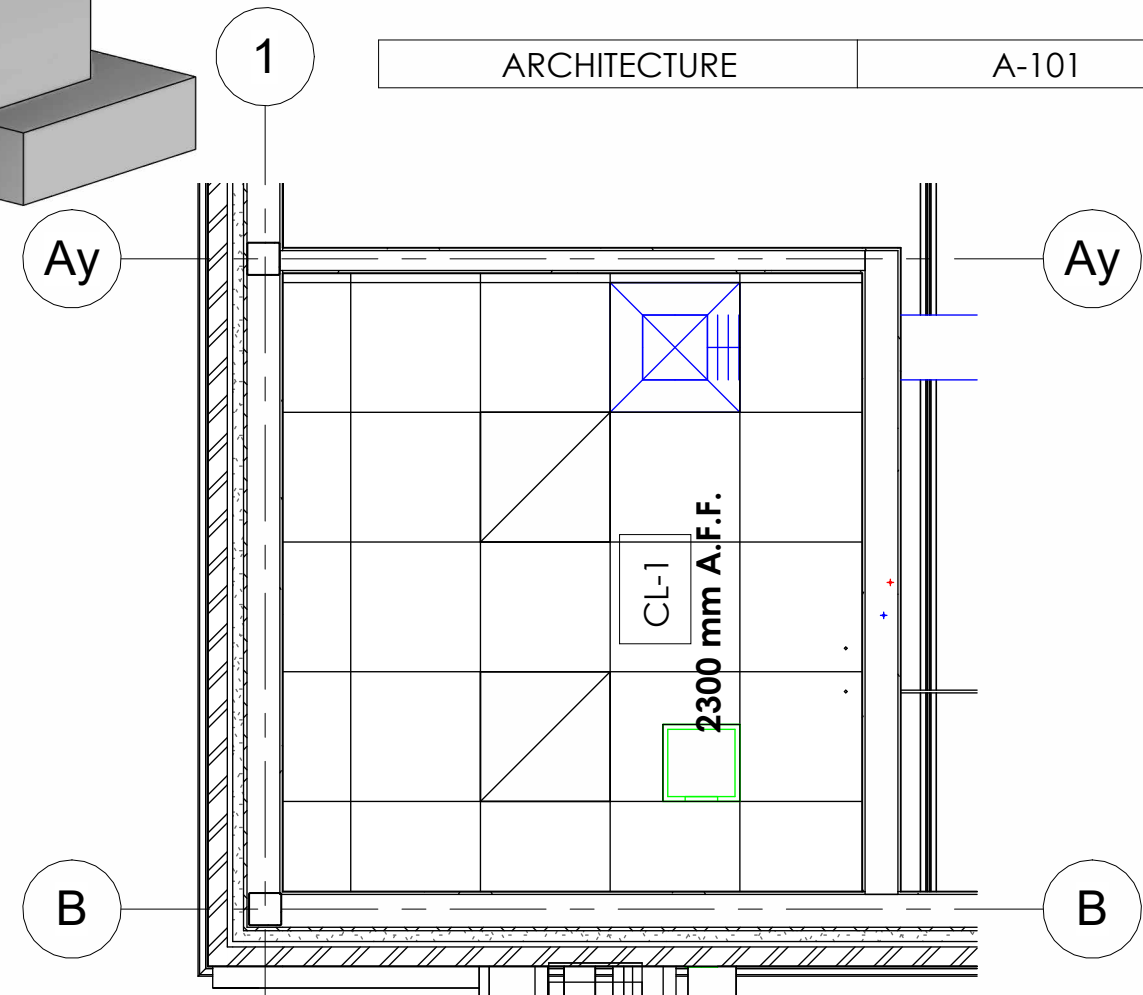

3 WASH. ROOM R.C.P.
1:35

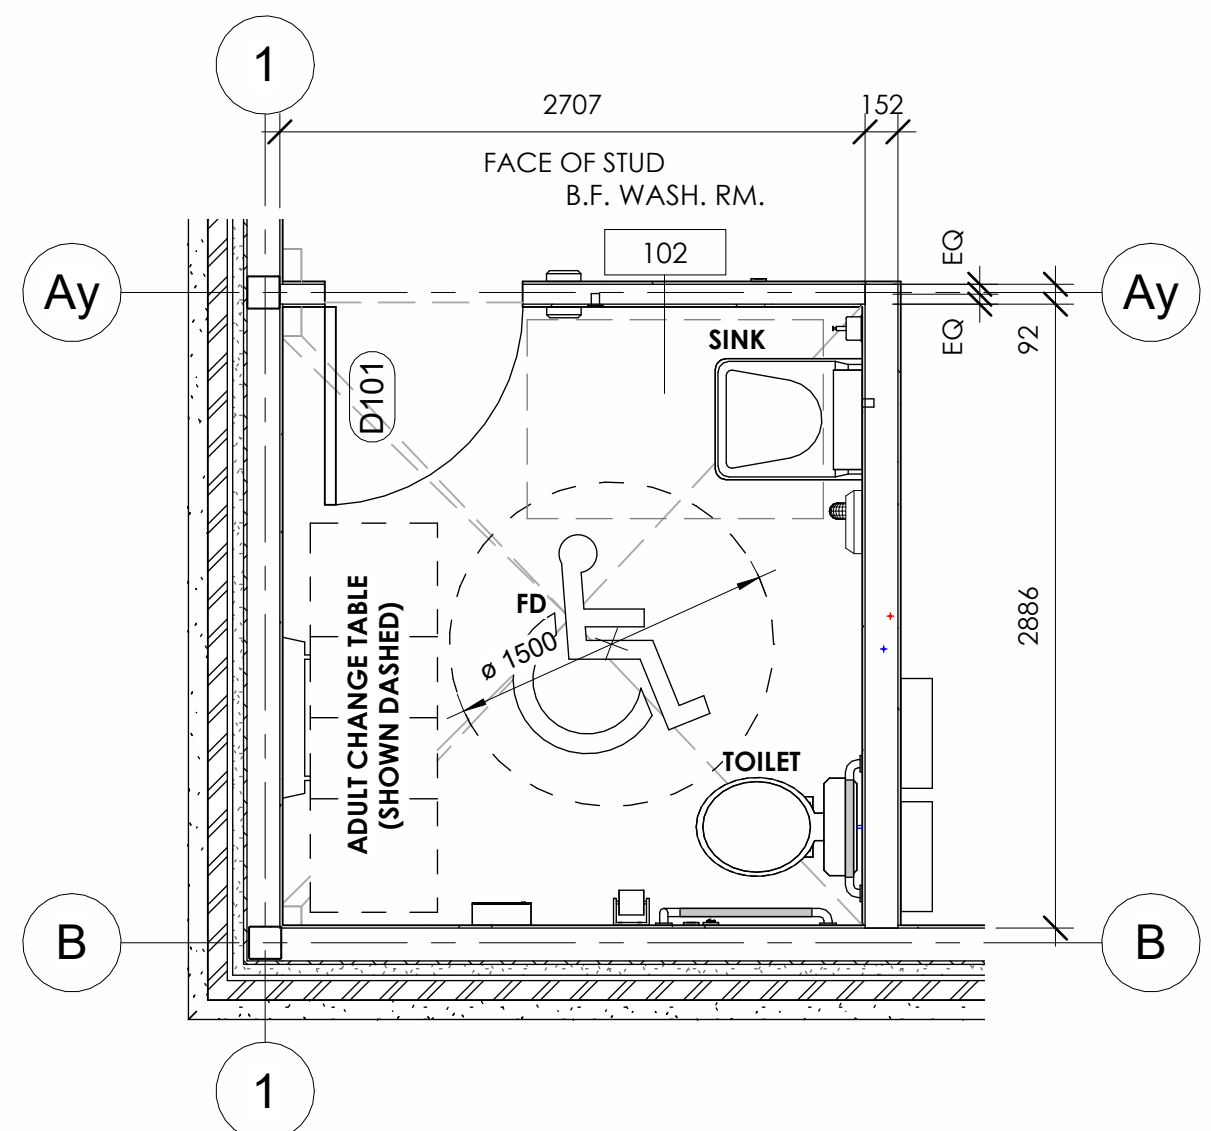

4 Enlarged B.F. Washroom Plan
1:35

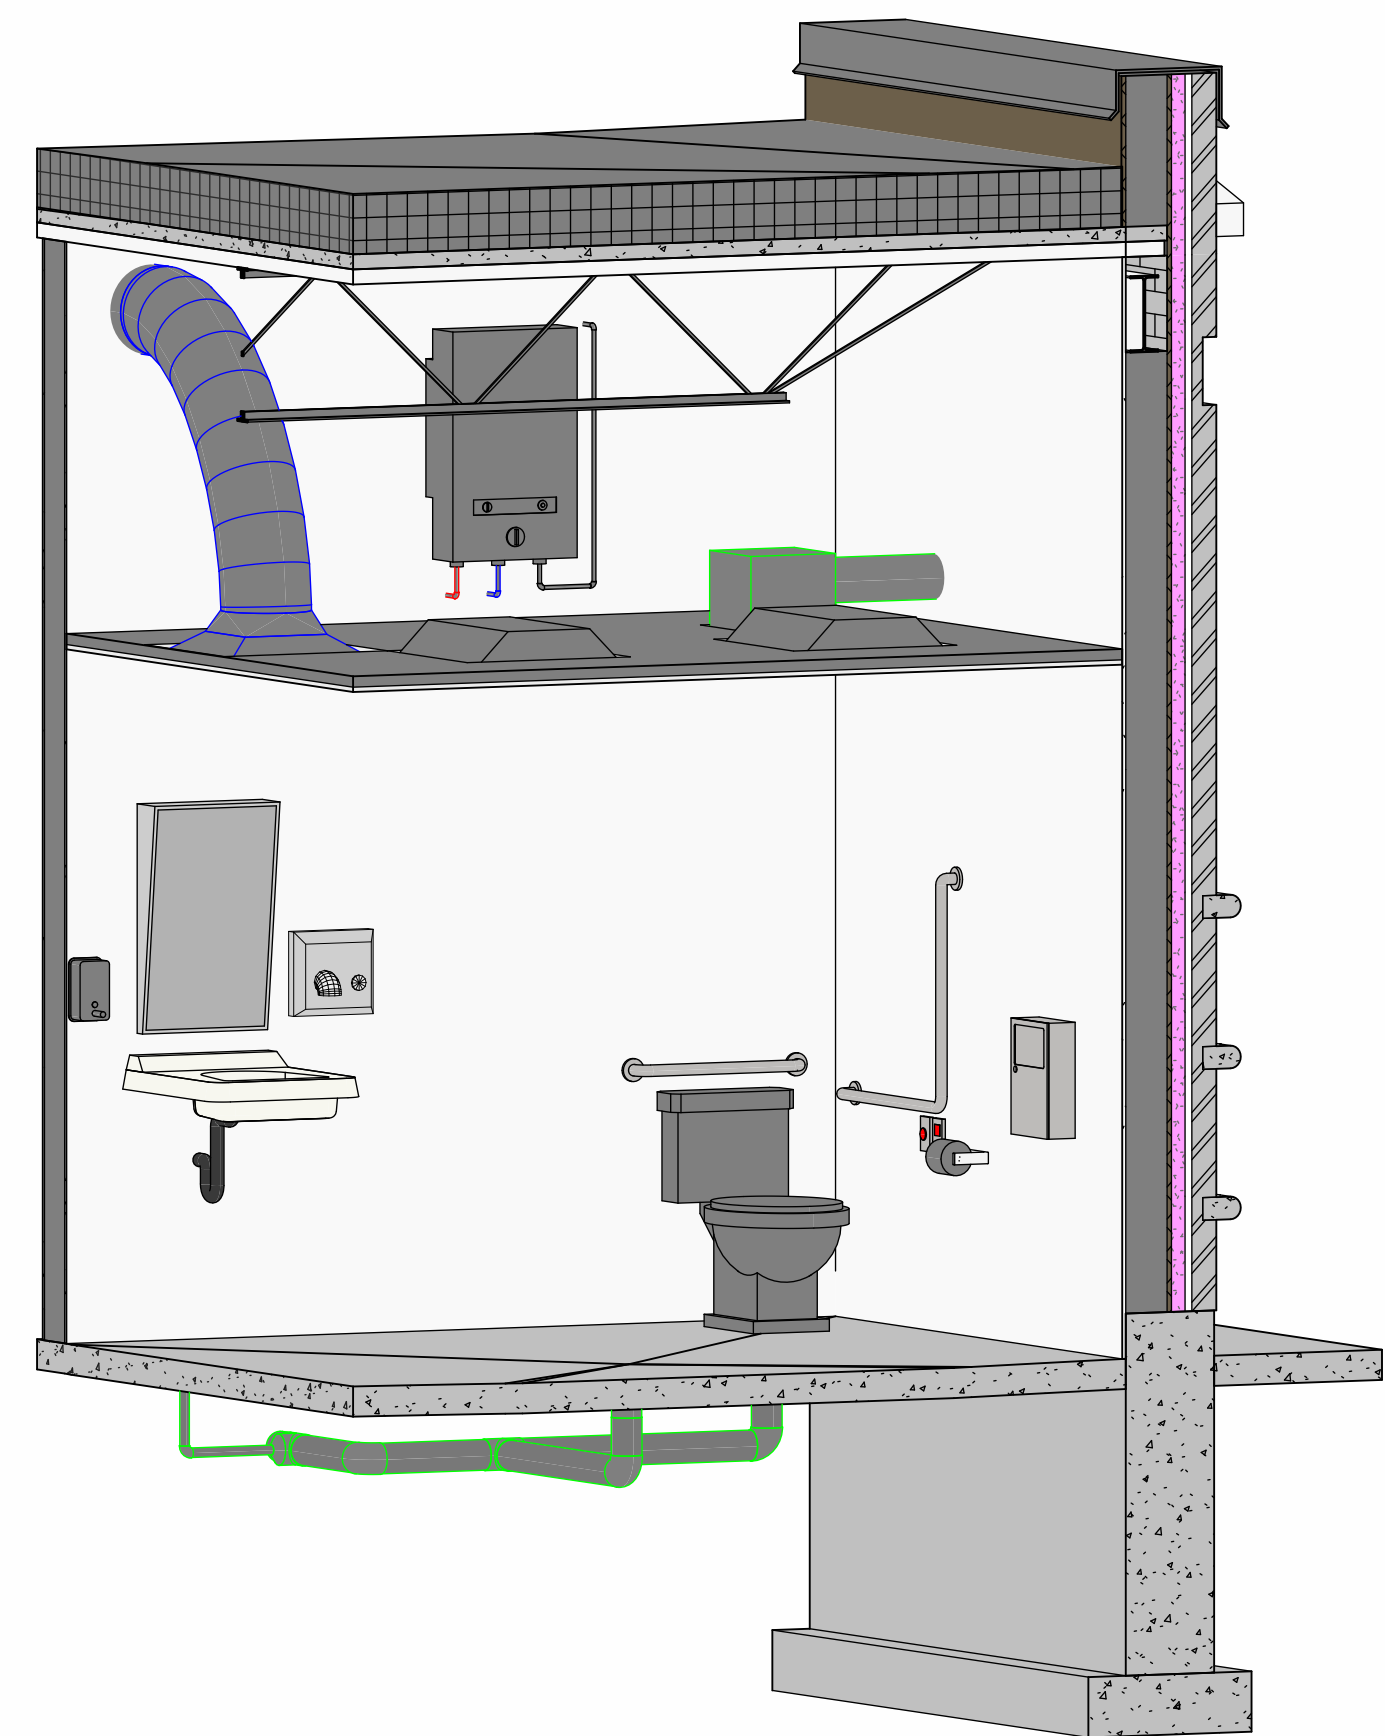

5 B.F. WASHROOM ISOMETRIC

FANSHAWE
School of Building Technology
ARCHITECTURAL
TECHNOLOGY

PROJECT TITLE
Capstone Commerical
Project

PROJECT ADDRESS
1001 Commercial Way,
London, ON

DRAWING TITLE
ARCHITECTURE

DRAWN AFNM	DATE 01/04/25
W2025-VDC	A-101
CLASS No.	REVISION