
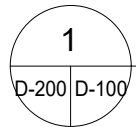


| ZONE: RSC3                | ALLOWABLE              |           | PROVIDED               |       |
|---------------------------|------------------------|-----------|------------------------|-------|
| LOT AREA (MIN):           | 3123.52 m <sup>2</sup> |           | 3123.52 m <sup>2</sup> |       |
| LOT FRONTAGE (MIN):       | 45 m                   |           | 70.5 m                 |       |
| LOT DEPTH (MIN):          | 60 m                   |           | 46.9 m                 |       |
| LANDSCAPED AREA (MIN):    | 468.528 m <sup>2</sup> | 15 %      | 1327.6 m <sup>2</sup>  | 42.5% |
| LOT COVERAGE (MAX):       | 937.056 m <sup>2</sup> | 30 %      | 631.5 m <sup>2</sup>   | 20.2% |
| BUILDING HEIGHT (MAX):    | 12.00 m                |           | 4.68 m                 |       |
| GROSS FLOOR AREA (GFA):   | 6000 m <sup>2</sup>    |           | 424.15 m <sup>2</sup>  |       |
| GFA FOR OFFICE USE (MAX): | 2000 m <sup>2</sup>    | 33.3333 % | 17.41                  | 4.1%  |
| PARKING REQUIREMENT:      | 5 Spaces               |           | 12 Spaces              |       |

| SITE LEGEND              |  |
|--------------------------|--|
| Main Entrance            |  |
| Light Post               |  |
| Secondry Entry / Exit    |  |
| Barrier Free             |  |
| Coniferous Tree          |  |
| Shrub                    |  |
| Stop Sign                |  |
| Traffic Direction Arrows |  |
| Trash Can                |  |
| Bench                    |  |
| Crosswalk                |  |
| Fire Route               |  |

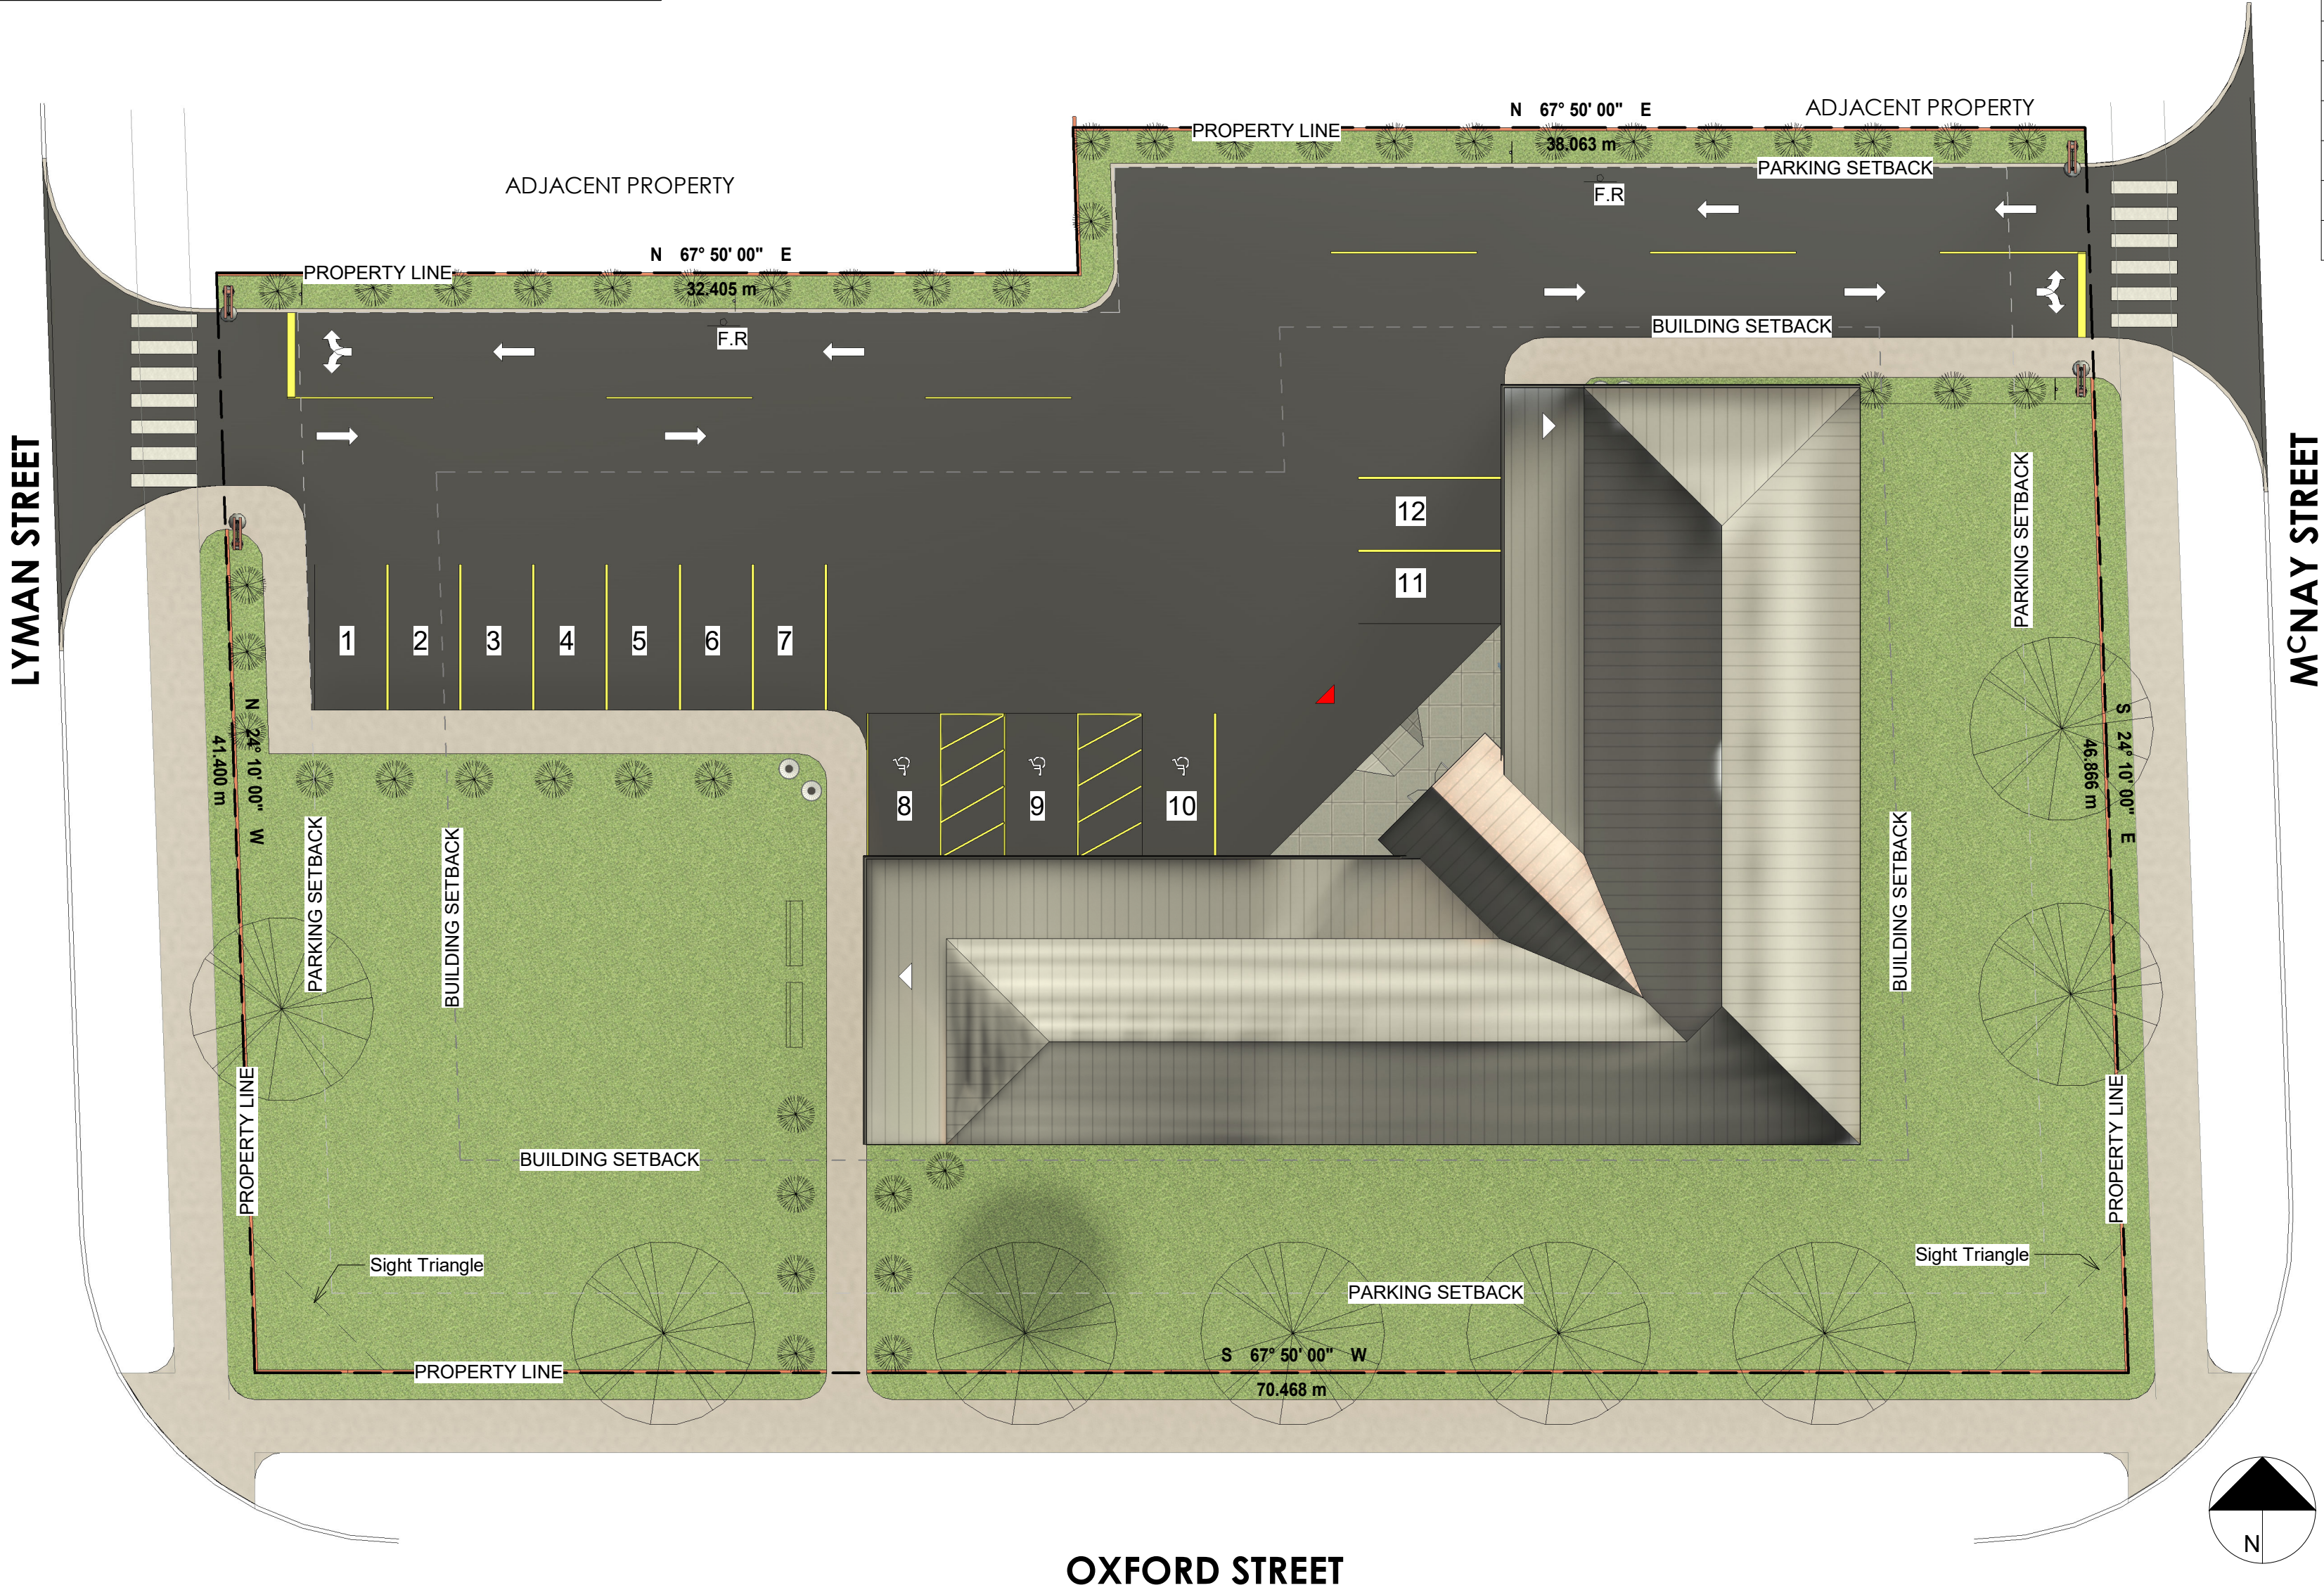


PROPOSED SITE PLAN

1 : 200



OXFORD WELLNESS CENTRE

DESIGN SITE PLAN

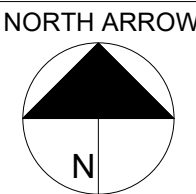

|              |              |
|--------------|--------------|
| PROJECT No.: | W24-001      |
| DATE:        | 15-02-24     |
| DRAWN BY:    | ABUL MOHAMED |
| CHECKED BY:  | Checker      |


D-100

SCALE: 1 : 200



Room Legend

- CONSULTATION
- CORRIDOR
- I.T
- JANITOR
- LAUNDRY
- MAIN VESTIBULE
- MECH.
- OFFICE
- RECEPTION
- STAFF LOUNGE
- STAFF WASH
- STAFF.VEST
- SUPPLY ROOM
- TREATMENT
- U.T.R
- WAITING ROOM
- WASHROOM

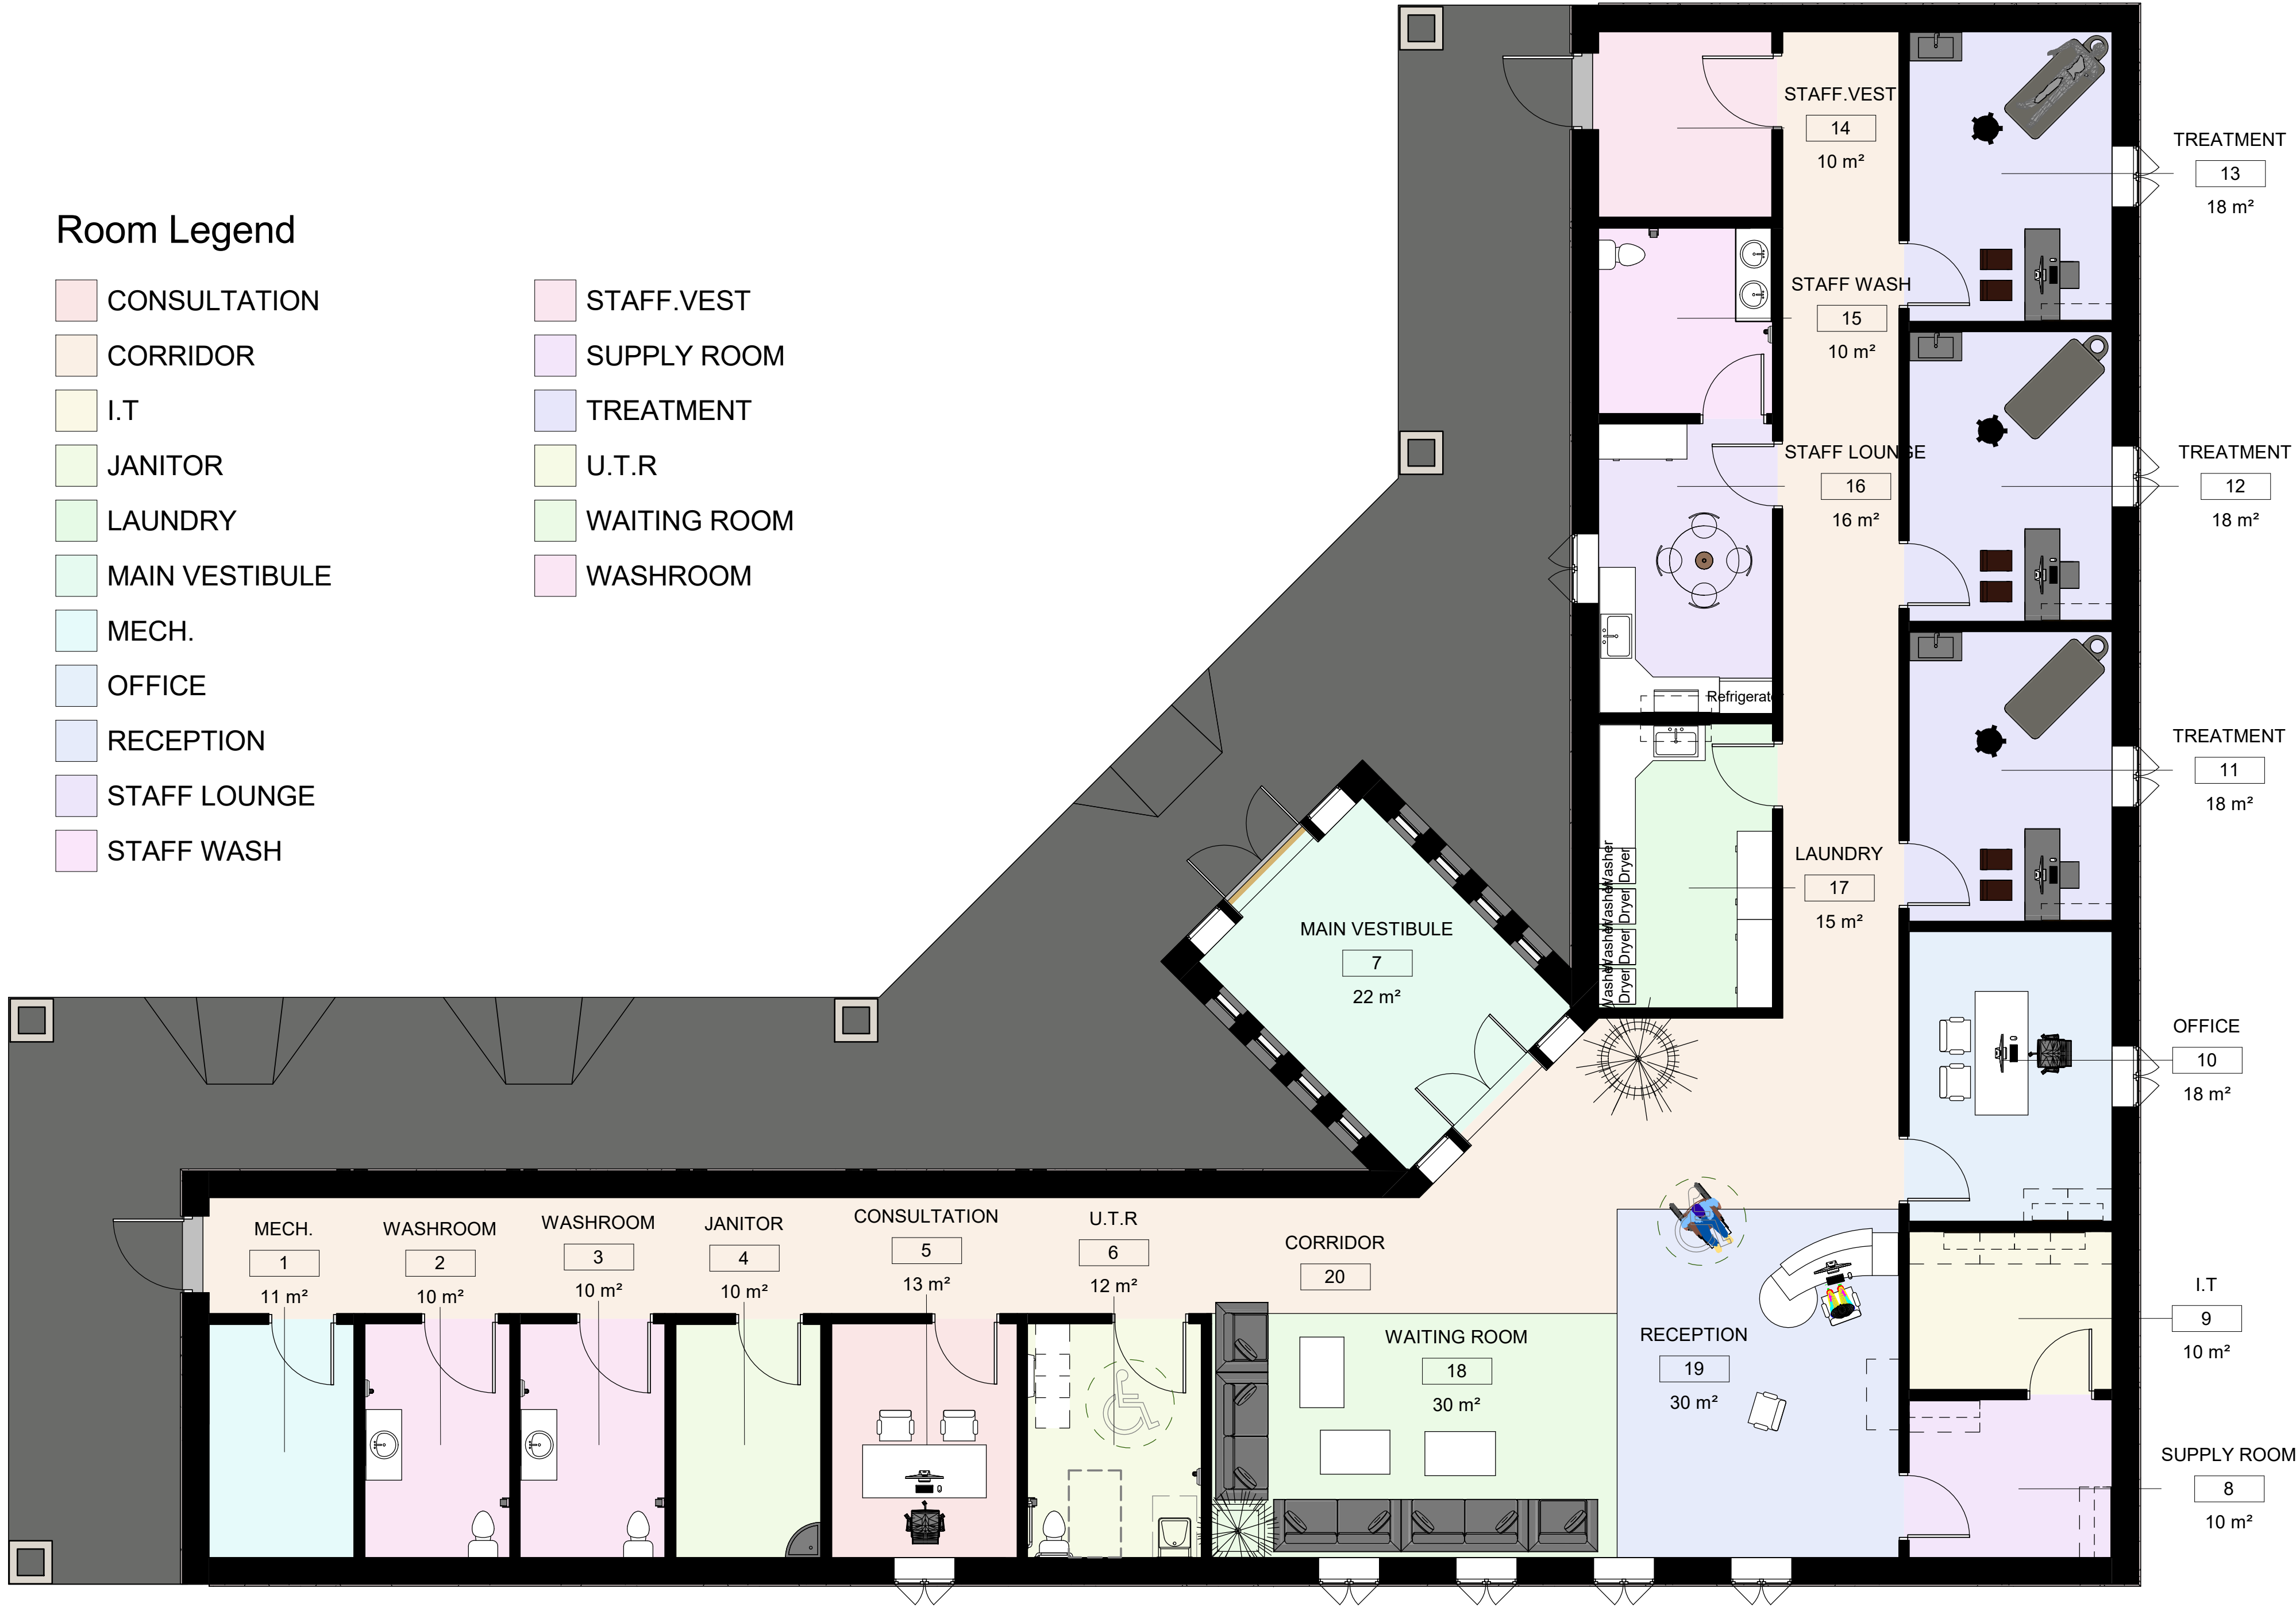

1  
D-200 D-101


PROPOSED FLOOR PLAN

1 : 75



OXFORD WELLNESS CENTRE

DESIGN FLOOR PLAN

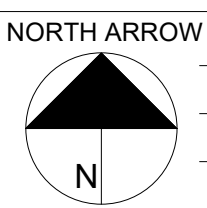

|              |              |
|--------------|--------------|
| PROJECT No.: | W24-001      |
| DATE:        | 15-02-24     |
| DRAWN BY:    | ABUL MOHAMED |
| CHECKED BY:  | Checker      |

D-101



1 : 75

C:\Users\la\_noormohamed226110\Desktop\Arch-1030 - CMU Wellness Centre.rvt 2/15/2024 12:48:53 PM







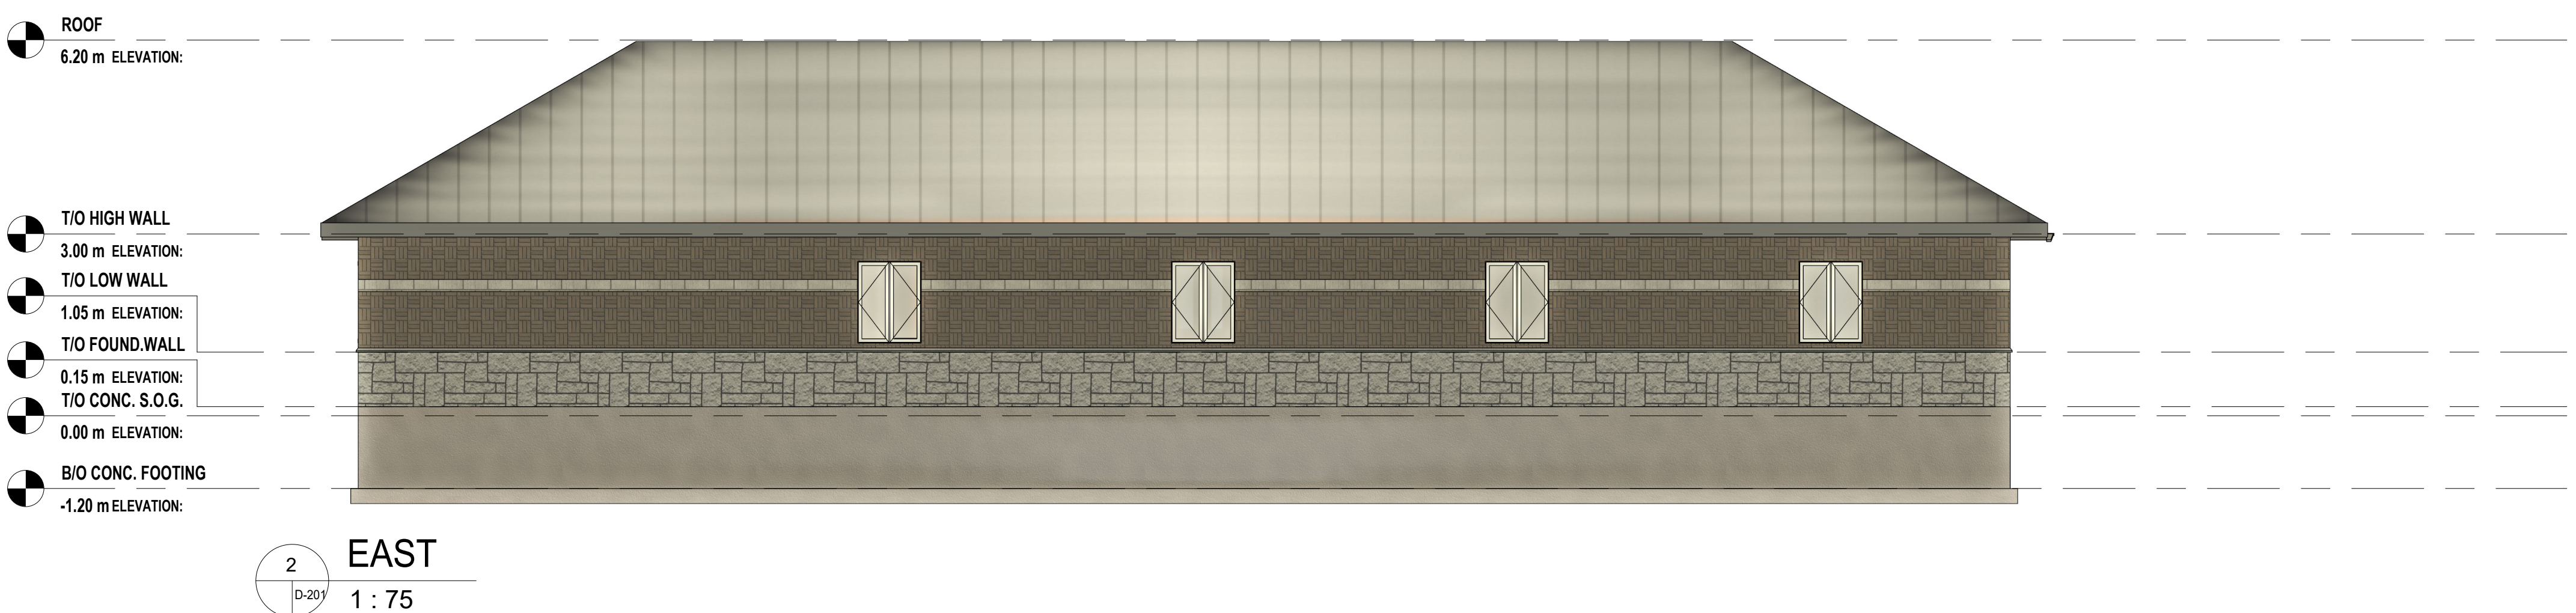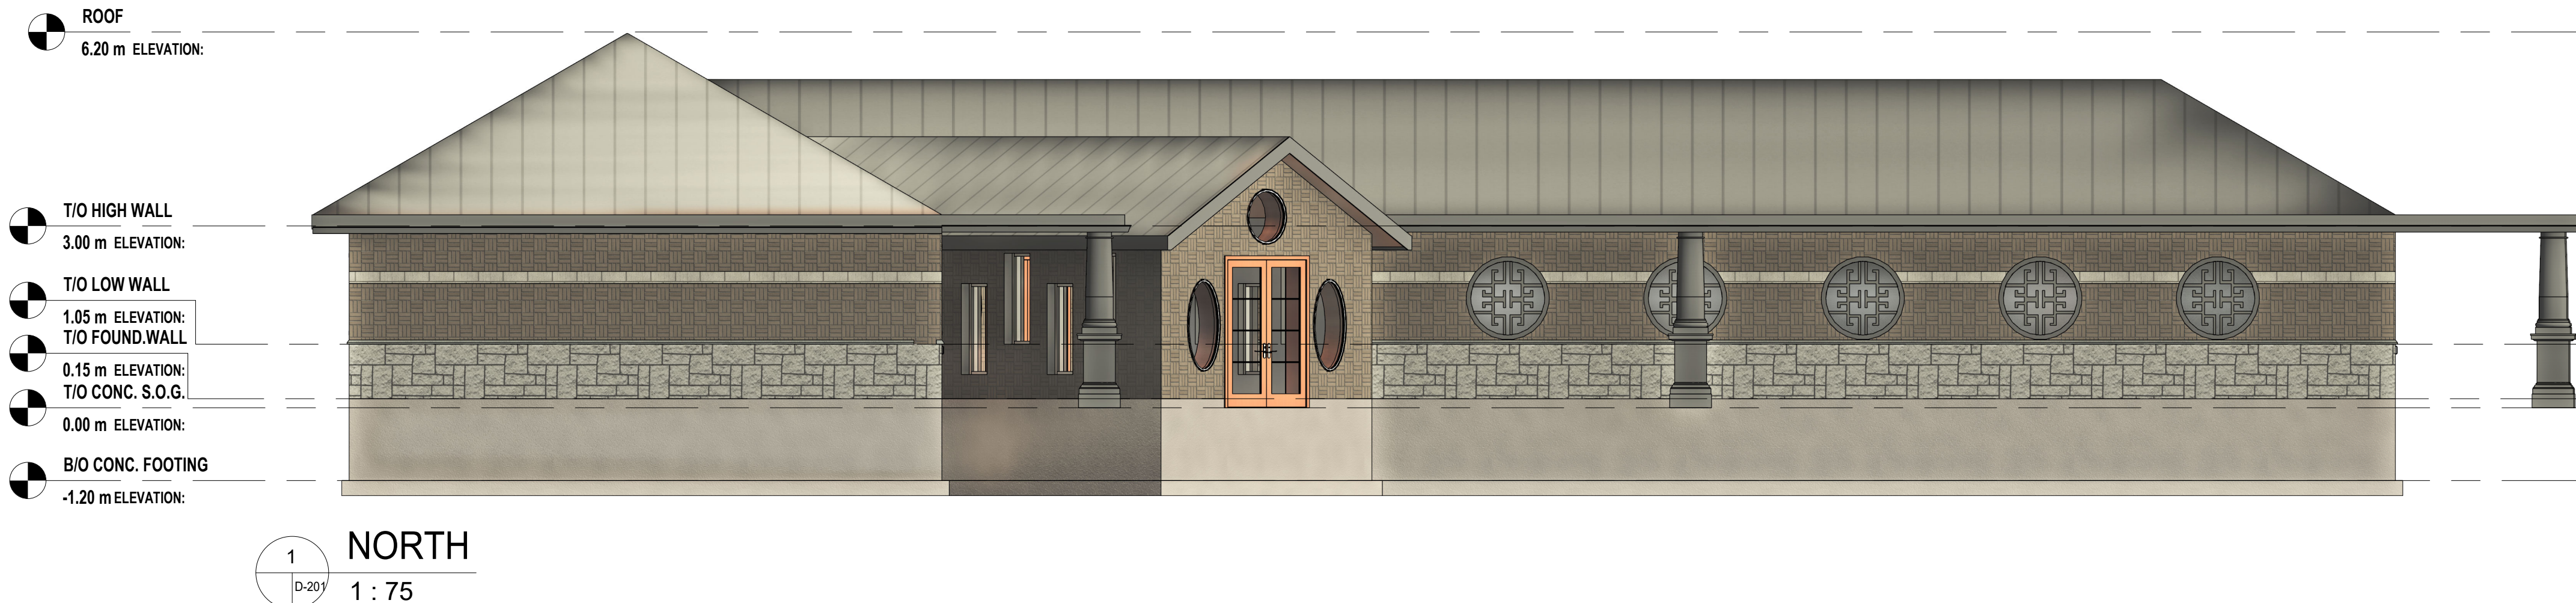





1 Main Entrance  
D-300



2 Oxford Street  
D-300



3 Waiting Area  
D-300



4 Oxford Street 1  
D-300