
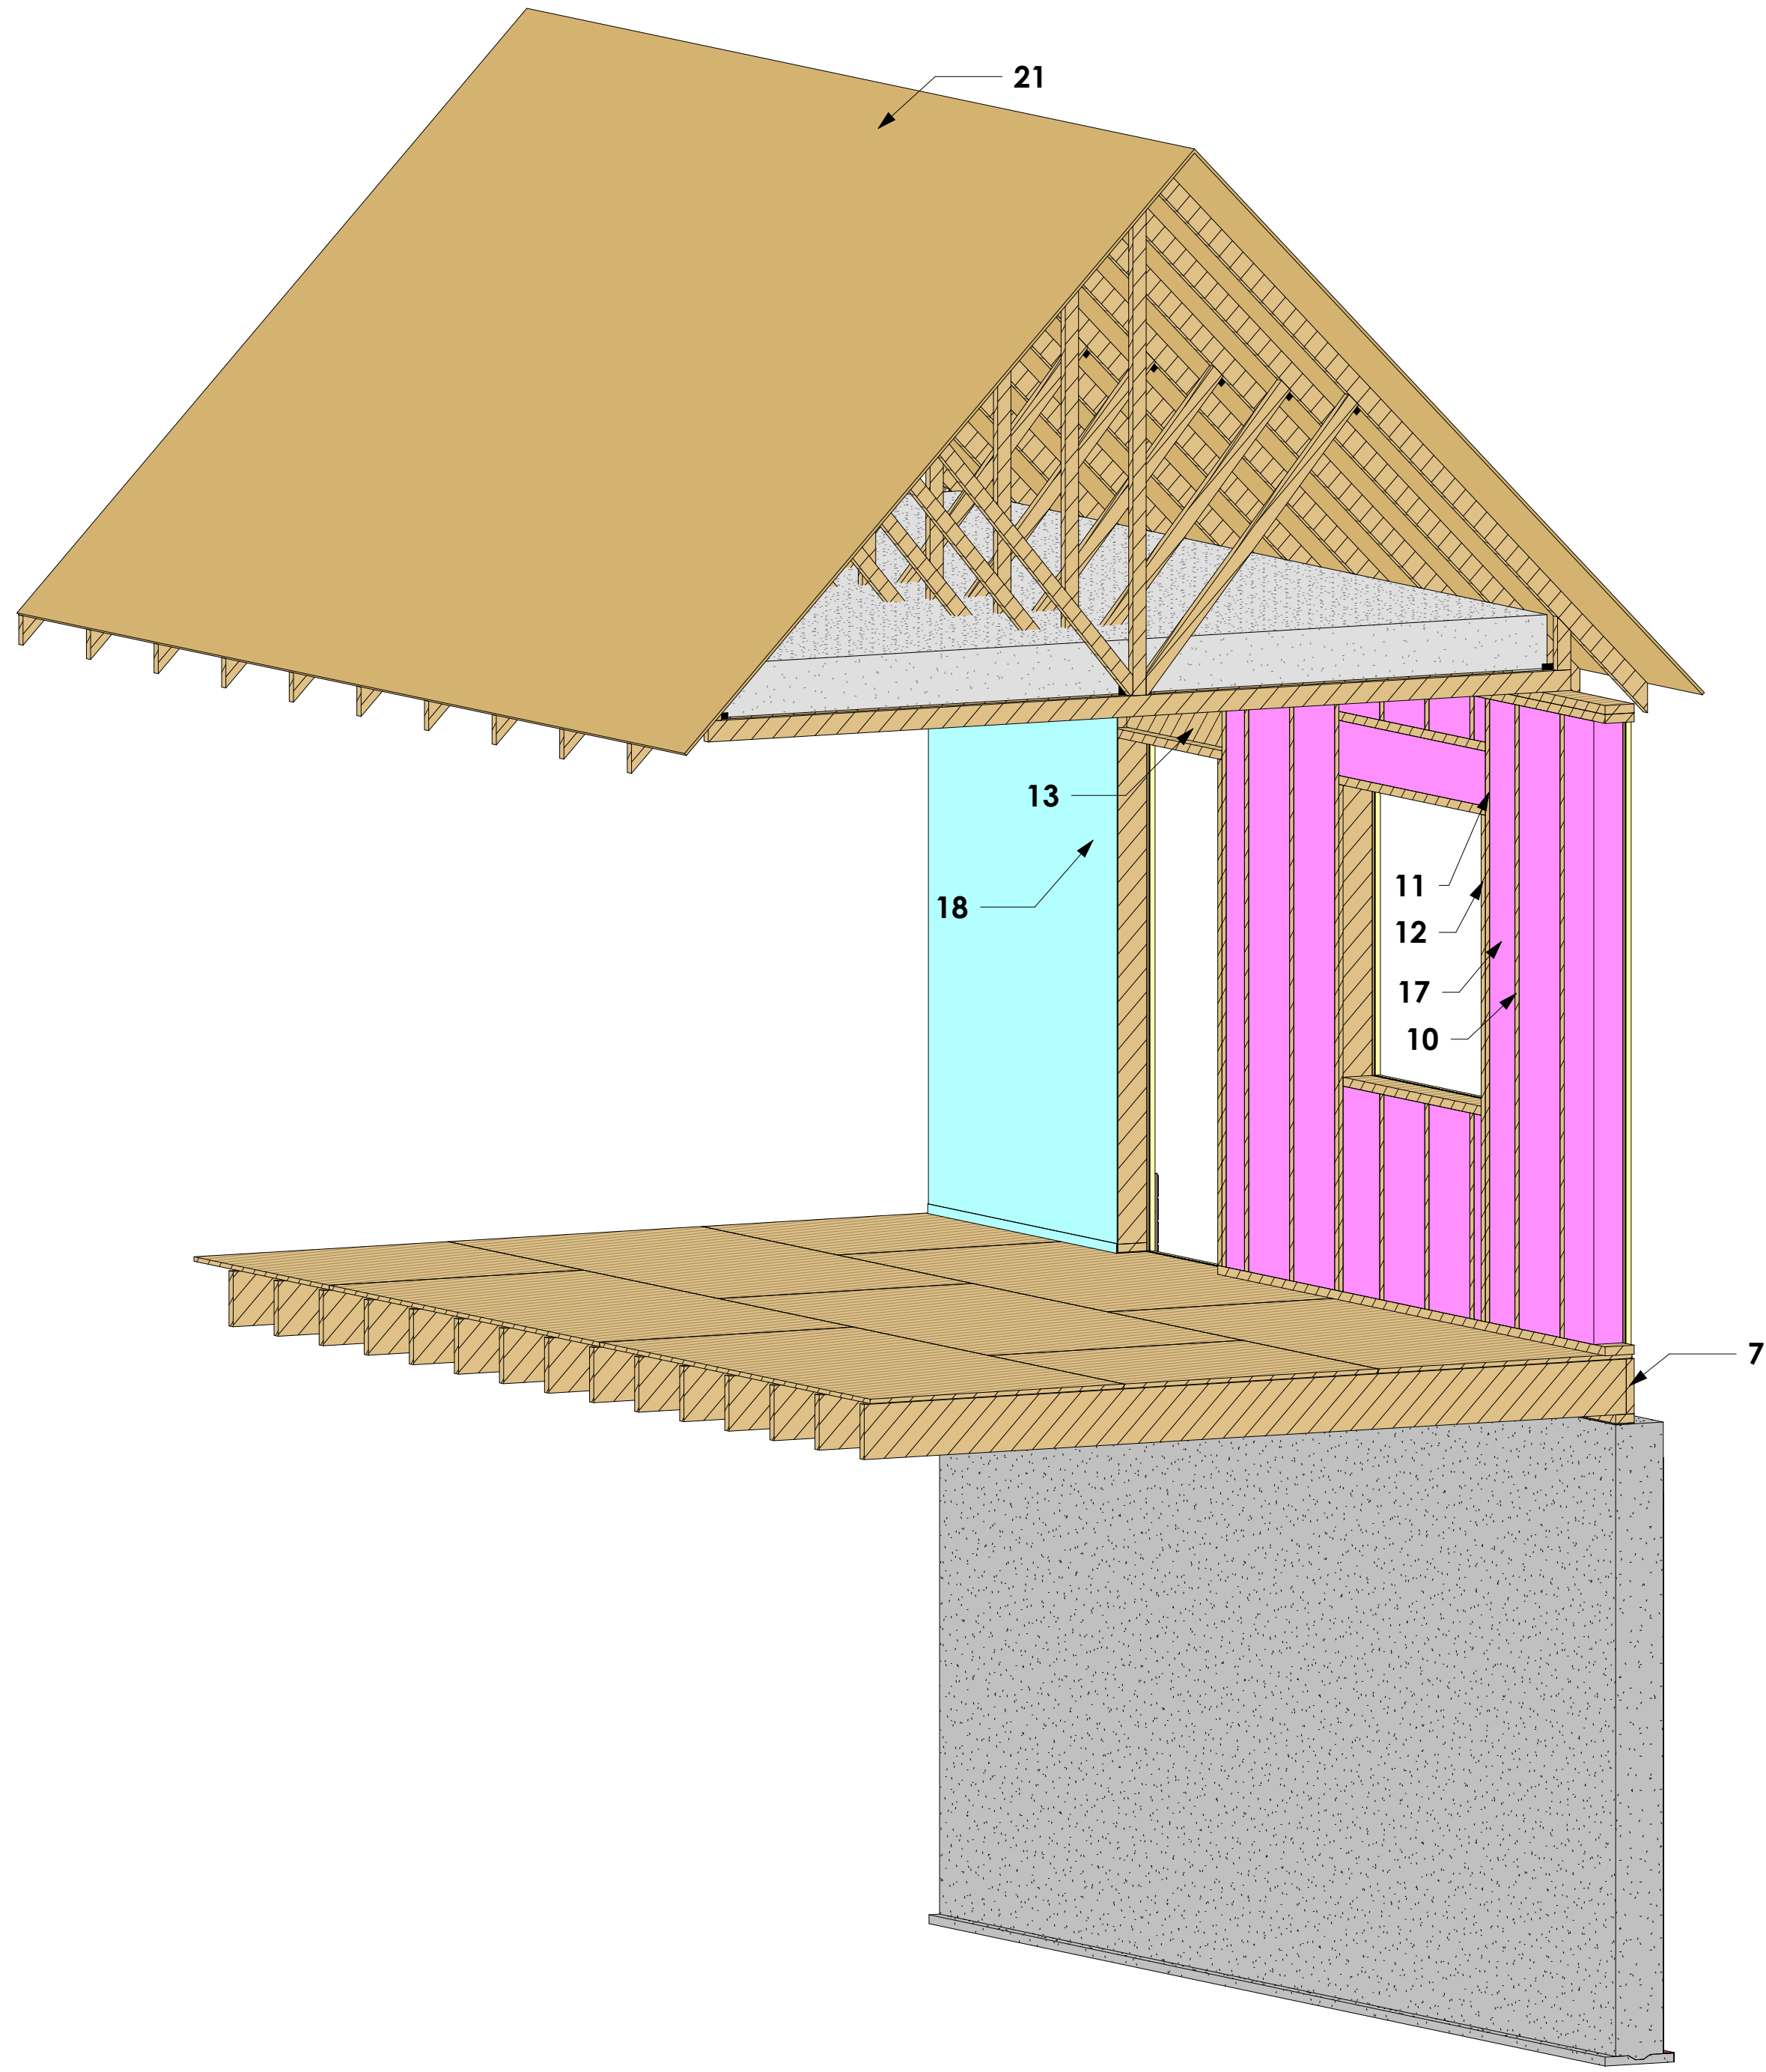


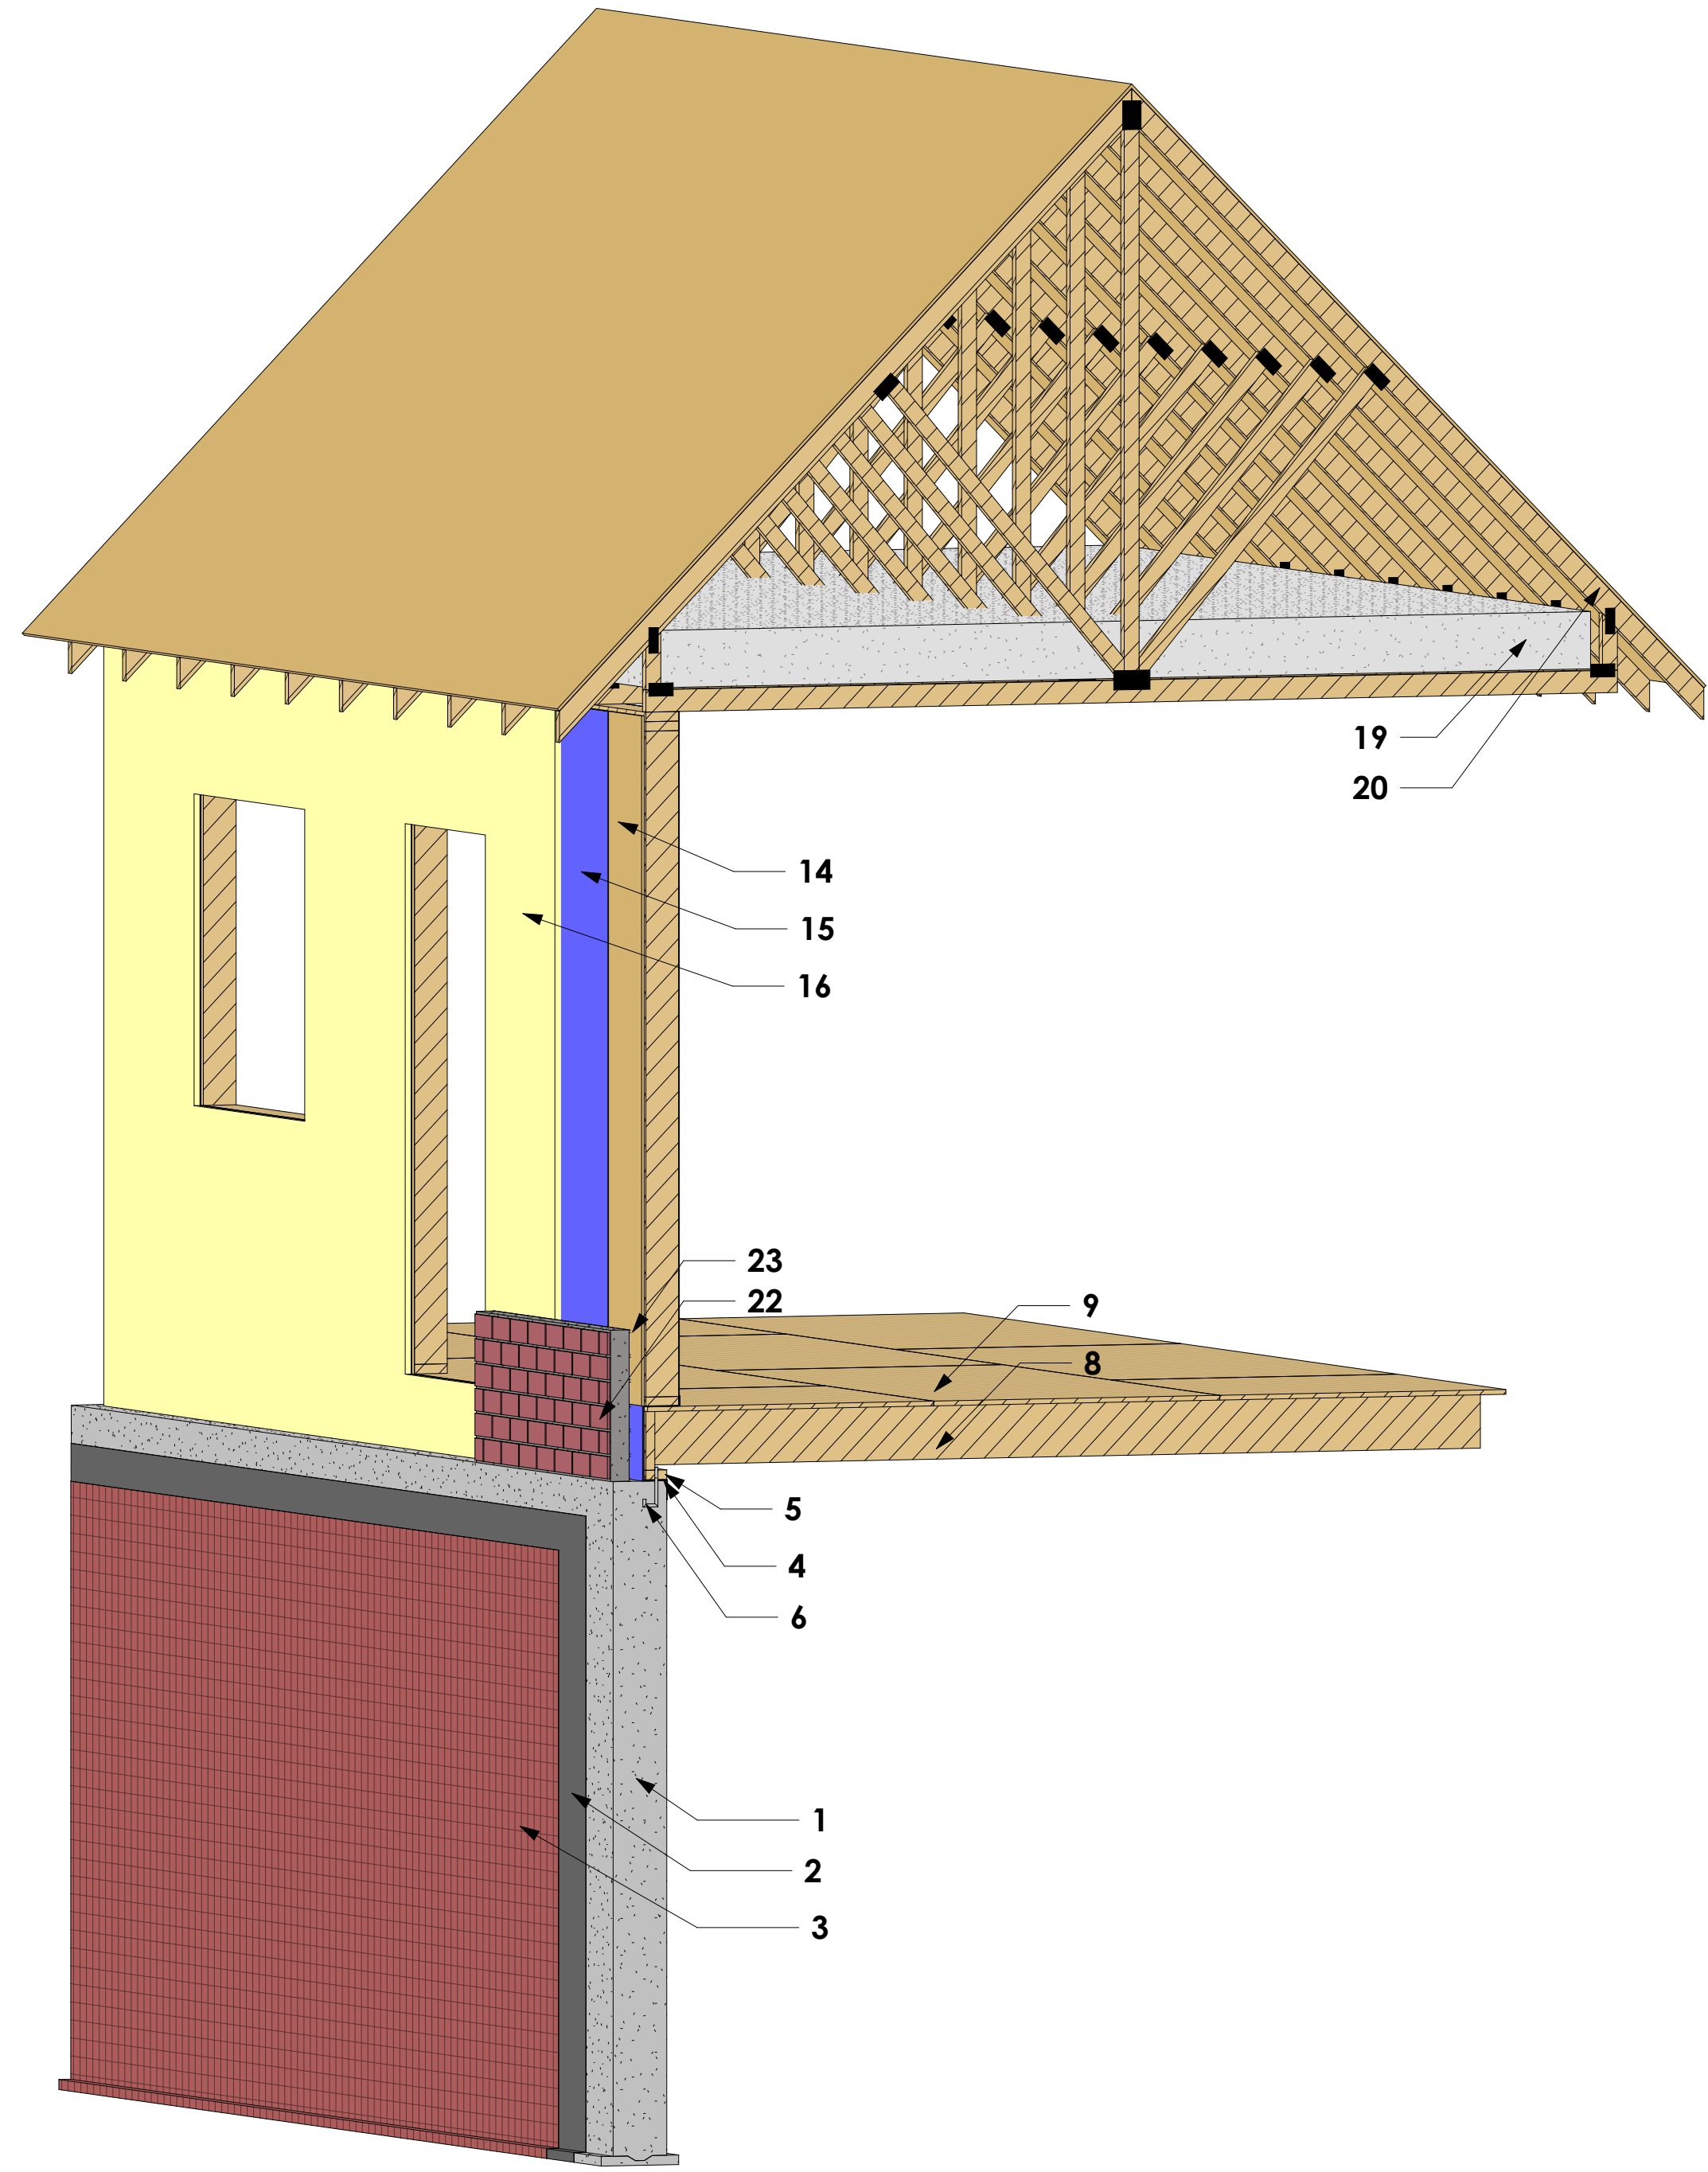

MATERIAL LEGEND

1. 9" Foundation Wall	6. Anchor Bolts	11. 2x6 Kind Stud	16. R5 1" Rigid Insulation - Manufacturer - Johns Manville	21. 1/2" Plywood Sheathing (Roof)
2. Waterproofing Membrane - Manufacturer - SOPREMA	7. 2x10 Rim Joist	12. 2x6 Jack Stud	17. R19 Batt Insulation - Manufacturer - Johns Manville	22. 3 1/2" Deep Brick
3. Drainage Mat - Manufacturer - Canada Mats	8. 2x10 Floor Joist	13. 2-2x10 Lintel	18. Vapour Barrier (Walls and Ceiling) - Manufacturer - 3M™	23. 1" Air Space
4. Sill Gasket - Manufacturer - Owens Corning	9. 3/4 Plywood Sheathing (Floor)	14. 7/16" OSB Sheathing (Wall)	19. R50 Blown In Insulation(Attic) - Manufacturer - Johns Manville	
5. 2x4 Sill	10. 2x6 Studs @ 16 o.c.	15. Air Barrie - Manufacturer - 3M™	20. Pre-Eng Roof Truss @ 24" o.c.	

MATS-3010
Assignment 1

SCALE 1/2" = 1'-0"

1/2" = 1'-0"

Owner



Architectural Technology

School of Building Technology

London Ontario Canada