


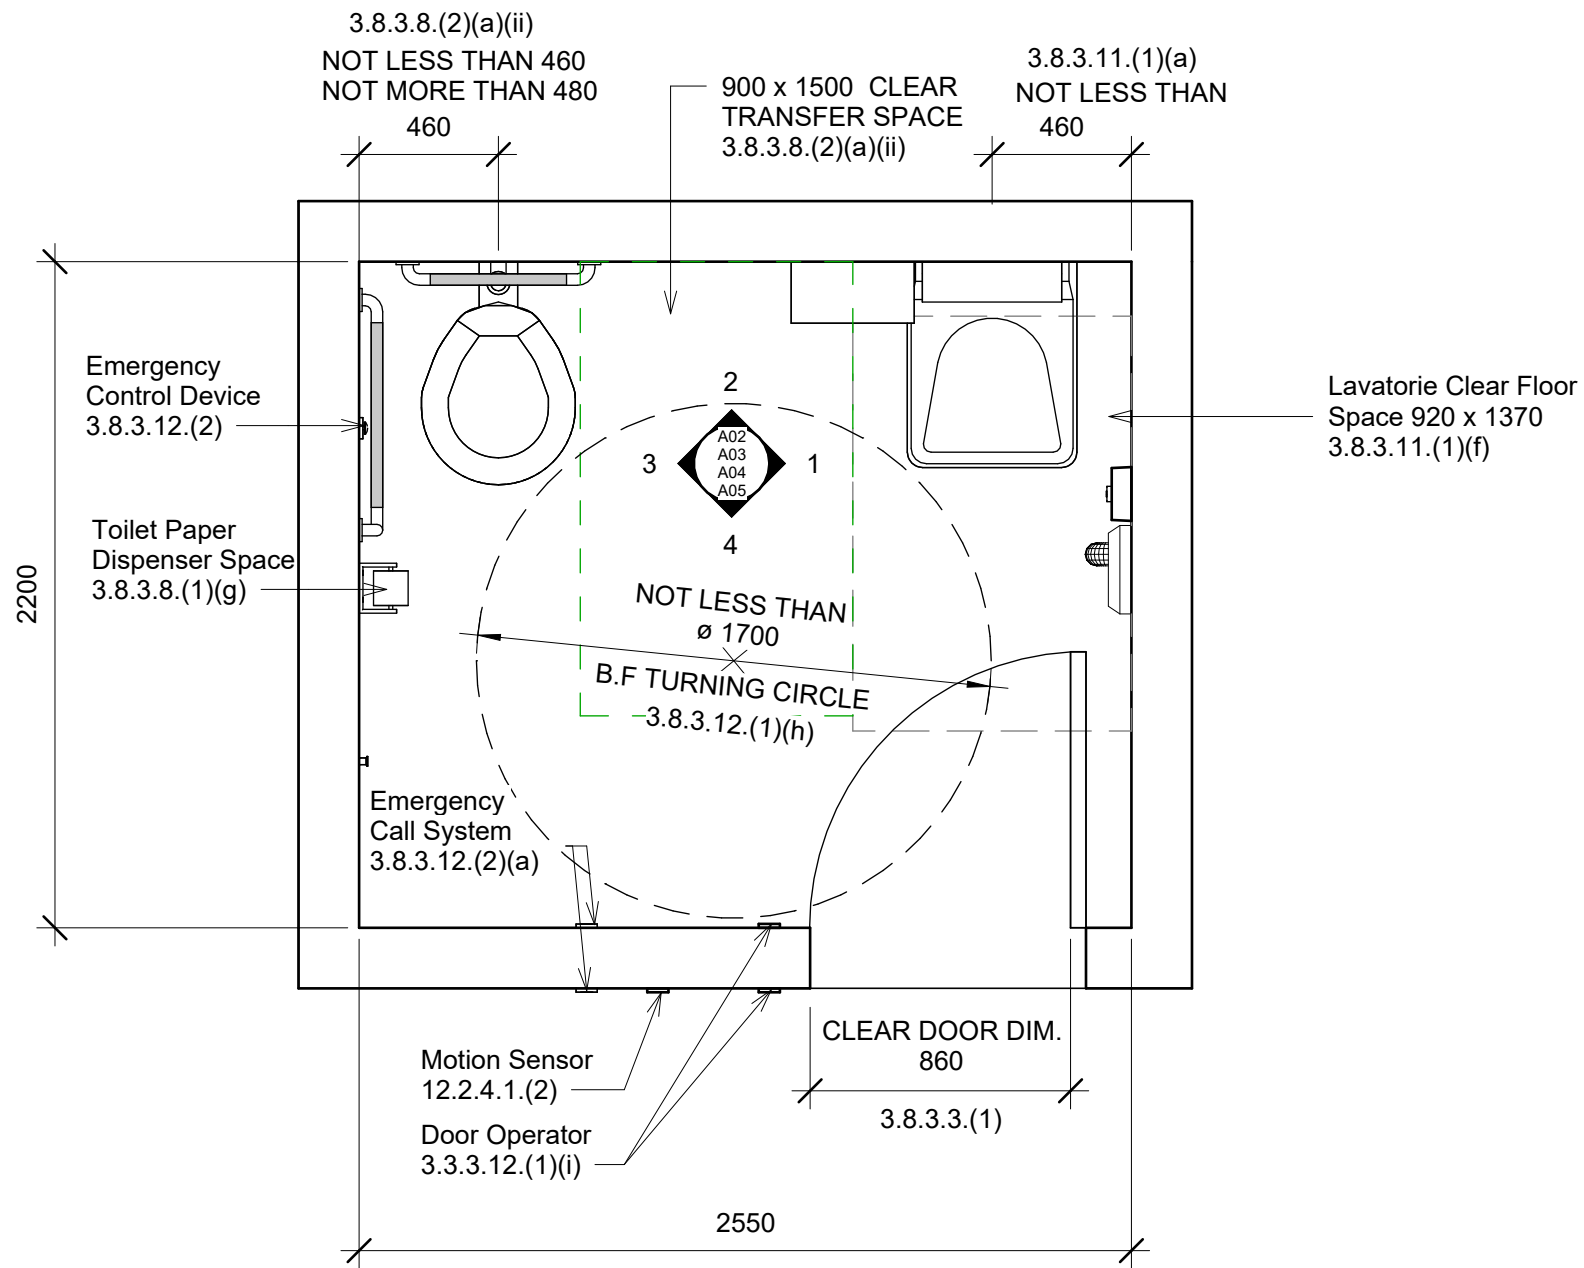

A U.T.R Washroom Plan
1 : 25




School of Building Technology
**ARCHITECTURAL
TECHNOLOGY**

Project Title
Barrier Free Design (U.T.R.)

Drawing Title
U.T.R. Washroom Plan

Course Code		ARCH-1034-(01)-24W	
Date		11 April 2024	Drawing A01
Drawn by		AFNM	
Checked by		HG	Scale 1 : 25

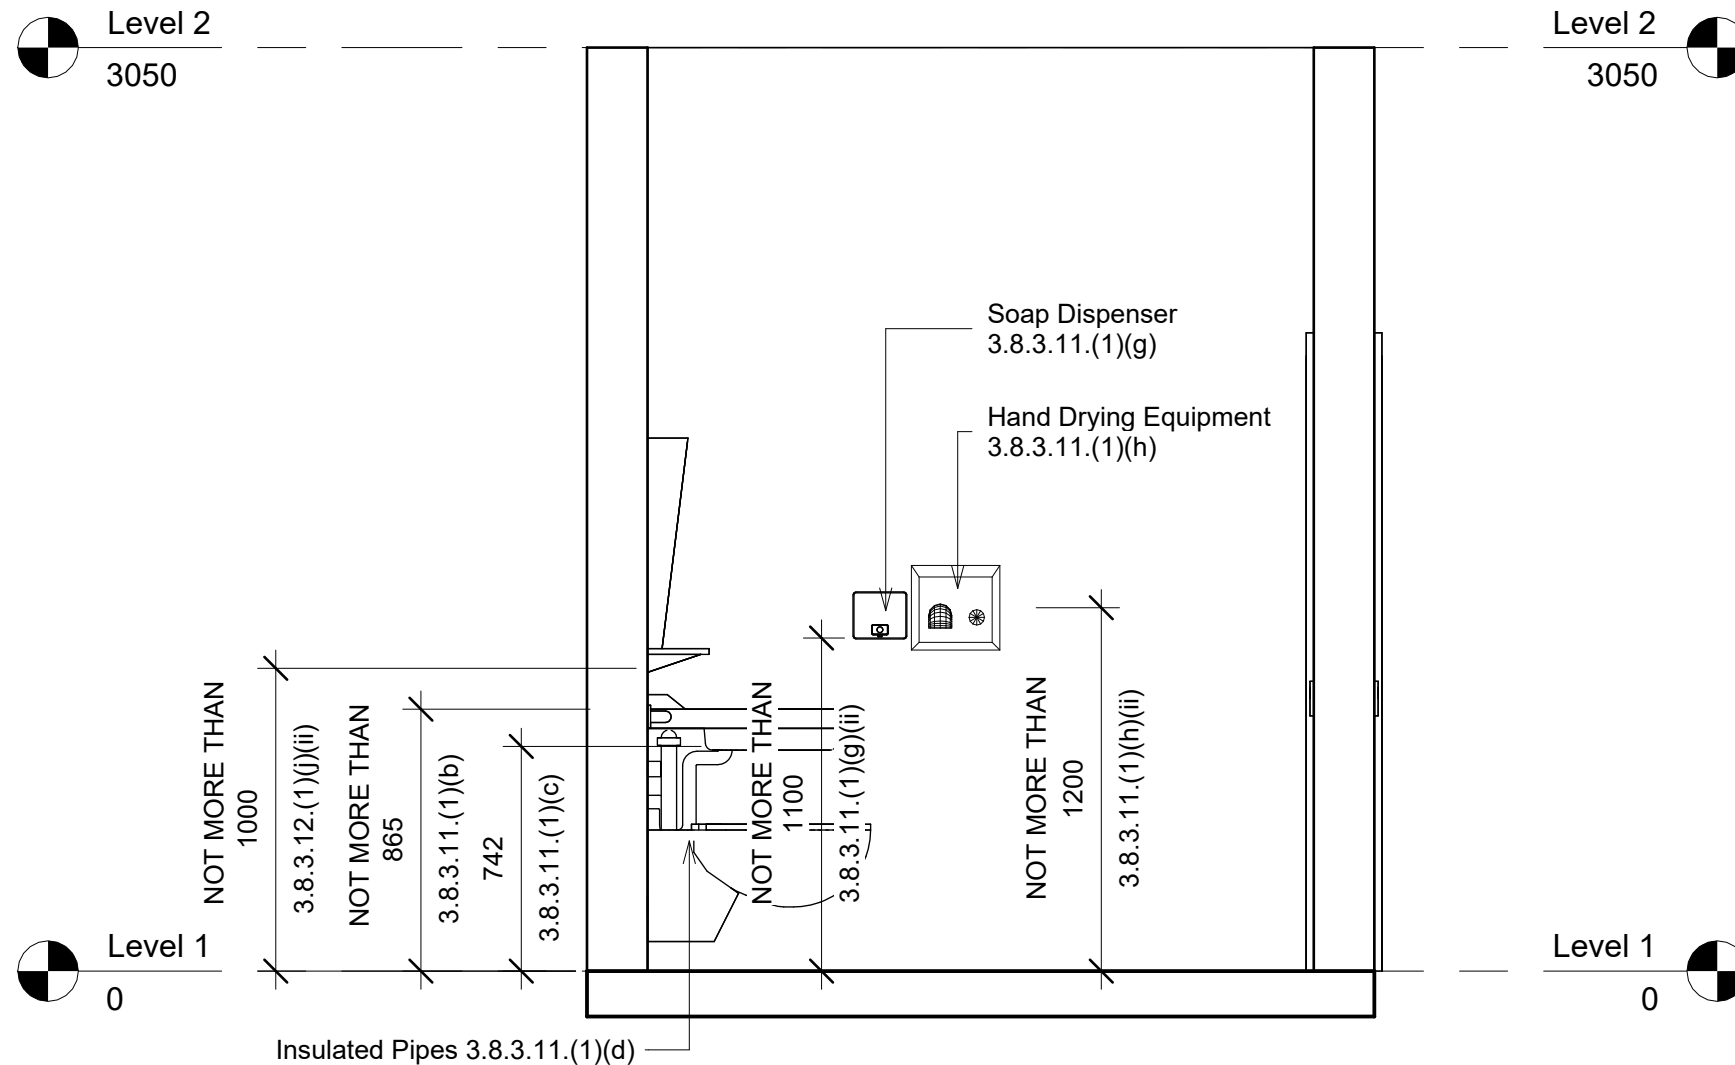

1 East Elevation
1 : 25



School of Building Technology
ARCHITECTURAL
TECHNOLOGY

Project Title

Barrier Free Design (U.T.R.)

Drawing Title

East Elevation

Course Code

ARCH-1034-(01)-24W

Date

11 April 2024

Drawn by

AFNM


Checked by

HG

Drawing

A02

Scale 1 : 25

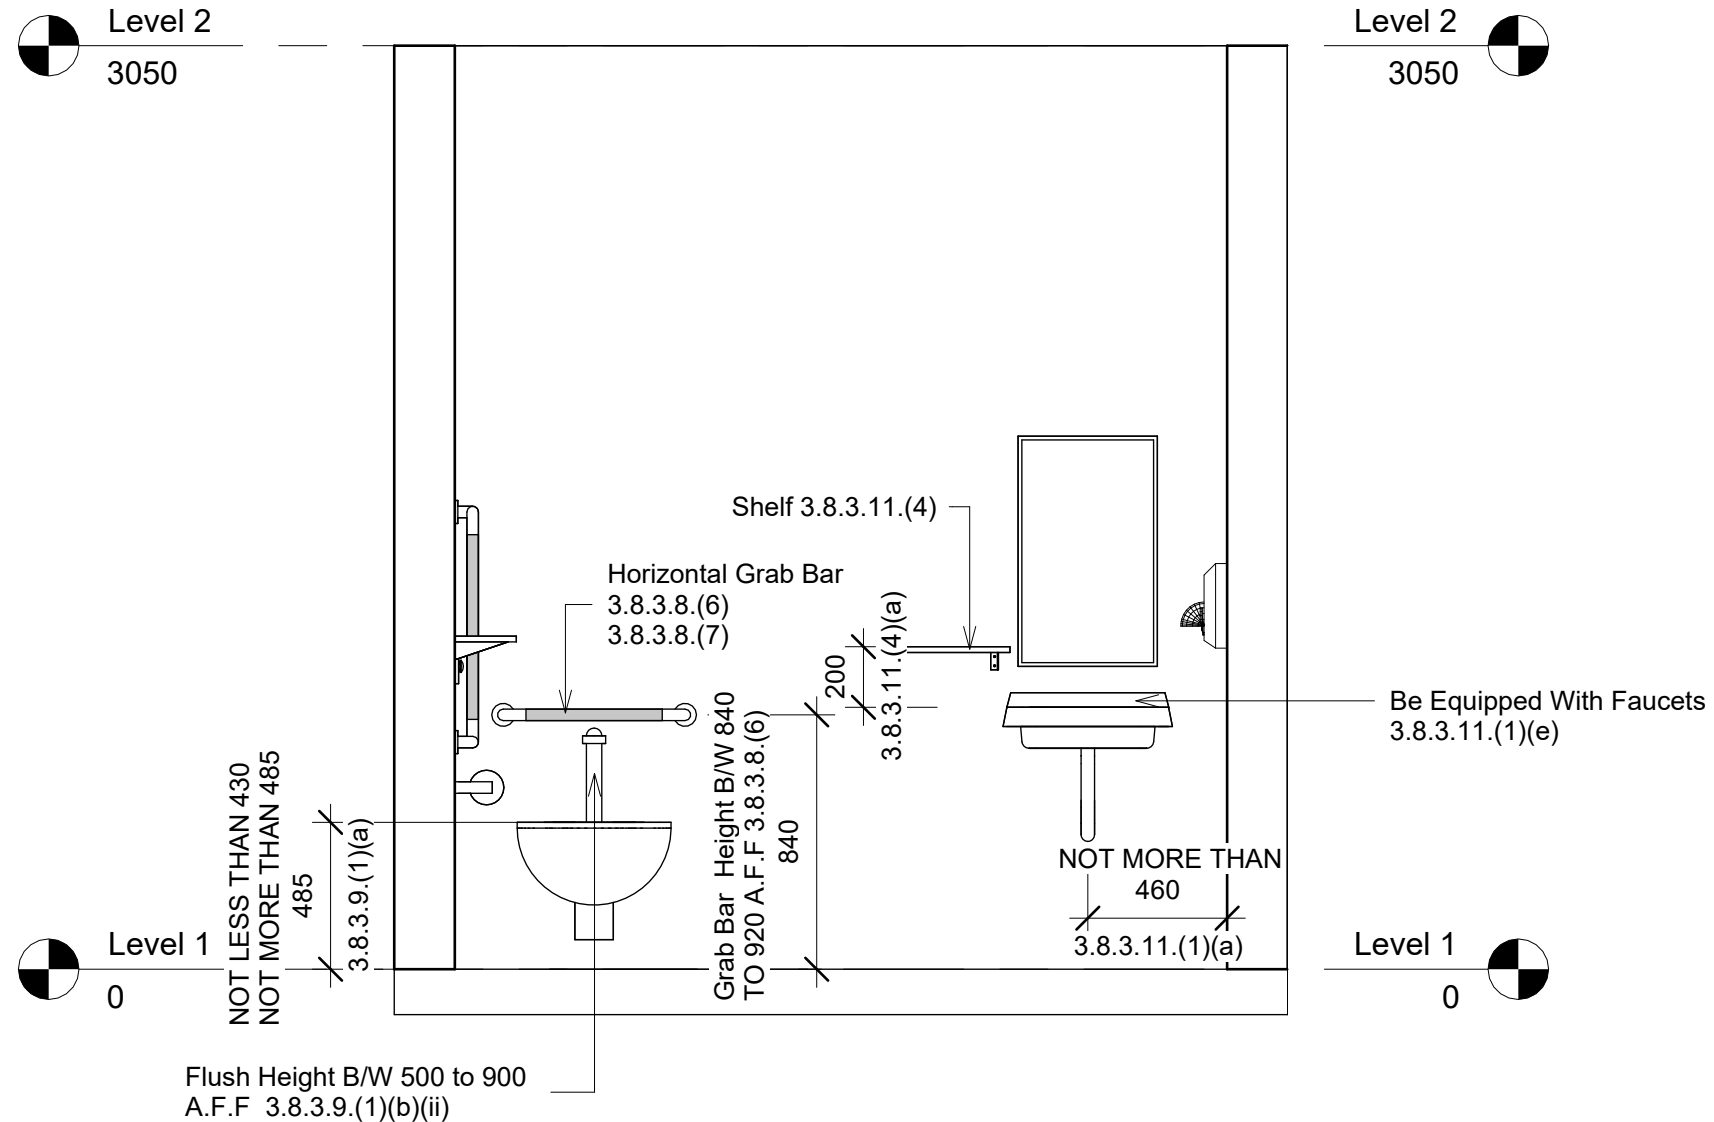

2 North Elevation
1 : 25



School of Building Technology
ARCHITECTURAL
TECHNOLOGY

Project Title

Barrier Free Design (U.T.R.)

Drawing Title

North Elevation

Course Code

ARCH-1034-(01)-24W

Date

11 April 2024

Drawn by

AFNM


Checked by

HG

Drawing

A03

Scale 1 : 25

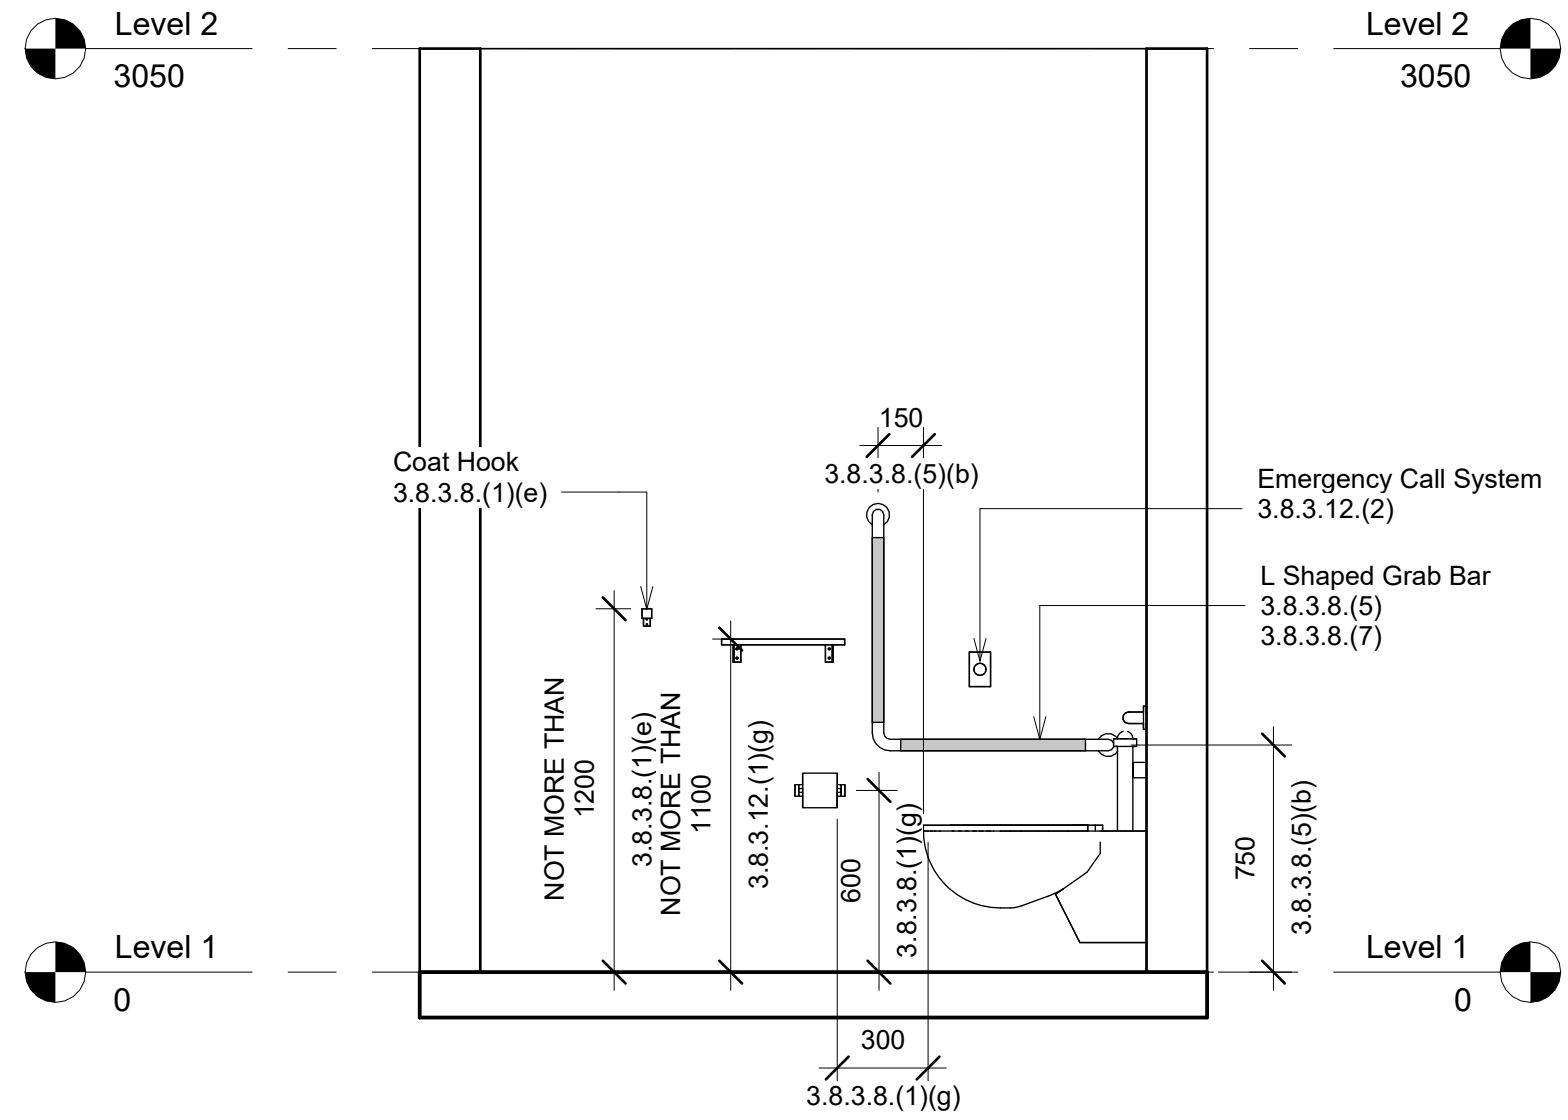

3 West Elevation
1 : 25



School of Building Technology
ARCHITECTURAL
TECHNOLOGY

Project Title
Barrier Free Design (U.T.R.)
Drawing Title
West Elevation

Course Code	ARCH-1034-(01)-24W	
Date	11 April 2024	Drawing A04
Drawn by	AFNM	
Checked by	HG	Scale 1 : 25

Level 2
3050

Level 2
3050


Door C/W graspable latch-operating
mechanism 3.8.3.12.(1)(b)

Door C/W Power Door Operator
3.8.3.12.(1)(i)

Latch Height B/W 900 TO 1000 A.F.F
3.8.3.12.(1)(b)(ii)(B)

Level 1
0

Level 1
0

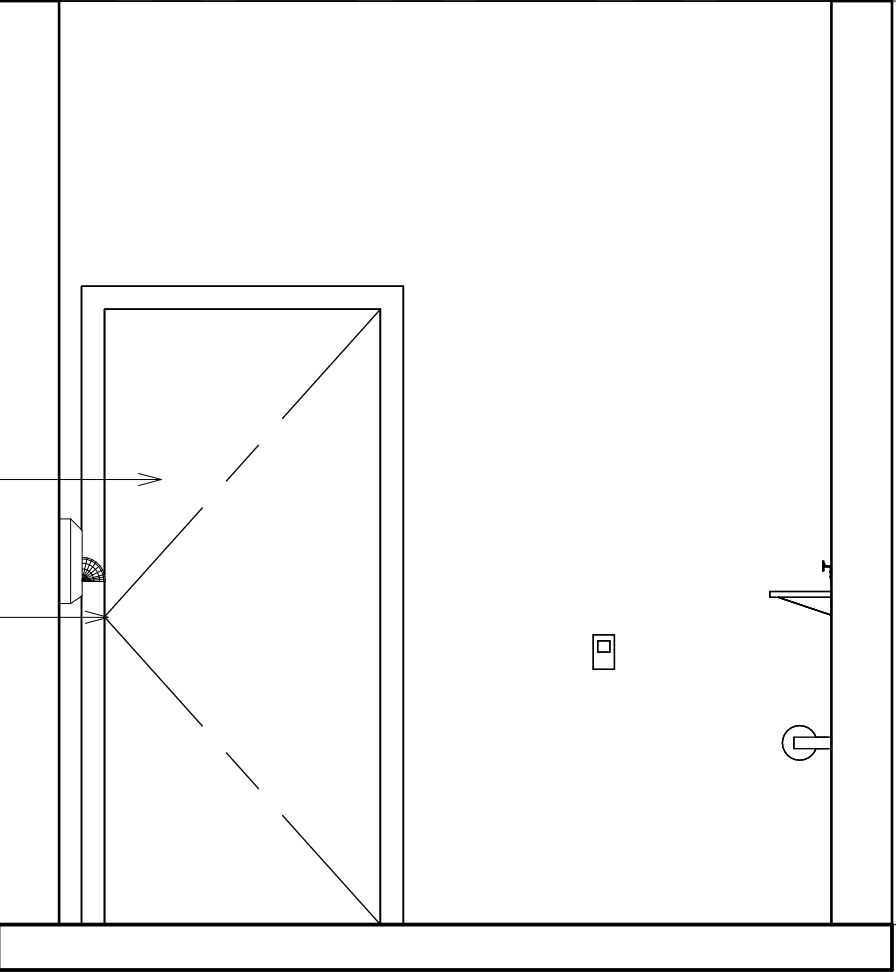

4 South Elevation
1 : 25



School of Building Technology
ARCHITECTURAL
TECHNOLOGY

Project Title
Barrier Free Design (U.T.R.)
Drawing Title
South Elevation

Course Code	ARCH-1034-(01)-24W	
Date	11 April 2024	Drawing A05 Scale 1 : 25
Drawn by	AFNM	
Checked by	HG	