




OXFORD WELLNESS CENTRE

1080 OXFORD ST. London, ON

Sheet List		
Sheet Name	Sheet Number	Drawn By
SITE PLAN, ROOF PLAN & ZONING	A-300	AFNM
FLOOR PLAN	A-301	AFNM
ELEVATIONS	A-302	AFNM
ELEVATIONS & BUILDING SECTION	A-303	AFNM
WALL SECTIONS & DETAILS	A-304	AFNM

ZONE: RSC3	ALLOWABLE	PROVIDED
LOT AREA (MIN):	3123.52 m ²	3123.52 m ²
LOT FRONTAGE (MIN):	45 m	70.5 m
LOT DEPTH (MIN):	60 m	46.9 m
LANDSCAPED AREA (MIN):	468,528 m ² 15 %	1327.6 m ² 42.5 %
LOT COVERAGE (MAX):	937,056 m ² 30 %	631.5 m ² 20.2 %
BUILDING HEIGHT (MAX):	12.00 m	4.68 m
GROSS FLOOR AREA (GFA):	6000 m ²	424.15 m ²
GFA FOR OFFICE USE (MAX):	2000 m ² 33.3333 %	17.41 4.1 %
PARKING REQUIREMENT:	5 Spaces	12 Spaces

SITE LEGEND	
Main Entrance	▲
Light Post	⊙
Secondry Entry / Exit	▷
Barrier Free	♿
Coniferous Tree	⊗
Shrub	⊗
Stop Sign	⊞
Traffic Direction Arrows	↩ ↪
Trash Can	⊙
Bench	▬
Crosswalk	▬▬▬▬
Fire Route	F.R

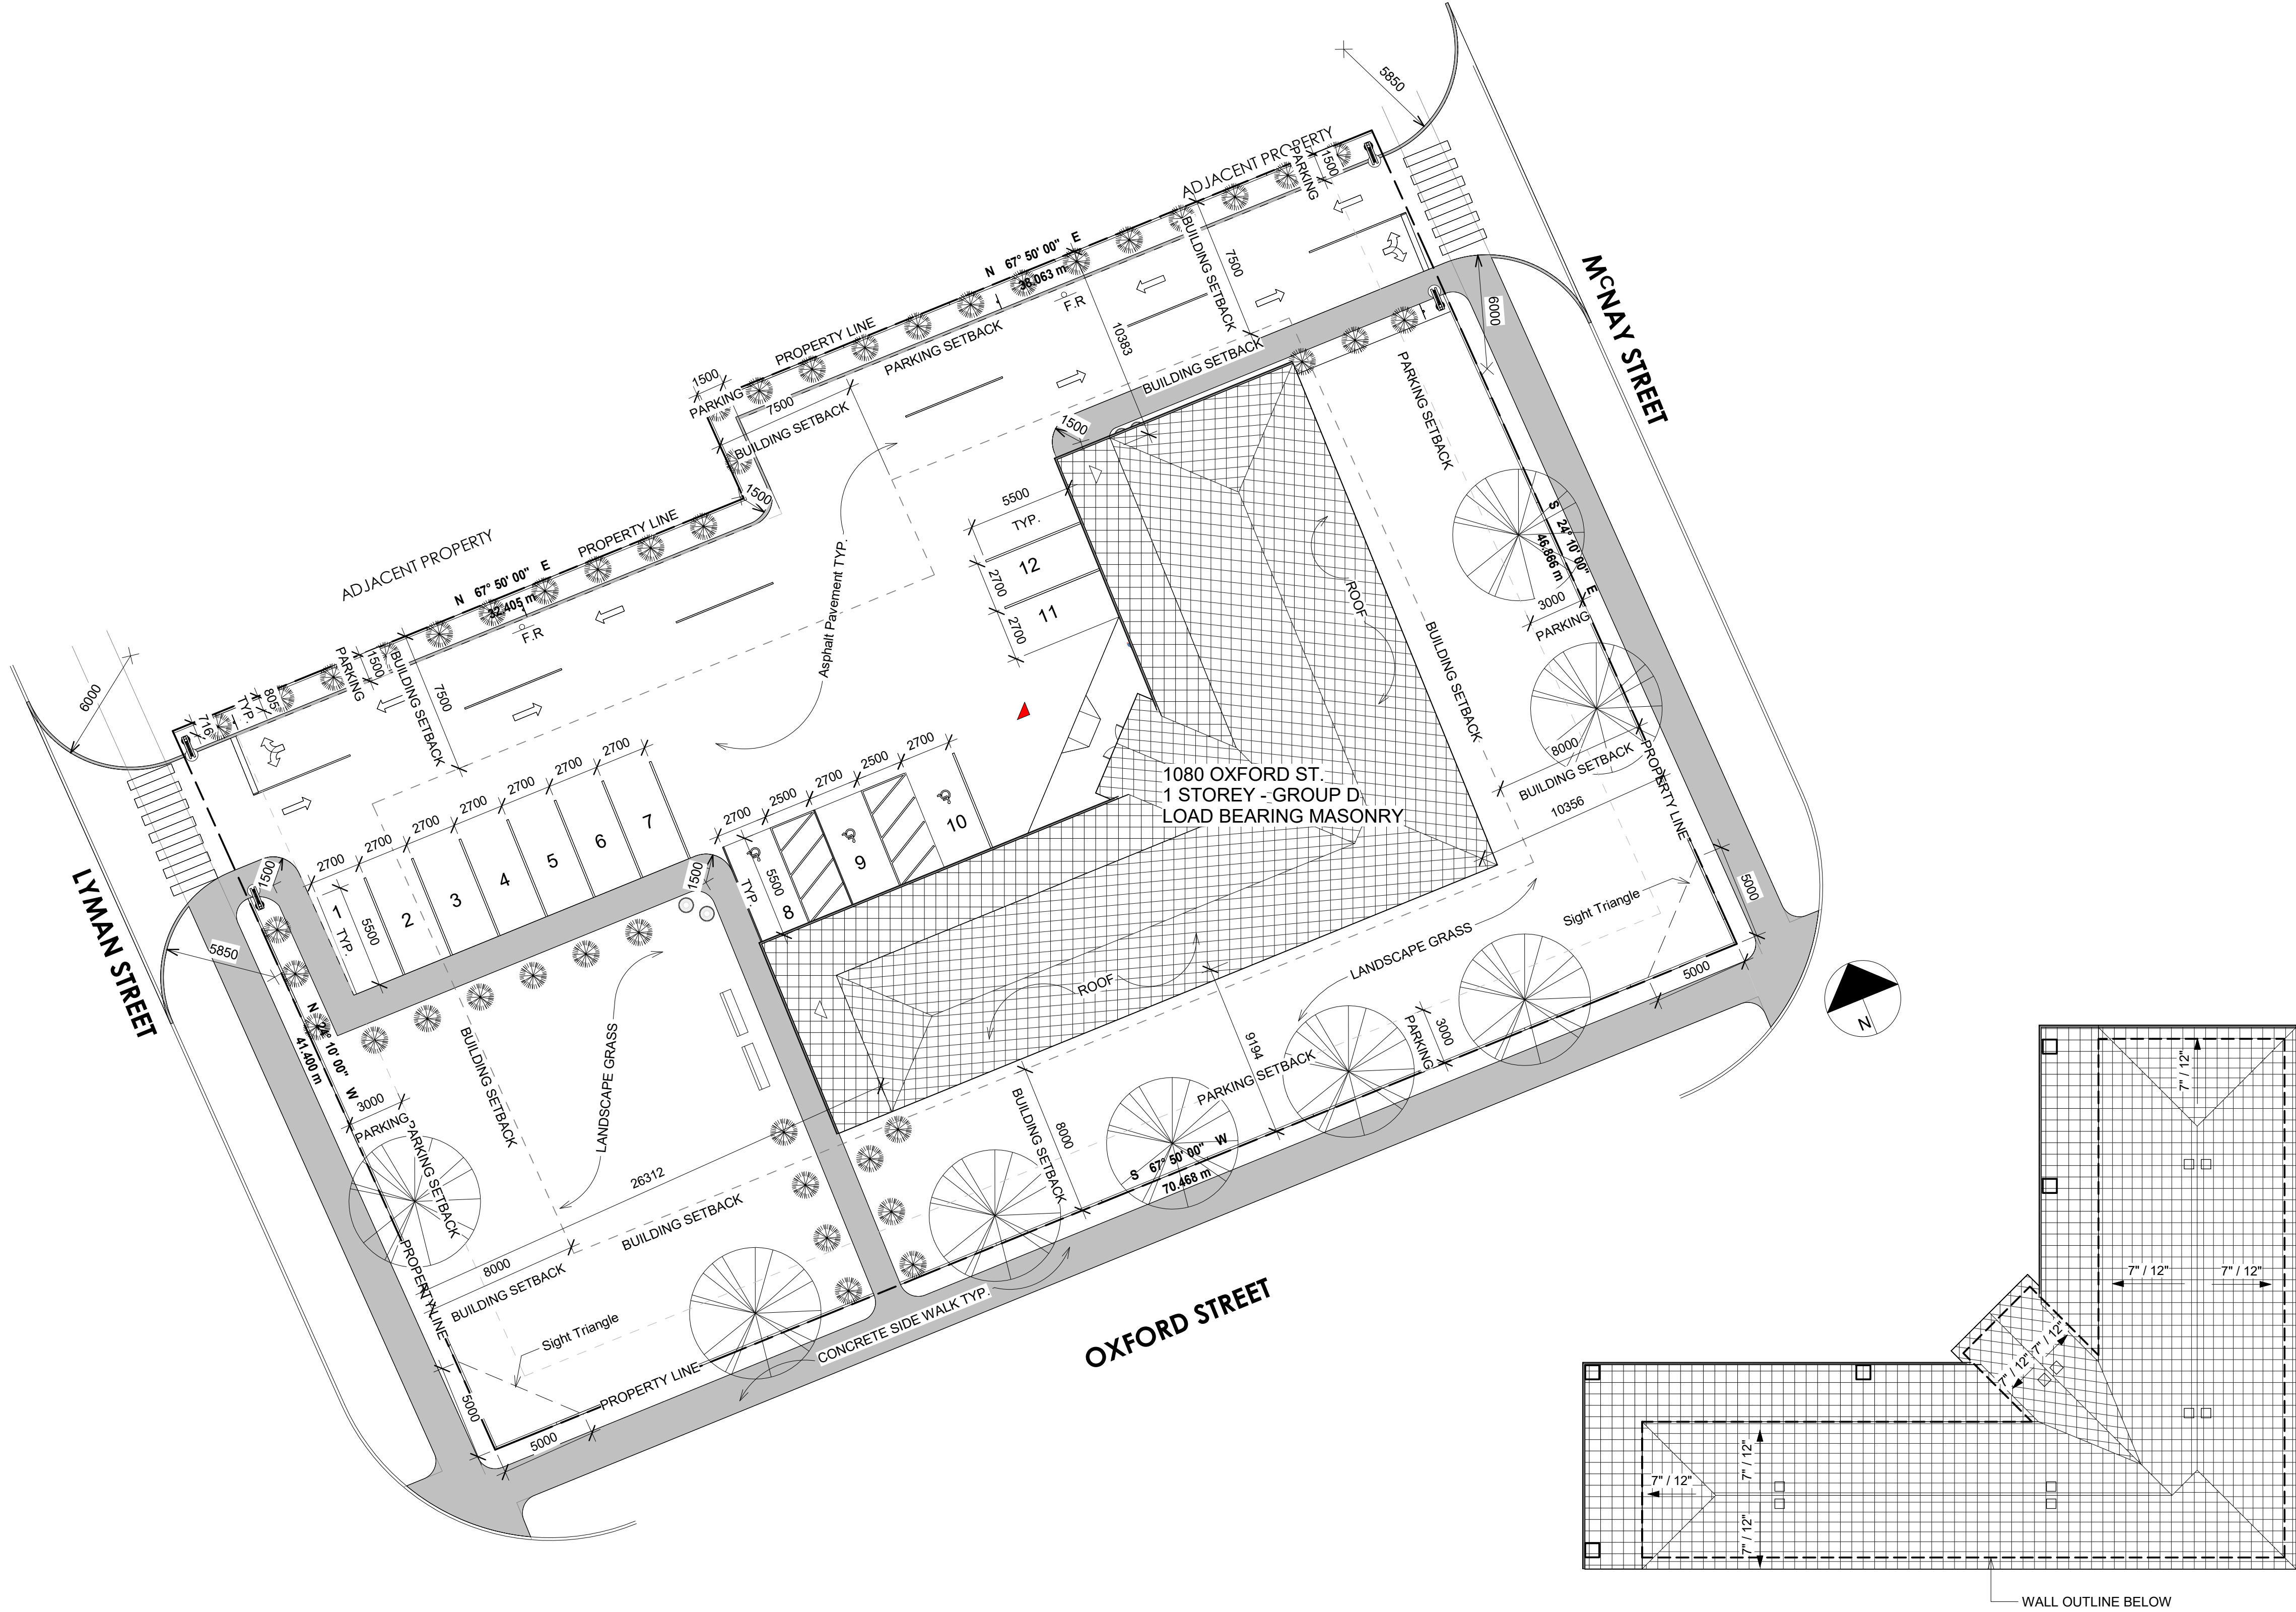

1 SITE PLAN
1 : 200

2 ROOF PLAN
1 : 200

NORTH ARROW

PRELIMINARY
NOT FOR CONSTRUCTION

PROJECT TITLE
OXFORD WELLNESS
CENTRE
CLIENT:
FANSHAWE COLLEGE
PROJECT ADDRESS
LONDON, ON

DRAWING TITLE
SITE PLAN, ROOF PLAN & ZONING

CHECKED | DRAWN | DATE
JF | AFNM | 03/14/24

W24-001 | A-300
PROJECT No. | DRAWING

NORTH ARROW

PRELIMINARY
NOT FOR CONSTRUCTION

PROJECT TITLE
**OXFORD WELLNESS
CENTRE**
CLIENT:
FANSHAWE COLLEGE
PROJECT ADDRESS
LONDON, ON








DRAWING TITLE
FLOOR PLAN

CHECKED JF | DRAWN AFNM | DATE 03/14/24

W24-001
PROJECT No.


A-301
DRAWING

LEGENDS

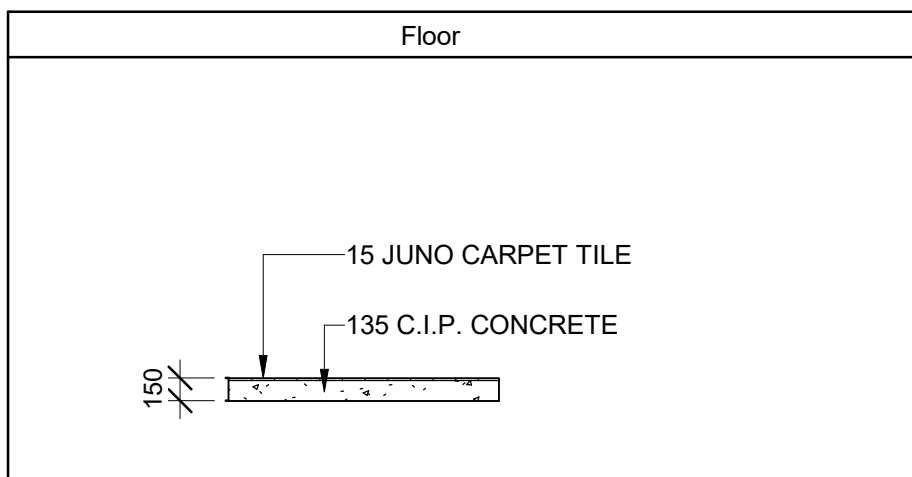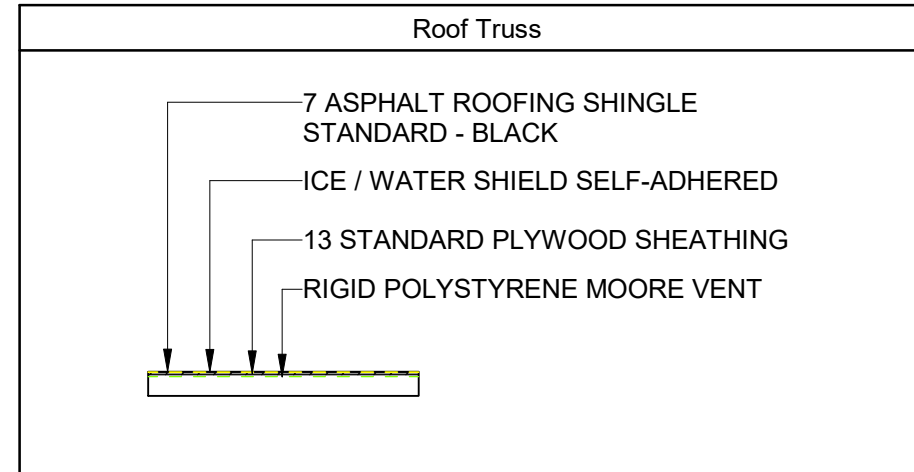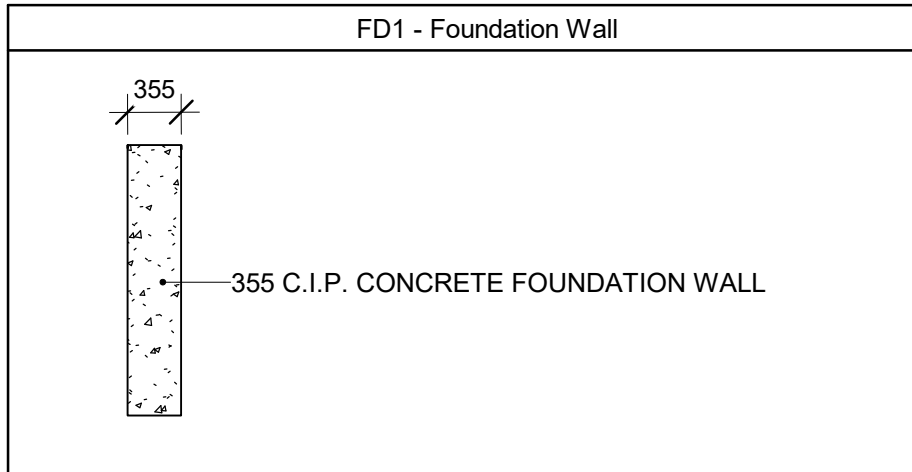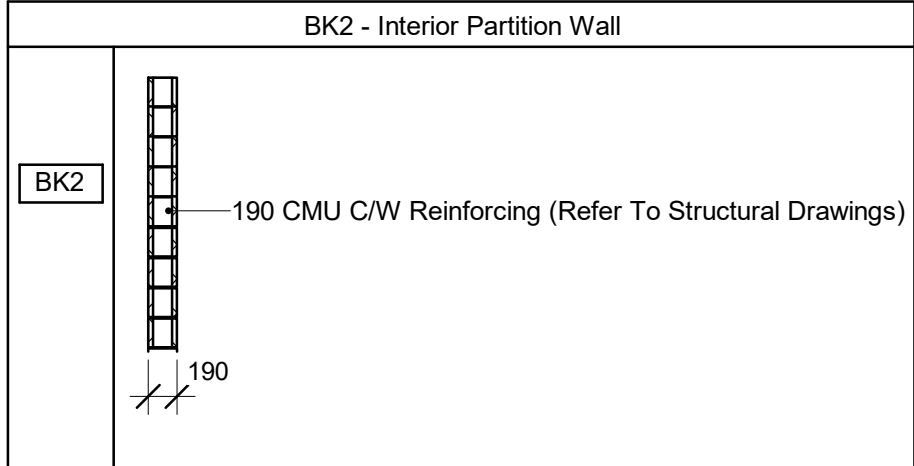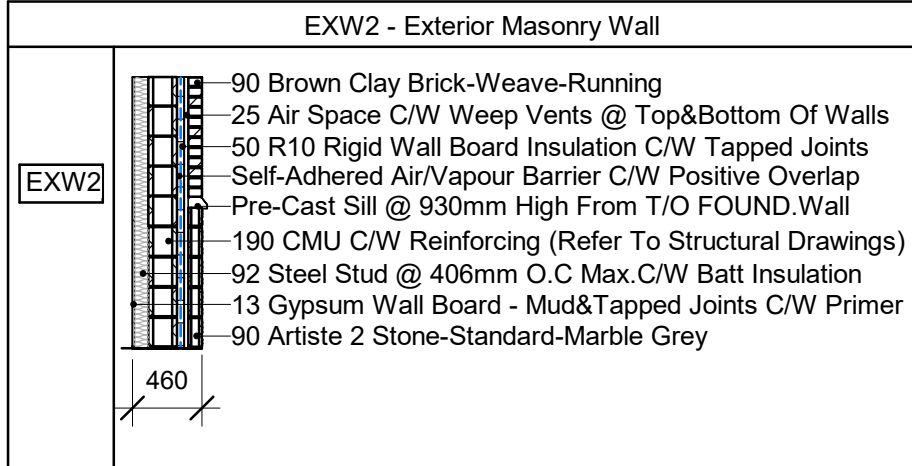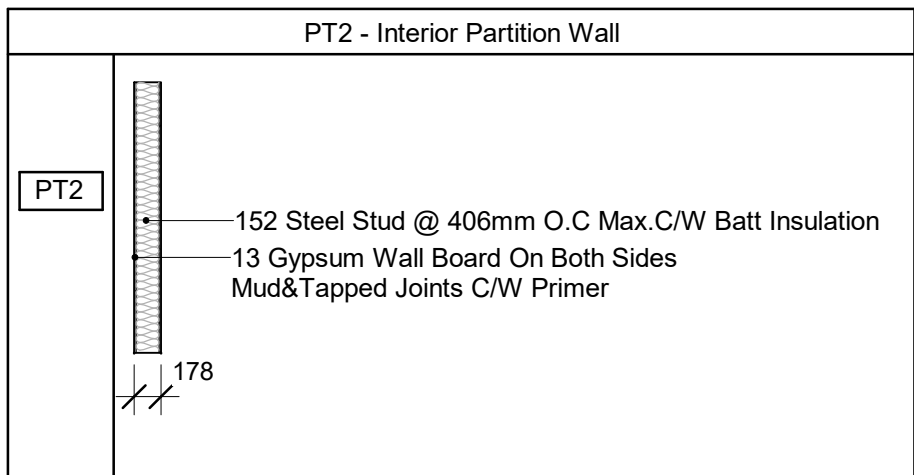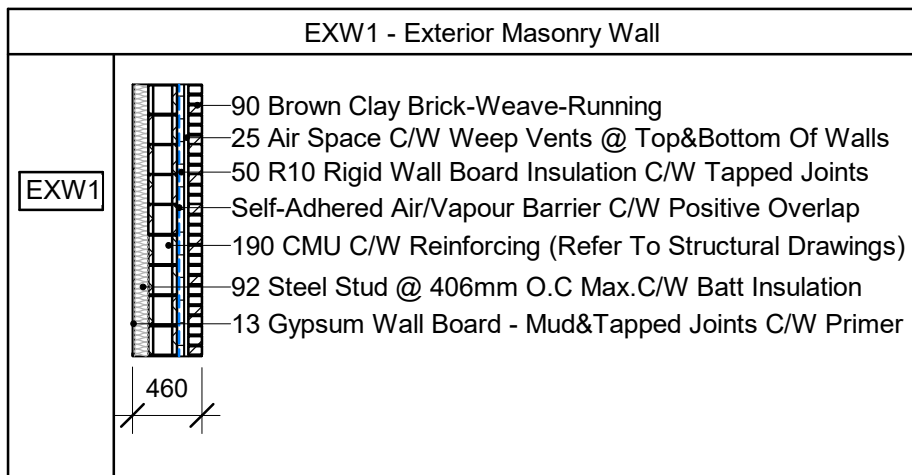

Door Schedule				
Type Mark	Count	Height	Width	Family and Type
D1	2	2438	1829	Door-Exterior-Double-Full Glass-Wood_Clad: 1829 x 2438
D2	3	2184	1219	Door-Exterior-Single-Two_Lite: 1219 x 2184
D3	11	2184	1067	Door-Passage-Single-Vision_Lite: sample
D4	1	2134	915	M_Single-Flush: 0915 x 2134mm
D5	3	2438	1219	Door-Passage-Single-Flush: 1219 x 2438

Window Schedule					
Type Mark	Count	Height	Width	Sill Height	Family and Type
W1	10	1200	1050	1150	M_Window-Casement-Double: 1050 x 1250mm
W2	2	1524	762	600	Window-Fixed-Oval: 1
W2	2	1524	762	914	Window-Fixed-Oval: 1
W3	6	1200	914	1150	001_CHINA_WINDOW: 1
W5	1	914	914	2695	Window-Fixed-Round: 1

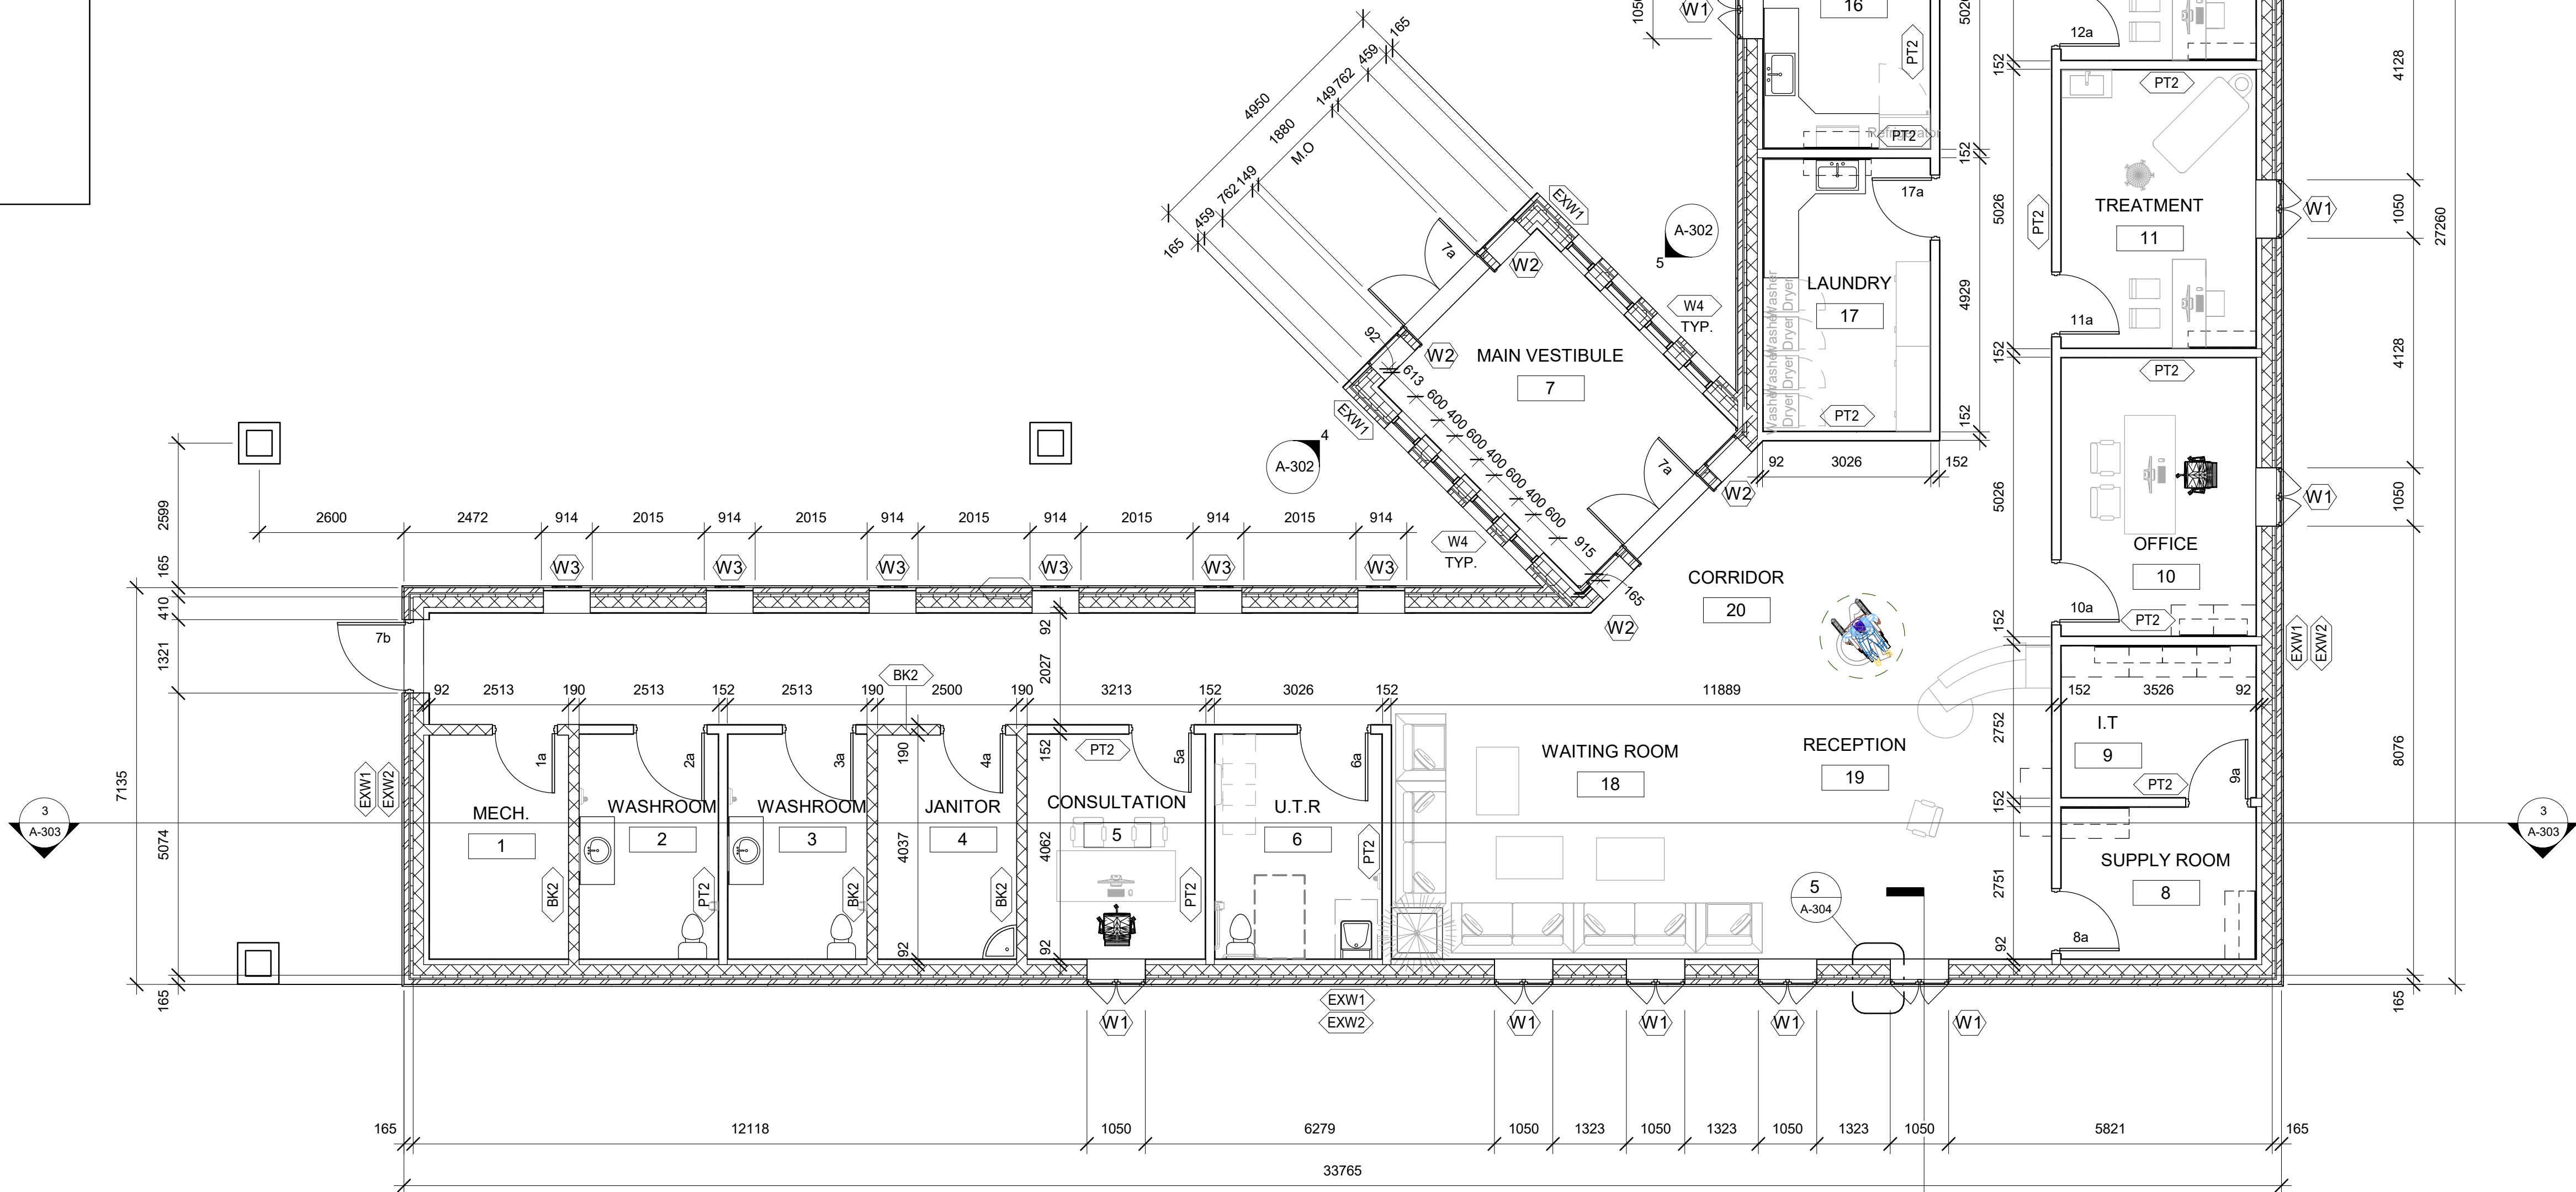

1
A-302 A-301
FLOOR PLAN
1 : 75

1
A-302
A-301


2
A-304

3
A-303

A-302
2

A-303
2


A-303
1

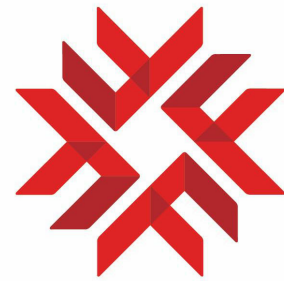


FANSHAWE

DONALD J. SMITH
SCHOOL OF BUILDING
TECHNOLOGY


NORTH ARROW

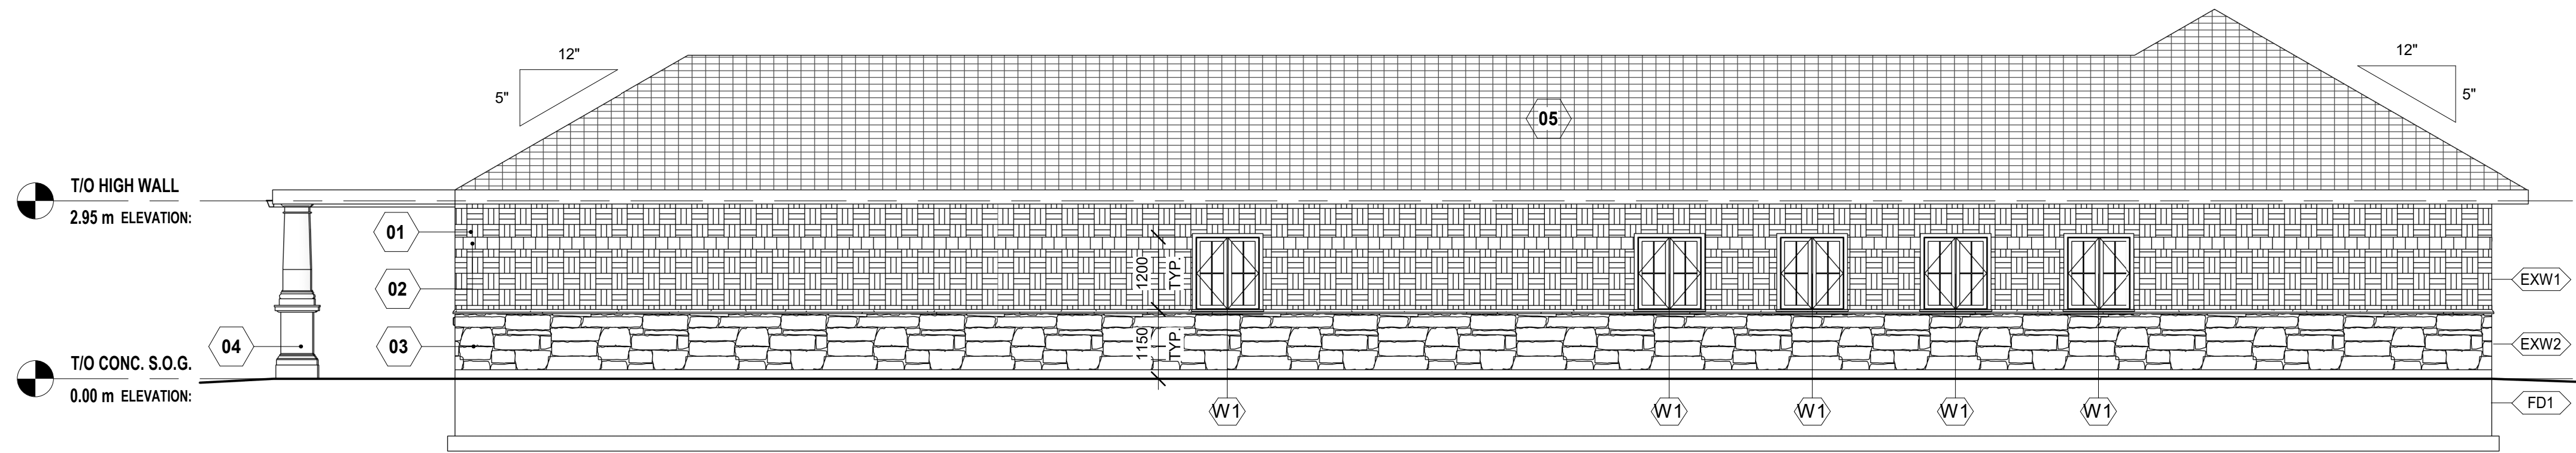


1 SOUTH
1 : 75

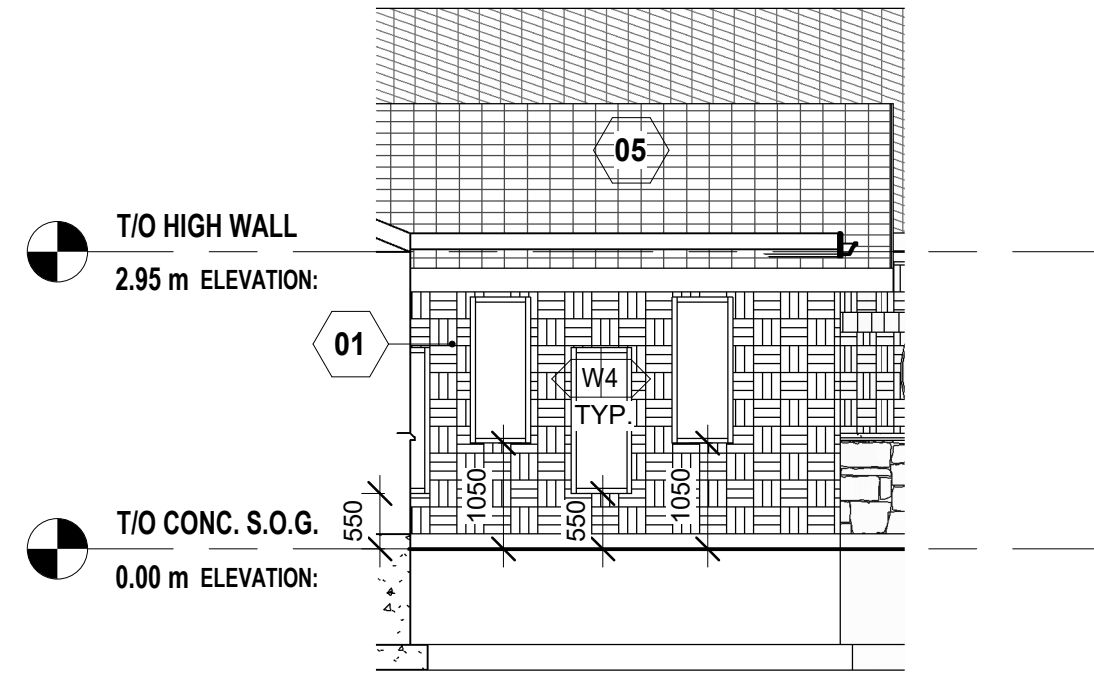


5 PARTIAL NORTH
1 : 75

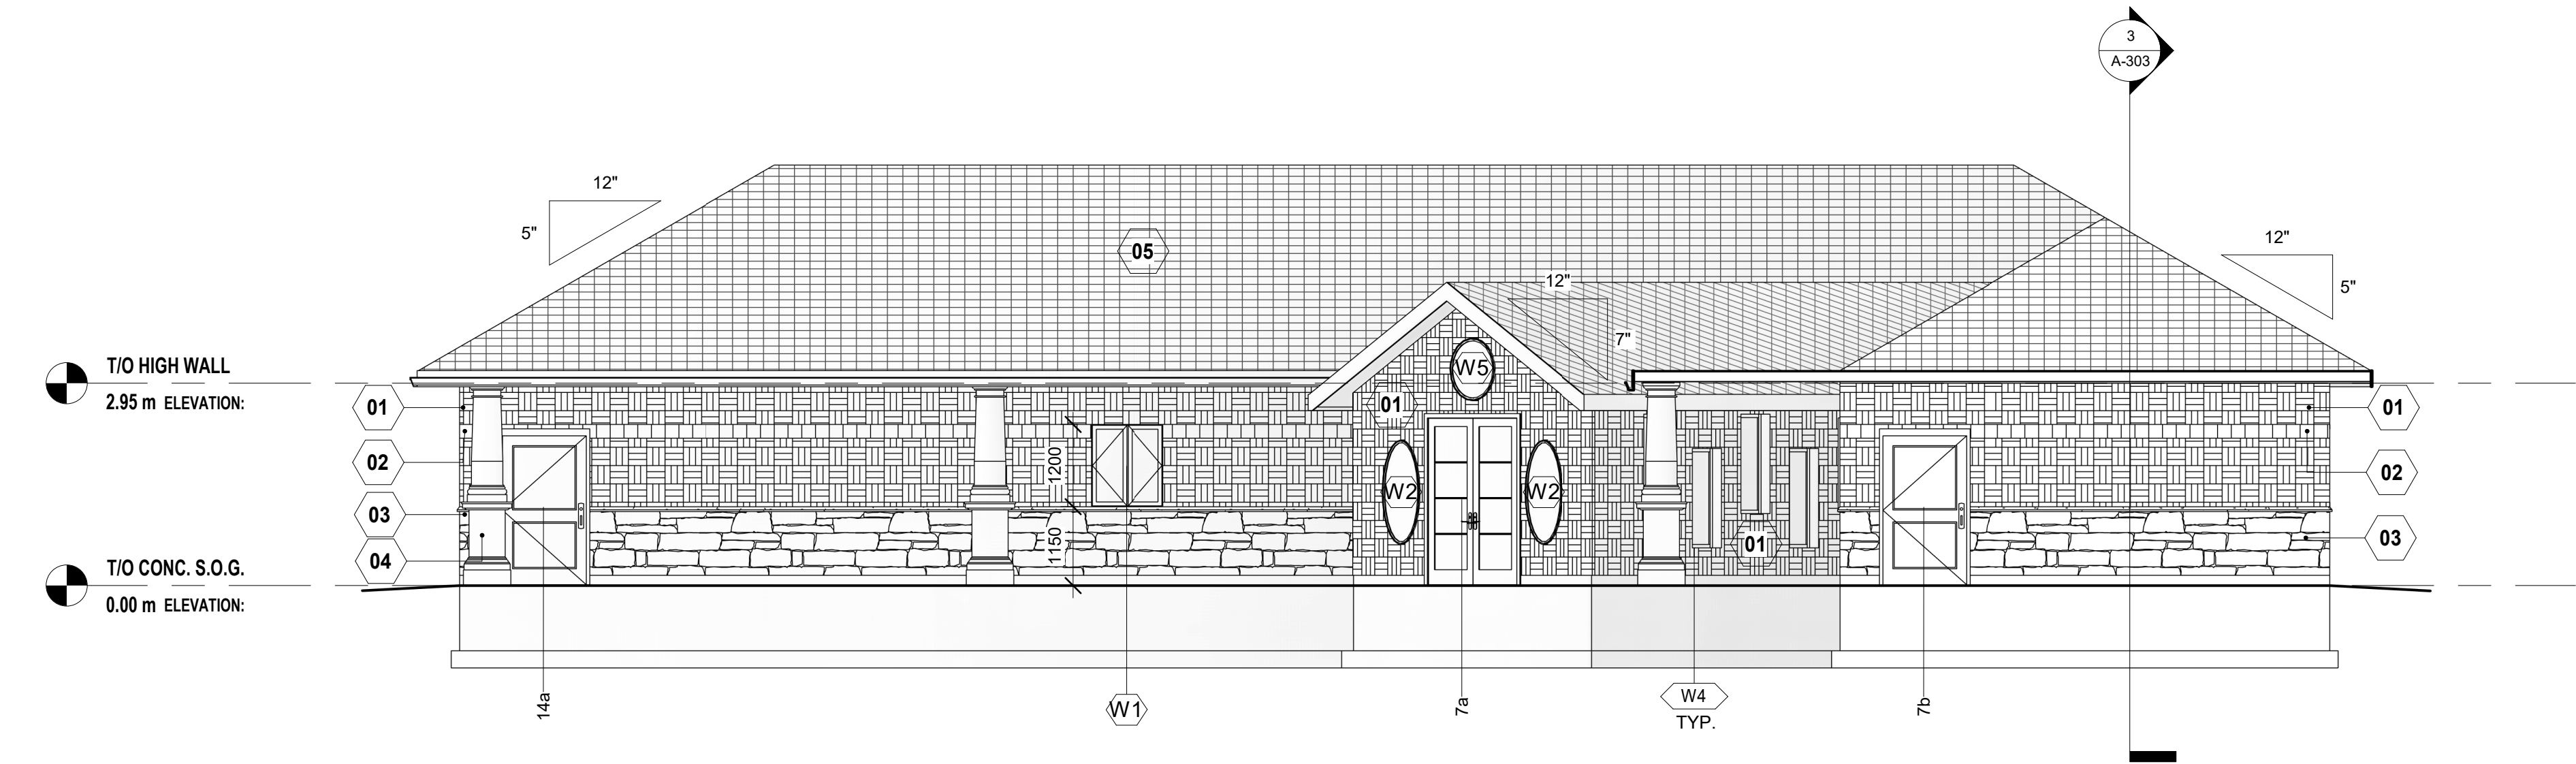

2 WEST
1 : 75

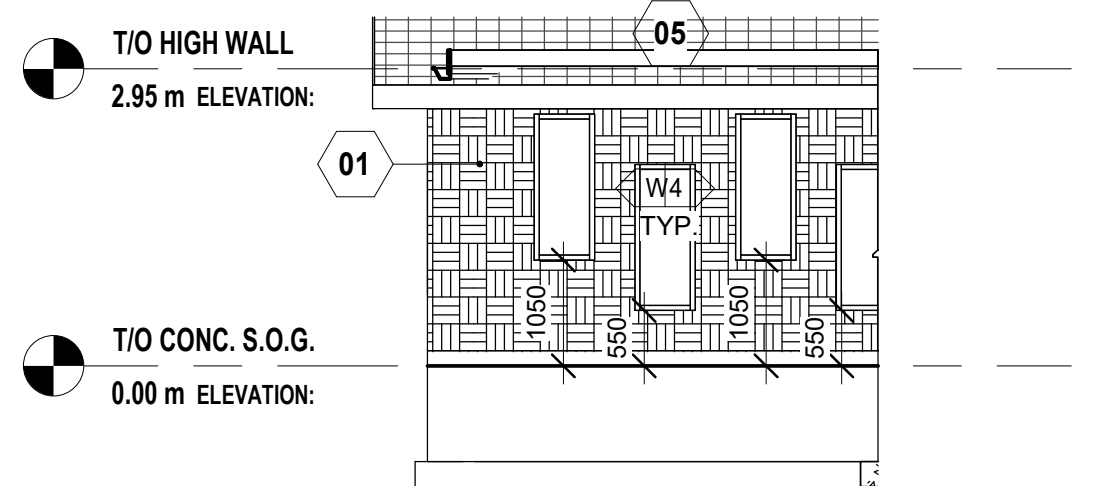

4 PARTIAL WEST
1 : 75

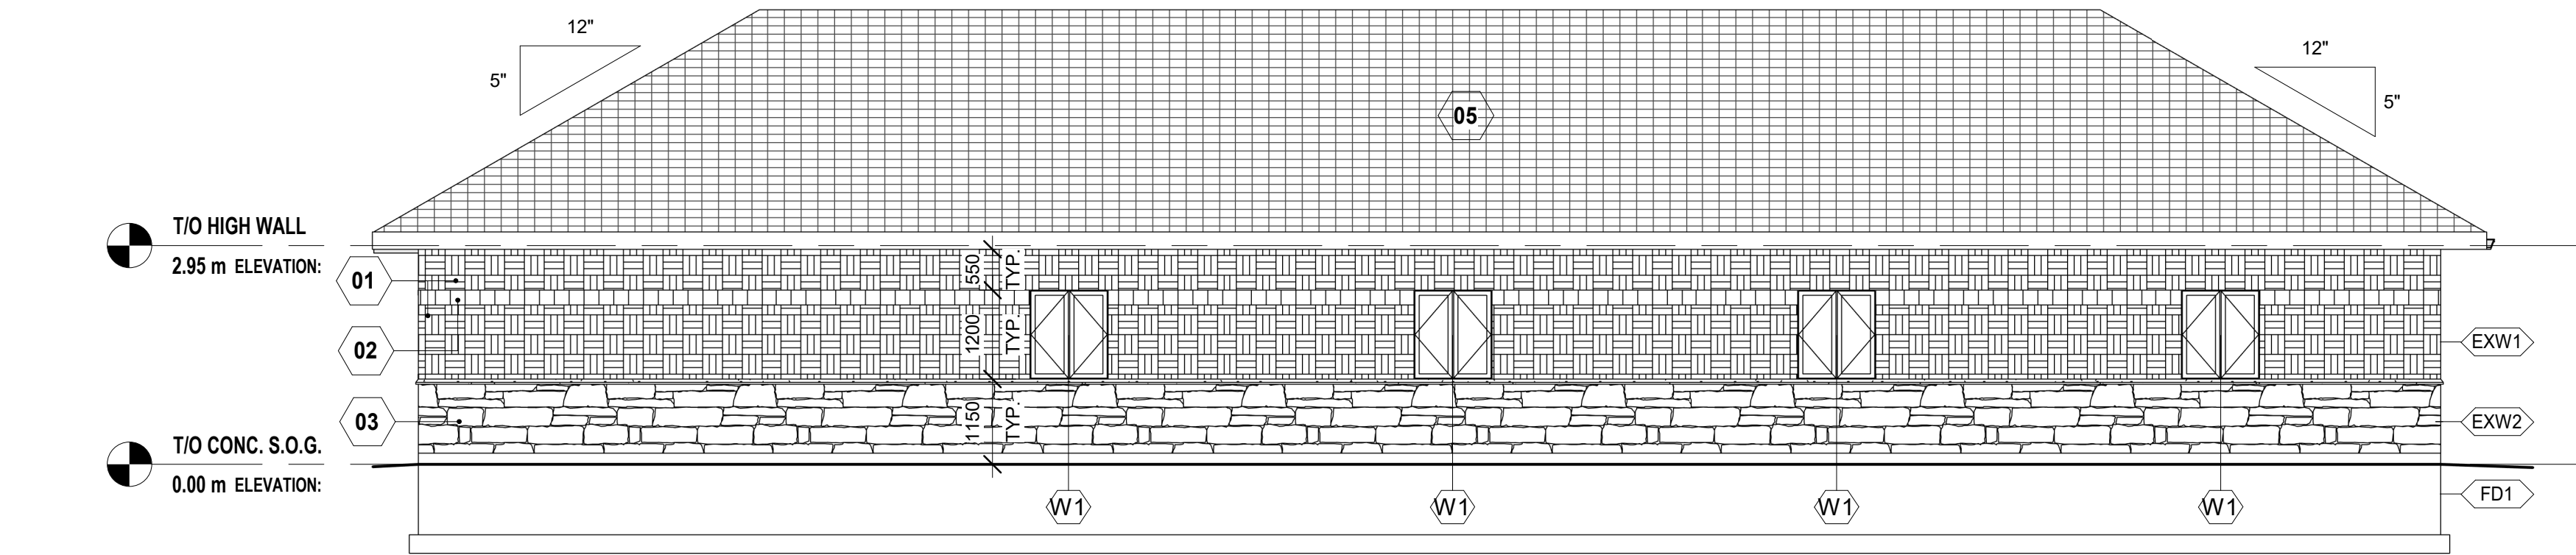

3 EAST
1 : 75

LEGENDS

- 01 90 Brown Clay Brick-Basket Weave
- 02 90 Light Grey CMU Vertical Stack Bond
- 03 90 Artiste 2 Stone-Standard-Marble Grey
- 04 Doric Column TYP.
- 05 Roof TYP.

Door Schedule

Type Mark	Count	Height	Width	Family and Type
D1	2	2438	1829	Door-Exterior-Double-Full Glass-Wood_Clad: 1829 x 2438
D2	3	2184	1219	Door-Exterior-Single-Two_Lite: 1219 x 2184
D3	11	2184	1067	Door-Passage-Single-Vision_Lite: sample
D4	1	2134	915	M_Single-Flush: 0915 x 2134mm
D5	3	2438	1219	Door-Passage-Single-Flush: 1219 x 2438

Window Schedule

Type Mark	Count	Height	Width	Sill Height	Family and Type
W1	10	1200	1050	1150	M_Window-Casement-Double: 1050 x 1250mm
W2	2	1524	762	600	Window-Fixed-Oval: 1
W2	2	1524	762	914	Window-Fixed-Oval: 1
W3	6	1200	914	1150	001_CHINA_WINDOW: 1
W5	1	914	914	2695	Window-Fixed-Round: 1

PROJECT TITLE
OXFORD WELLNESS
CENTRE

CLIENT:
FANSHAWE COLLEGE

PROJECT ADDRESS
LONDON, ON

DRAWING TITLE
ELEVATIONS

CHECKED JF DRAWN AFNM DATE 03/14/24


W24-001

PROJECT No.

A-302

DRAWING



PRELIMINARY
NOT FOR CONSTRUCTION

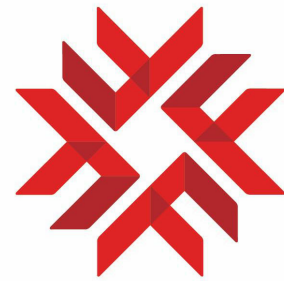


FANSHAWE
DONALD J. SMITH
SCHOOL OF BUILDING
TECHNOLOGY

NORTH ARROW

PRELIMINARY
NOT FOR CONSTRUCTION

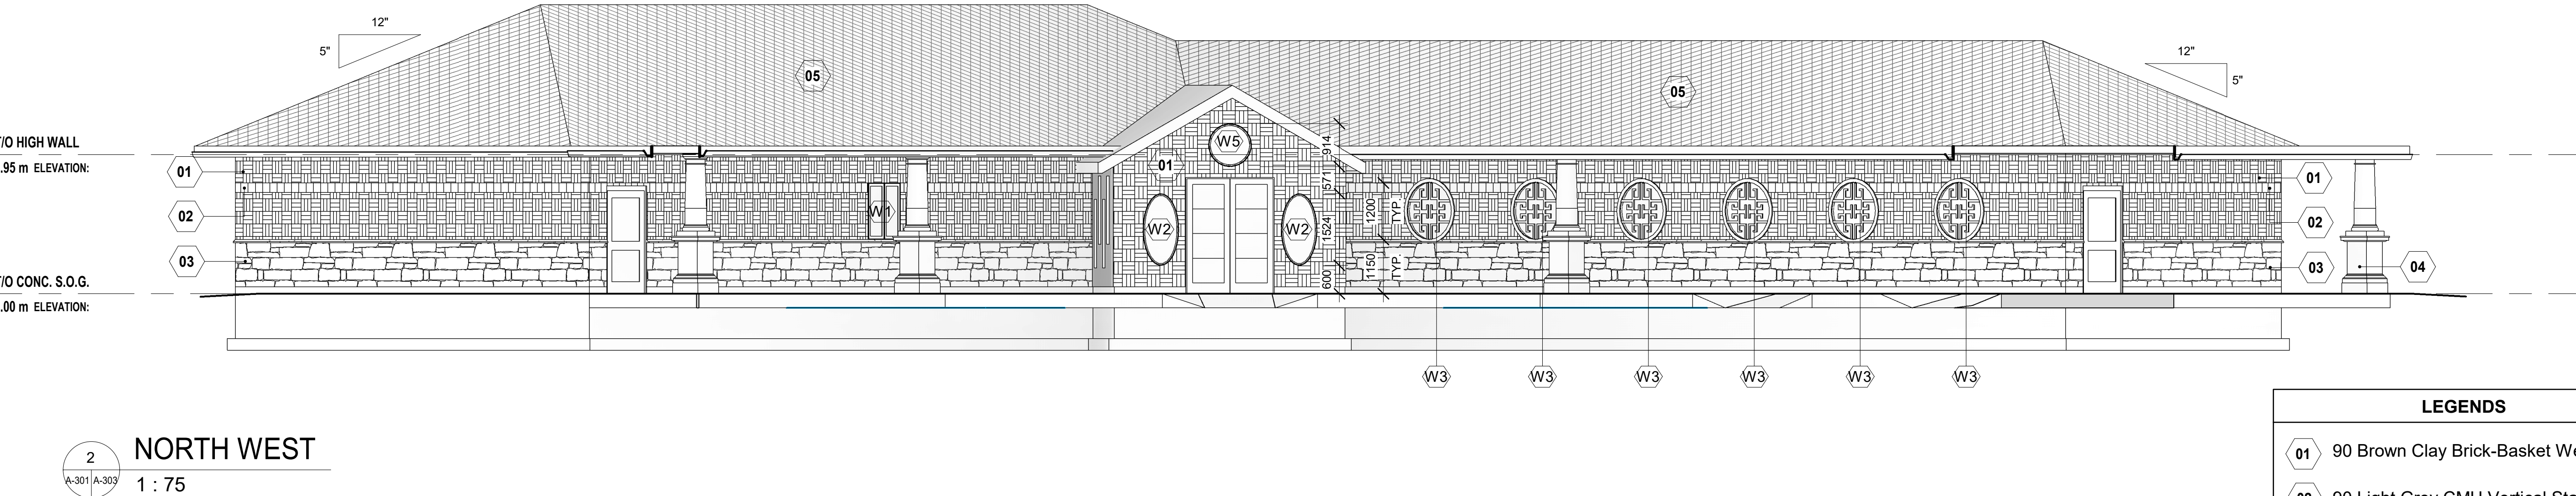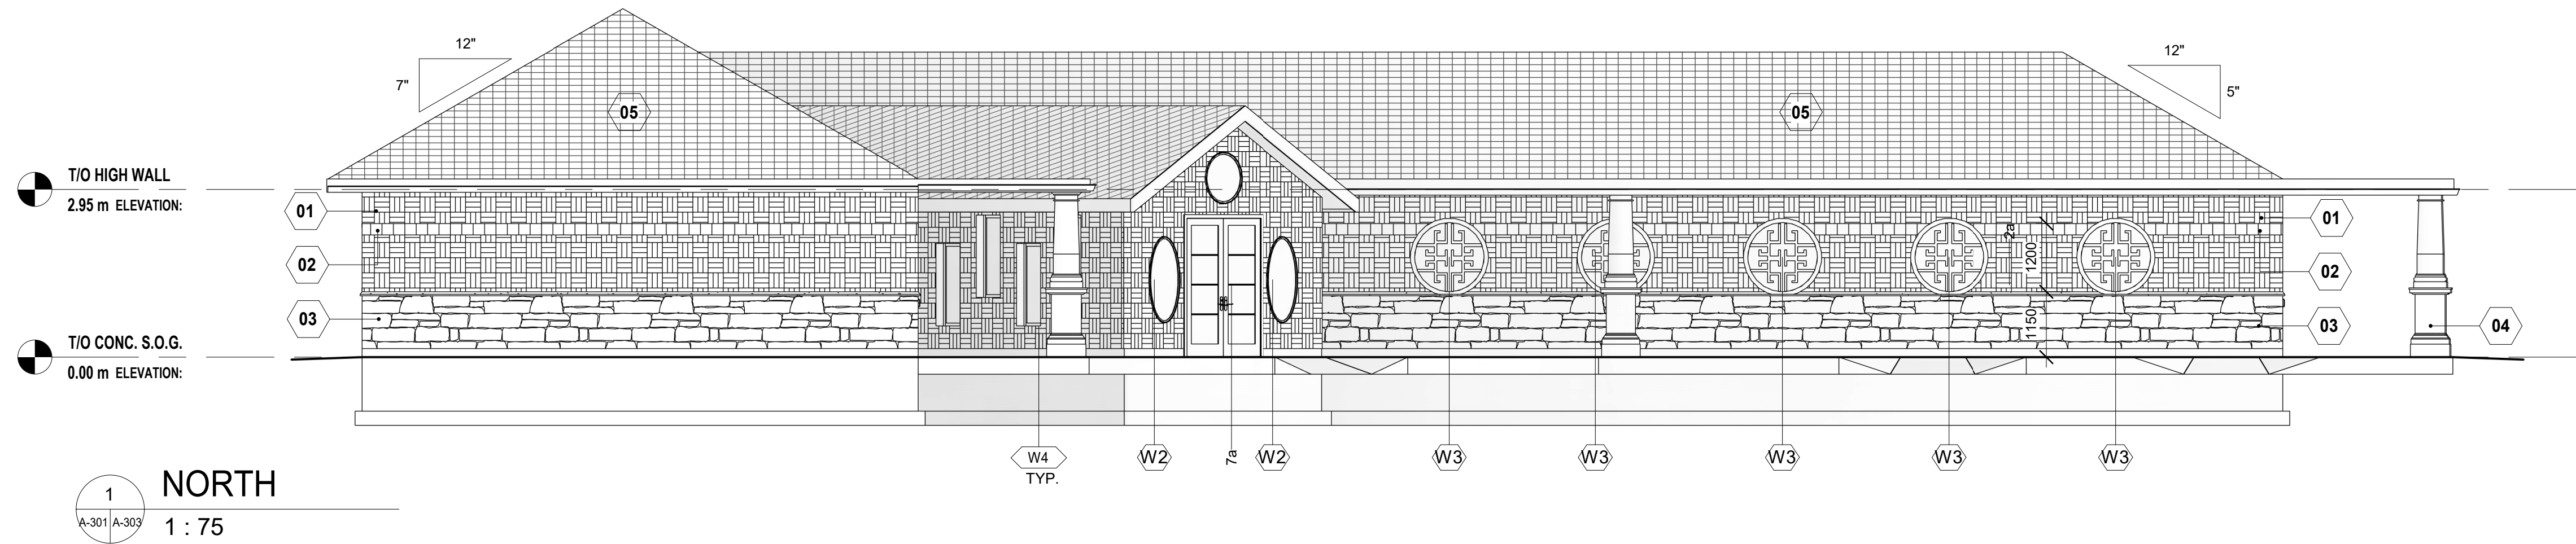

LEGENDS	
01	90 Brown Clay Brick-Basket Weave
02	90 Light Grey CMU Vertical Stack Bond
03	90 Artiste 2 Stone-Standard-Marble Grey
04	Doric Column TYP.
05	Roof TYP.

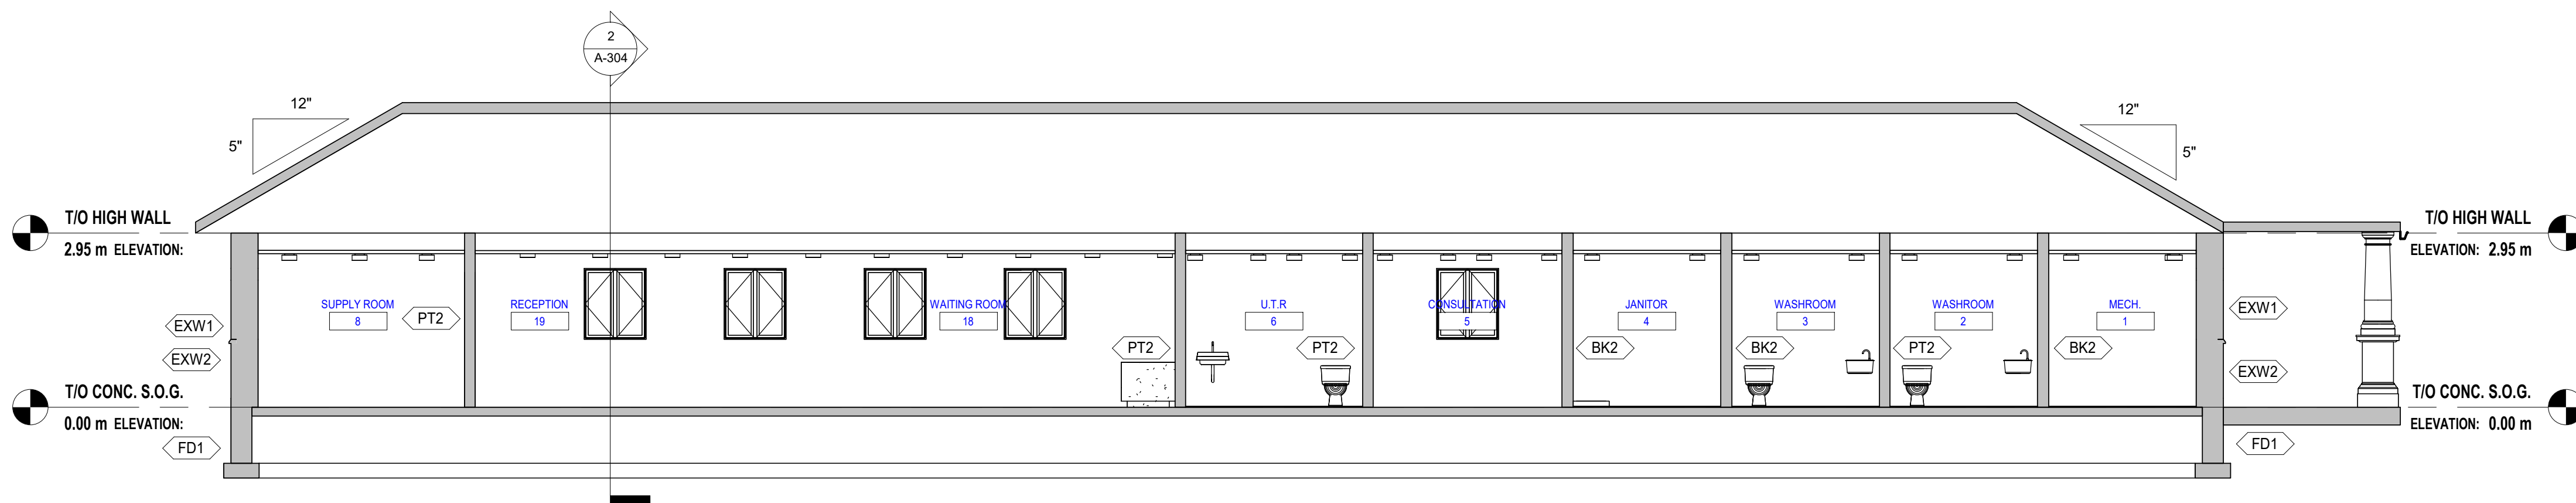

Door Schedule				
Type Mark	Count	Height	Width	Family and Type
D1	2	2438	1829	Door-Exterior-Double-Full Glass-Wood_Clad: 1829 x 2438
D2	3	2184	1219	Door-Exterior-Single-Two_Lite: 1219 x 2184
D3	11	2184	1067	Door-Passage-Single-Vision_Lite: sample
D4	1	2134	915	M_Single-Flush: 0915 x 2134mm
D5	3	2438	1219	Door-Passage-Single-Flush: 1219 x 2438

Window Schedule					
Type Mark	Count	Height	Width	Sill Height	Family and Type
W1	10	1200	1050	1150	M_Window-Casement-Double: 1050 x 1250mm
W2	2	1524	762	600	Window-Fixed-Oval: 1
W2	2	1524	762	914	Window-Fixed-Oval: 1
W3	6	1200	914	1150	001_CHINA_WINDOW: 1
W5	1	914	914	2695	Window-Fixed-Round: 1

PROJECT TITLE
OXFORD WELLNESS
CENTRE


CLIENT:
FANSHAWE COLLEGE

PROJECT ADDRESS
LONDON, ON

DRAWING TITLE
ELEVATIONS & BUILDING SECTION

CHECKED JF | DRAWN AFNM | DATE 03/14/24

W24-001 | A-303
PROJECT No. | DRAWING

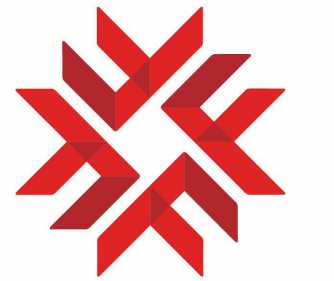

FANSHAWE
DONALD J. SMITH
SCHOOL OF BUILDING
TECHNOLOGY

NORTH ARROW

PRELIMINARY
NOT FOR CONSTRUCTION

PROJECT TITLE
**OXFORD WELLNESS
CENTRE**
CLIENT:
FANSHAWE COLLEGE
PROJECT ADDRESS
LONDON, ON

DRAWING TITLE
WALL SECTIONS & DETAILS

CHECKED | DRAWN | DATE
JF | AFNM | 02/29/24

W24-001 | **A-304**
PROJECT No. | DRAWING

E:\Working drawing\New folder\WD - Arch-1030 - CMU Wellness
Centre.rvt

4/4/2024 3:57:46 PM

