


DOODLE

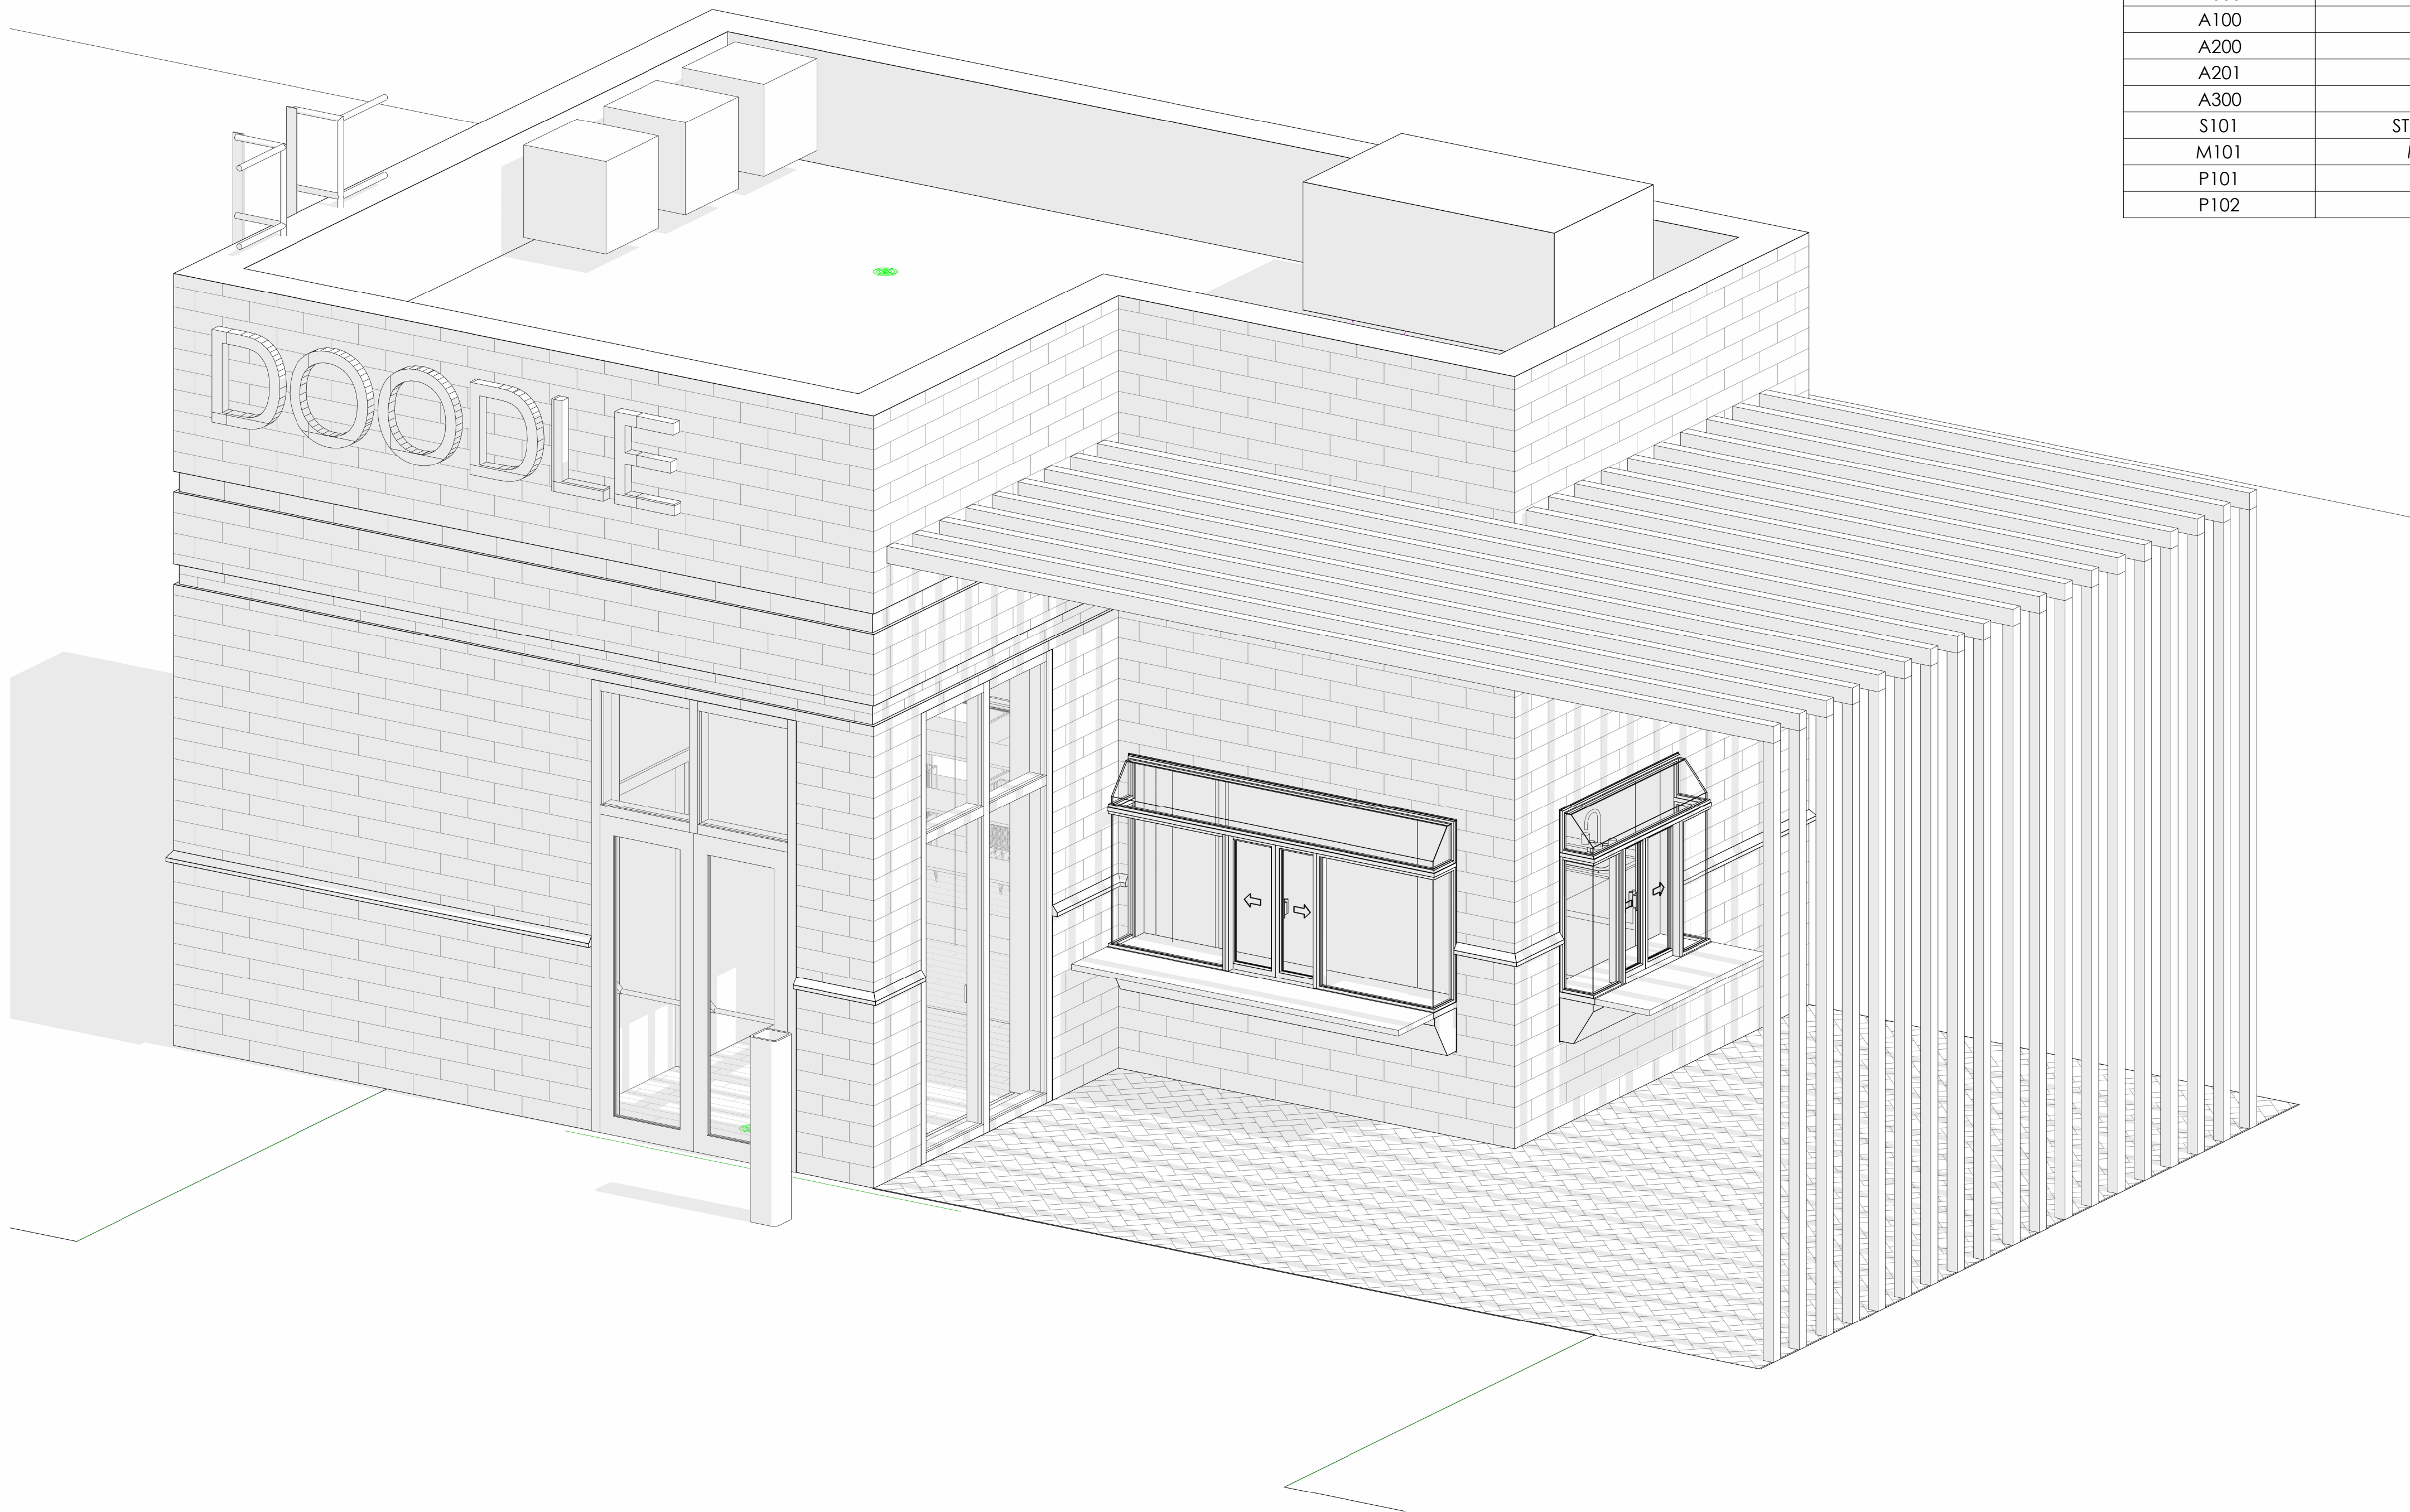

ARCHITECT
MANASWI PATEL

PROJECT MANAGER
KARUNYAA KARUNYAA

STRUCTURAL ENGINEER
KHUSHI SORATHIA

M.E.P. ENGINEER
ABUL FAZAL NOOR MOHAMED

DOODLE	
SHEET NO.	SHEET NAME
A000	COVER PAGE
A100	FLOOR PLAN
A200	ELEVATIONS
A201	ELEVATIONS
A300	SECTION
S101	STRUCTURAL PLANS AND 3DS
M101	MEP PLAN AND 3D VIEWS
P101	SCHEDULE
P102	COST ESTIMATION



NORTH ARROW



GRENRAL NOTES:-

- 1. DO NOT SCALE DRAWINGS. WRITTEN DIMENSIONS SHALL HAVE PRECEDENCE OVER SCALED DIMENSIONS.
- 2. ALL WORK SHALL COMPLY WITH THE 2012 ONTARIO BUILDING CODE AND AMENDMENTS.
- 3. CONTRACTORS MUST CHECK AND VERIFY ALL DIMENSIONS AND SPECIFICATIONS AND REPORT ANY DISCREPANCIES TO THE ARCHITECT BEFORE PROCEEDING WITH THE WORK.
- 4. ALL CONTRACTORS AND SUB-CONTRACTORS SHALL HAVE A SET OF APPROVED CONSTRUCTION DOCUMENTS ON SITE AT ALL TIMES.
- 5. ALL DOCUMENTS REMAIN THE PROPERTY OF THE ARCHITECT. UNAUTHROIZED USE, MODIFICATION, AND/OR REPRODUCTION OF THESE DOCUMENTS IS PROHIBITED WITHOUT WRITTEN PERMISSION. THE CONTRACT DOCUMENTS WERE PREPARED BY THE CONSULTANT FOR THE ACCOUNT OF THE OWNER.
- 6. THE MATERIAL CONTAINED HEREIN REFLECTS THE CONSULTANTS BEST JUDEGMENT IN LIGHT OF THE INFORMATION AVAILABLE TO HIM/HER AT THE TIME OF PREPARATION. ANY USE WHICH A THIRD PARTY MAKES OF THE CONTRACT DOCUMENTS, OR ANY RELIANCE ON/OR DESCIIONS TO BE MADE BASED ON THEM ARE THE RESPONSIBILITY OF SUCH THIRD PARTIES.
- 7. THE CONSULTANT ACCEPTS NO RESPONSIBILITY FOR DAMAGES, IF ANY, SUFFERED BY ANY THIRD PARTY AS A RESULT OF DECISIONS MADE OR ACTIONS BASED ON THE CONTRACT DOCUMENTS

PRELIMINARY
NOT FOR CONSTRUCTION

PROJECT TITLE
DOODLE


CLIENT:
FANSHAWE COLLEGE
PROJECT ADDRESS
LONDON , ON

DRAWING TITLE
COVER PAGE

CHECKED | DRAWN | DATE
JF | MP | 07/30/25




3002-25S
PROJECT No.

A000
DRAWING

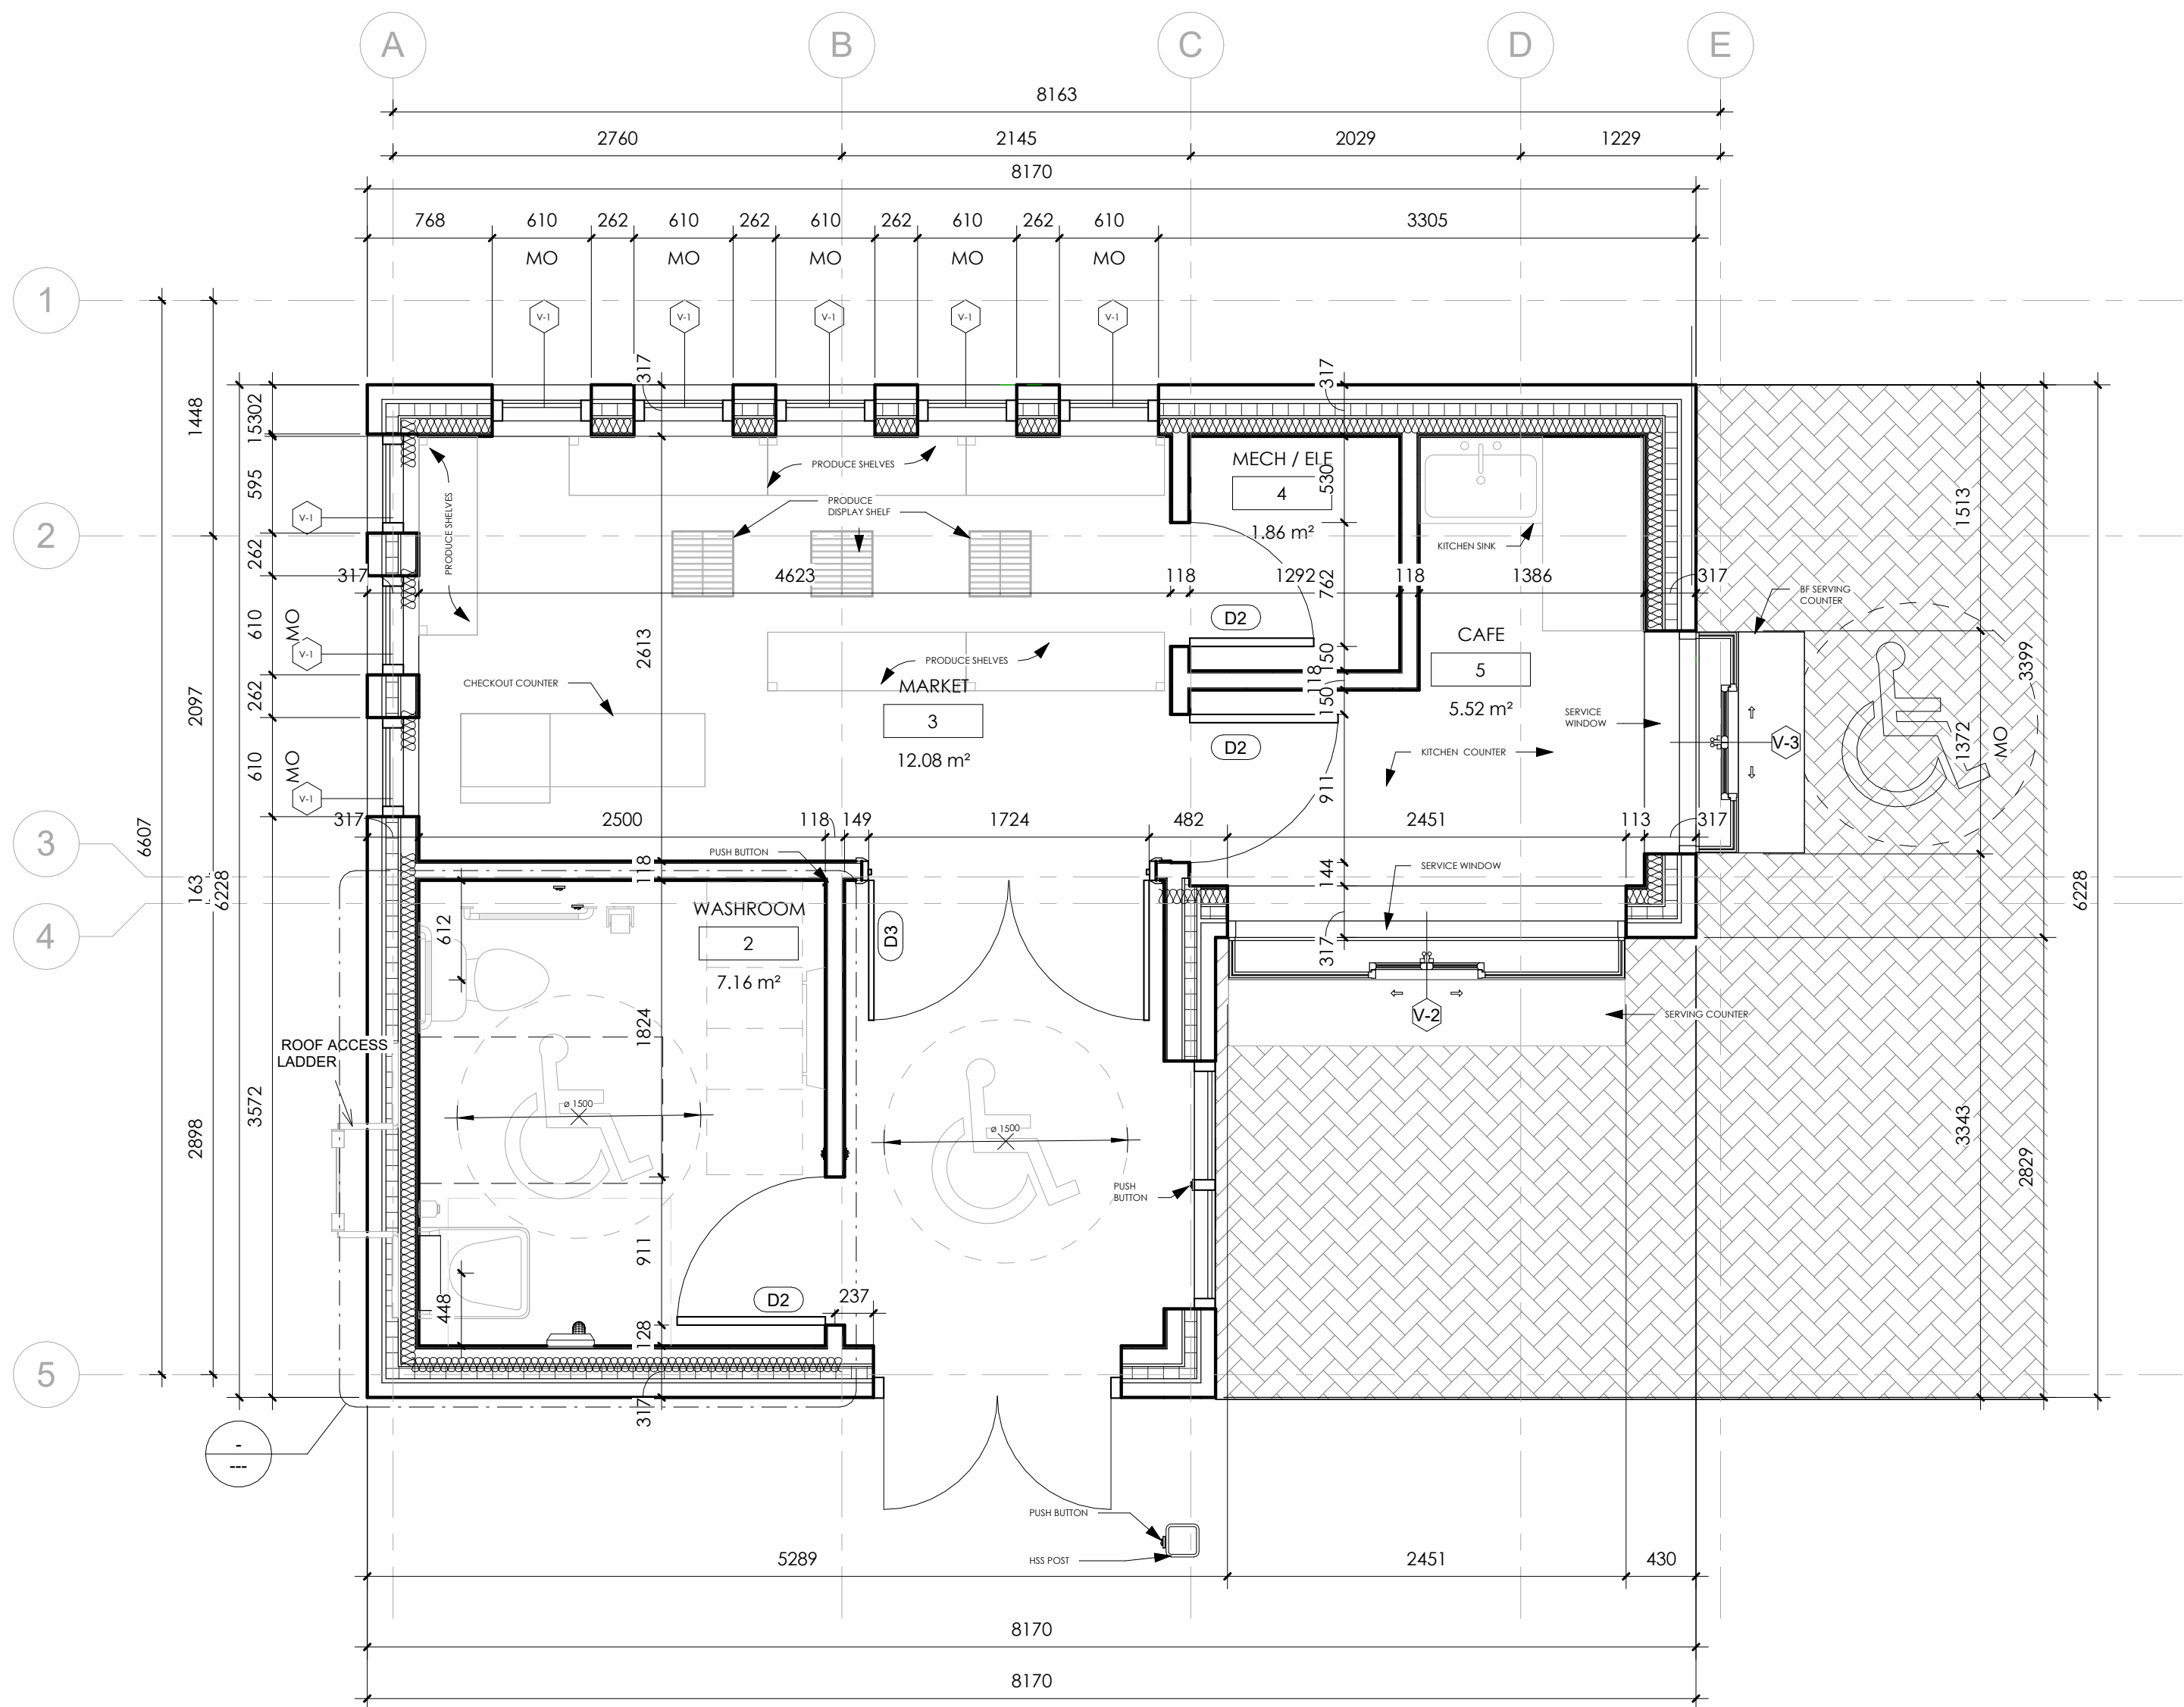

1 FLOOR PLAN
3/8" = 1'-0"

ASSEMBLIES				
EXTERIOR AND INTERIOR WALLS	W-E1/MASONRY VENEER WALL	W-E2/CURTAIN WALL	W-F1/ 200 FOUNDATION WALL	FL-FL1/ 150 SLAB ON GRADE
	90 BRICK MASONRY VENEER 25 AIR SPACE AIR BARRIER 75 RIGID INSULATION 16 O.S.B. SHEATHING 92 METAL STUD @ 610MM O.C. 6 MIL POLY VAPOUR BARRIER 13 GYPSUM WALL BOARD	THERMALLY BROKEN CLEAR ANODIZED ALUMINUM FRAMING (TYP.) ARGON FILLED CLEAR DUAL PANE GLAZING (REFER TO ELEVATION)	200 C.I.P. FOUNDATION WALL TORCH APPLIED WATER PROOFING MEMBRANE PROTECTION BOARD FASTENED TO EXT. SIDE AS PER MANUFACTURE	150 C.I.P. CONCRETE
	W-P1/ 92 METAL STUD ON GWB ON BOTH SIDES	13 GYPSUM WALL BOARD 92 METAL STUD 13 GYPSUM WALL BOARD	W-CL1	R-R1/ EPDM ROOF
	13 GYPSUM WALL BOARD 92 METAL STUD 13 GYPSUM WALL BOARD		600 X 600 ACT PANEL	EPDM MEMBRANE 200 RIGID INSULATION w/ SLOPED INSULATION VAPOUR BARRIER 90 METAL DECK

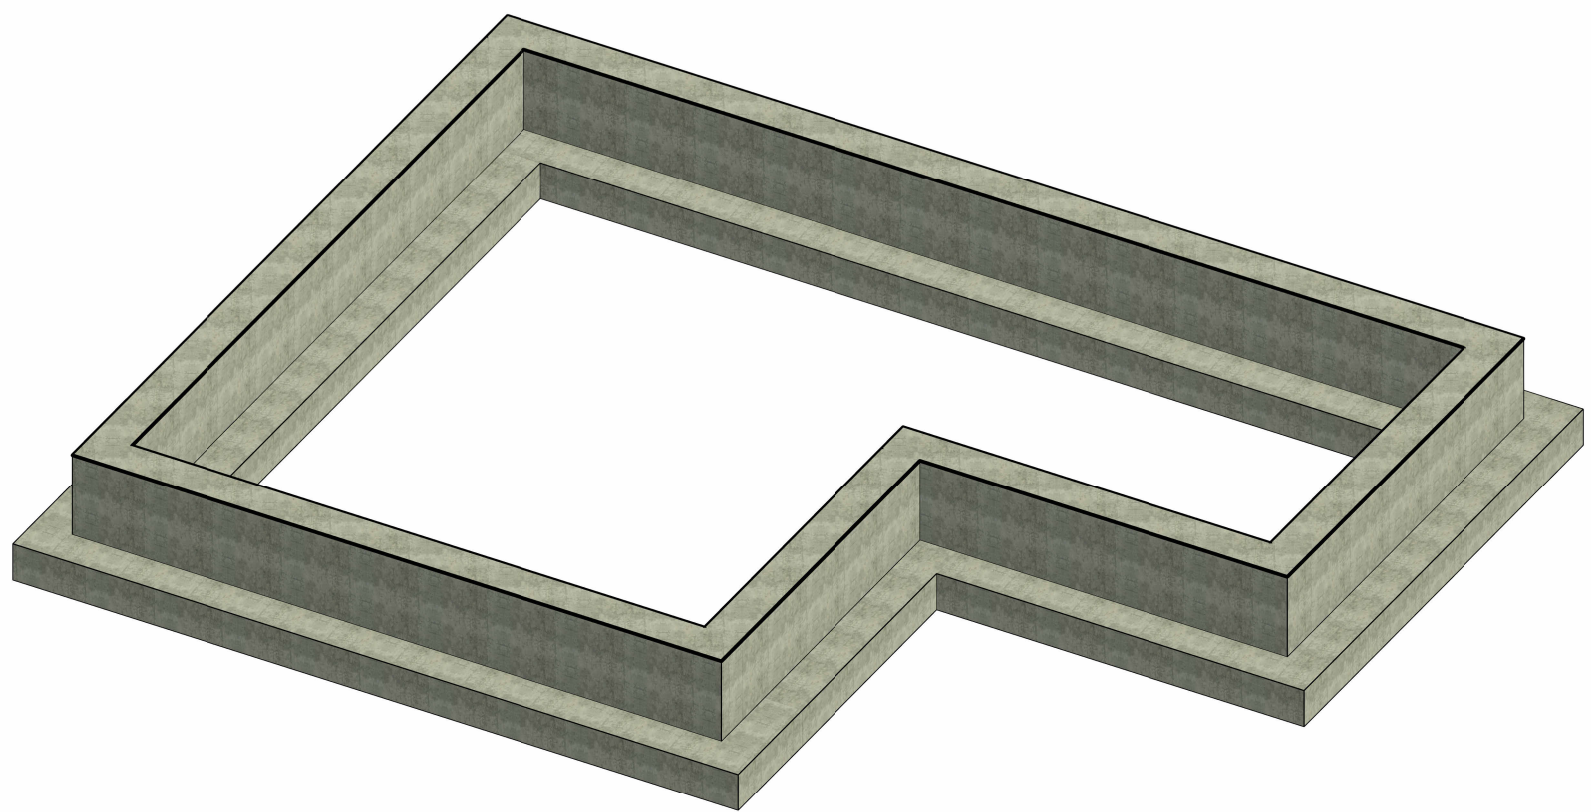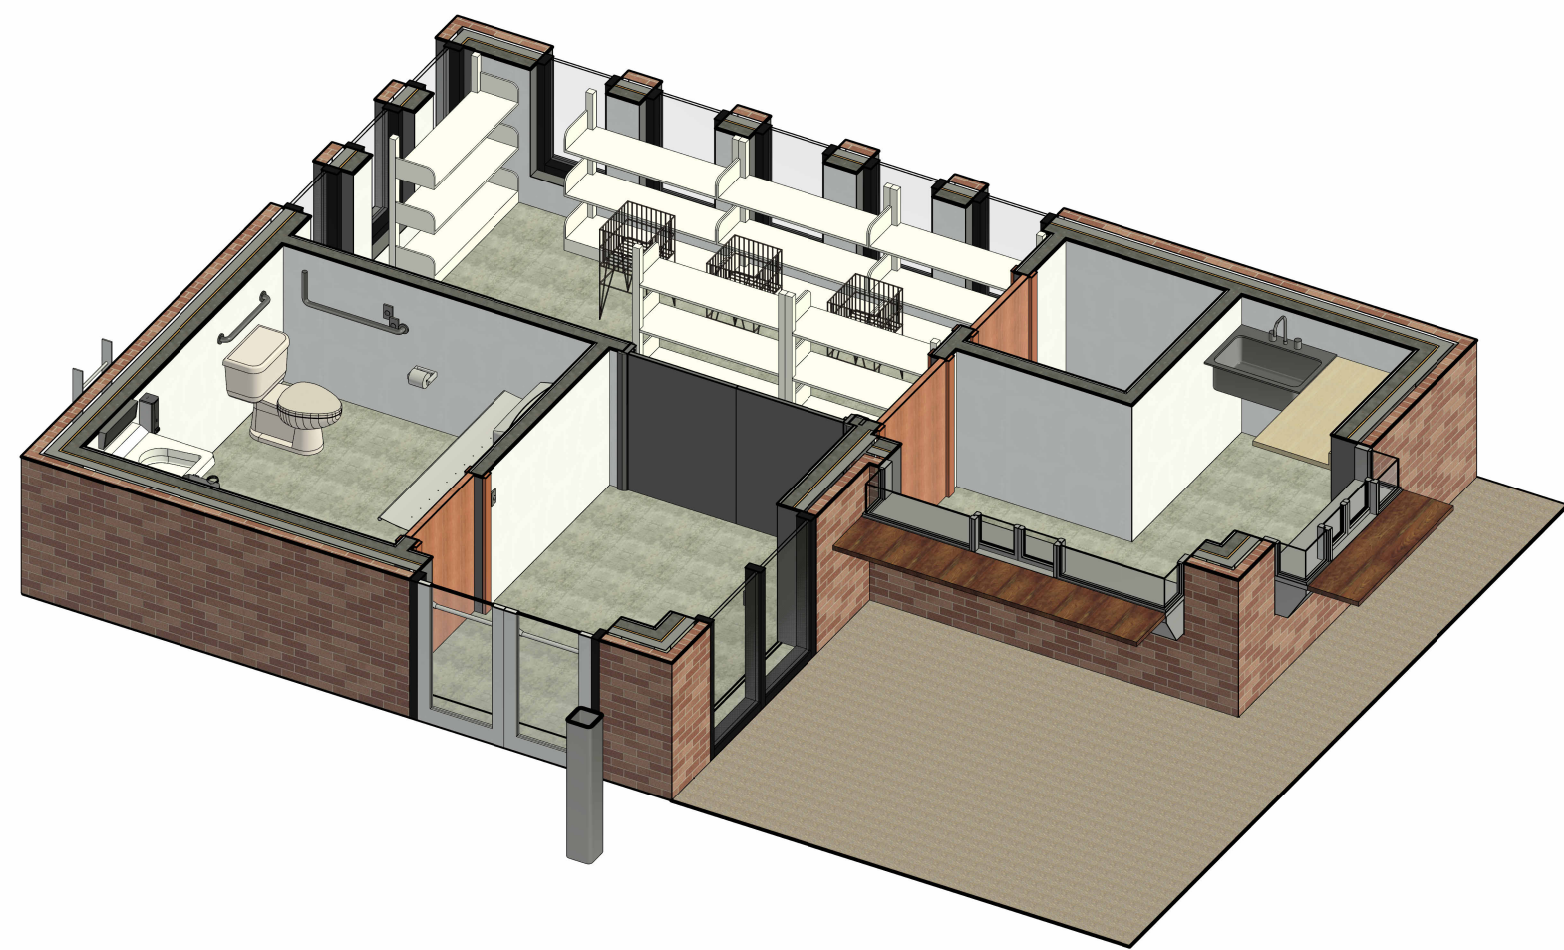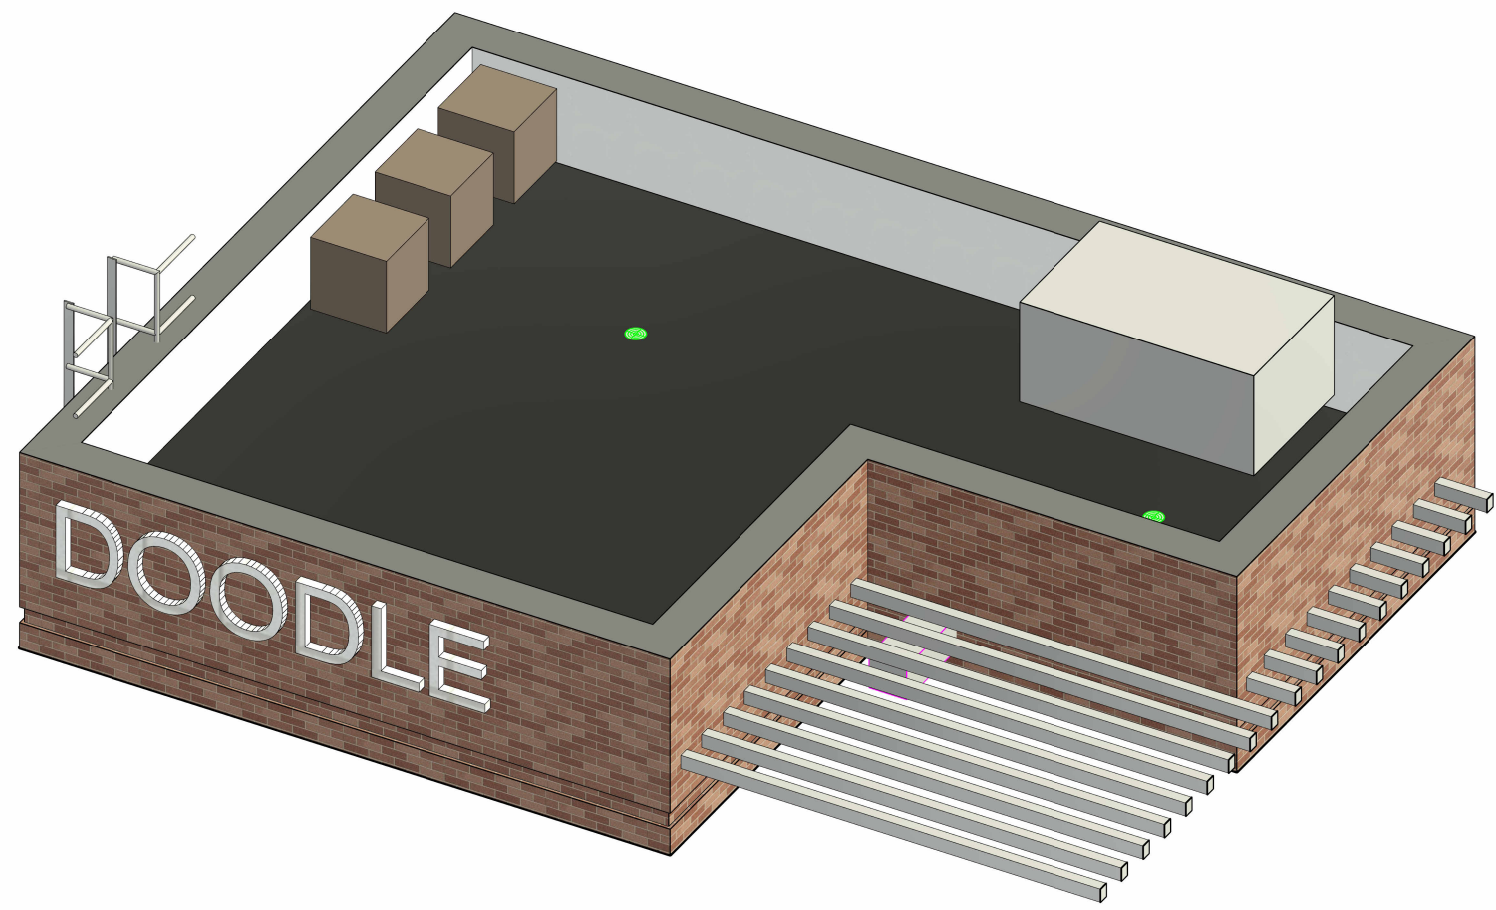

NORTH ARROW



GRENRAL NOTES:-

1. DO NOT SCALE DRAWINGS. WRITTEN DIMENSIONS SHALL HAVE PRECEDENCE OVER SCALED DIMENSIONS.
2. ALL WORK SHALL COMPLY WITH THE 2012 ONTARIO BUILDING CODE AND AMENDMENTS.
3. CONTRACTORS MUST CHECK AND VERIFY ALL DIMENSIONS AND SPECIFICATIONS AND REPORT ANY DISCREPANCIES TO THE ARCHITECT BEFORE PROCEEDING WITH THE WORK.
4. ALL CONTRACTORS AND SUB-CONTRACTORS SHALL HAVE A SET OF APPROVED CONSTRUCTION DOCUMENTS ON SITE AT ALL TIMES.
5. ALL DOCUMENTS REMAIN THE PROPERTY OF THE ARCHITECT. UNAUTHORIZED USE, MODIFICATION, AND/OR REPRODUCTION OF THESE DOCUMENTS IS PROHIBITED WITHOUT WRITTEN PERMISSION. THE CONTRACT DOCUMENTS WERE PREPARED BY THE CONSULTANT FOR THE ACCOUNT OF THE OWNER.
6. THE MATERIAL CONTAINED HEREIN REFLECTS THE CONSULTANTS BEST JUDGMENT IN LIGHT OF THE INFORMATION AVAILABLE TO HIM/HER AT THE TIME OF PREPARATION. ANY USE WHICH A THIRD PARTY MAKES OF THE CONTRACT DOCUMENTS, OR ANY RELIANCE ON/OR DECISIONS TO BE MADE BASED ON THEM ARE THE RESPONSIBILITY OF SUCH THIRD PARTIES.
7. THE CONSULTANT ACCEPTS NO RESPONSIBILITY FOR DAMAGES, IF ANY, SUFFERED BY ANY THIRD PARTY AS A RESULT OF DECISIONS MADE OR ACTIONS BASED ON THE CONTRACT DOCUMENTS

PRELIMINARY
NOT FOR CONSTRUCTION

PROJECT TITLE
DOODLE

CLIENT:
FANSHAWE COLLEGE
PROJECT ADDRESS
LONDON , ON

DRAWING TITLE
FLOOR PLAN


CHECKED | DRAWN | DATE
JF | MP | 07/30/25

3002-25S


PROJECT No.

A100

DRAWING

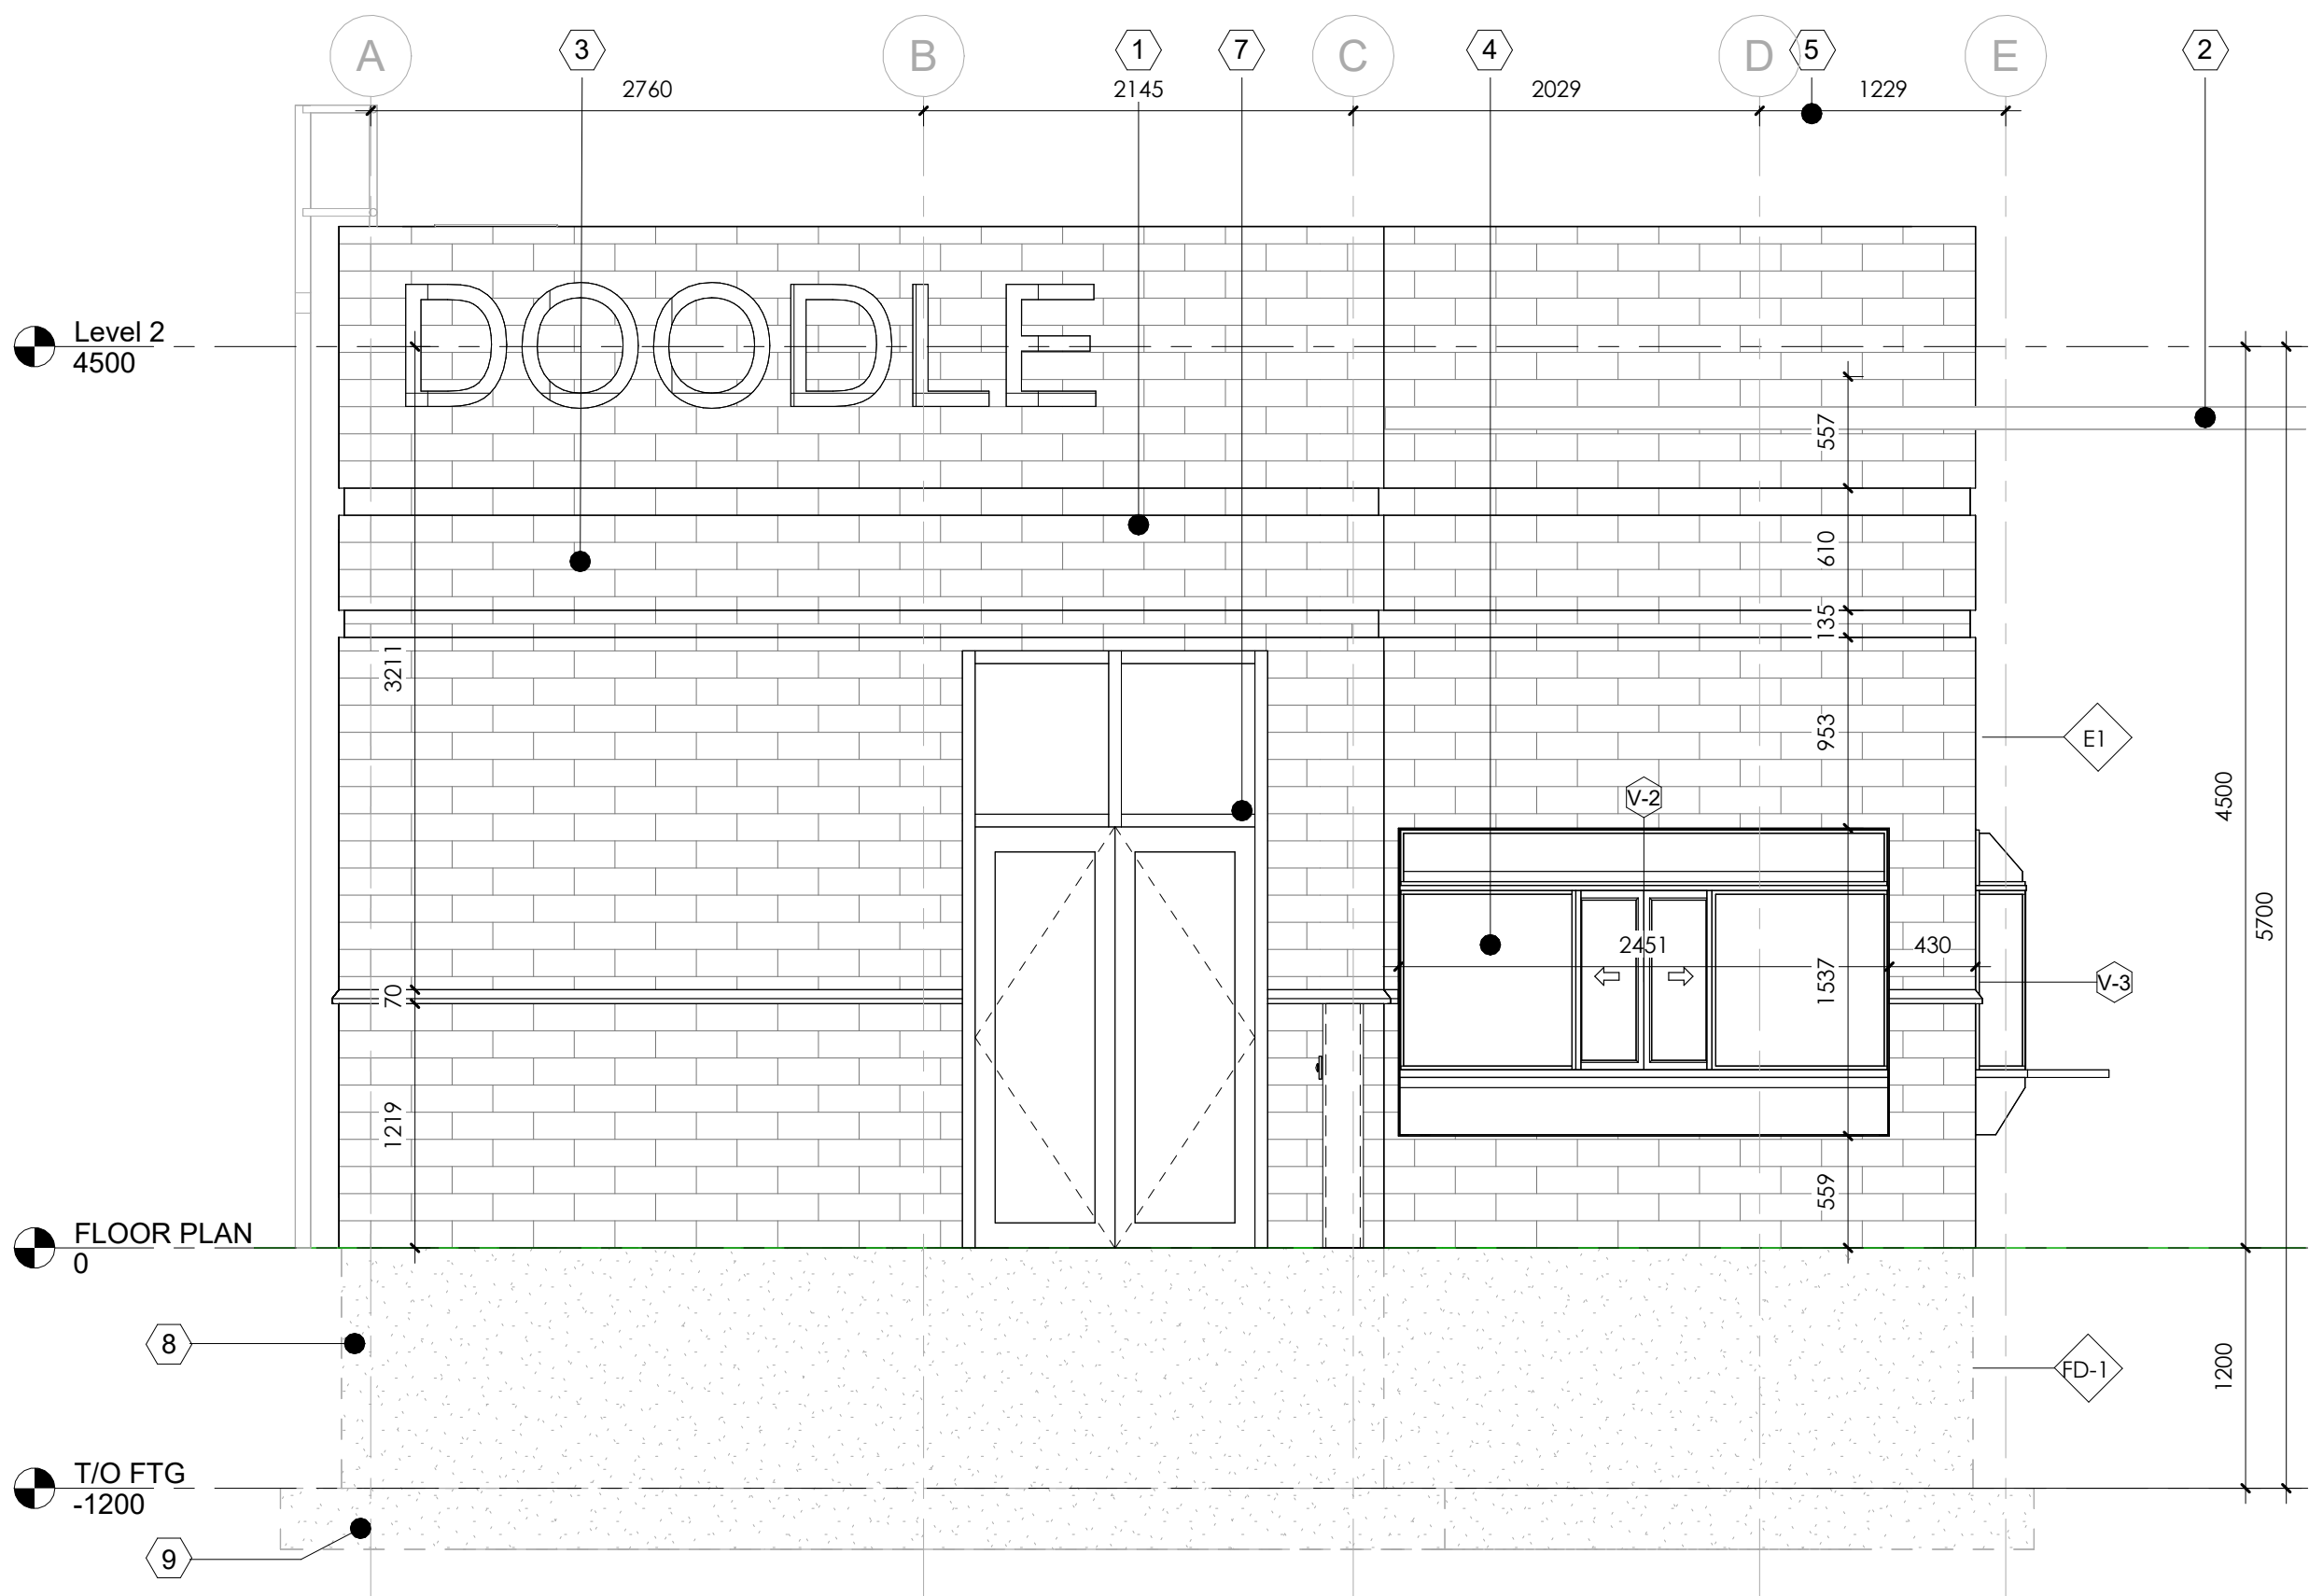

SOUTH ELEVATION
3/8" = 1'-0"

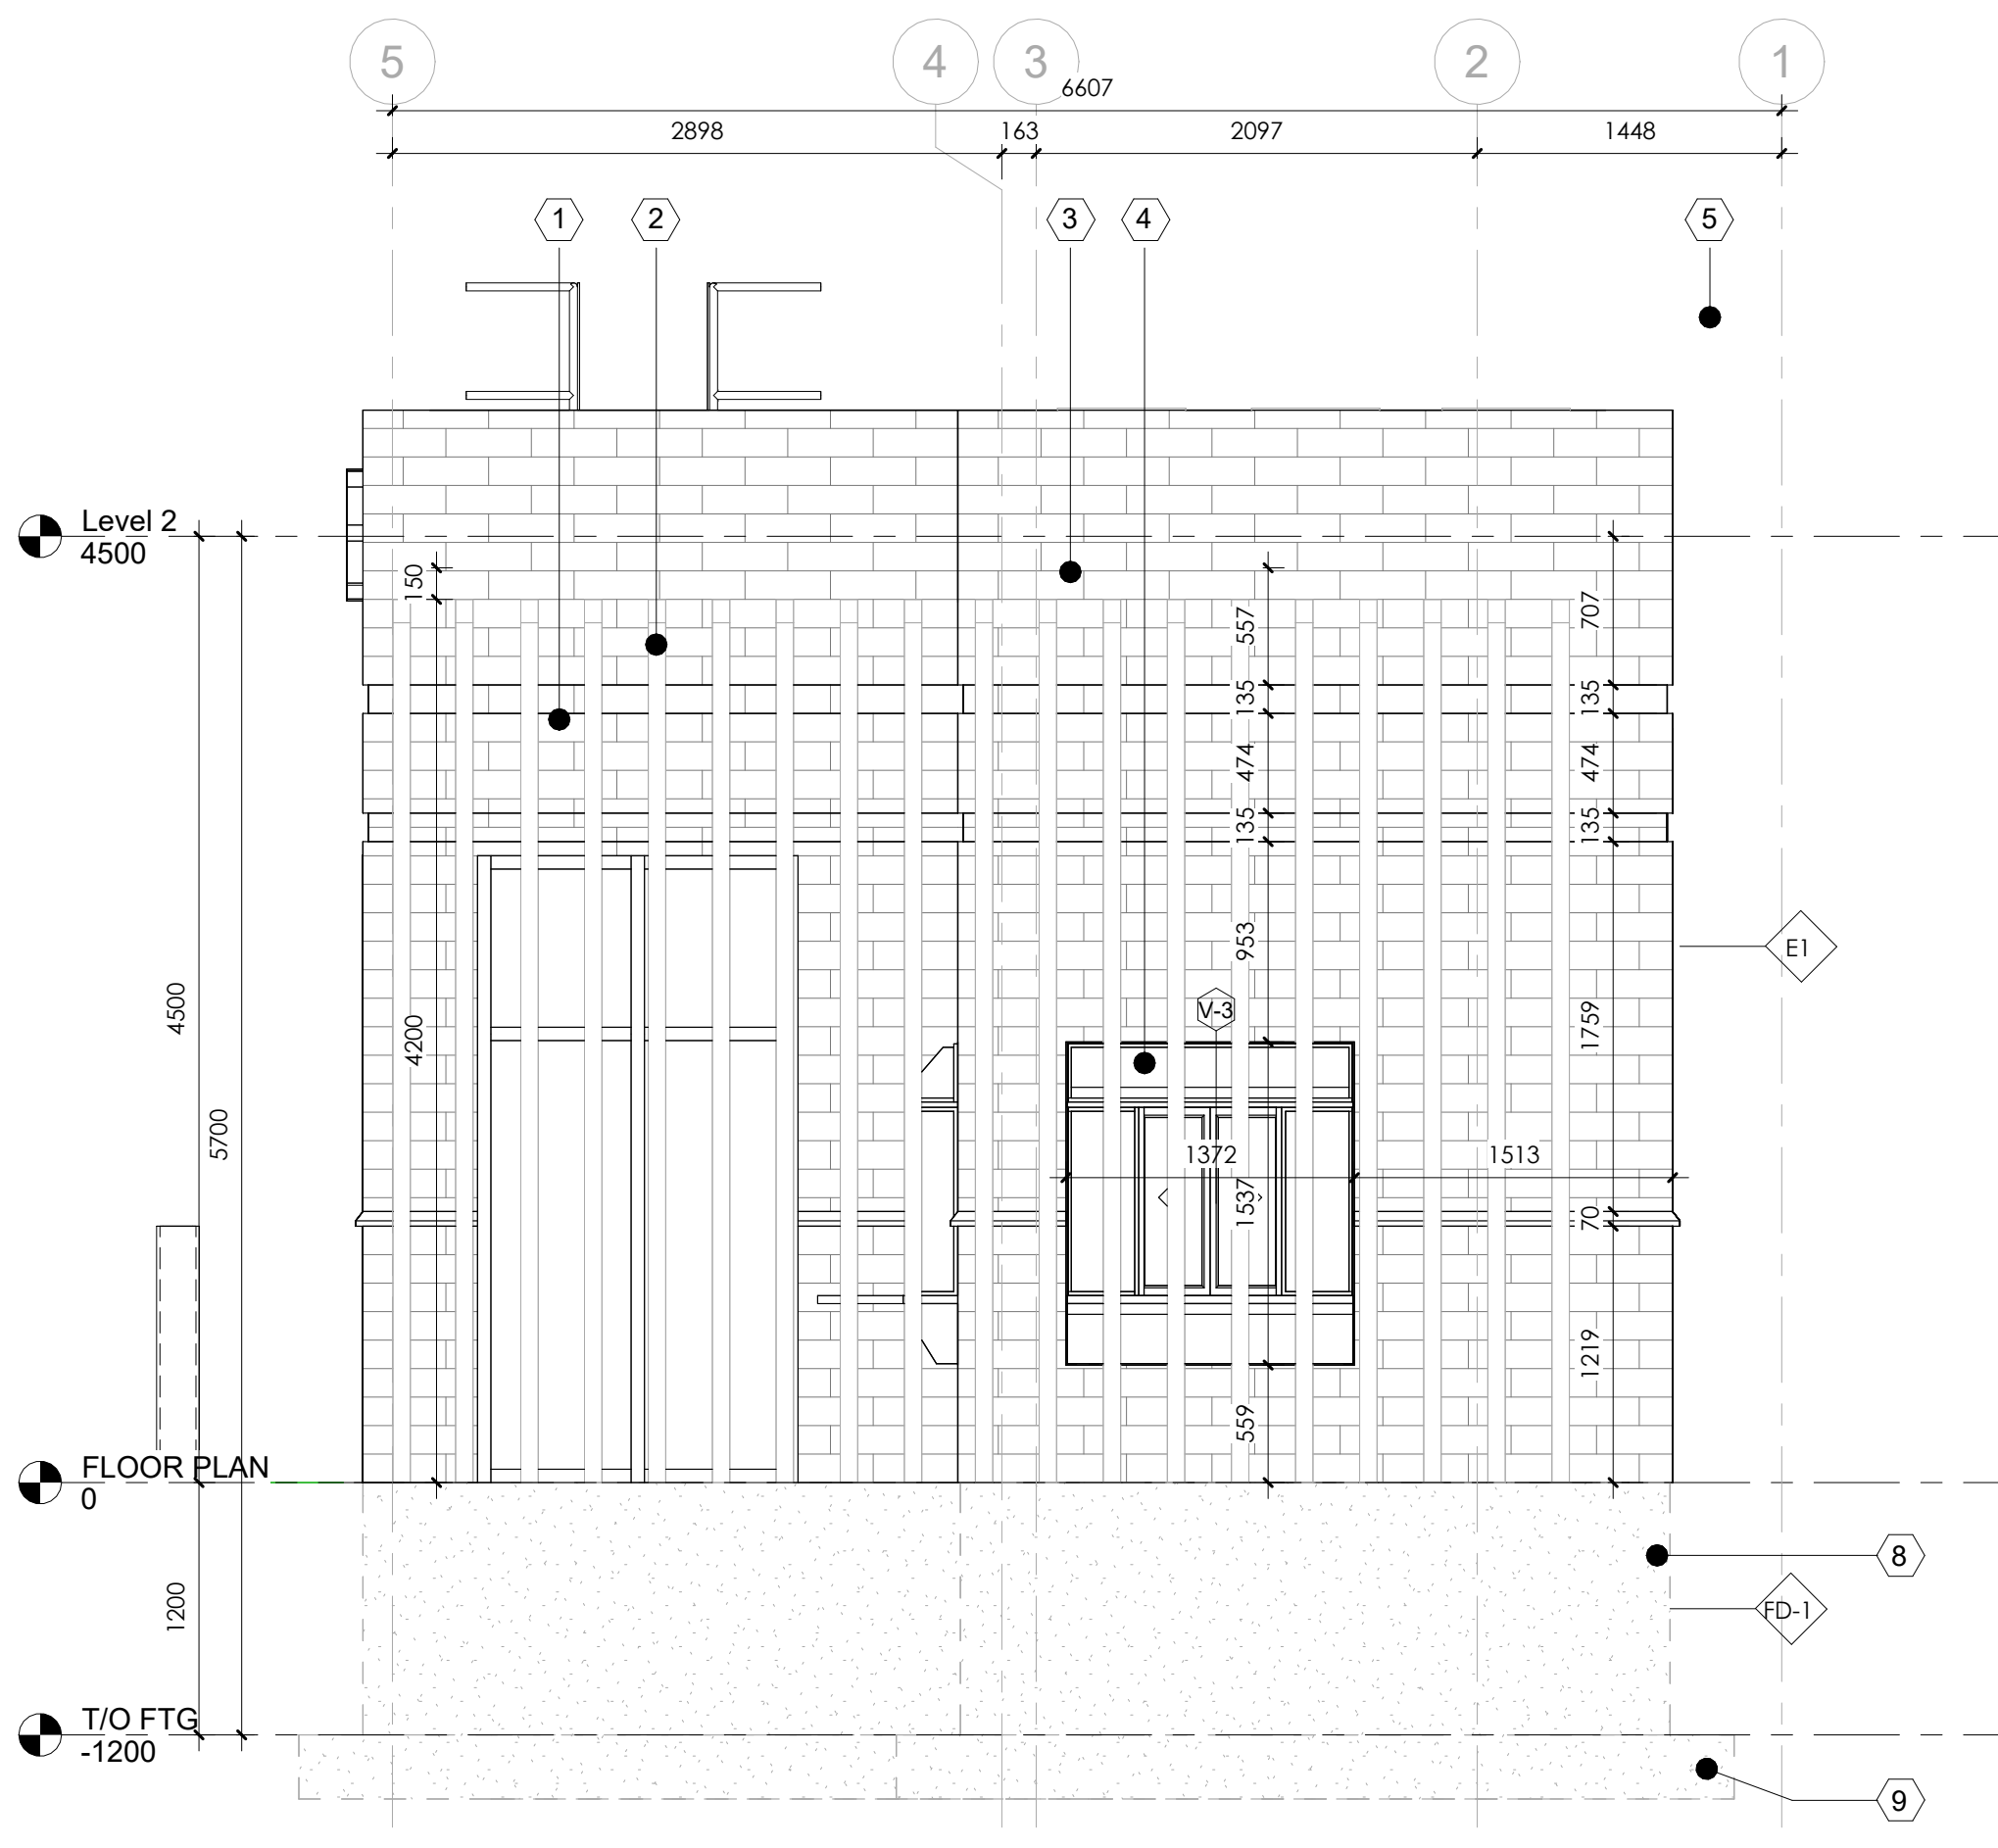

EAST ELEVATION
3/8" = 1'-0"

MATERIAL LEGEND

- CURTAIN WALL FRAMING
CLEAR GLASS SEALED UNITS IN ALUMINUM CURTAIN WALL FRAMING.
PAINTED: BLACK
- WOODEN PERGOLA: SUPPLIED AND INSTALLED BY A SPECIALIZED PERGOLA COMPANY, CONSTRUCTED USING PRESSURE-TREATED TIMBER OR ENGINEERED WOOD SUITABLE FOR EXTERIOR USE IN ONTARIO CLIMATE. FINISH TO BE WEATHER-RESISTANT STAIN OR PAINT AS SPECIFIED. DIMENSIONS AND CONNECTIONS TO BE AS PER APPROVED ARCHITECTURAL AND ENGINEERED DRAWINGS.
- ARCHITECTURAL BRICK
FINISH CONTEMPORARY SERIES NUEVA COLLECTION BRICK BY BRAMPTON BRICK
COLOUR : AUBURN MATT
- THERMALLY BROKEN DOUBLE GLAZED ALUMINUM WINDOW WITH OPERABLE PANES. FRAME TO BE PAINTED BLACK. REFER TO MANUFACTURE SPECIFICATIONS
- ROOF ACCESS LADDER. REFER TO MANUFACTURE SPECIFICATIONS
- THERMALLY BROKEN DOUBLE GLAZED ALUMINUM FIXED WINDOW. FRAME TO BE PAINTED BLACK. REFER TO MANUFACTURE SPECIFICATIONS
- ALUMINIUM FRAMED GLAZED DOUBLE DOOR. FRAMES PAINTED BLACK. REFER TO MANUFACTURE SPECIFICATIONS.
- 12" CAST IN PLACE CONCRETE FOUNDATION W/ KEYWAY
REFER TO STRUCTURE DRAWINGS.
- 36x12" CAST IN PLACE CONCRETE STRIP FOOTING
REFER TO STRUCTURE DRAWINGS.

NORTH ARROW



GENERAL NOTES:-

- DO NOT SCALE DRAWINGS. WRITTEN DIMENSIONS SHALL HAVE PRECEDENCE OVER SCALED DIMENSIONS.
- ALL WORK SHALL COMPLY WITH THE 2012 ONTARIO BUILDING CODE AND AMENDMENTS.
- CONTRACTORS MUST CHECK AND VERIFY ALL DIMENSIONS AND SPECIFICATIONS AND REPORT ANY DISCREPANCIES TO THE ARCHITECT BEFORE PROCEEDING WITH THE WORK.
- ALL CONTRACTORS AND SUB-CONTRACTORS SHALL HAVE A SET OF APPROVED CONSTRUCTION DOCUMENTS ON SITE AT ALL TIMES.
- ALL DOCUMENTS REMAIN THE PROPERTY OF THE ARCHITECT. UNAUTHORIZED USE, MODIFICATION, AND/OR REPRODUCTION OF THESE DOCUMENTS IS PROHIBITED WITHOUT WRITTEN PERMISSION. THE CONTRACT DOCUMENTS WERE PREPARED BY THE CONSULTANT FOR THE ACCOUNT OF THE OWNER.
- THE MATERIAL CONTAINED HEREIN REFLECTS THE CONSULTANT'S BEST JUDGMENT IN LIGHT OF THE INFORMATION AVAILABLE TO HIM/HER AT THE TIME OF PREPARATION. ANY USE WHICH A THIRD PARTY MAKES OF THE CONTRACT DOCUMENTS, OR ANY RELIANCE ON/OR DECISIONS TO BE MADE BASED ON THEM ARE THE RESPONSIBILITY OF SUCH THIRD PARTIES.
- THE CONSULTANT ACCEPTS NO RESPONSIBILITY FOR DAMAGES, IF ANY, SUFFERED BY ANY THIRD PARTY AS A RESULT OF DECISIONS MADE OR ACTIONS BASED ON THE CONTRACT DOCUMENTS

PRELIMINARY
NOT FOR CONSTRUCTION

PROJECT TITLE
DOODLE


CLIENT:
FANSHAWE COLLEGE
PROJECT ADDRESS
LONDON , ON

DRAWING TITLE
ELEVATIONS



CHECKED | DRAWN | DATE
JF | MP | 07/30/25

3002-25S
PROJECT No.

A200
DRAWING

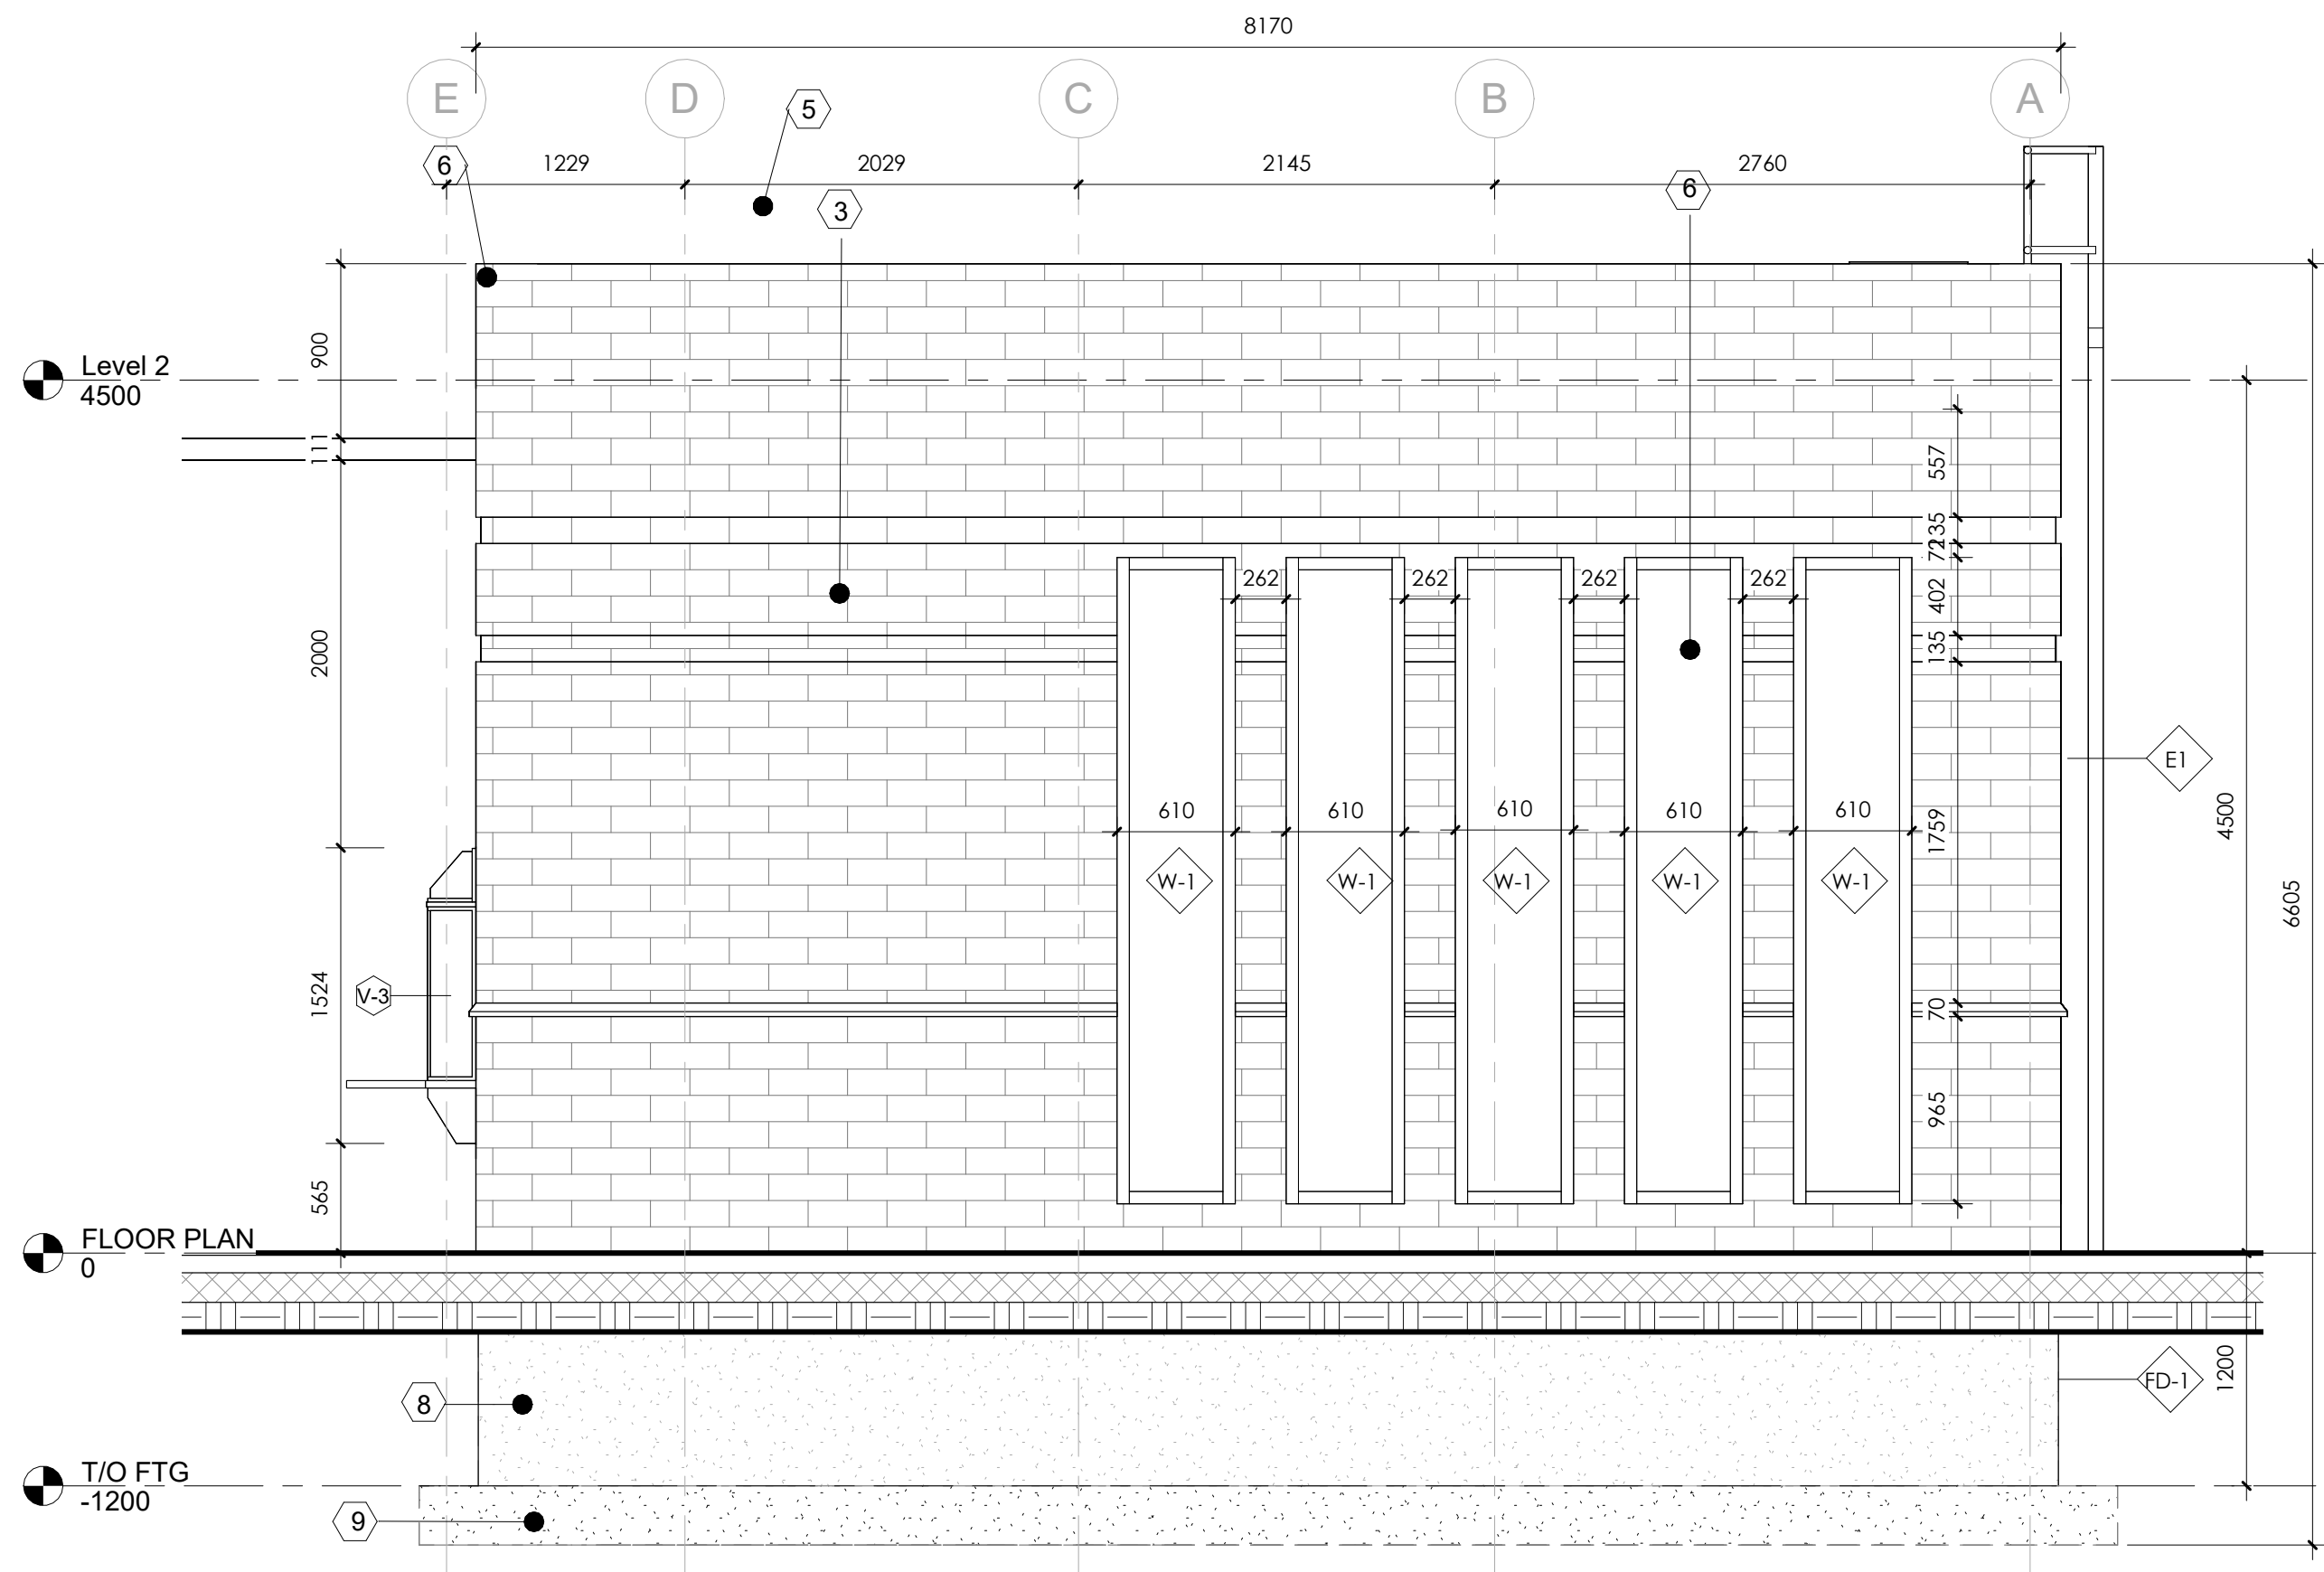


1 NORTH ELEVATION
3/8" = 1'-0"

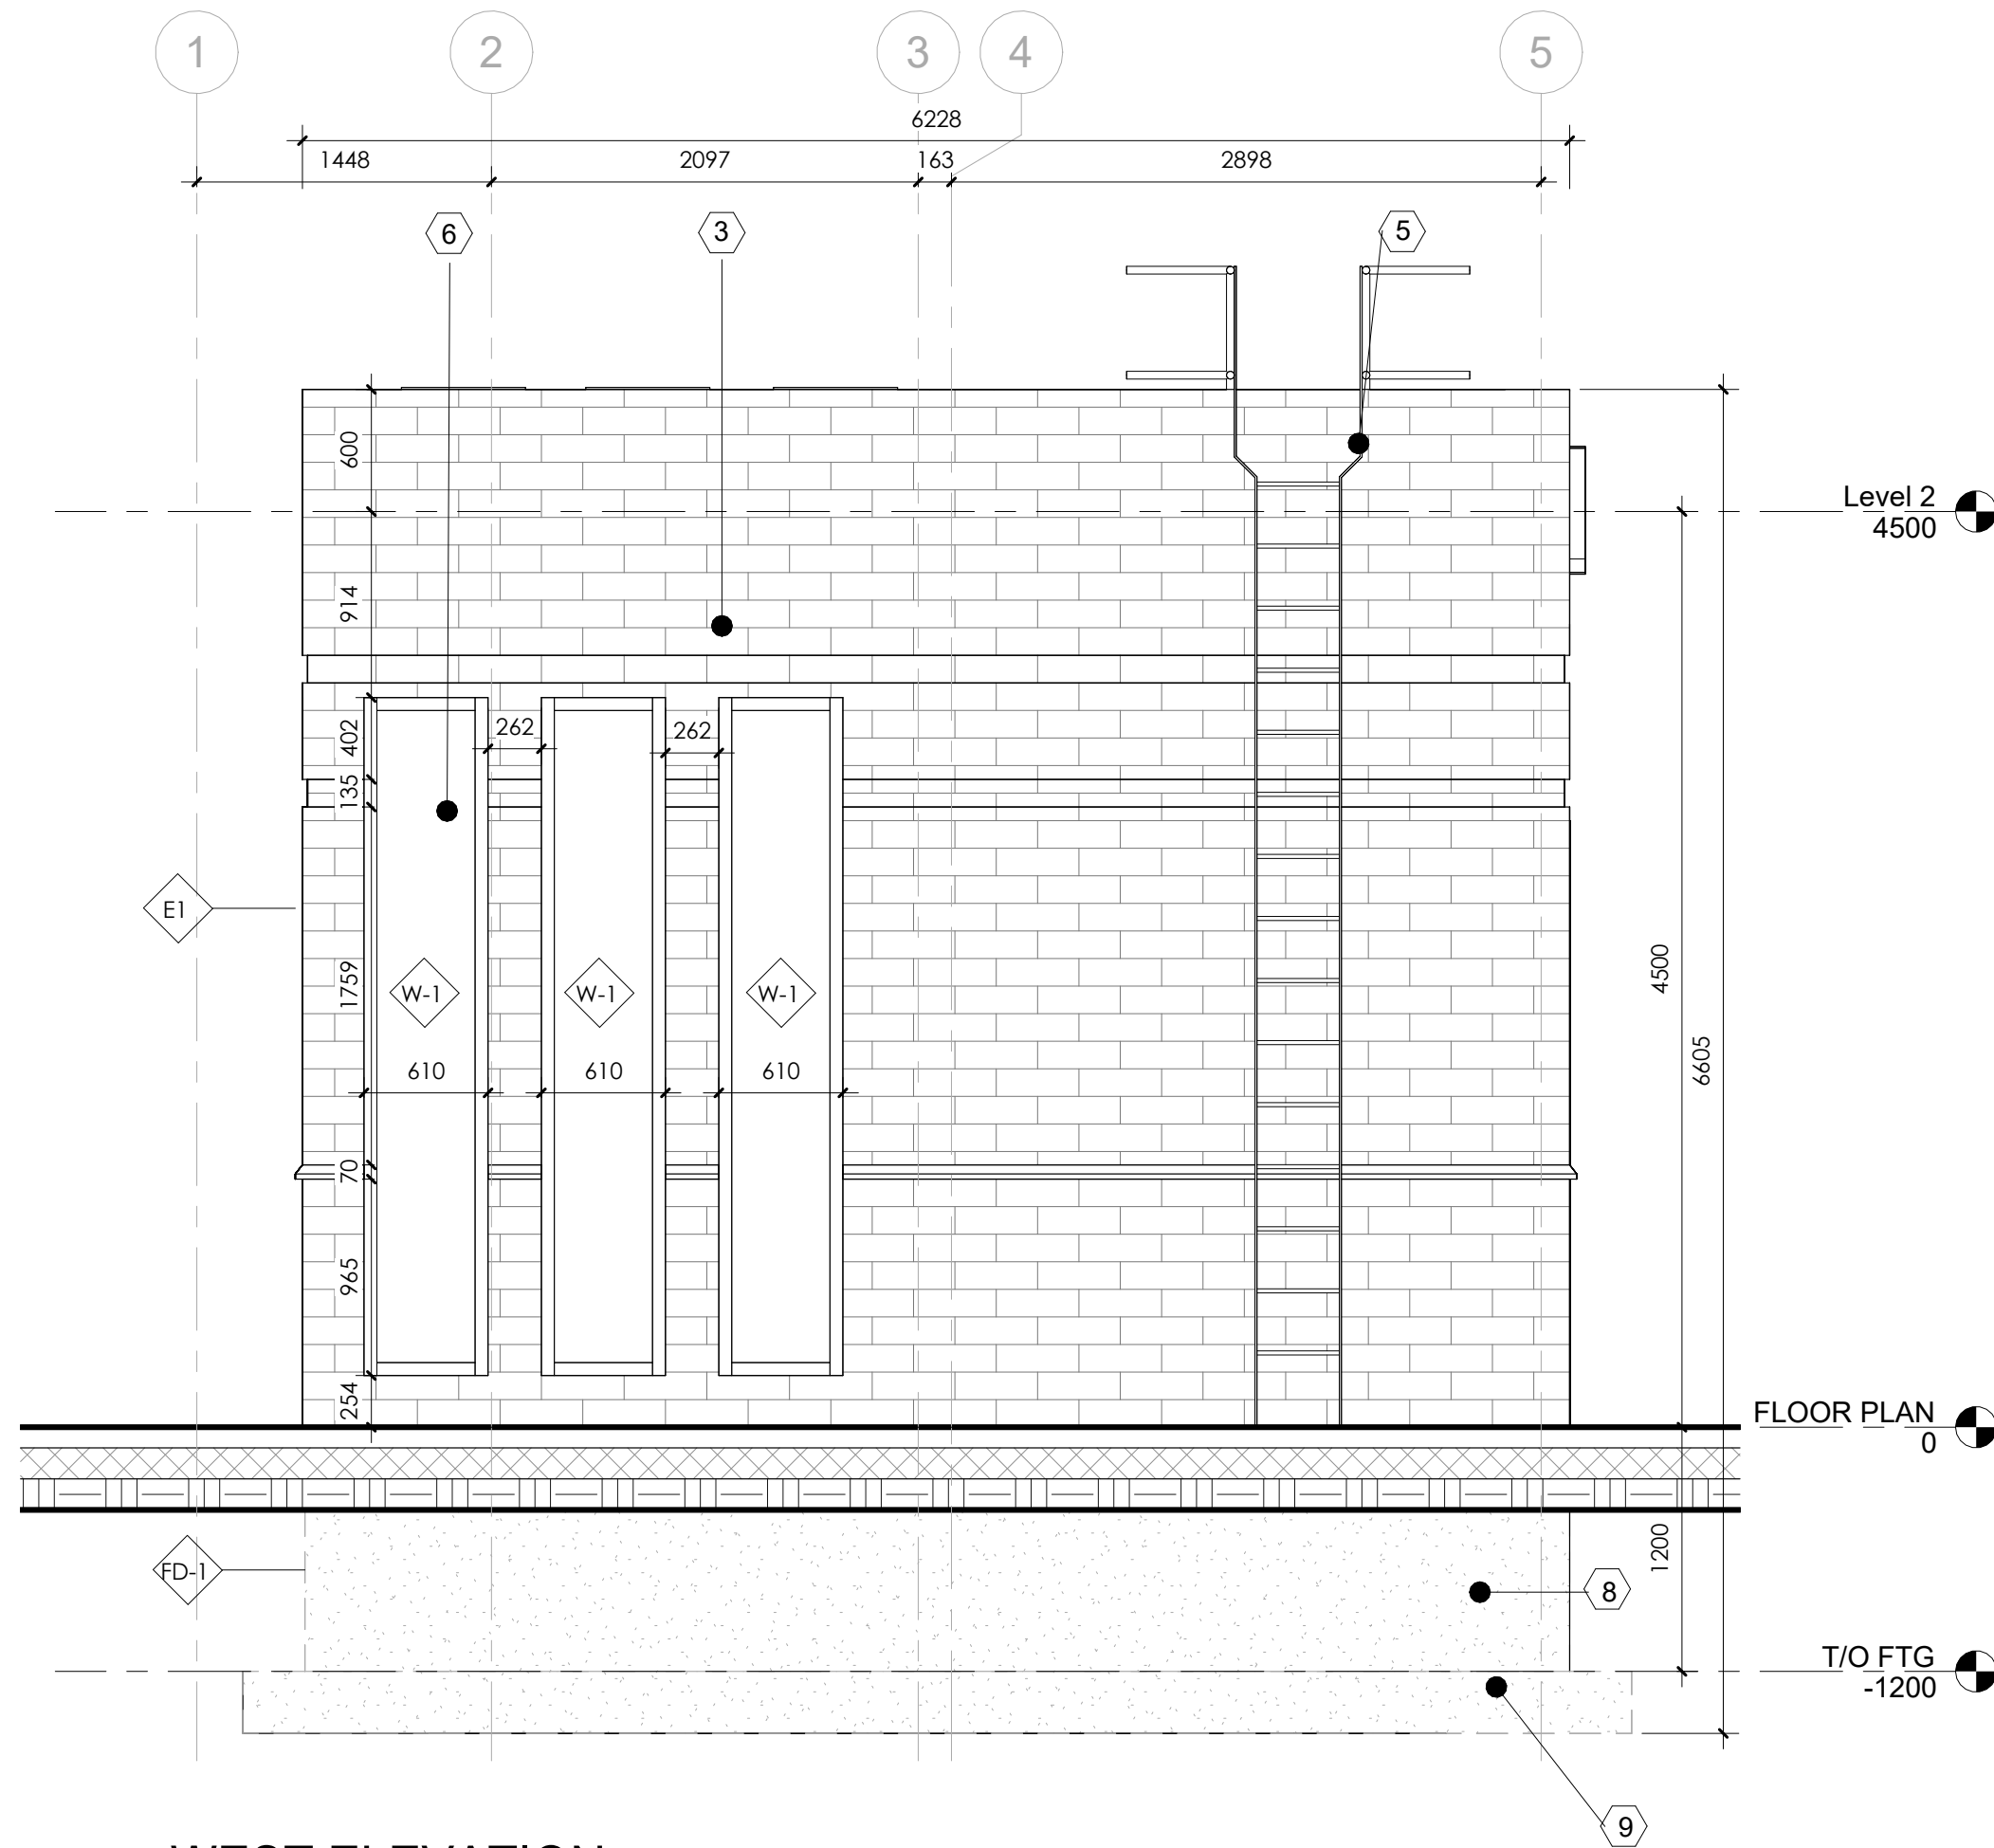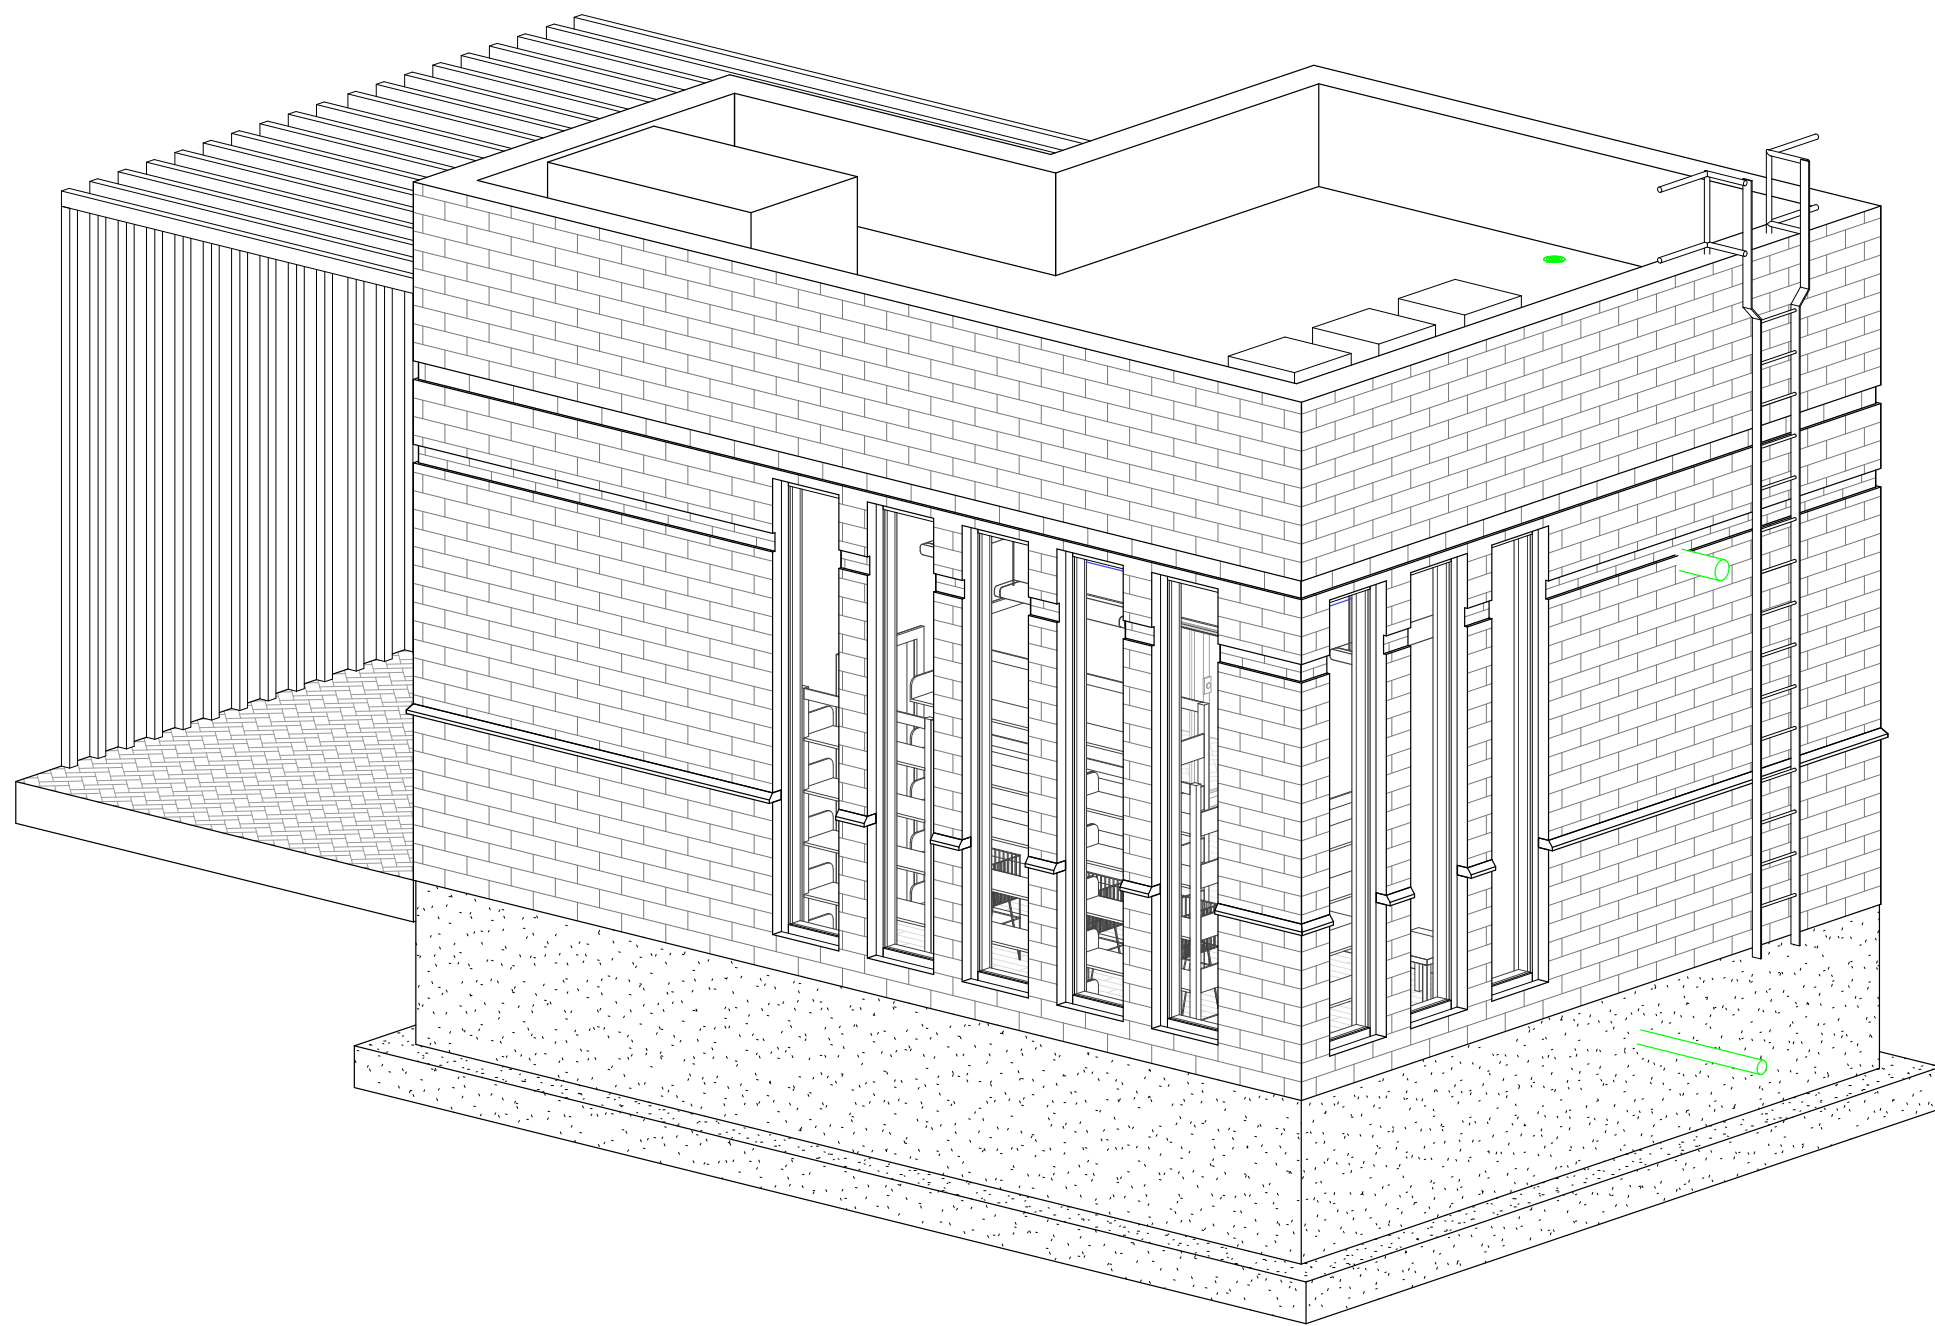

2 WEST ELEVATION
3/8" = 1'-0"

MATERIAL LEGEND

- 1 CURTAIN WALL FRAMING
CLEAR GLASS SEALED UNITS IN ALUMINUM CURTAIN WALL FRAMING.
PAINTED: BLACK
- 2 WOODEN PERGOLA: SUPPLIED AND INSTALLED BY A SPECIALIZED PERGOLA COMPANY, CONSTRUCTED
USING PRESSURE-TREATED TIMBER OR ENGINEERED WOOD SUITABLE FOR
EXTERIOR USE IN ONTARIO CLIMATE. FINISH TO BE WEATHER-RESISTANT STAIN OR PAINT AS SPECIFIED.
DIMENSIONS AND
CONNECTIONS TO BE AS PER APPROVED ARCHITECTURAL AND ENGINEERED DRAWINGS.
- 3 ARCHITECTURAL BRICK
FINISH CONTEMPORARY SERIES NUEVA COLLECTION BRICK BY BRAMPTON BRICK
COLOUR : AUBURN MATT
- 4 THERMALLY BROKEN DOUBLE GLAZED ALUMINUM WINDOW WITH OPERABLE PANES. FRAME TO BE PAINTED BLACK. REFER TO
MANUFACTURE SPECIFICATIONS
- 5 ROOF ACCESS LADDER. REFER TO MANUFACTURE SPECIFICATIONS
- 6 THERMALLY BROKEN DOUBLE GLAZED ALUMINUM FIXED WINDOW. FRAME TO BE
PAINTED BLACK. REFER TO MANUFACTURE SPECIFICATIONS
- 7 ALUMINIUM FRAMED GLAZED DOUBLE DOOR. FRAMES PAINTED
BLACK. REFER TO MANUFACTURE SPECIFICATIONS.
- 8 12" CAST IN PLACE CONCRETE FOUNDATION W/ KEYWAY
REFER TO STRUCTURE DRAWINGS.
- 9 36x12" CAST IN PLACE CONCRETE STRIP FOOTING
REFER TO STRUCTURE DRAWINGS.

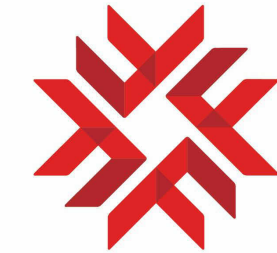

FANSHAWE
DONALD J. SMITH
SCHOOL OF BUILDING
TECHNOLOGY

NORTH ARROW



GENERAL NOTES:-

1. DO NOT SCALE DRAWINGS. WRITTEN DIMENSIONS SHALL HAVE PRECEDENCE OVER SCALED DIMENSIONS.
2. ALL WORK SHALL COMPLY WITH THE 2012 ONTARIO BUILDING CODE AND AMENDMENTS.
3. CONTRACTORS MUST CHECK AND VERIFY ALL DIMENSIONS AND SPECIFICATIONS AND REPORT ANY DISCREPANCIES TO THE ARCHITECT BEFORE PROCEEDING WITH THE WORK.
4. ALL CONTRACTORS AND SUB-CONTRACTORS SHALL HAVE A SET OF APPROVED CONSTRUCTION DOCUMENTS ON SITE AT ALL TIMES.
5. ALL DOCUMENTS REMAIN THE PROPERTY OF THE ARCHITECT. UNAUTHORIZED USE, MODIFICATION, AND/OR REPRODUCTION OF THESE DOCUMENTS IS PROHIBITED WITHOUT WRITTEN PERMISSION. THE CONTRACT DOCUMENTS WERE PREPARED BY THE CONSULTANT FOR THE ACCOUNT OF THE OWNER.
6. THE MATERIAL CONTAINED HEREIN REFLECTS THE CONSULTANTS BEST JUDGMENT IN LIGHT OF THE INFORMATION AVAILABLE TO HIM/HER AT THE TIME OF PREPARATION. ANY USE WHICH A THIRD PARTY MAKES OF THE CONTRACT DOCUMENTS, OR ANY RELIANCE ON/OR DECISIONS TO BE MADE BASED ON THEM ARE THE RESPONSIBILITY OF SUCH THIRD PARTIES.
7. THE CONSULTANT ACCEPTS NO RESPONSIBILITY FOR DAMAGES, IF ANY, SUFFERED BY ANY THIRD PARTY AS A RESULT OF DECISIONS MADE OR ACTIONS BASED ON THE CONTRACT DOCUMENTS

PRELIMINARY
NOT FOR CONSTRUCTION

PROJECT TITLE
DOODLE



CLIENT:
FANSHAWE COLLEGE
PROJECT ADDRESS
LONDON , ON

DRAWING TITLE
ELEVATIONS


CHECKED | DRAWN | DATE
JF | MP | 07/30/25

3002-25S
PROJECT No.


A201
DRAWING

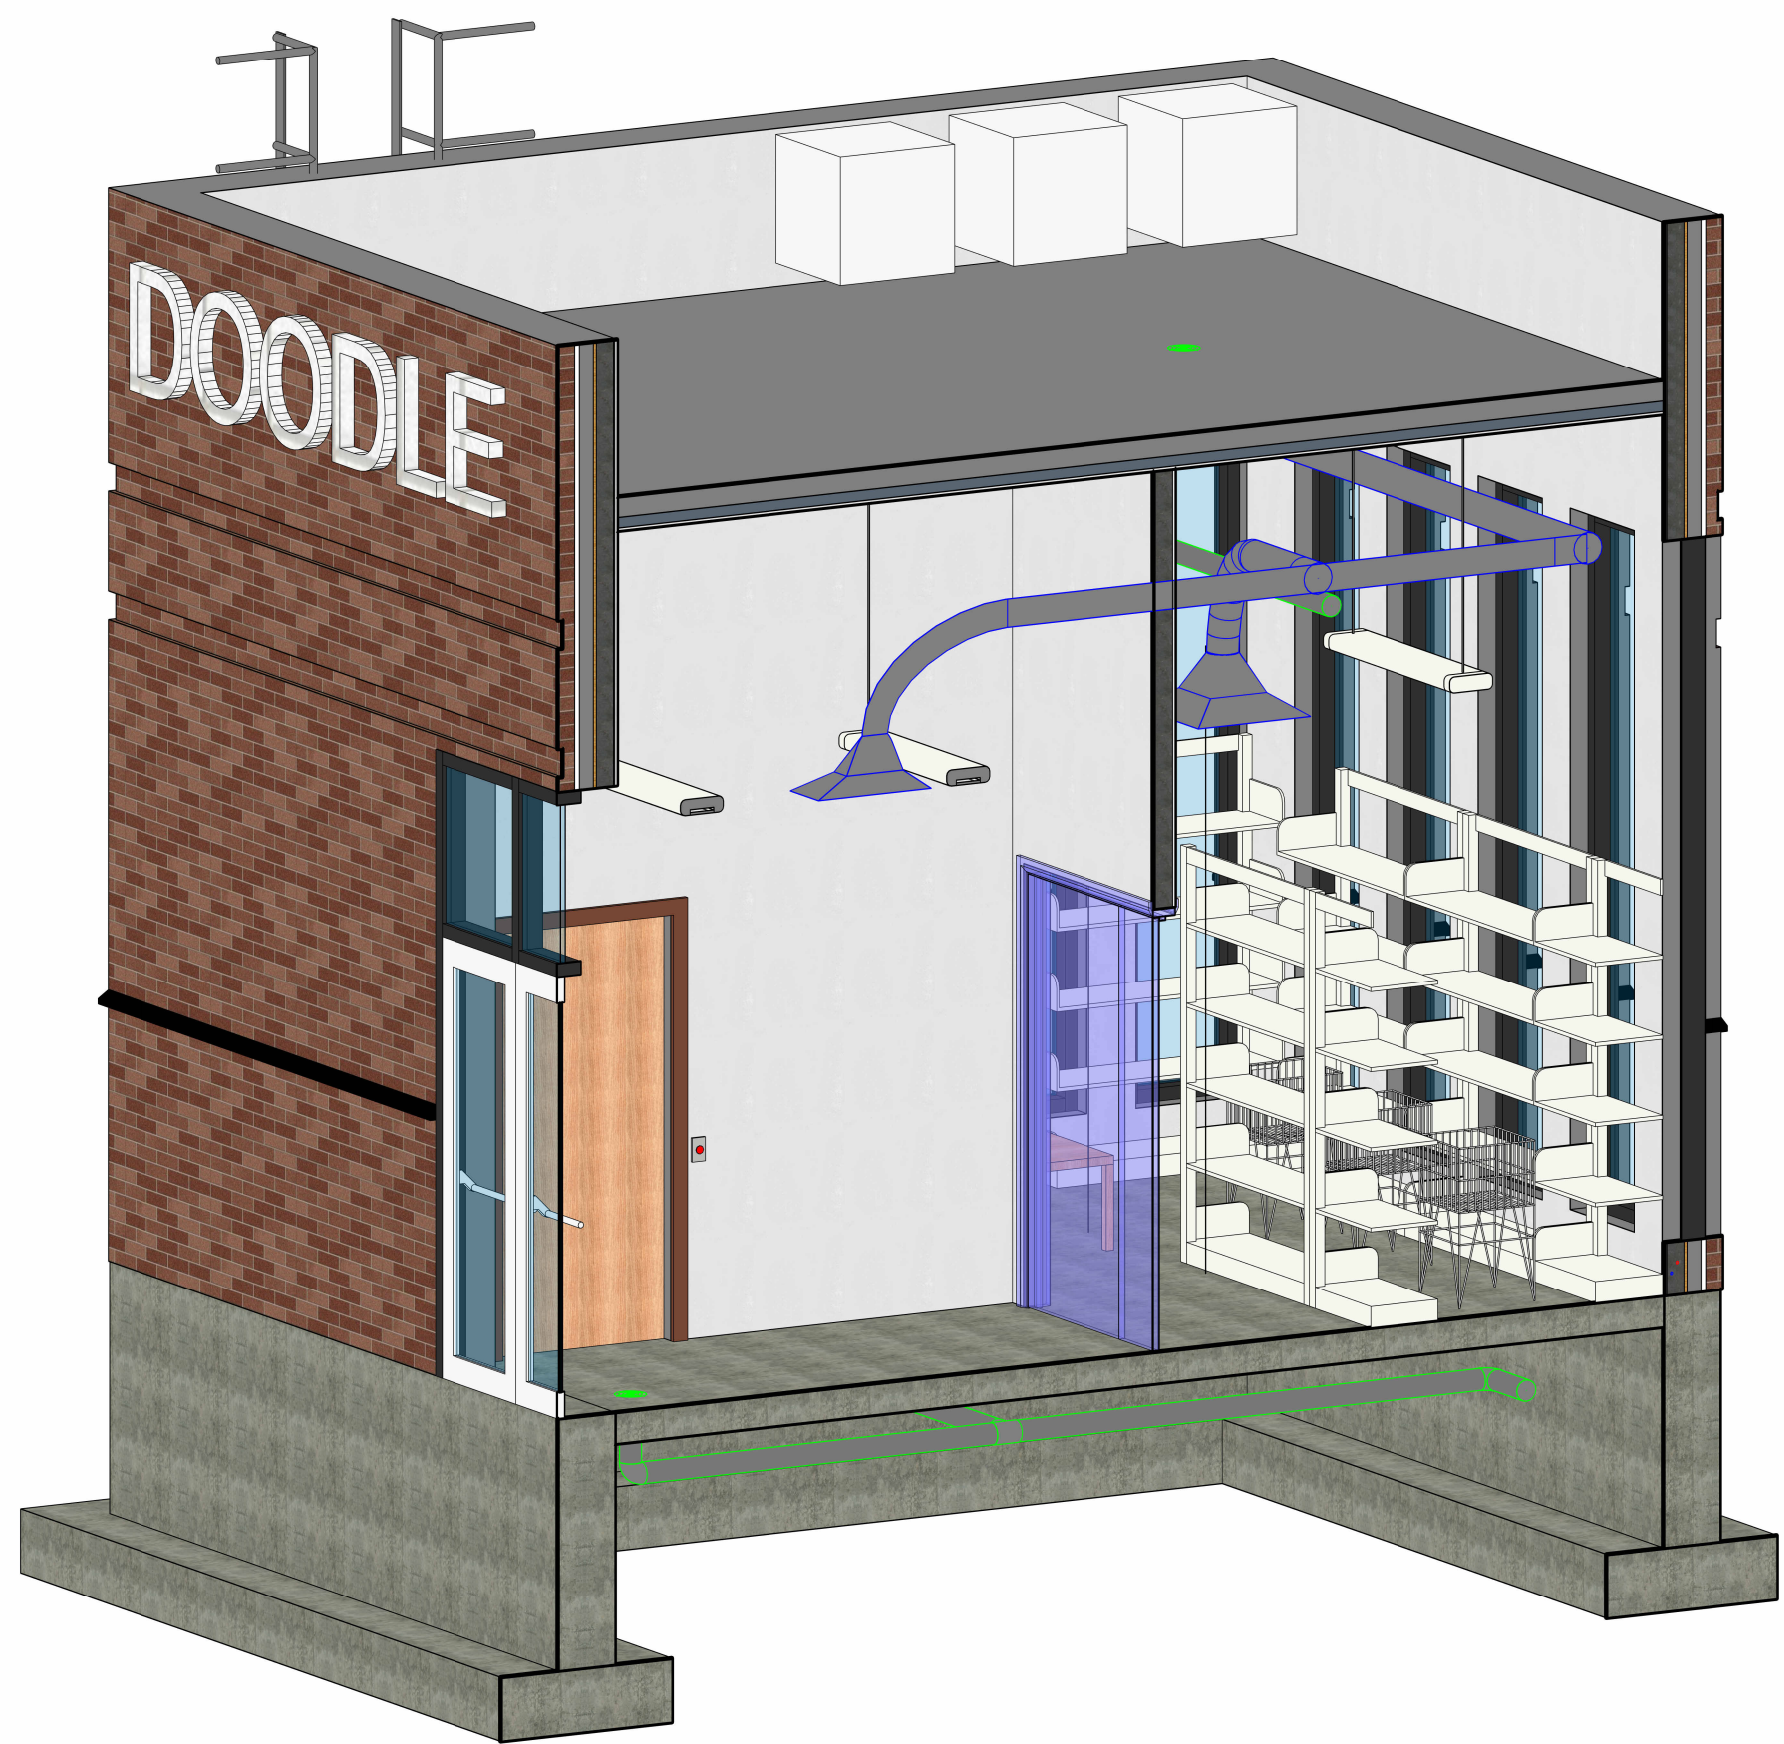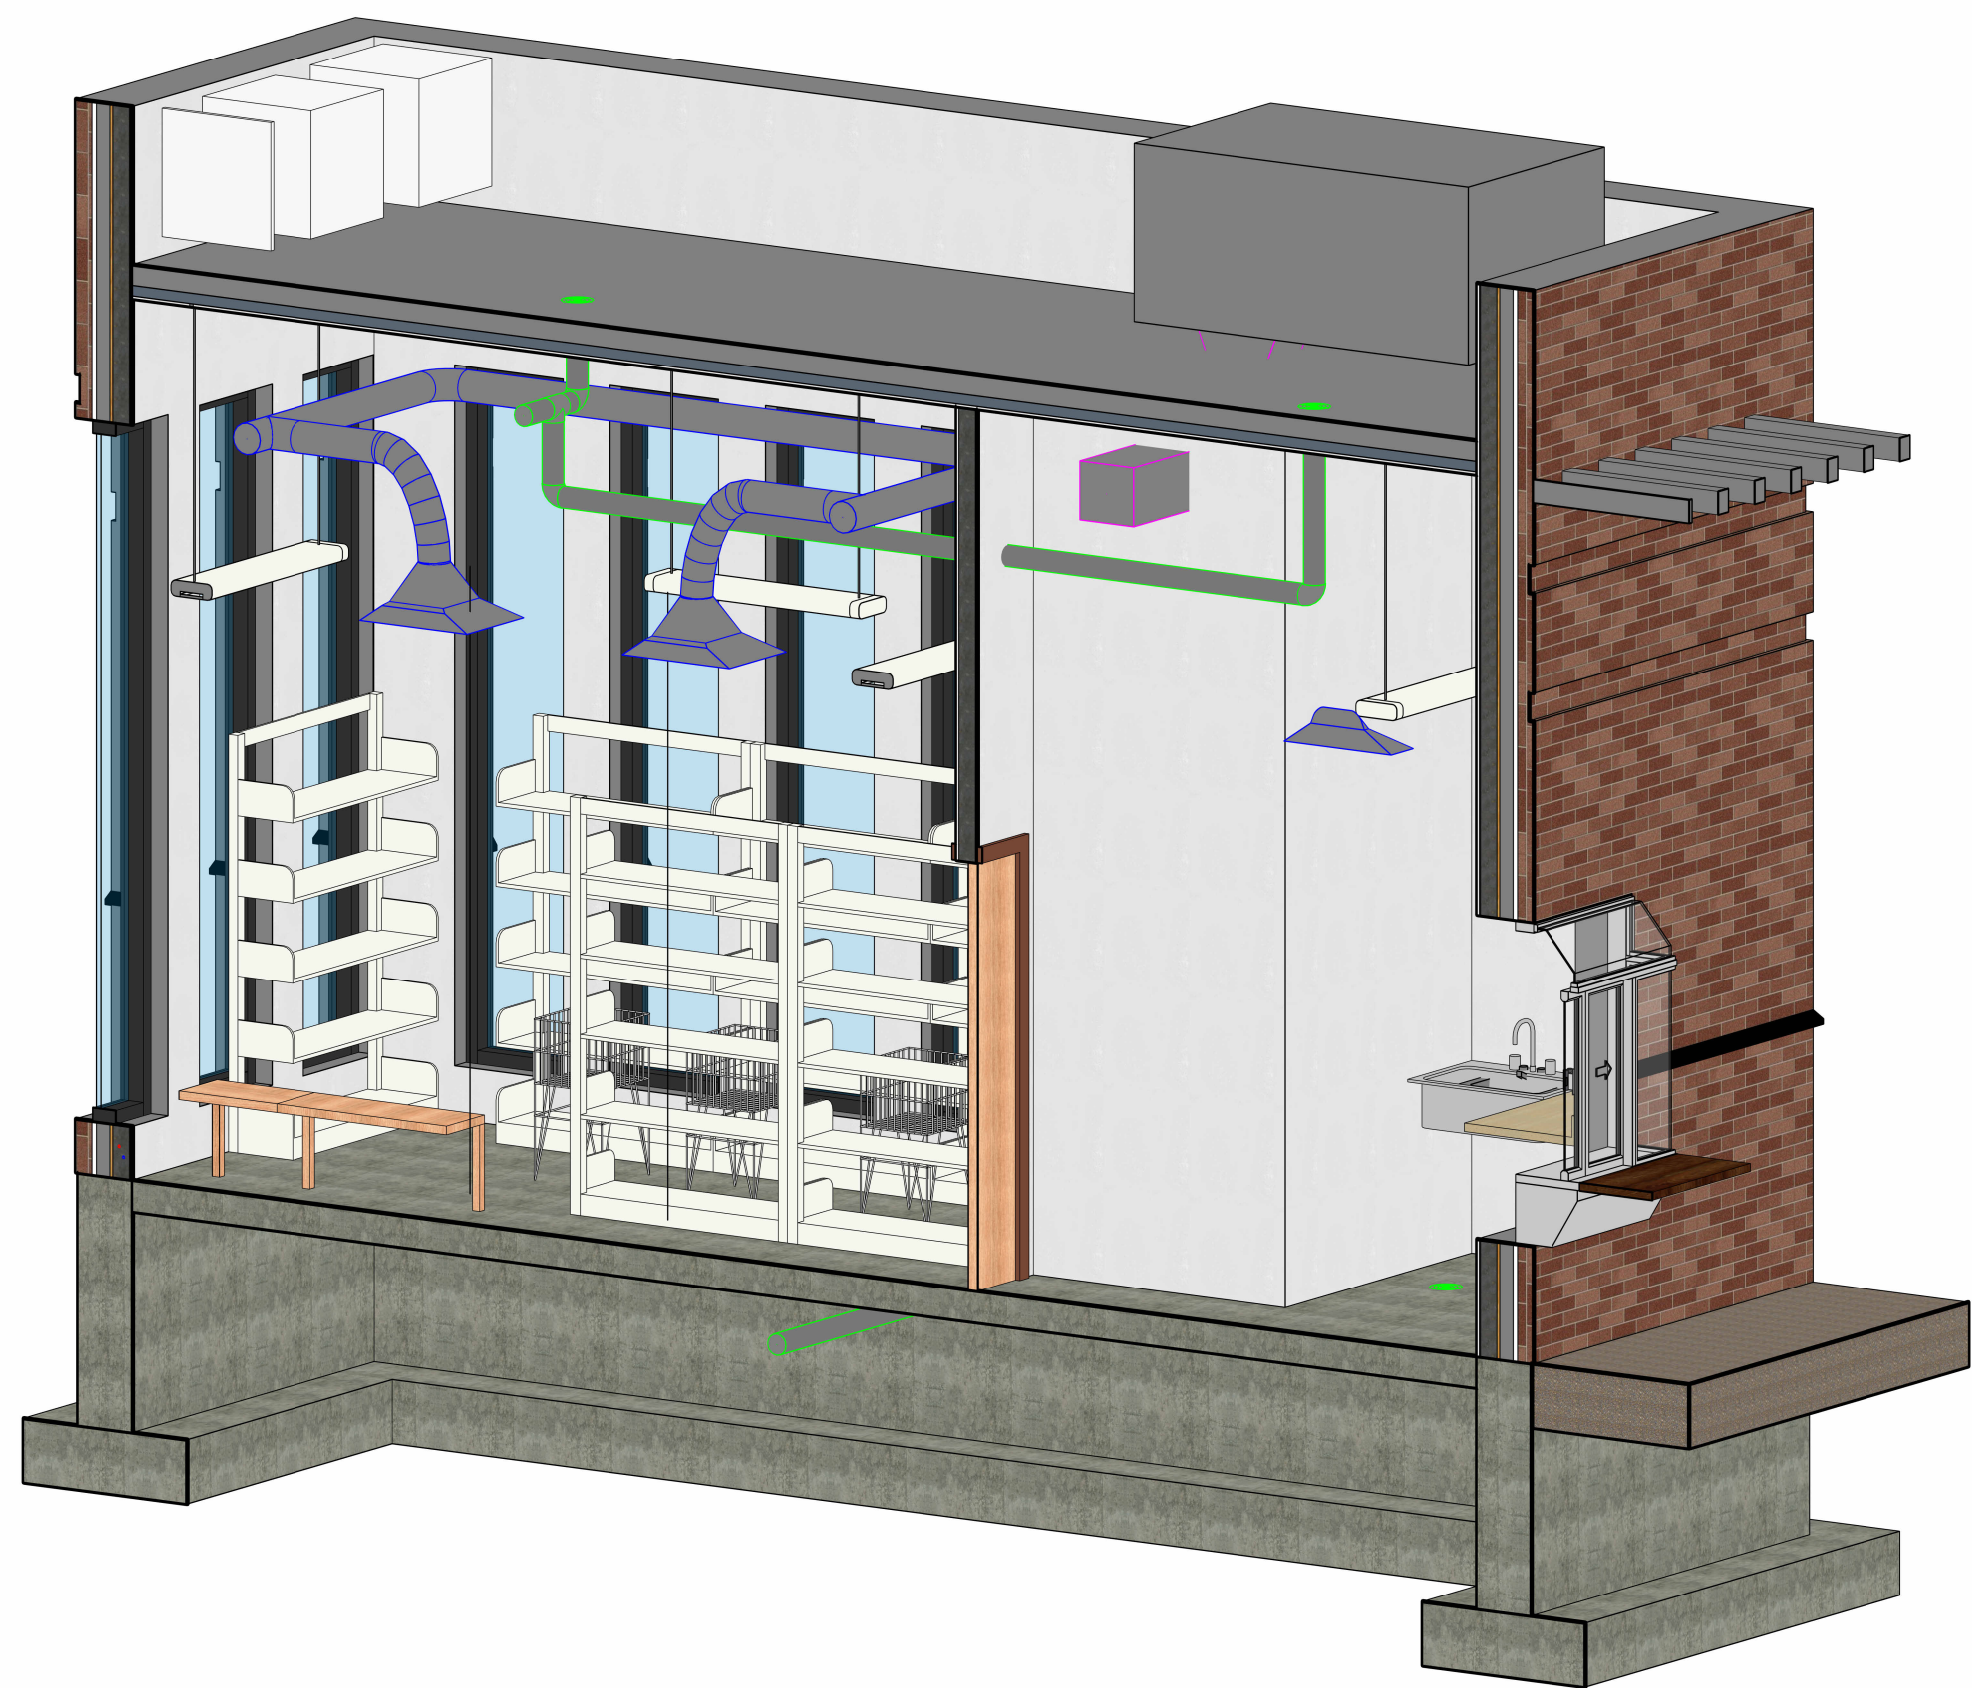

BUILDING SECTION 1
3/8" = 1'-0"

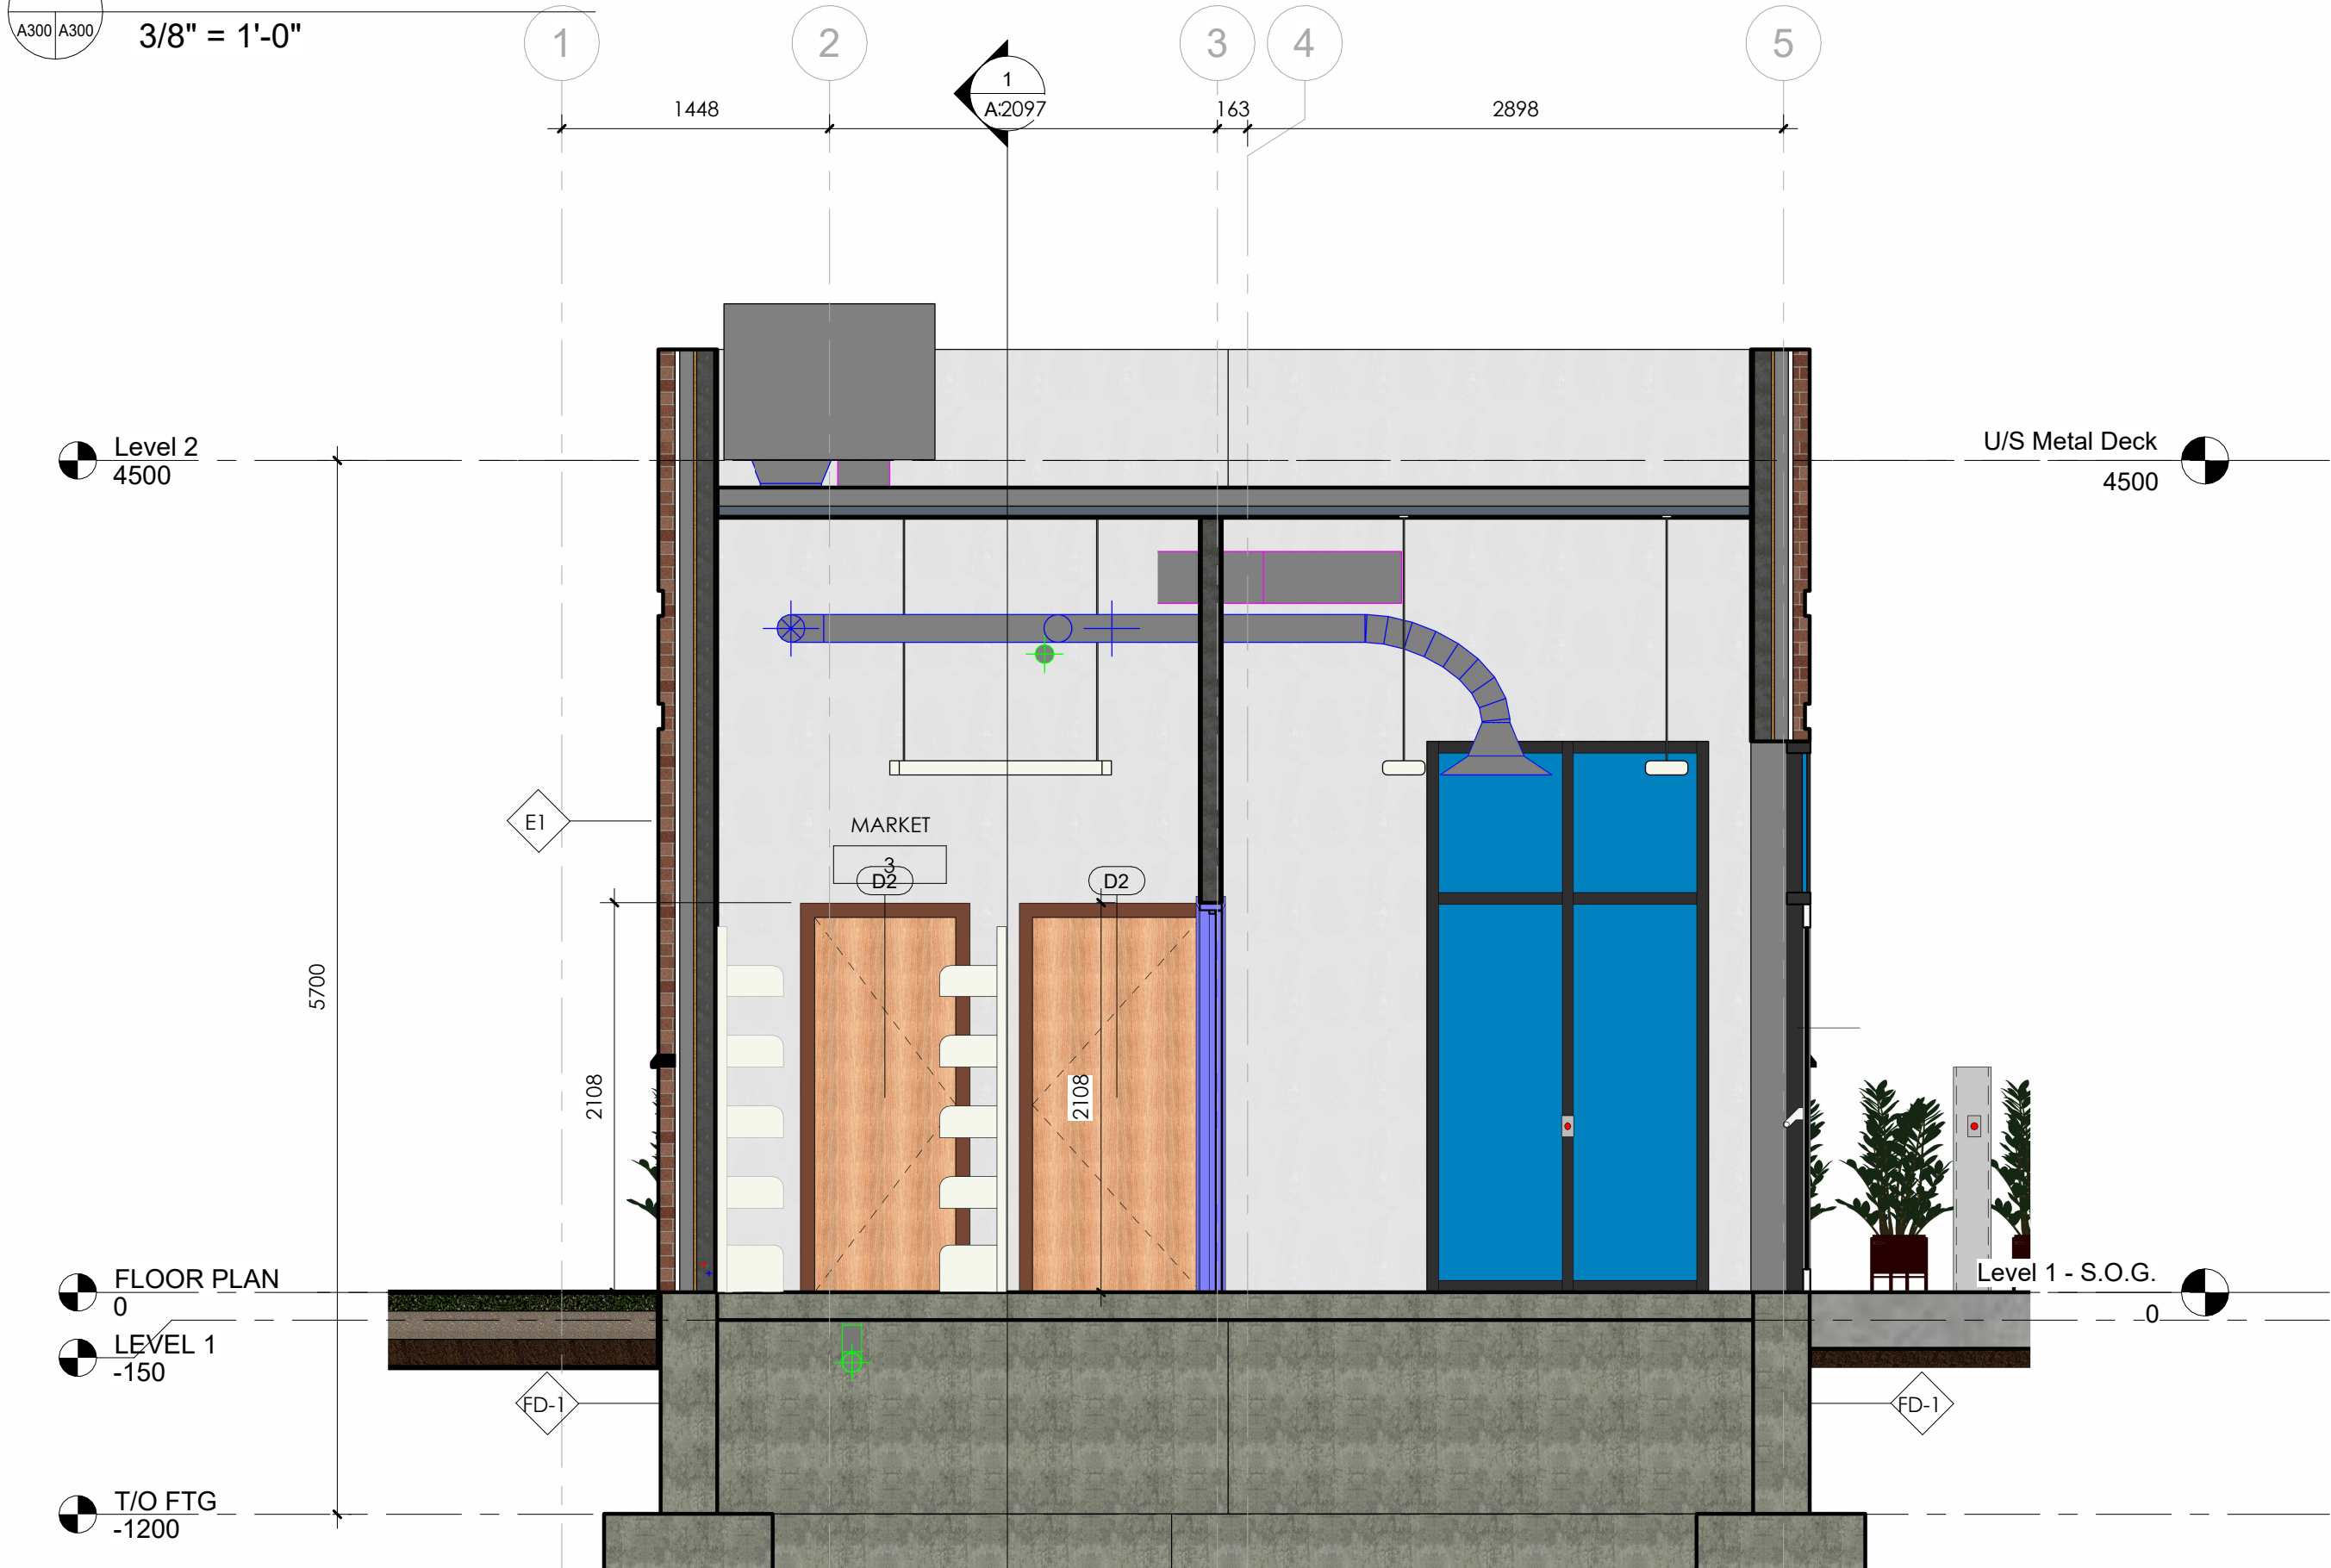

BUILDING SECTION 2
3/8" = 1'-0"

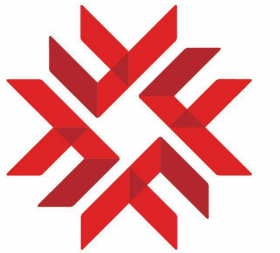

FANSHAWE
DONALD J. SMITH
SCHOOL OF BUILDING
TECHNOLOGY

NORTH ARROW



GENERAL NOTES:-

1. DO NOT SCALE DRAWINGS. WRITTEN DIMENSIONS SHALL HAVE PRECEDENCE OVER SCALED DIMENSIONS.
2. ALL WORK SHALL COMPLY WITH THE 2012 ONTARIO BUILDING CODE AND AMENDMENTS.
3. CONTRACTORS MUST CHECK AND VERIFY ALL DIMENSIONS AND SPECIFICATIONS AND REPORT ANY DISCREPANCIES TO THE ARCHITECT BEFORE PROCEEDING WITH THE WORK.
4. ALL CONTRACTORS AND SUB-CONTRACTORS SHALL HAVE A SET OF APPROVED CONSTRUCTION DOCUMENTS ON SITE AT ALL TIMES.
5. ALL DOCUMENTS REMAIN THE PROPERTY OF THE ARCHITECT. UNAUTHORIZED USE, MODIFICATION, AND/OR REPRODUCTION OF THESE DOCUMENTS IS PROHIBITED WITHOUT WRITTEN PERMISSION. THE CONTRACT DOCUMENTS WERE PREPARED BY THE CONSULTANT FOR THE ACCOUNT OF THE OWNER.
6. THE MATERIAL CONTAINED HEREIN REFLECTS THE CONSULTANT'S BEST JUDGMENT IN LIGHT OF THE INFORMATION AVAILABLE TO HIM/HER AT THE TIME OF PREPARATION. ANY USE WHICH A THIRD PARTY MAKES OF THE CONTRACT DOCUMENTS, OR ANY RELIANCE ON/OR DECISIONS TO BE MADE BASED ON THEM ARE THE RESPONSIBILITY OF SUCH THIRD PARTIES.
7. THE CONSULTANT ACCEPTS NO RESPONSIBILITY FOR DAMAGES, IF ANY, SUFFERED BY ANY THIRD PARTY AS A RESULT OF DECISIONS MADE OR ACTIONS BASED ON THE CONTRACT DOCUMENTS

PRELIMINARY
NOT FOR CONSTRUCTION


PROJECT TITLE
DOODLE

CLIENT:
FANSHAWE COLLEGE
PROJECT ADDRESS
LONDON , ON


DRAWING TITLE
SECTION

CHECKED | DRAWN | DATE
JF | MP | 07/30/25


3002-25S | **A300**
PROJECT No. | DRAWING

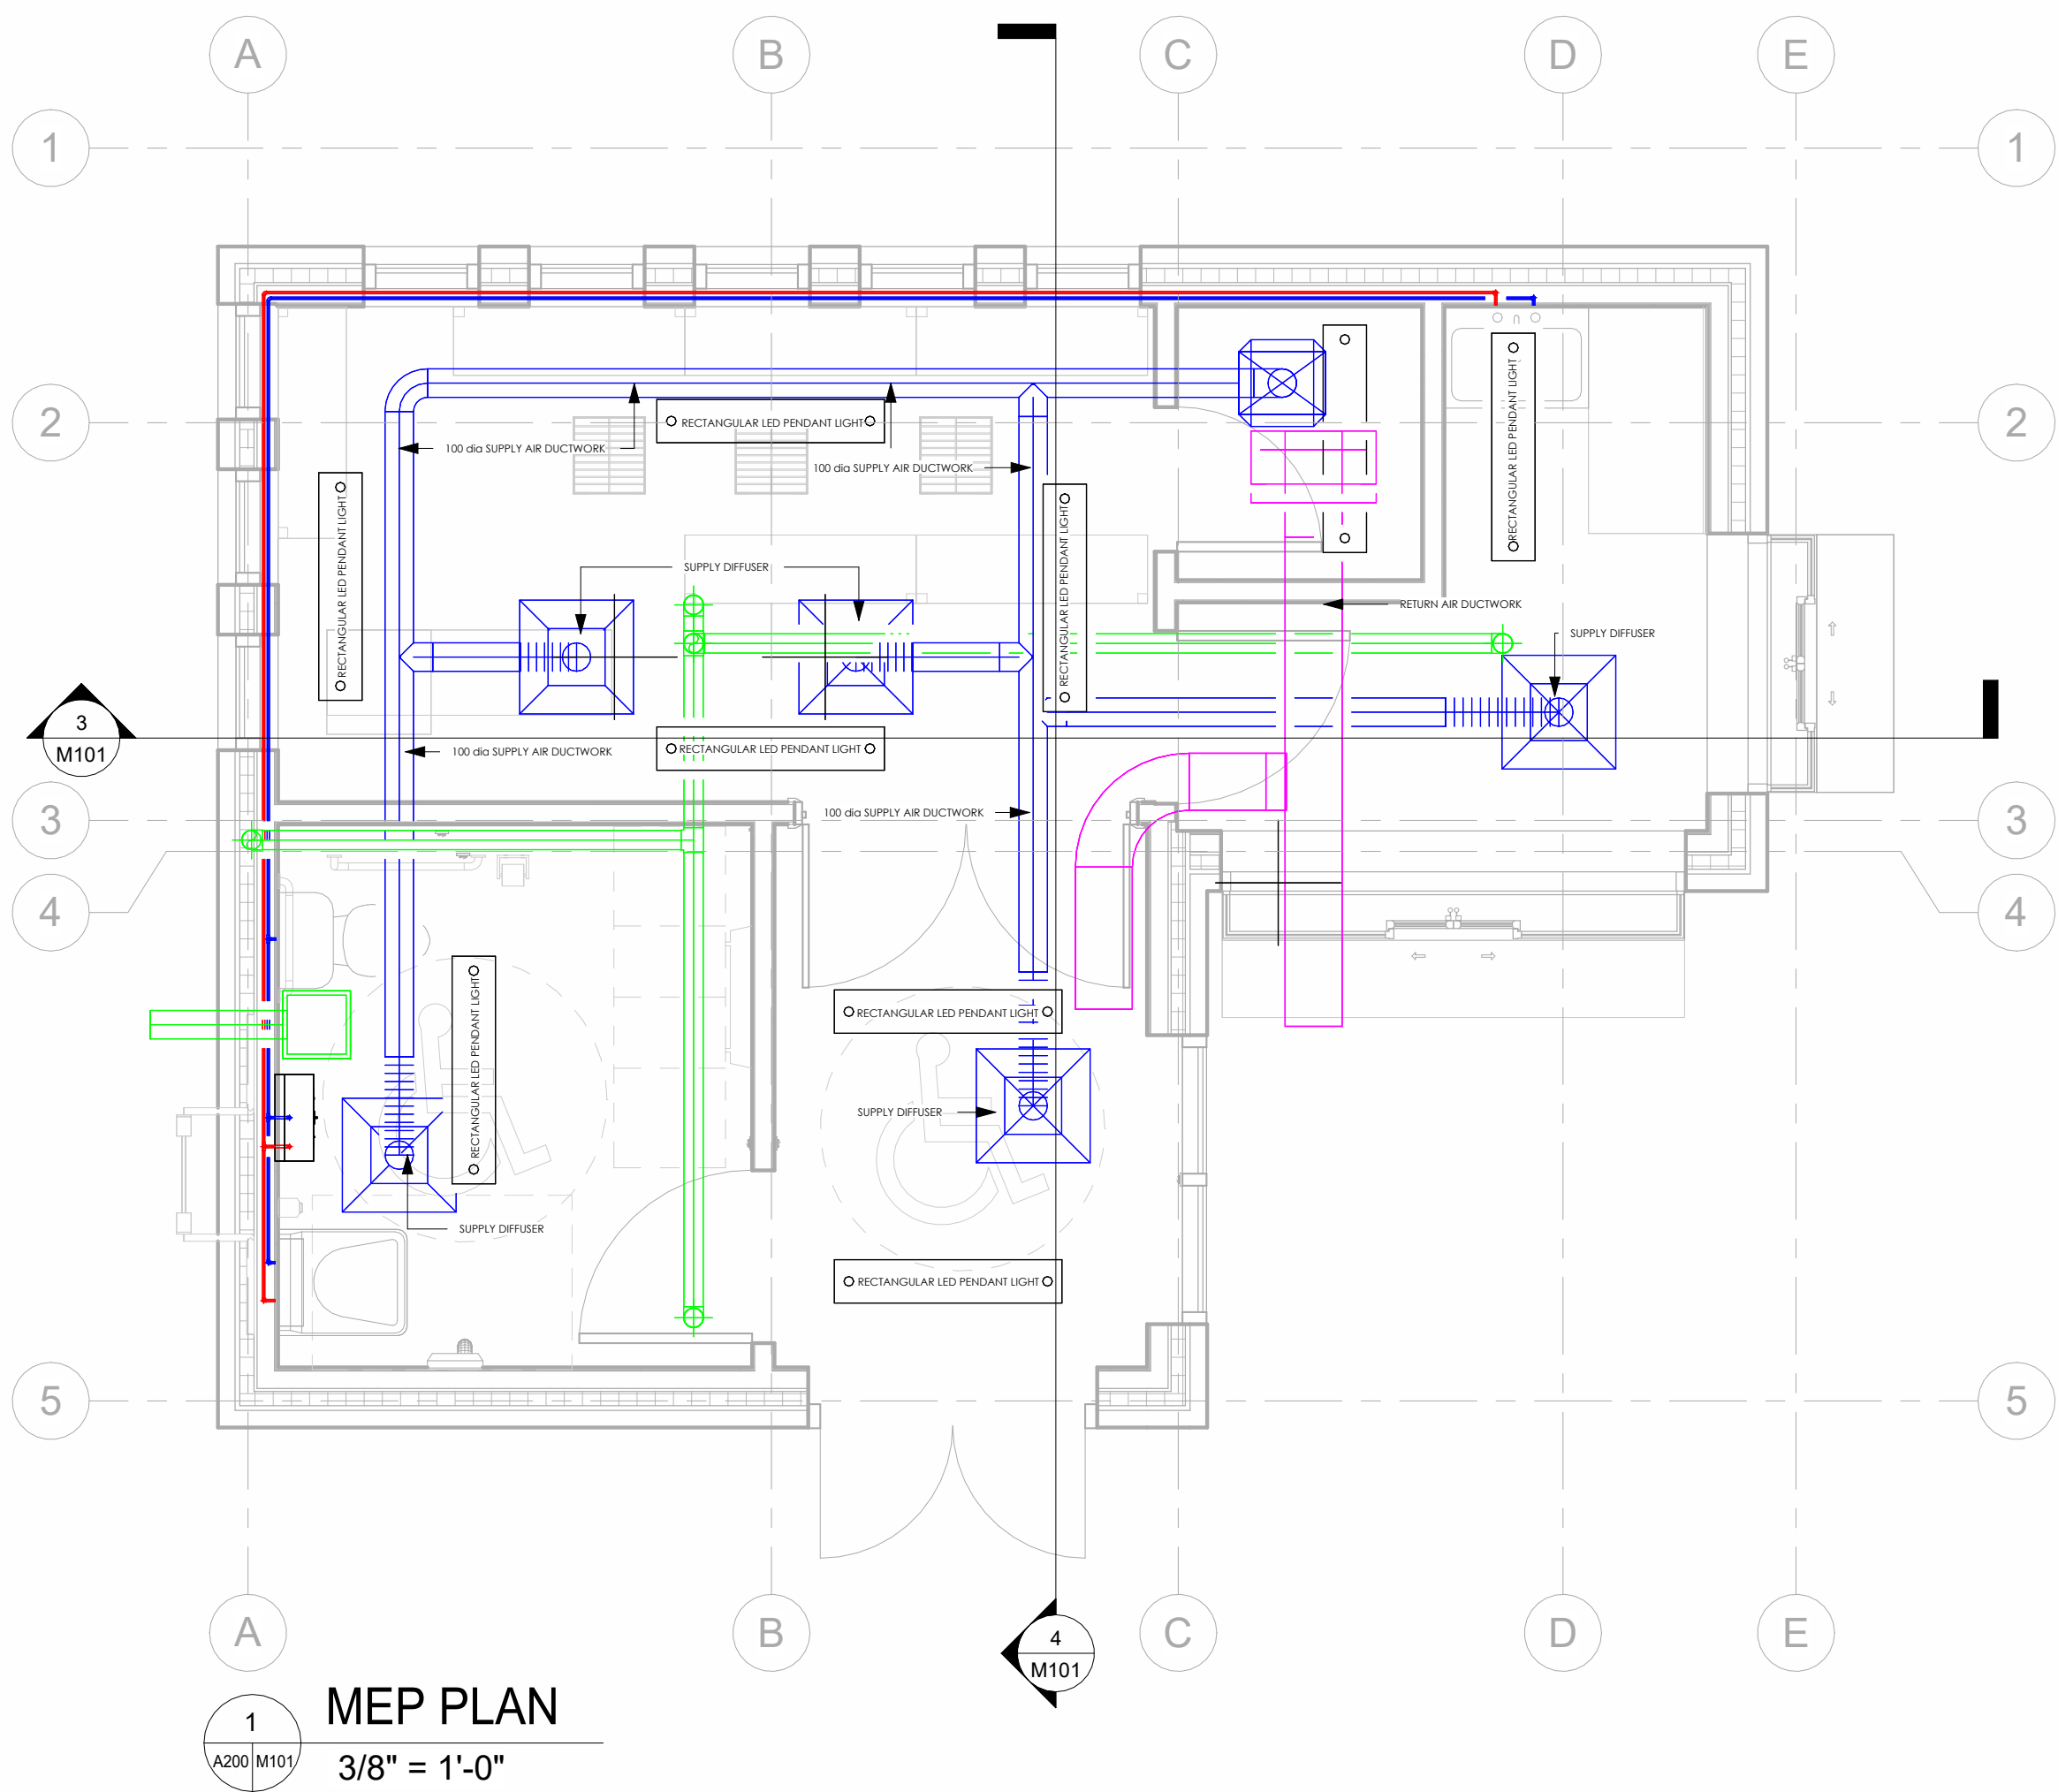

MEP PLAN
3/8" = 1'-0"

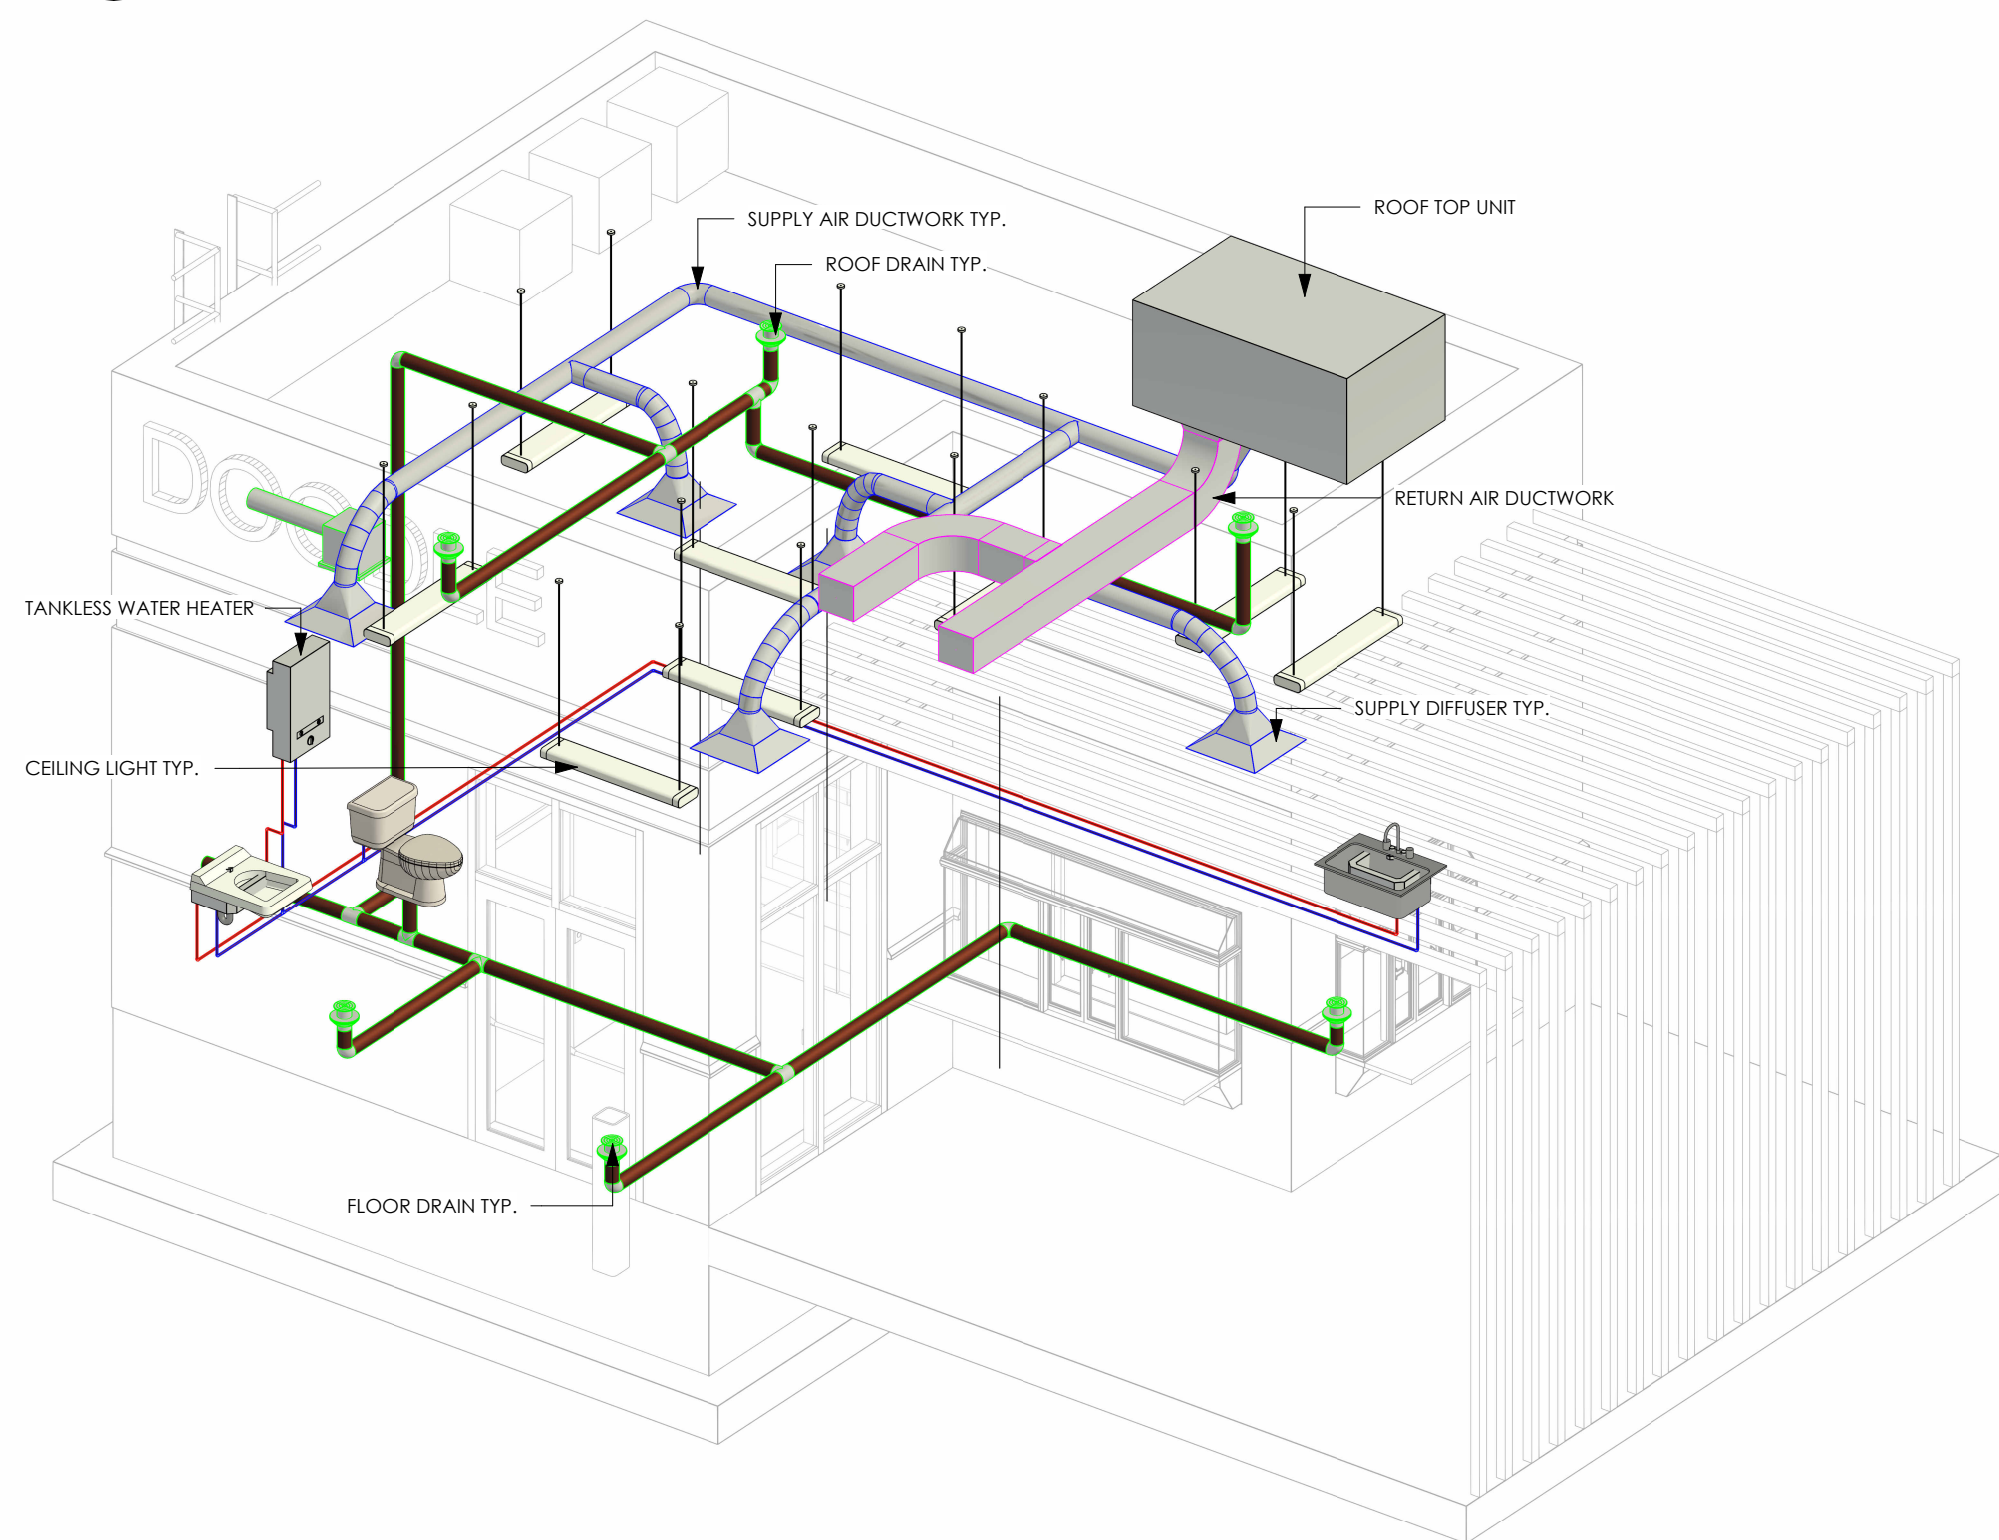


3D MEP

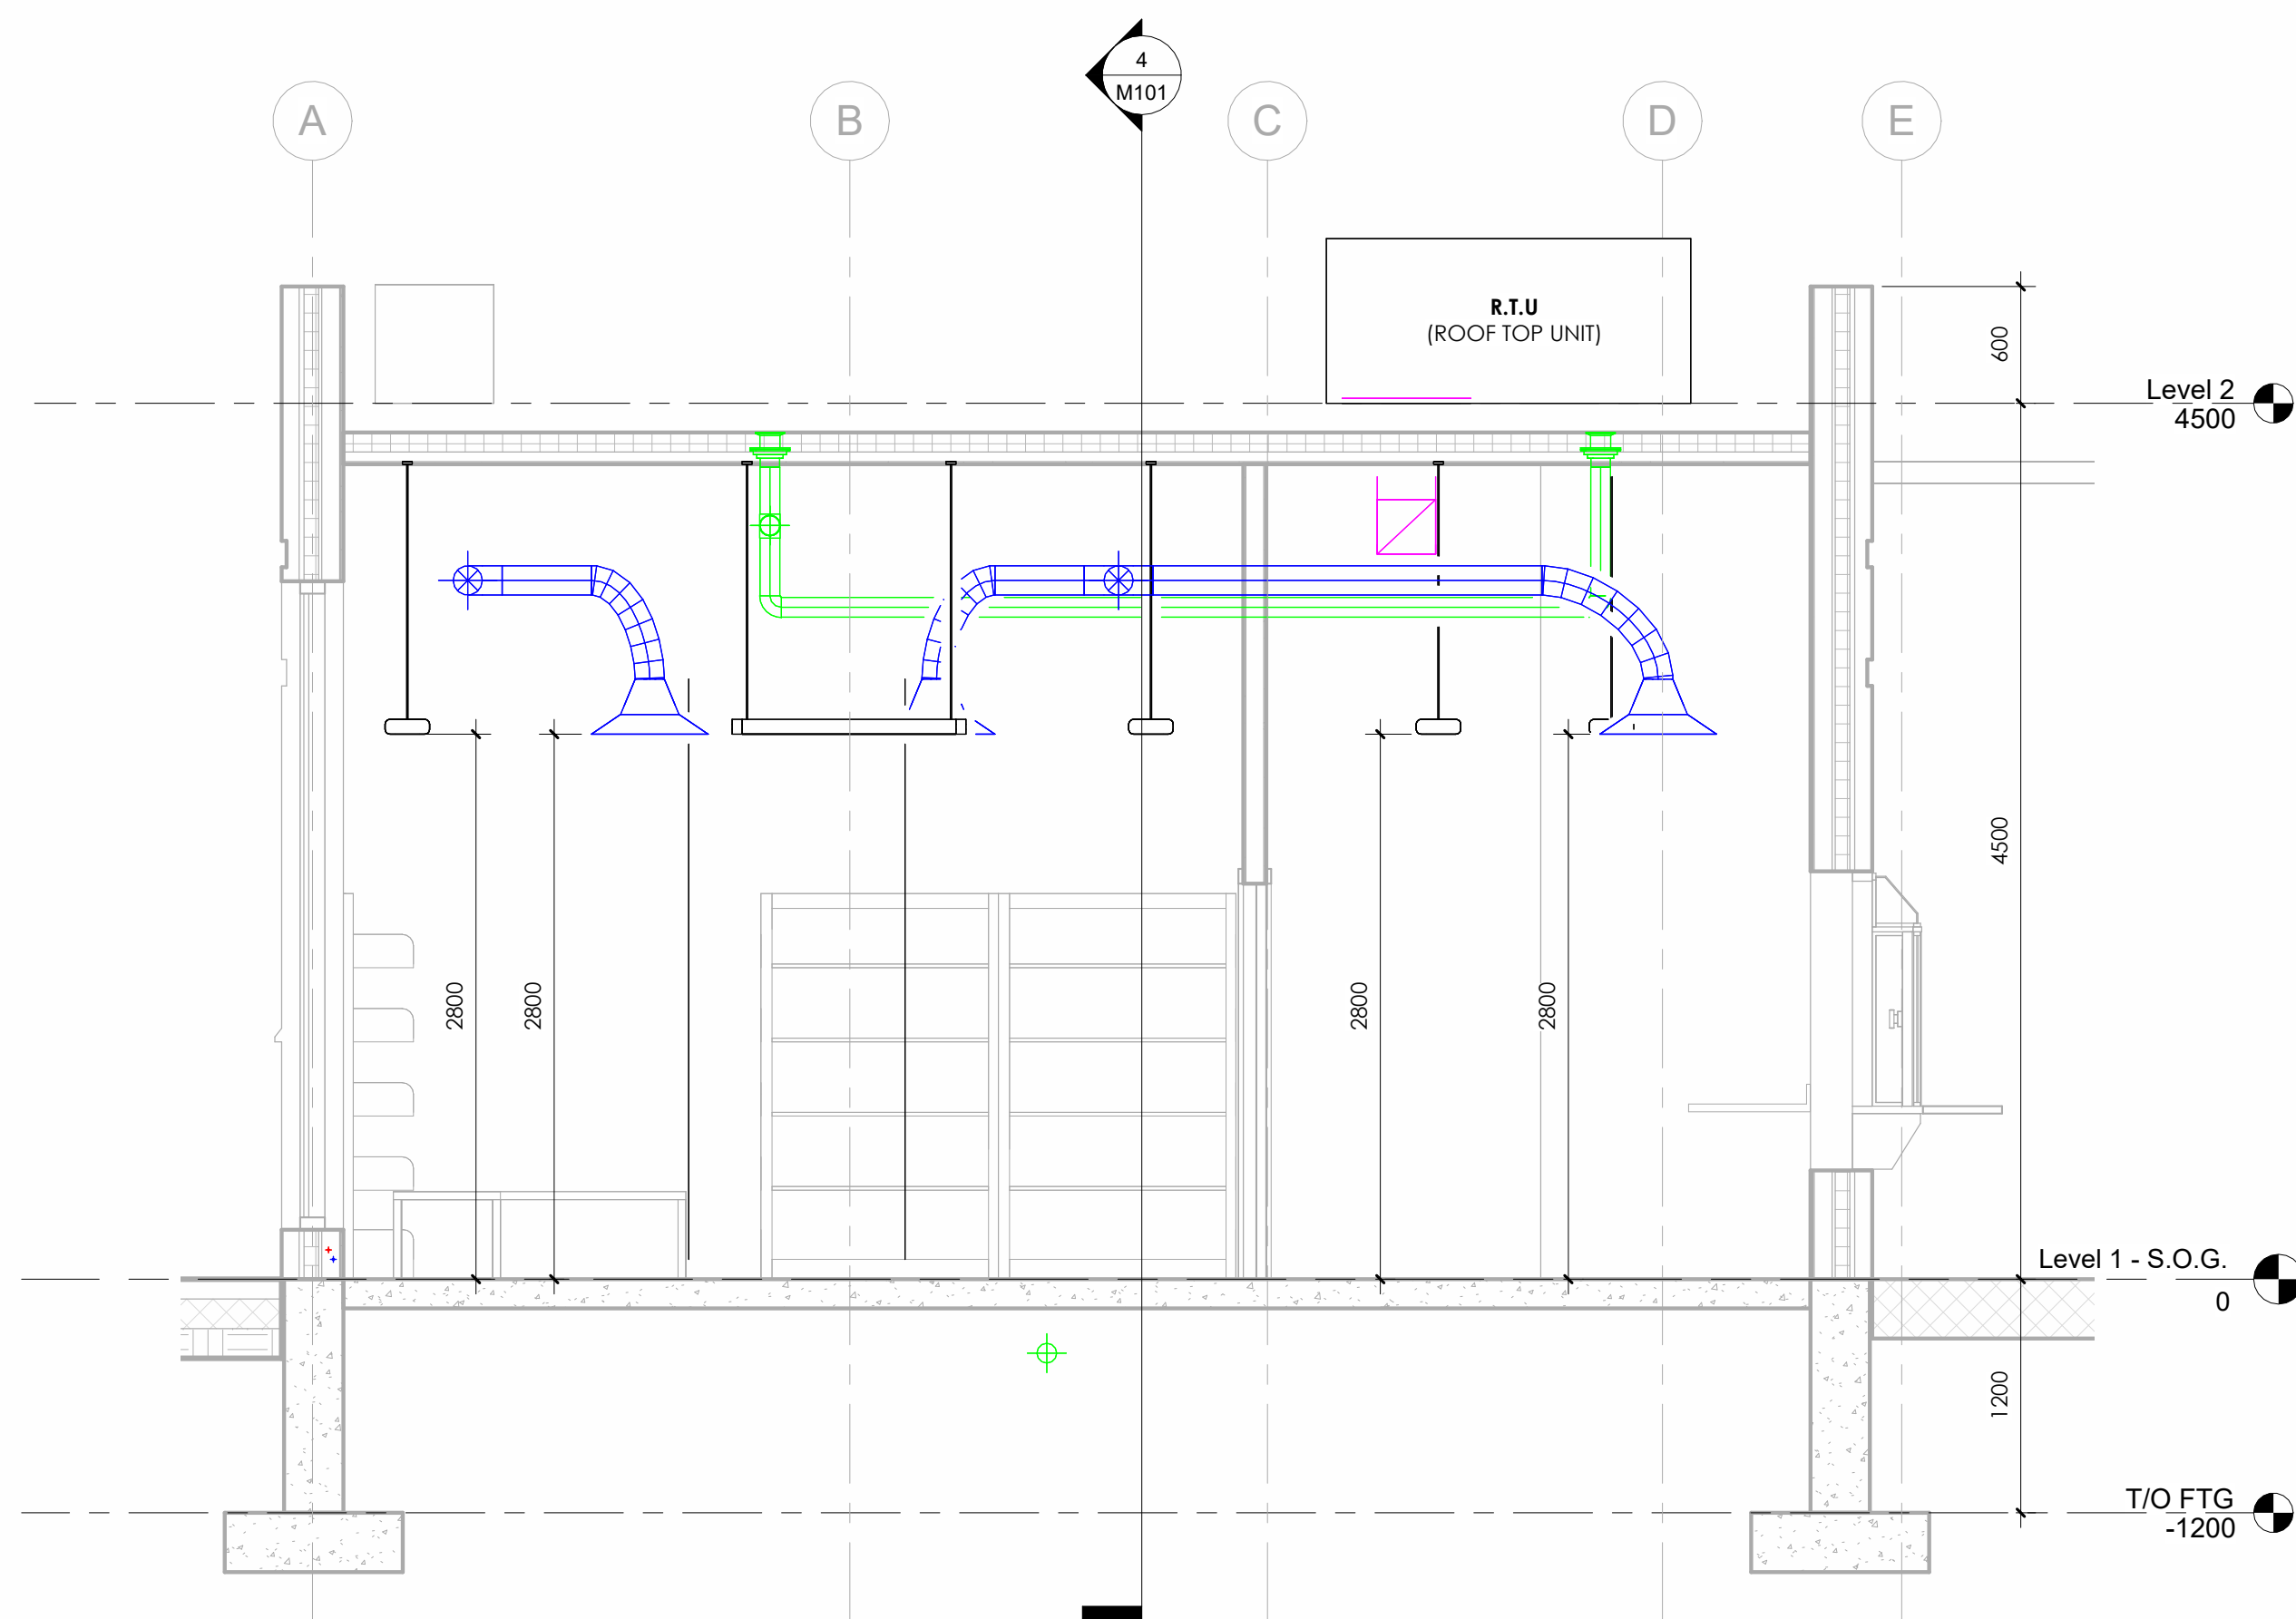


SYSTEMS M.E.P. SECTION 1

3/8" = 1'-0"

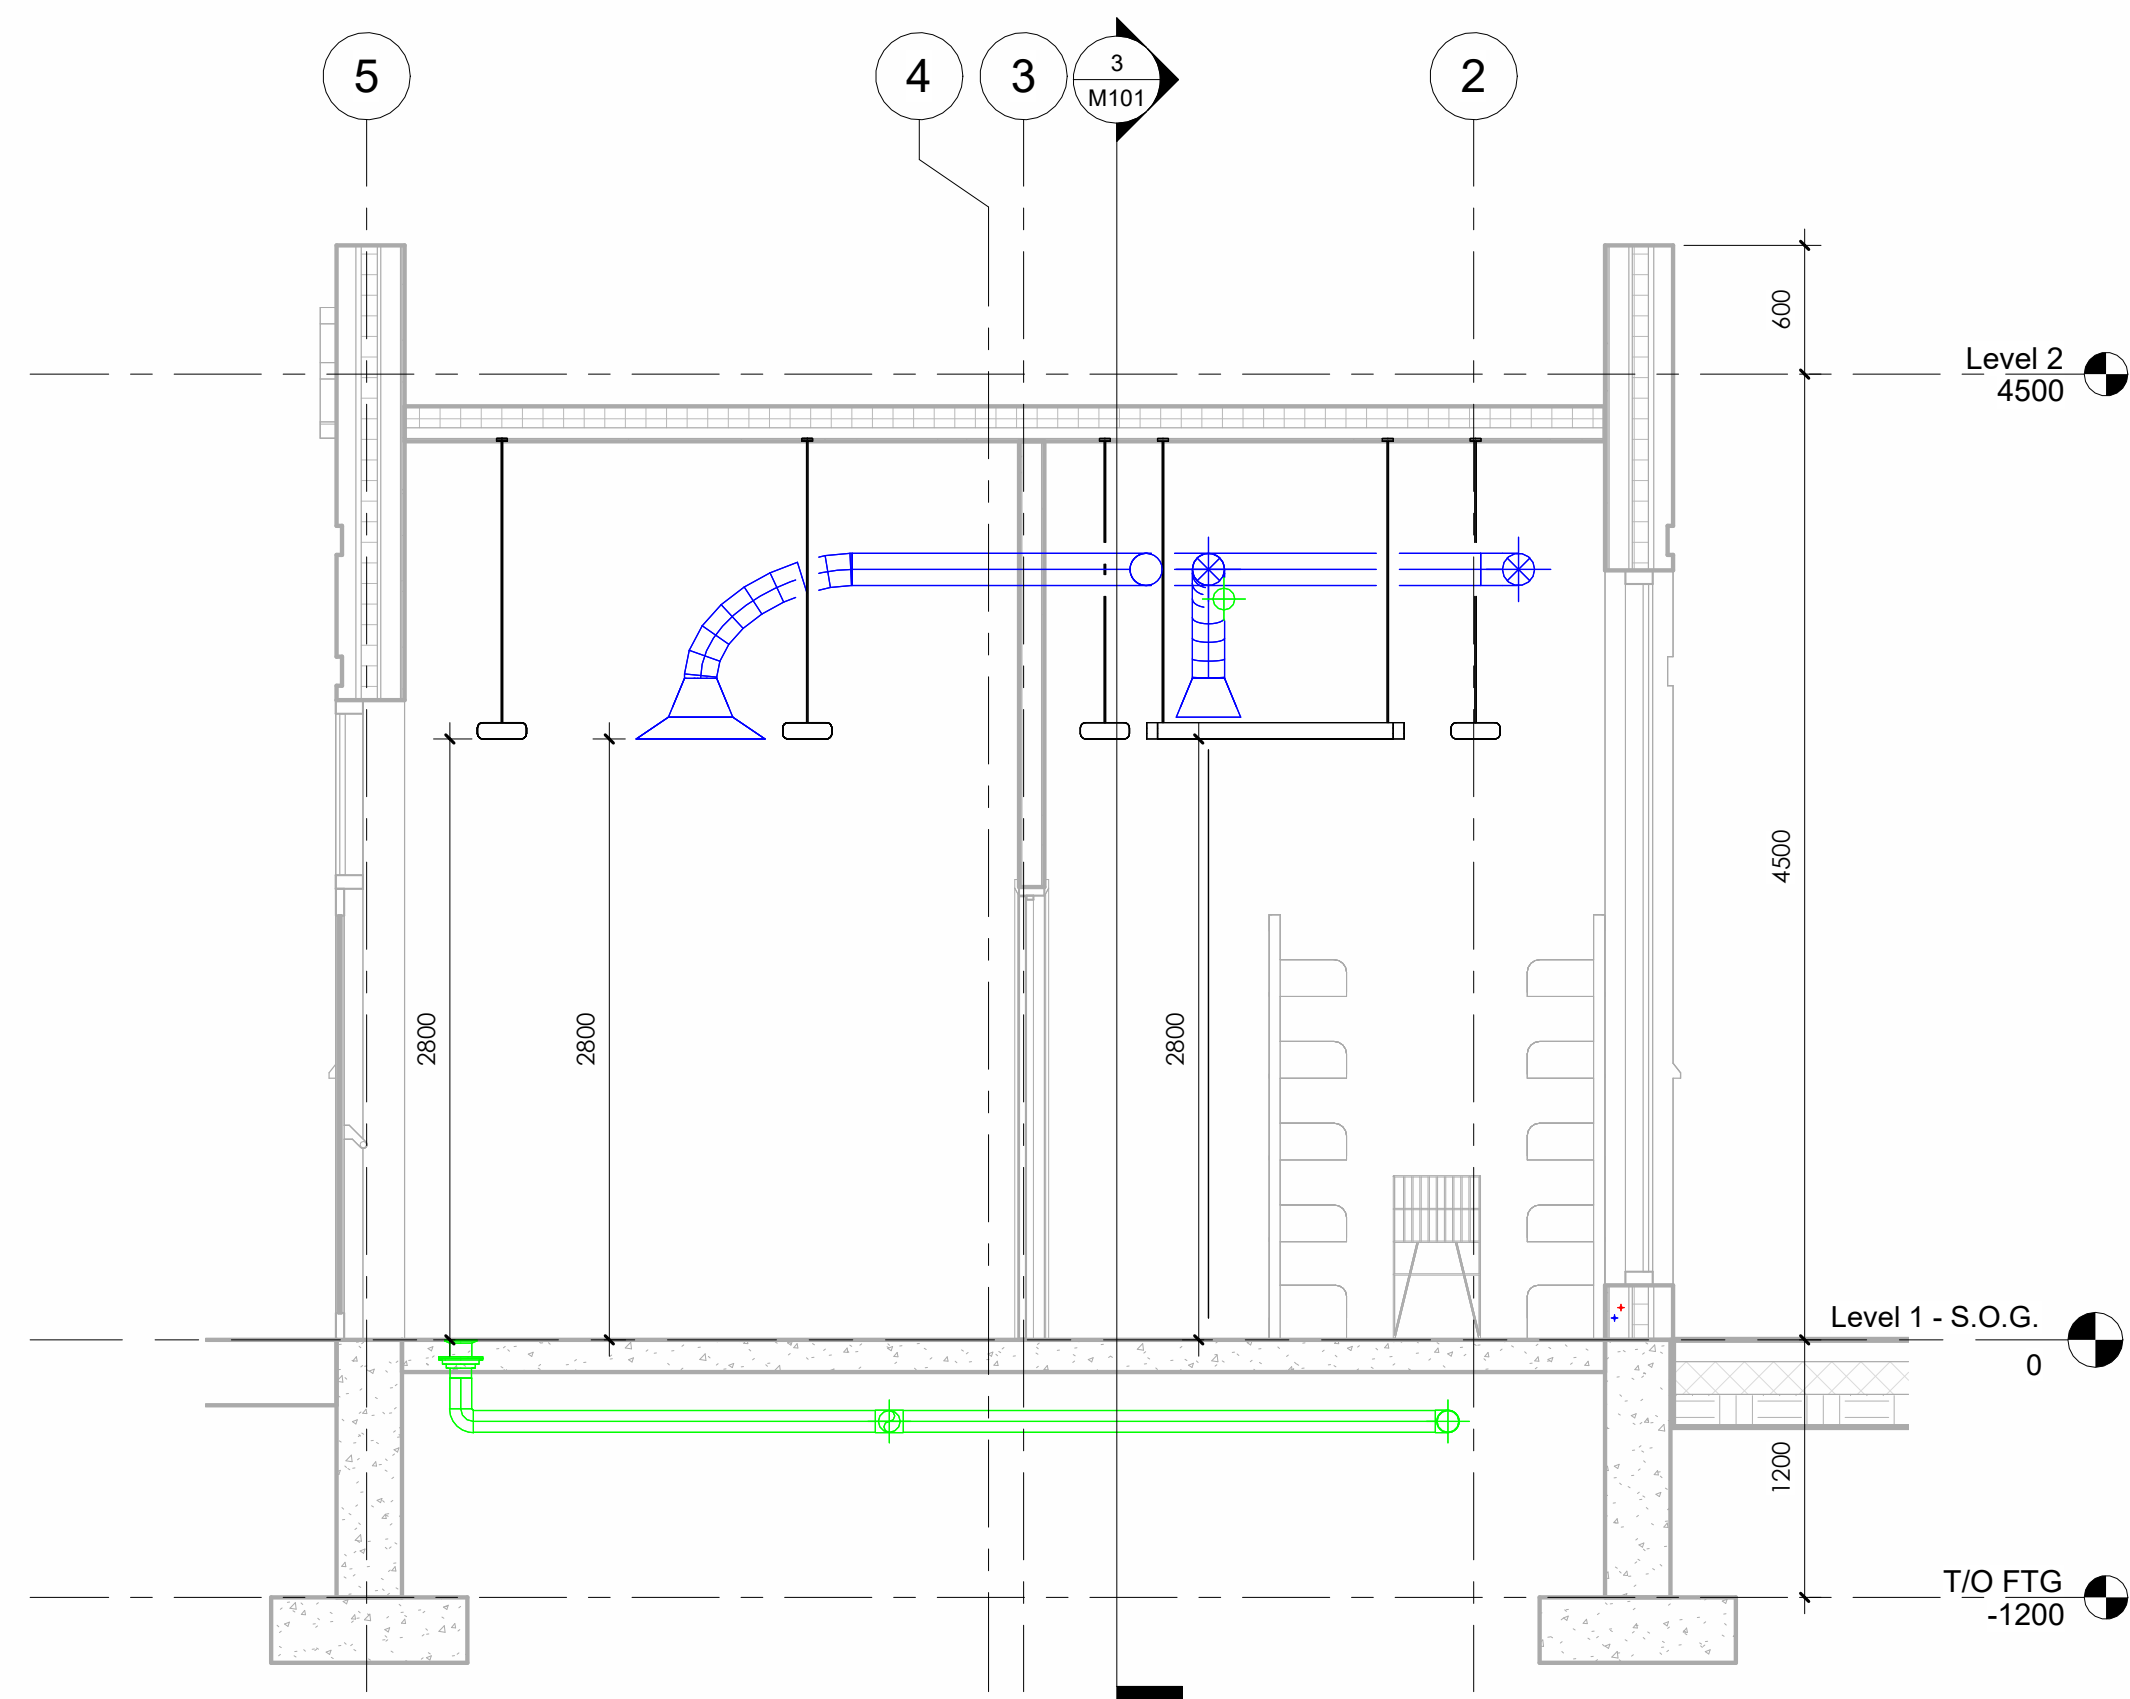

SYSTEMS M.E.P. SECTION 2


3/8" = 1'-0"

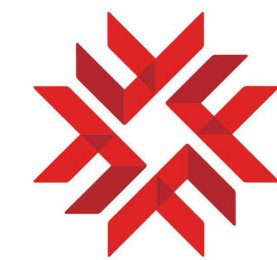

FANSHAWE

DONALD J. SMITH
SCHOOL OF BUILDING
TECHNOLOGY

NORTH ARROW

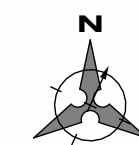

GRENRAL NOTES:-

1. DO NOT SCALE DRAWINGS. WRITTEN DIMENSIONS SHALL HAVE PRECEDENCE OVER SCALED DIMENSIONS.
2. ALL WORK SHALL COMPLY WITH THE 2012 ONTARIO BUILDING CODE AND AMENDMENTS.
3. CONTRACTORS MUST CHECK AND VERIFY ALL DIMENSIONS AND SPECIFICATIONS AND REPORT ANY DISCREPANCIES TO THE ARCHITECT BEFORE PROCEEDING WITH THE WORK.
4. ALL CONTRACTORS AND SUB-CONTRACTORS SHALL HAVE A SET OF APPROVED CONSTRUCTION DOCUMENTS ON SITE AT ALL TIMES.
5. ALL DOCUMENTS REMAIN THE PROPERTY OF THE ARCHITECT. UNAUTHORIZED USE, MODIFICATION, AND/OR REPRODUCTION OF THESE DOCUMENTS IS PROHIBITED WITHOUT WRITTEN PERMISSION. THE CONTRACT DOCUMENTS WERE PREPARED BY THE CONSULTANT FOR THE ACCOUNT OF THE OWNER.
6. THE MATERIAL CONTAINED HEREIN REFLECTS THE CONSULTANT'S BEST JUDGMENT IN LIGHT OF THE INFORMATION AVAILABLE TO HIM/HER AT THE TIME OF PREPARATION. ANY USE WHICH A THIRD PARTY MAKES OF THE CONTRACT DOCUMENTS, OR ANY RELIANCE ON/OR DECISIONS TO BE MADE BASED ON THEM ARE THE RESPONSIBILITY OF SUCH THIRD PARTIES.
7. THE CONSULTANT ACCEPTS NO RESPONSIBILITY FOR DAMAGES, IF ANY, SUFFERED BY ANY THIRD PARTY AS A RESULT OF DECISIONS MADE OR ACTIONS BASED ON THE CONTRACT DOCUMENTS

PRELIMINARY
NOT FOR CONSTRUCTION

PROJECT TITLE
DOODLE


CLIENT:
FANSHAWE COLLEGE
PROJECT ADDRESS
LONDON , ON

DRAWING TITLE
MEP PLAN AND 3D VIEWS

CHECKED | DRAWN | DATE
JF | AFNM | 14-08-25

3002-25S | M101
PROJECT No. | DRAWING

ID	Task Mode	Task Name	Duration	Start	Finish	Predecessors	Resource Names
1	🚀	Project Timeframe	111 days?	Tue 4/15/25	Mon 9/15/25		
2	🚀	Site Work	5 days?	Tue 4/15/25	Mon 4/21/25		
3	🚀	Project Award	2 days	Tue 4/15/25	Wed 4/16/25		
4	🚀	Tender & Procurement	3 days	Thu 4/17/25	Mon 4/21/25		
5	🚀	CONSTRUTION COMMENCEMENT	5 days	Mon 4/28/25	Fri 5/2/25		
6	🚀	Site Preparation	2 days	Mon 5/5/25	Tue 5/6/25		
7	🚀	Mobilization/Site Servicing	3 days	Wed 5/7/25	Fri 5/9/25		
8	🚀	Substructure	3 days	Tue 5/13/25	Thu 5/15/25		
9	🚀	Excavation	3 days	Thu 5/15/25	Mon 5/19/25		
10	🚀	Footing Formwork, Reinf. & Framing	2 days	Tue 5/20/25	Wed 5/21/25		
11	🚀	Pour Conc. Footings	1 day	Thu 5/22/25	Thu 5/22/25		
12	🚀	Foundation Wall Formwork	2 days	Thu 5/22/25	Fri 5/23/25		
13	🚀	Pour Concrete Walls	1 day	Mon 5/26/25	Mon 5/26/25		
14	🚀	Under Slab Services	3 days	Tue 5/27/25	Thu 5/29/25		
15	🚀	Granular Backfill around Foundation	3 days	Fri 5/30/25	Tue 6/3/25		
16	🚀	Foundations Complete	0 days	Tue 6/3/25	Tue 6/3/25		
17	🚀	Superstructure	12 days	Wed 6/4/25	Tue 6/17/25		
18	🚀	Slab on Grade Construction	1 day	Wed 6/4/25	Wed 6/4/25		
19	🚀	Exterior Wall Framing	5 days	Wed 6/11/25	Mon 6/16/25		
20	🚀	Roof Framework, Sheating Roof Build Up	1 day	Tue 6/17/25	Tue 6/17/25		
21	🚀	Insulation and Waterproofing	8 days	Tue 6/17/25	Thu 6/26/25		
22	🚀	Windows and Glazing	4 days	Thu 6/26/25	Tue 7/1/25		
23	🚀	Exterior Finishes	10 days	Wed 7/2/25	Wed 7/16/25		
24	🚀	HVAC Roof Top Unit Installation	1 day	Tue 6/17/25	Tue 6/17/25		
25	🚀	Bee Hives Installation in Roof	1 day	Wed 6/18/25	Wed 6/18/25		
26	🚀	Exterior Shell Complete	1 day	Thu 6/19/25	Thu 6/19/25		
27	🚀	Interior Core	4 days	Fri 6/20/25	Wed 6/25/25		
28	🚀	Interior Framing	3 days	Fri 6/20/25	Tue 6/24/25		
29	🚀	MEP Rough in	4 days	Wed 6/25/25	Mon 6/30/25		
30	🚀	Parapet Wall Framing	1 day	Mon 6/30/25	Mon 6/30/25		
31	🚀	Solar Panel Mount Installation	1 day	Tue 7/1/25	Tue 7/1/25		
32	🚀	Framing Complete	0 days	Wed 7/2/25	Wed 7/2/25		
33	🚀	Building Envelope	5 days	Thu 7/3/25	Thu 7/10/25		
34	🚀	Air & Vapour Barrier Installation	1 day	Thu 7/3/25	Thu 7/3/25		
35	🚀	Waterproofing and & Roof Insulation Installation	3 days	Fri 7/4/25	Tue 7/8/25		
36	🚀	Curtain Wall Installation	2 days	Wed 7/9/25	Thu 7/10/25		
37	🚀	Ext Cladding c/w Strapping	5 days	Thu 7/10/25	Wed 7/16/25		
38	🚀	Ext Building Envelope Complete	0 days	Thu 7/17/25	Thu 7/17/25		
39	🚀	Parapet Cap Installation	1 day	Thu 7/17/25	Thu 7/17/25		
40	🚀	Roof Ladder	1 day	Fri 7/18/25	Fri 7/18/25		
41	🚀	Int Finishes	3 days	Mon 7/21/25	Wed 7/23/25		
42	🚀	Conc SOG Polished finish & Protection	1 day	Mon 7/21/25	Mon 7/21/25		
43	🚀	Int Building Cleaning	0.5 days	Tue 7/22/25	Tue 7/22/25		
44	🚀	Drywall Installation	3 days	Tue 7/22/25	Thu 7/24/25		
45	🚀	Millwork	3 days	Fri 7/25/25	Tue 7/29/25		
46	🚀	Prime and Painting	2 days	Tue 7/29/25	Wed 7/30/25		
47	🚀	ACP Grid Installatio	2 days	Thu 7/31/25	Fri 8/1/25		
48	🚀	ACP Tile Installation	1 day	Fri 8/1/25	Fri 8/1/25		
49	🚀	B.F. W/R & Café Accessory Installtions	2 days	Mon 8/4/25	Tue 8/5/25		
50	🚀	Int Finishes Final Complete	0 days	Tue 8/5/25	Tue 8/5/25		
51	🚀	MEP	3 days	Wed 8/6/25	Fri 8/8/25		
52	🚀	Int Plumbing Rough-In	2 days	Wed 8/6/25	Thu 8/7/25		
53	🚀	Int Electrical Rough-In	1 day	Fri 8/8/25	Fri 8/8/25		
54	🚀	Plumbing Fixtures & Equipment	2 days	Mon 8/11/25	Tue 8/12/25		
55	🚀	Electrical Fixtures & Equipment	2 days	Wed 8/13/25	Thu 8/14/25		
56	🚀	HVAC Equipment and Ductwork Installation	3 days	Fri 8/15/25	Tue 8/19/25		
57	🚀	MEP Commissioning	1 day	Tue 8/19/25	Tue 8/19/25		
58	🚀	HVAC Commissing	1 day	Wed 8/20/25	Wed 8/20/25		
59	🚀	MEP & Coordination Complete	0 days	Thu 8/21/25	Thu 8/21/25		
60	🚀	Landscaping	3 days	Mon 8/25/25	Wed 8/27/25		
61	🚀	Rooffop & Pavers & Sleepers	1 day	Mon 8/25/25	Mon 8/25/25		
62	🚀	Stamped Conc Pavers Poured	2 days	Tue 8/26/25	Wed 8/27/25		
63	🚀	Landscaping & Planting	3 days	Wed 8/27/25	Fri 8/29/25		
64	🚀	Outdoor Wood Canopy, Bar & Signage Installation	1 day	Mon 9/1/25	Mon 9/1/25		
65	🚀	Apiary Installation	1 day	Tue 9/2/25	Tue 9/2/25		
66	🚀	Site & Building Clean up	2 days	Wed 9/3/25	Thu 9/4/25		
67	🚀	Final Inspections/Occupancy Walkthrough	2 days	Mon 9/8/25	Tue 9/9/25		
68	🚀	Consultant Deficiencies	2 days	Wed 9/10/25	Thu 9/11/25		
69	🚀	Building Turnover	0 days	Fri 9/12/25	Fri 9/12/25		

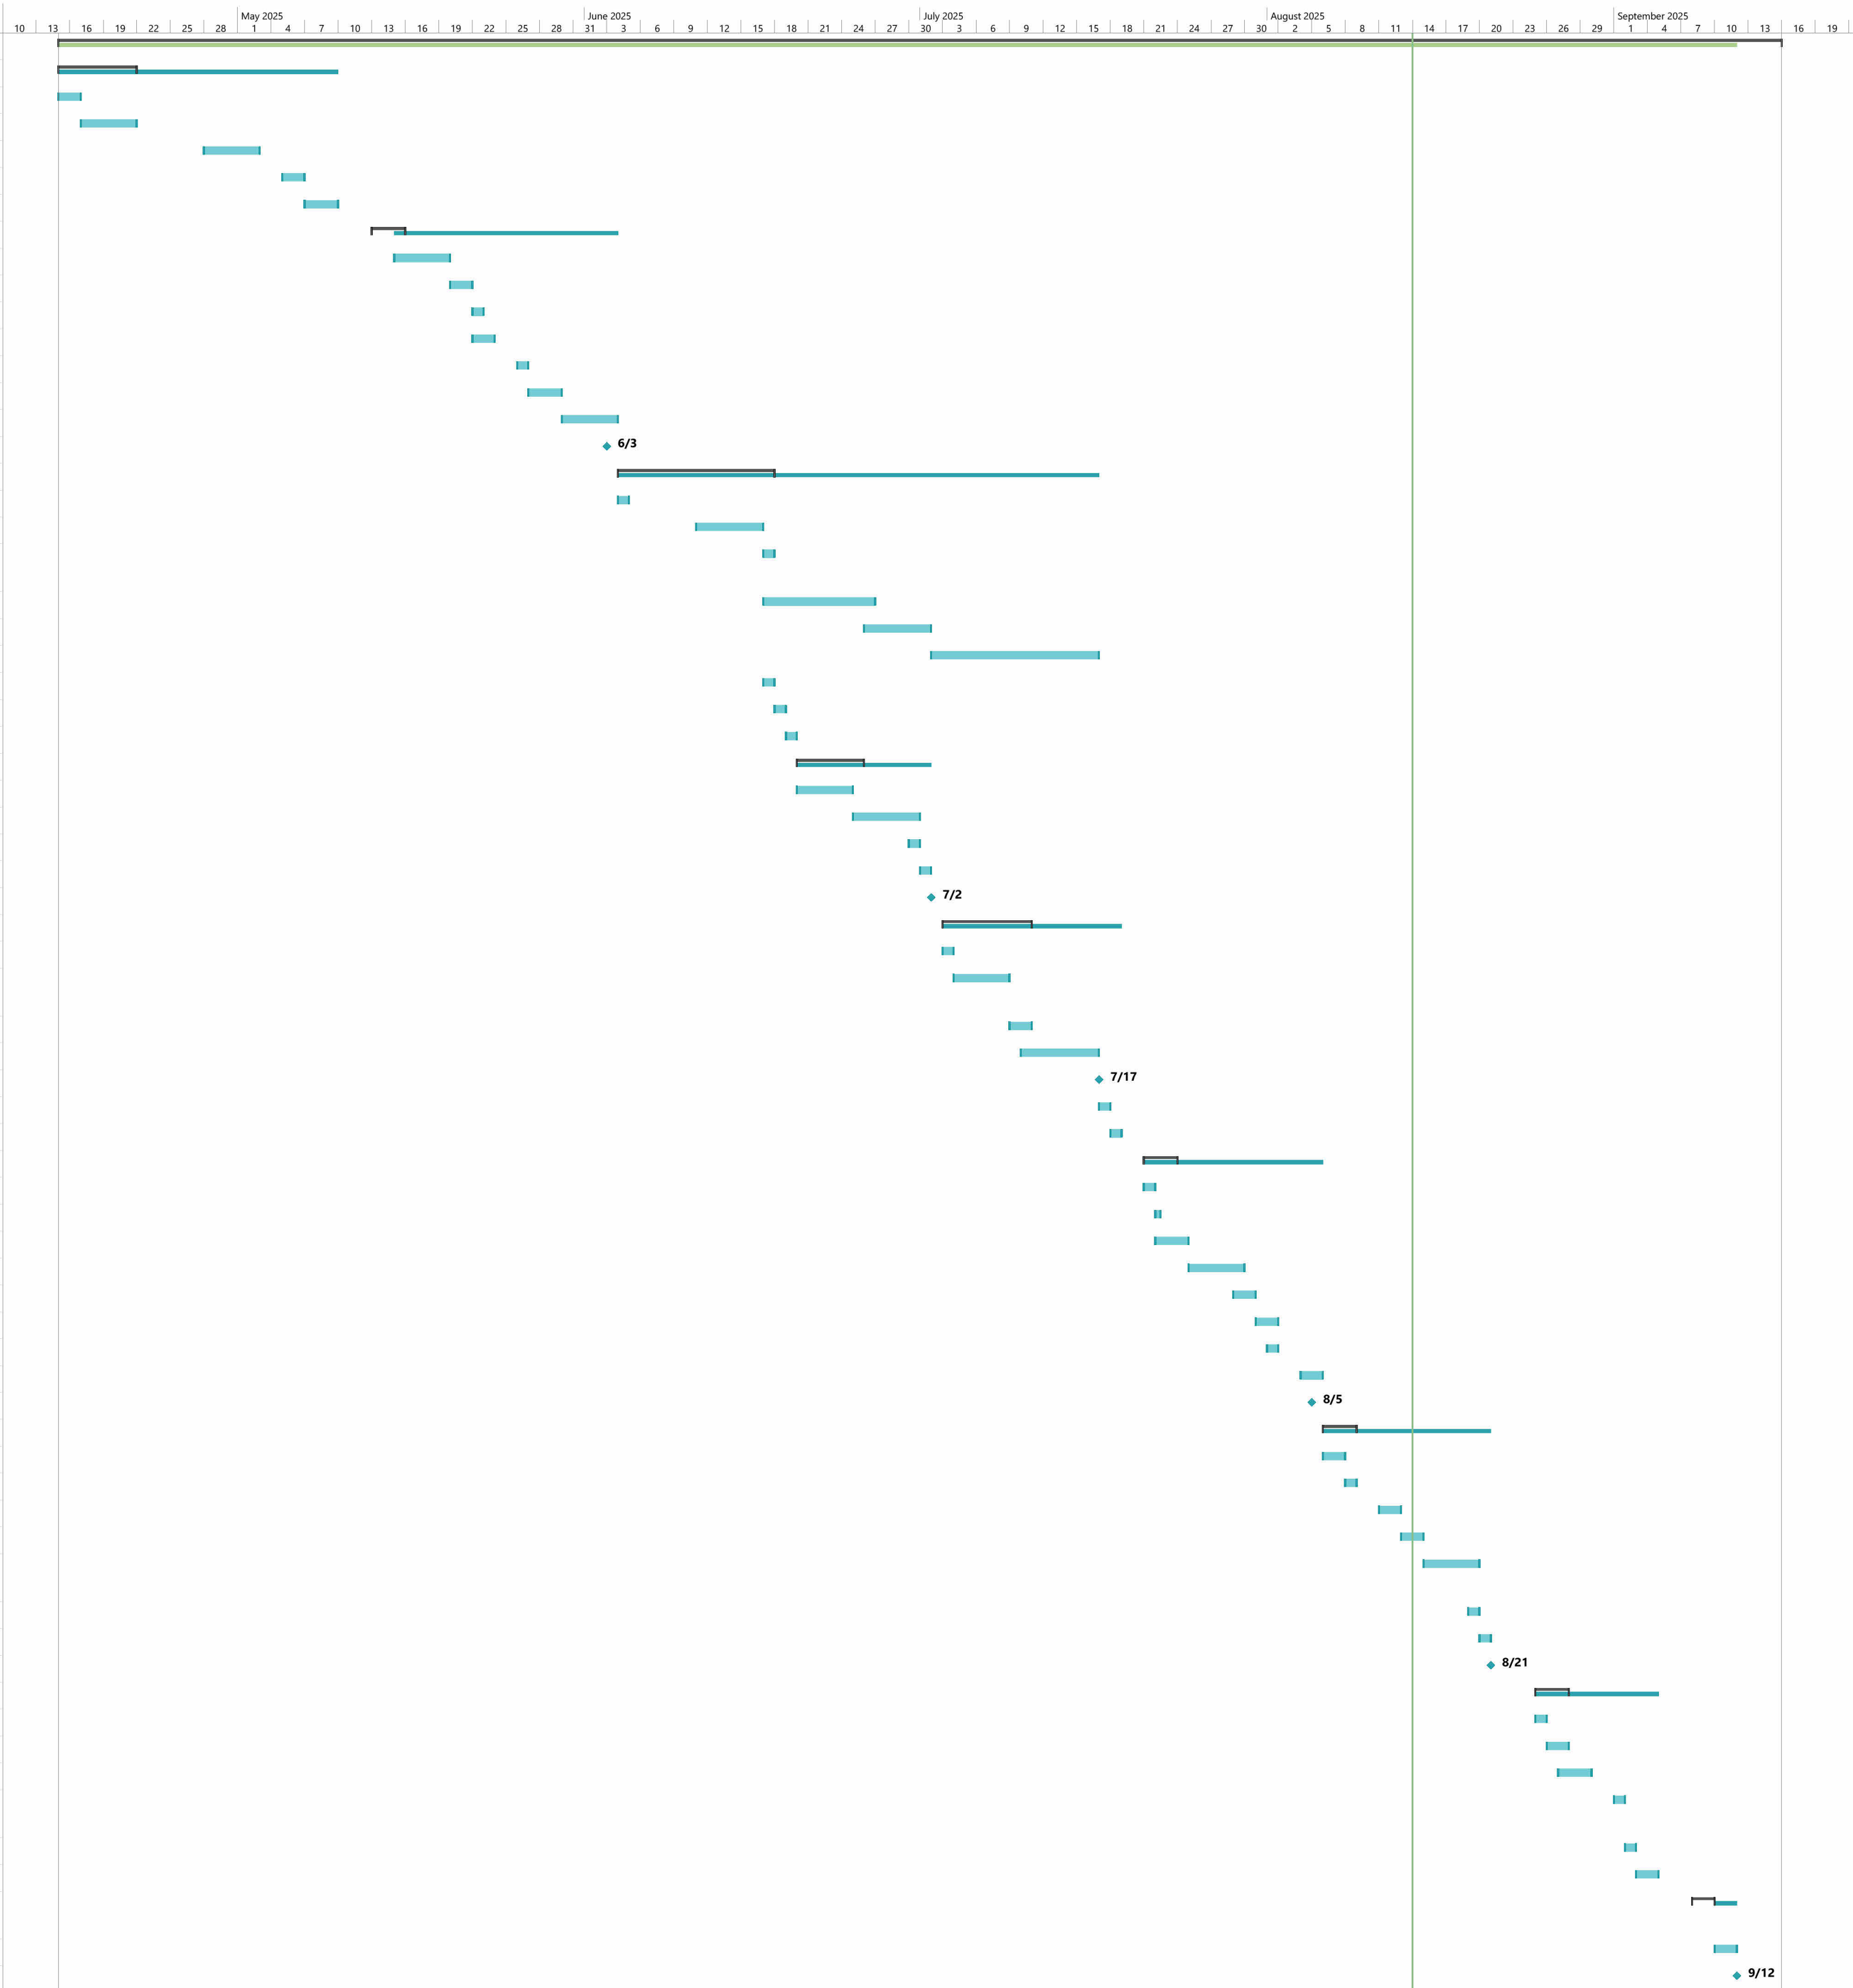

Project: DOODLE.mpp
Date: Thu 8/14/25

Task Split

Milestone

Summary

Project Summary

Inactive Task

Inactive Milestone

Inactive Summary

Manual Task

Duration-only

Manual Summary Rollup

Manual Summary

Start-only

Finish-only

External Tasks


External Milestone

Deadline

Progress

Manual Progress

Page 1

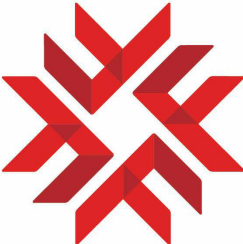

FANSHAWE

DONALD J. SMITH

SCHOOL OF BUILDING

TECHNOLOGY

NORTH ARROW



GRENRAL NOTES:-

1. DO NOT SCALE DRAWINGS. WRITTEN DIMENSIONS SHALL HAVE PRECEDENCE OVER SCALED DIMENSIONS.

2. ALL WORK SHALL COMPLY WITH THE 2012 ONTARIO BUILDING CODE AND AMENDMENTS.

3. CONTRACTORS MUST CHECK AND VERIFY ALL DIMENSIONS AND SPECIFICATIONS AND REPORT ANY DISCREPANCIES TO THE ARCHITECT BEFORE PROCEEDING WITH THE WORK.

4. ALL CONTRACTORS AND SUB-CONTRACTORS SHALL HAVE A SET OF APPROVED CONSTRUCTION DOCUMENTS ON SITE AT ALL TIMES.

5. ALL DOCUMENTS REMAIN THE PROPERTY OF THE ARCHITECT. UNAUTHROIZED USE, MODIFICATION, AND/OR REPRODUCTION OF THESE DOCUMENTS IS PROHIBITED WITHOUT WRITTEN PERMISSION. THE CONTRACT DOCUMENTS WERE PREPARED BY THE CONSULTANT FOR THE ACCOUNT OF THE OWNER.

6. THE MATERIAL CONTAINED HEREIN REFLECTS THE CONSULTANTS BEST JUDEGMENT IN LIGHT OF THE INFORMATION AVAILABLE TO HIM/HER AT THE TIME OF PREPARATION. ANY USE WHICH A THIRD PARTY MAKES OF THE CONTRACT DOCUMENTS, OR ANY RELIANCE ON/OR DESCISSIONS TO BE MADE BASED ON THEM ARE THE RESPONSIBILITY OF SUCH THIRD PARTIES.

7. THE CONSULTANT ACCEPTS NO RESPONSIBILITY FOR DAMAGES. IF ANY, SUFFERED BY ANY THIRD PARTY AS A RESULT OF DESCISSIONS MADE OR ACTIONS BASED ON THE CONTRACT DOCUMENTS

PROJECT TITLE

DOODLE

CLIENT:

FANSHAWE COLLEGE

PROJECT ADDRESS

LONDON , ON

DRAWING TITLE

SCHEDULE

CHECKED
JF

DRAWN
KK

DATE
07/30/25

3002-25S

P101

PROJECT No.


DRAWING

8/14/2025 1:50:38 PM C:\Users\fazal\OneDrive\Desktop\doodle updated.rvt

GENERAL COST ESTIMATION				
Building Type	Location	Cost	Sq. ft.	Total
Retail/Strip Plaza	ON - GTA	\$265	538	\$142,570
According to 2024 Canadian Cost Guide				

BUDGET200,000

DOODLE CAFÉ								
Category	Subcategory	Unit of Measurement	Unit	Cost (\$)	Total (\$)	Description	Totals (\$)	Percentage
Design Cost	Architectural Design	item	1	3,000.00	3,000.00		9,800.00	4.90%
	Structural Engineer	item	1	2,000.00	2,000.00			
	MEP	item	1	2,000.00	2,000.00			
	Permit Fees	item	1	1,000.00	1,000.00			
	Site Survey	m2	50	1,800.00	1,800.00			
Site Work	Site Clearance	m2	50	40.00	400.00	Including machinery	400.00	0.20%
Foundations & Footings	Excavation	m3	35	40.00	1,400.00	Including machinery, labour, disposal of materials & backfill	14,057.82	7.03%
	Concrete-25MPA	m3	32.27	266.00	8,583.82	Including FDN, FTG, SOG - Duffern Concrete		
	Formwork	m2	70	46.00	3,220.00			
	Reinforcement	m2	35	10.00	350.00			
	Labour Cost	hrs	28	18.00	504.00			
Structural Elements	Exterior Stud Wall Framing	m2	42	120.00	5,040.00		9,020.00	4.51%
	Pergola	m2	10	269.00	2,690.00	Cedar/Pine		
	Wall Framing-interior	m2	30	43.00	1,290.00			
Building Envelope	Curtain Wall Entrance	m2	9.5	250.00	2,375.00	Including labor and installation cost	52,845.00	26.42%
	Brick Siding	m2	65	600.00	39,000.00	Including labor and installation cost		
	Rigid Insulation	m2	65	30.00	1,950.00	R-10, 2-inch thick		
	Roof Construction	m2	34	150.00	5,100.00	Including labor and installation cost		
	ACT Ceiling	m2	34	130.00	4,420.00	Including labor and installation cost		
Windows & Doors	Aluminum Windows - Curtain Wall	m2	17	250.00	4,250.00	Including installation cost	18,721.00	9.36%
	Aluminium Windows	no.	2	1,000.00	2,000.00	Including installation cost		
	Aluminium Double Door	no.	2	4,500.00	9,000.00	Including installation cost		
	Interior Doors	no.	3	1,157.00	3,471.00	Including installation cost		
MEP	Rooftop Unit	no.	1	3,000.00	3,000.00		9,543.00	4.77%
	Ceiling Light	no.	10	35.00	350.00			
	W/C Sink	no.	1	130.00	130.00			
	Brewery Sink	no.	1	300.00	300.00			
	Water Closet	no.	1	135.00	135.00			
	Tankless Water Heater	no.	1	2,350.00	2,350.00			
	Roof Drain	no.	3	112.00	336.00			
	Cold and Hot Pipes	m	11.98	150.00	1,797.00			
	Breaker Panel	no.	1	130.00	130.00			
	Bathroom Exhaust Fan	no.	1	55.00	55.00			
	Labour Cost	hrs	24	40.00	960.00			
Interior Finishes	Gypsum Wallboard	sheets	15	16.43	246.45	4x8ft sheet	1,911.45	0.96%
	Paint	gallon	1	65.00	65.00			
	Labour Cost	hrs	40	40.00	1,600.00			
Exterior Finishes	Building Signage	no.	1	900.00	900.00		2,055.00	1.03%
	Paint	gallon	3	65.00	195.00			
	Labour Cost	hrs	24	40.00	960.00			
Other	Rooftop Access Ladder	item	1	754.00	754.00		2,314.00	1.16%
	Beehive	no.	3	520.00	1,560.00			
Pretax					120,667.27			
Overhead (10%)					12,066.73			
Tax (13%)					15,686.75			
FINAL COST					148,420.74			

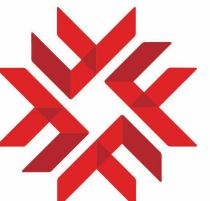

FANSHAWE
DONALD J. SMITH
SCHOOL OF BUILDING
TECHNOLOGY

NORTH ARROW



GRENRAL NOTES:-
1. DO NOT SCALE DRAWINGS. WRITTEN DIMENSIONS SHALL HAVE PRECEDENCE OVER SCALED DIMENSIONS.
2. ALL WORK SHALL COMPLY WITH THE 2012 ONTARIO BUILDING CODE AND AMENDMENTS.
3. CONTRACTORS MUST CHECK AND VERIFY ALL DIMENSIONS AND SPECIFICATIONS AND REPORT ANY DISCREPANCIES TO THE ARCHITECT BEFORE PROCEEDING WITH THE WORK.
4. ALL CONTRACTORS AND SUB-CONTRACTORS SHALL HAVE A SET OF APPROVED CONSTRUCTION DOCUMENTS ON SITE AT ALL TIMES.
5. ALL DOCUMENTS REMAIN THE PROPERTY OF THE ARCHITECT. UNAUTHROIZED USE, MODIFICATION, AND/OR REPRODUCTION OF THESE DOCUMENTS IS PROHIBITED WITHOUT WRITTEN PERMISSION. THE CONTRACT DOCUMENTS WERE PREPARED BY THE CONSULTANT FOR THE ACCOUNT OF THE OWNER.
6. THE MATERIAL CONTAINED HEREIN REFLECTS THE CONSULTANTS BEST JUDGEMENT IN LIGHT OF THE INFORMATION AVAILABLE TO HIM/HER AT THE TIME OF PREPARATION. ANY USE WHICH A THIRD PARTY MAKES OF THE CONTRACT DOCUMENTS, OR ANY RELIANCE ON/OR DECISIONS TO BE MADE BASED ON THEM ARE THE RESPONSIBILITY OF SUCH THIRD PARTIES.
7. THE CONSULTANT ACCEPTS NO RESPONSIBILITY FOR DAMAGES, IF ANY, SUFFERED BY ANY THIRD PARTY AS A RESULT OF DESICISIONS MADE OR ACTIONS BASED ON THE CONTRACT DOCUMENTS

PRELIMINARY
NOT FOR CONSTRUCTION

PROJECT TITLE
DOODLE

CLIENT:
FANSHAWE COLLEGE
PROJECT ADDRESS
LONDON , ON

DRAWING TITLE
COST ESTIMATION

CHECKED | DRAWN | DATE
JF | KK | 07/30/25

3002-25S | P102
PROJECT NO. | DRAWING